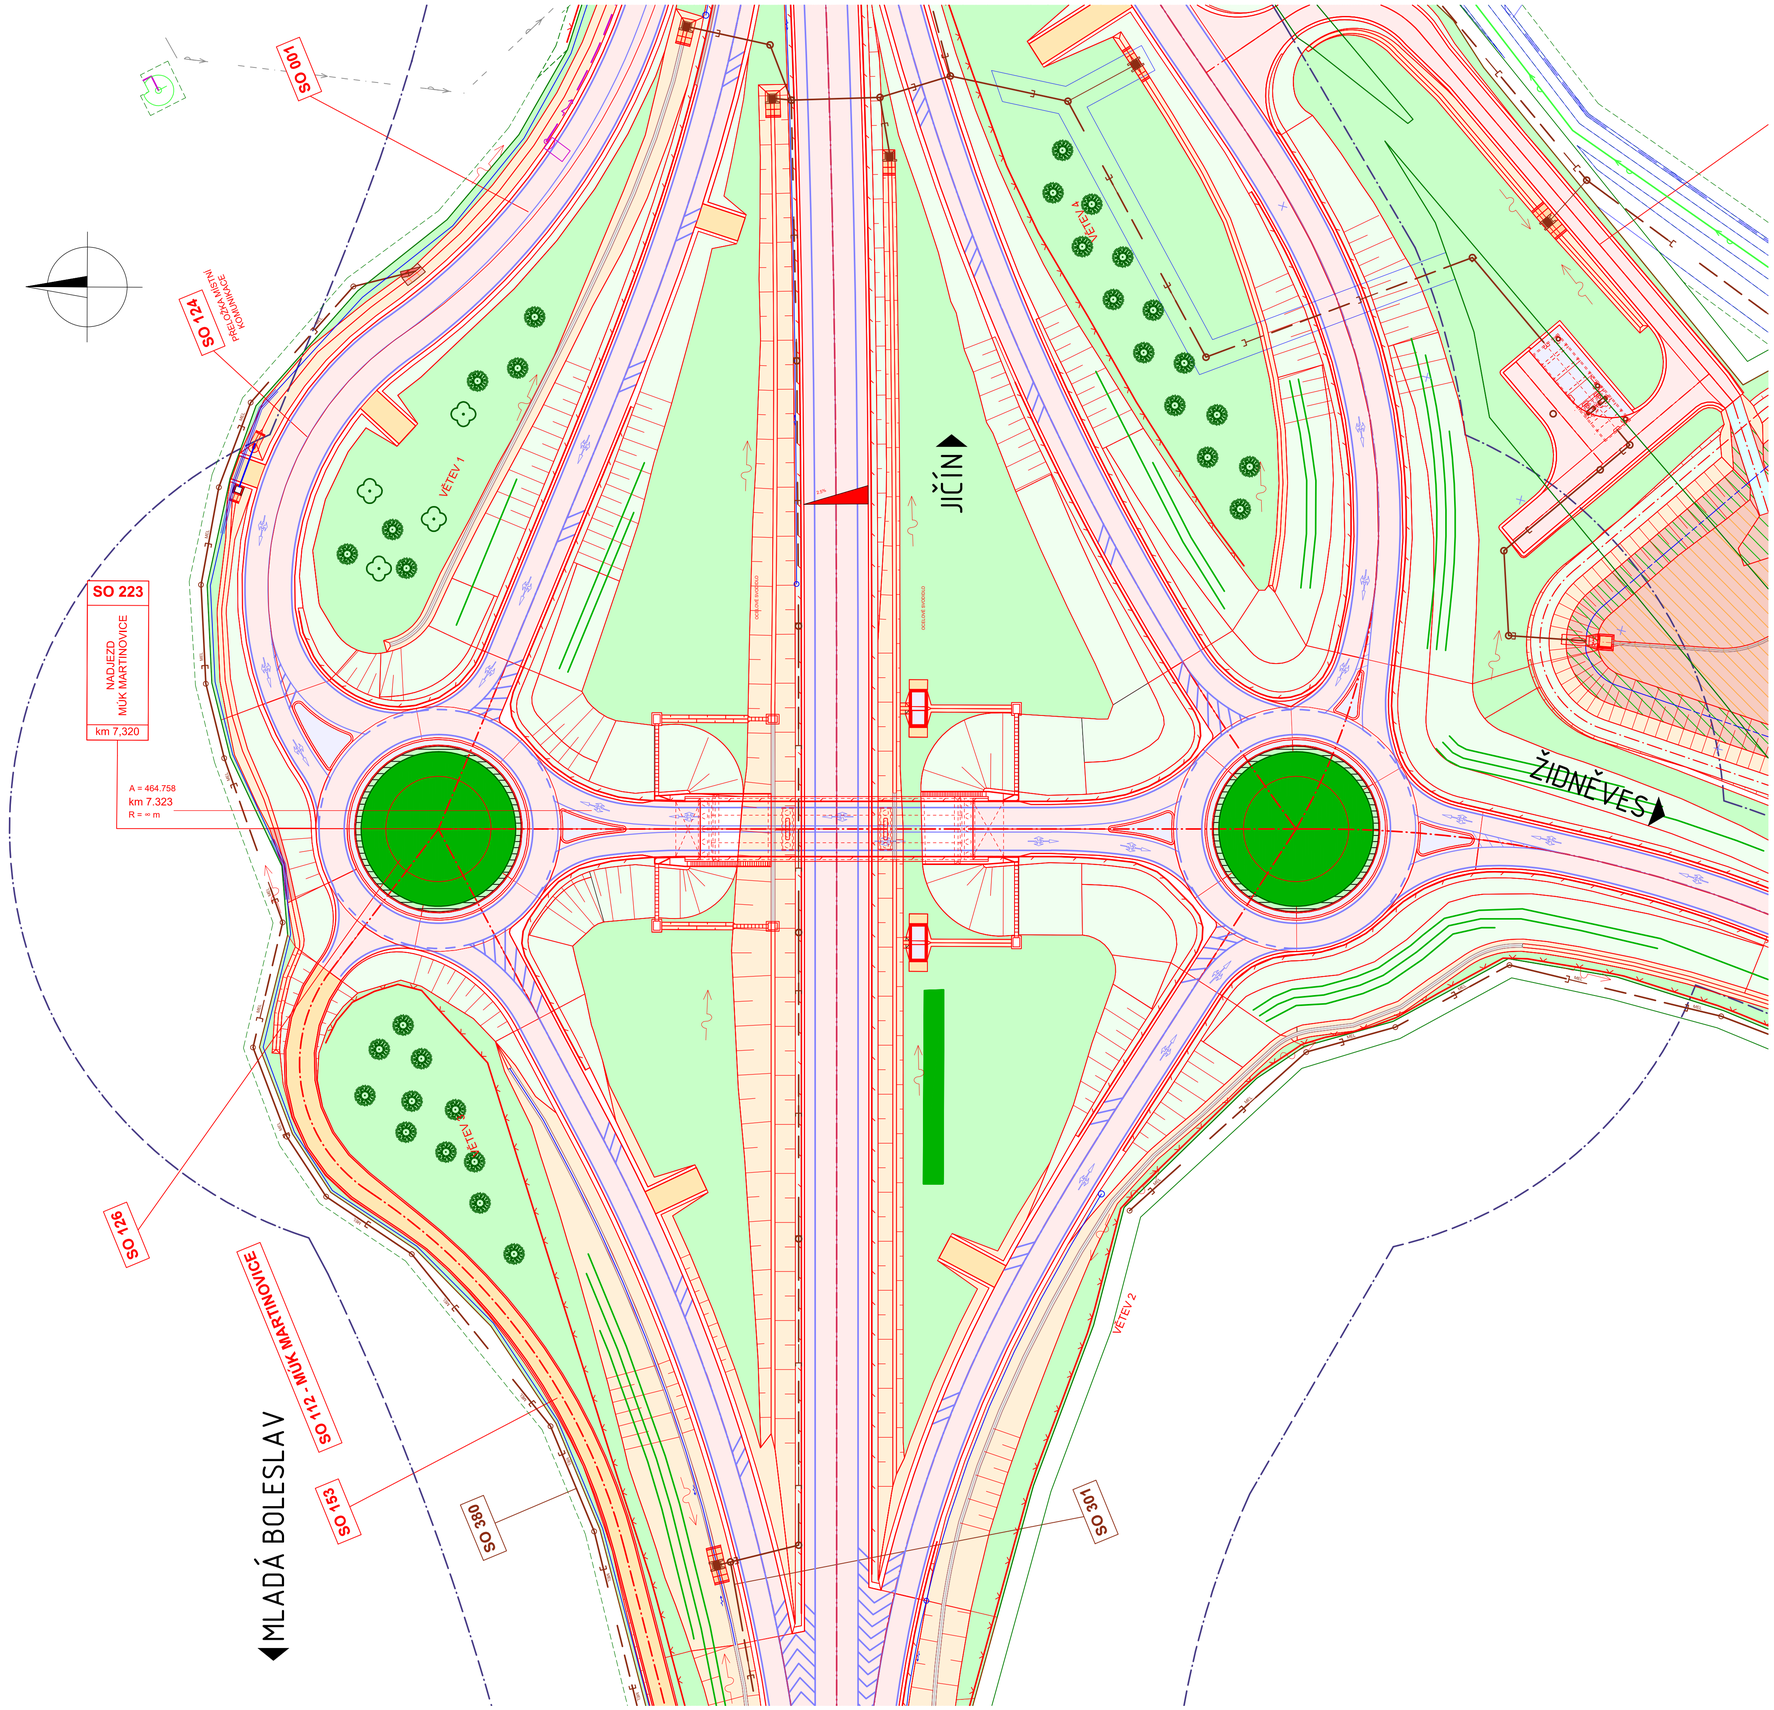



Souřadnicový systém: S-JTSK
Výškový systém: Bpv

**SO 223** NADJEZD MÚK MARTINOVICE V KM 7,320

**Objednatel:**
ŘEDITELSTVÍ SILNIC A DÁLNIC
**Ředitelství silnic a dálnic s. p.**
Čerčanská 2023/12, Krč, 140 00 Praha 4

**Valbek, spol. s r.o.**
Vaňurova 505/17
460 07 Liberec 3

| | | | | | |
|---|---|---|---|---|---|
| **Vypracoval** | ING. S. RŮŽIČKA | | **Zak. číslo** | **21-LI13-001** |
| **Zodp. projektant** | ING. S. RŮŽIČKA | | **Datum** | **02/2025** |
| **Tech. kontrola** | ING. I. BELDA | | **Stupeň** | **PDPS** |
| **Akce** | **I/16 MLADÁ BOLESLAV - MARTINOVICE** | | **Počet formátů** | **8x A4** |
| | | | **Měřítko** | **1:500** |
| | | | **Č. přílohy** | **Paré** |
| **Zhotovitel:** Valbek, spol. s r.o. Vaňurova 505/17 460 07 Liberec 3 | **Příloha** PŘEHLEDNÁ SITUACE | | 401 | |