


PŮDORYS 1:150

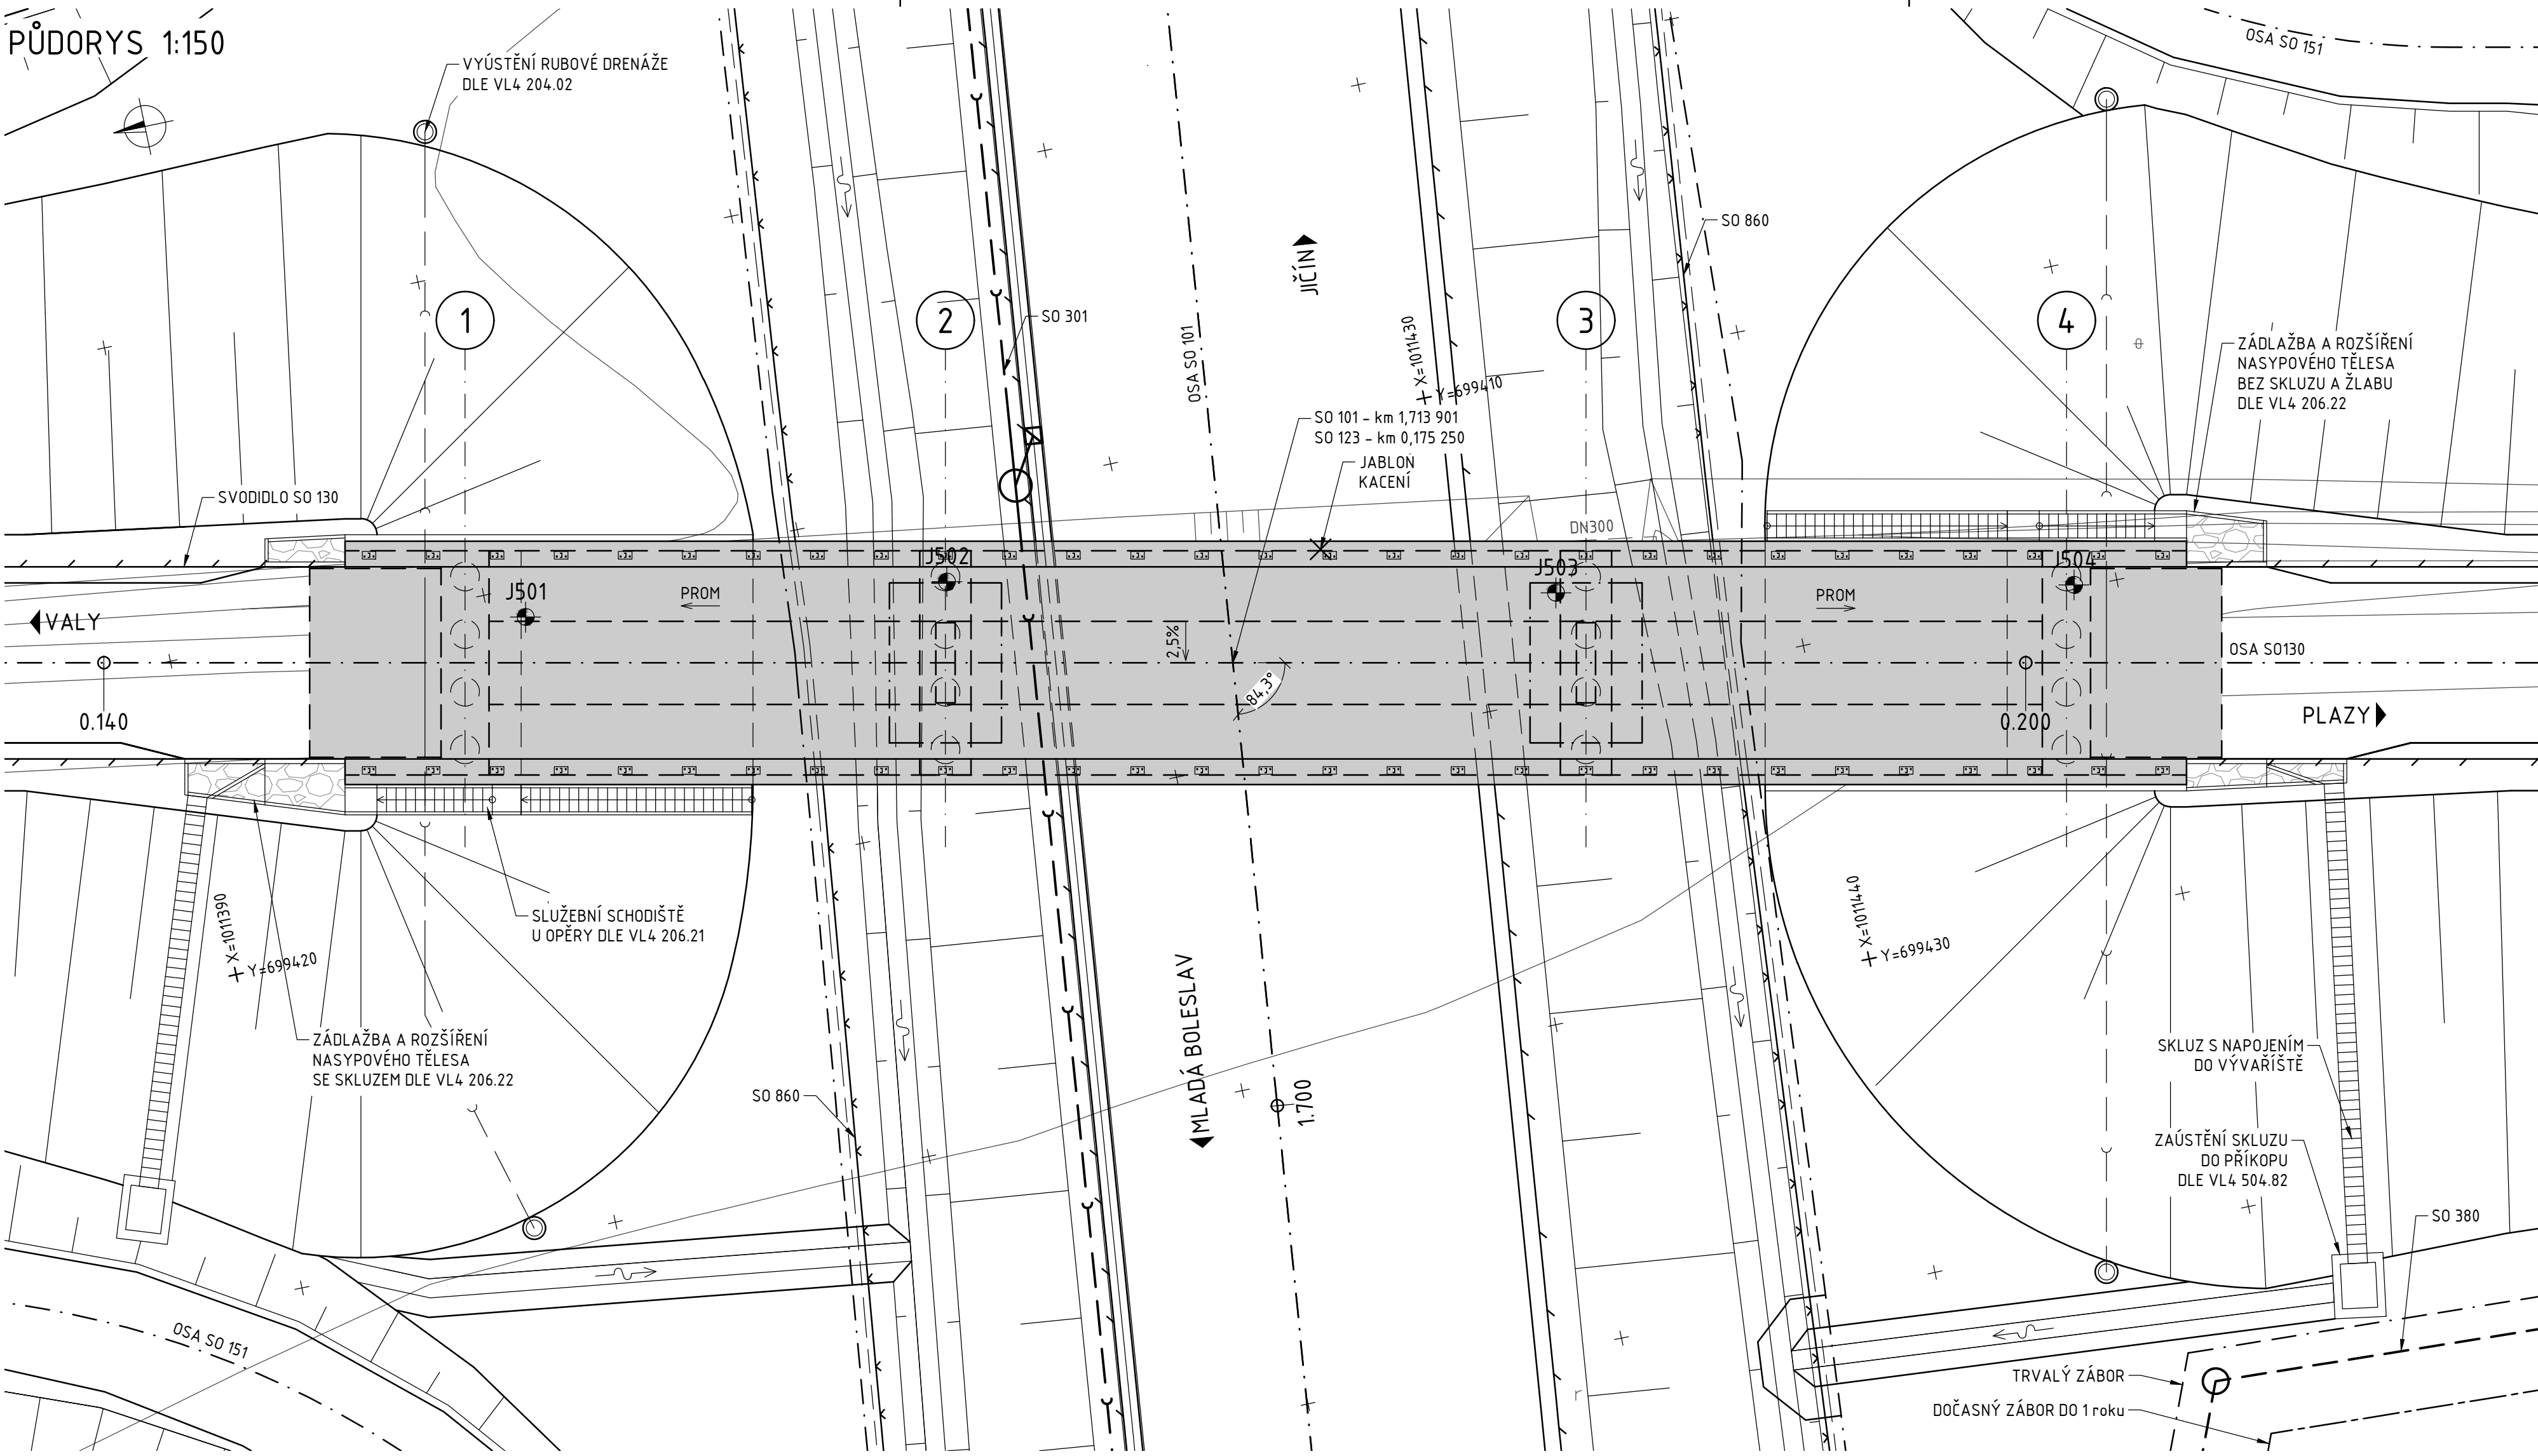


SOUVISEJÍCÍ OBJEKTY

SO 020 PŘÍPRAVA ÚZEMÍ
SO 101 SILNICE I/16 MLADÁ BOLESLAV - MARTINOVICE
SO 130 PŘELOŽKA MÍSTNÍ KOMUNIKACE V km 1,713
SO 151 PŘÍSTUPY NA POZEMKY K.Ú. PLAZY - ÚPRAVA 151.2 A 151.5
SO 301 ODVODNĚNÍ I/16
SO 380 ÚPRAVY MELIORACÍ ZÚ - KÚ
SO 860 OPLOČENÍ

SMĚROVÉ VEDENÍ SO 101


STANIČENÍ	Y	X	PARAMETR
1.699 962	699430.725	1011420.970	PŘÍMÁ
2.457 881	698677.149	1011501.983	

VÝŠKOVÉ VEDENÍ SO 101

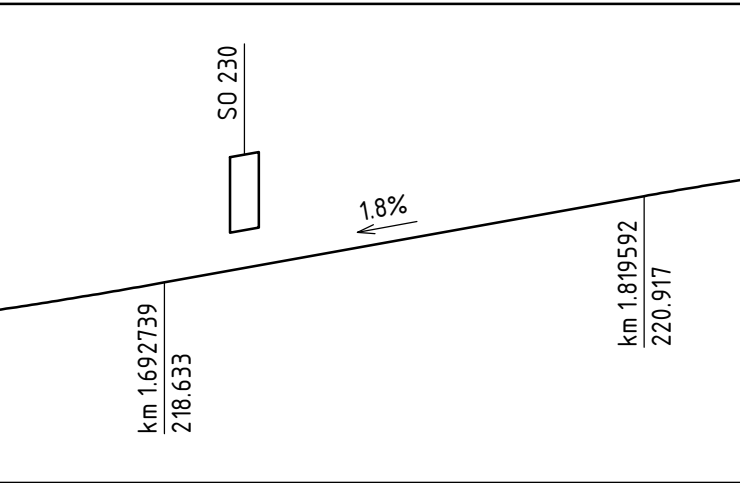

M01 -/5,5/30


POHLED VE SMĚRU STANIČENÍ

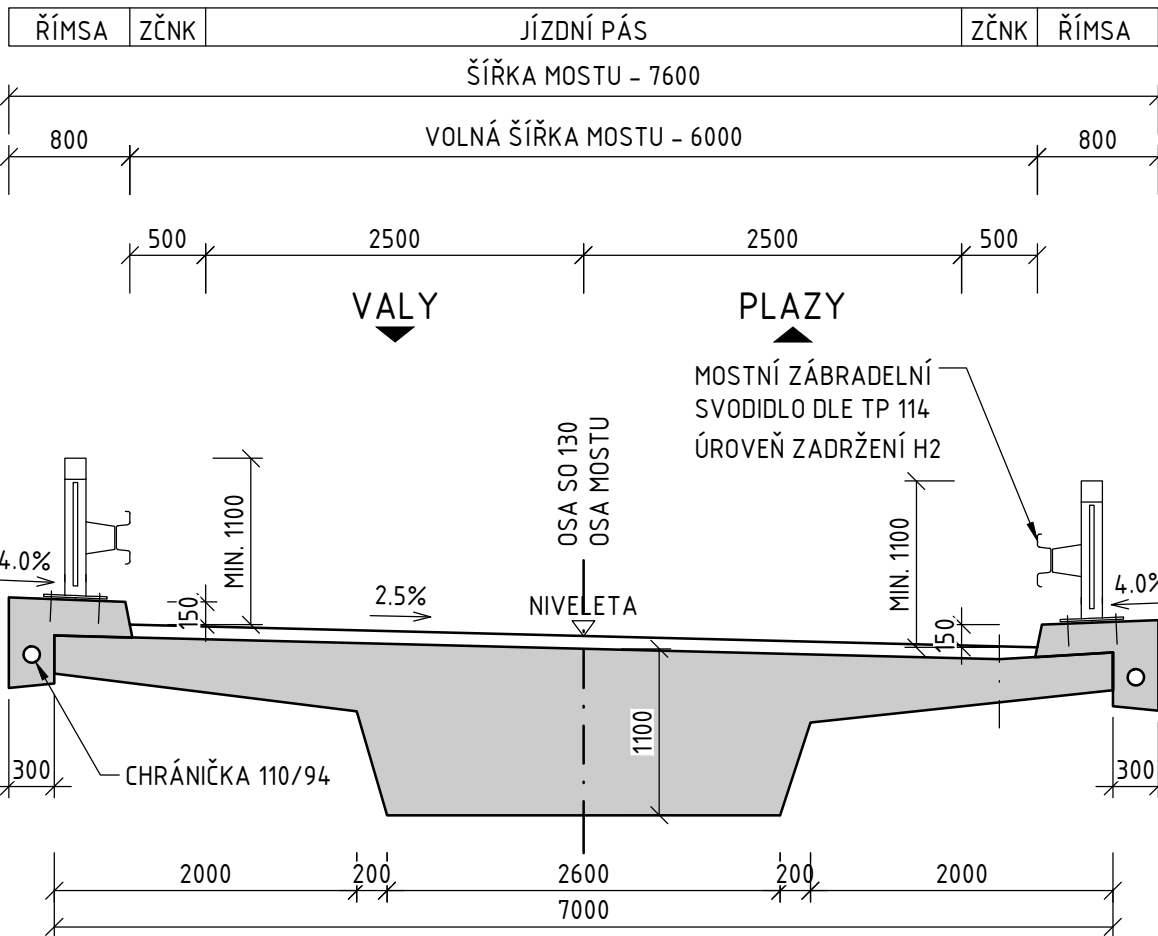

POZNÁMKY

- NEJLÉPŠÍ SOUČÁSTÍ VÝKRESU JSOU TECHNICKÉ SPECIFIKACE A POZNÁMKY UVEDENÉ NA VÝKRESE TECHNICKÝCH SPECIFIKACÍ A POZNÁMEK,


PODÉLNÝ ŘEZ 1:150

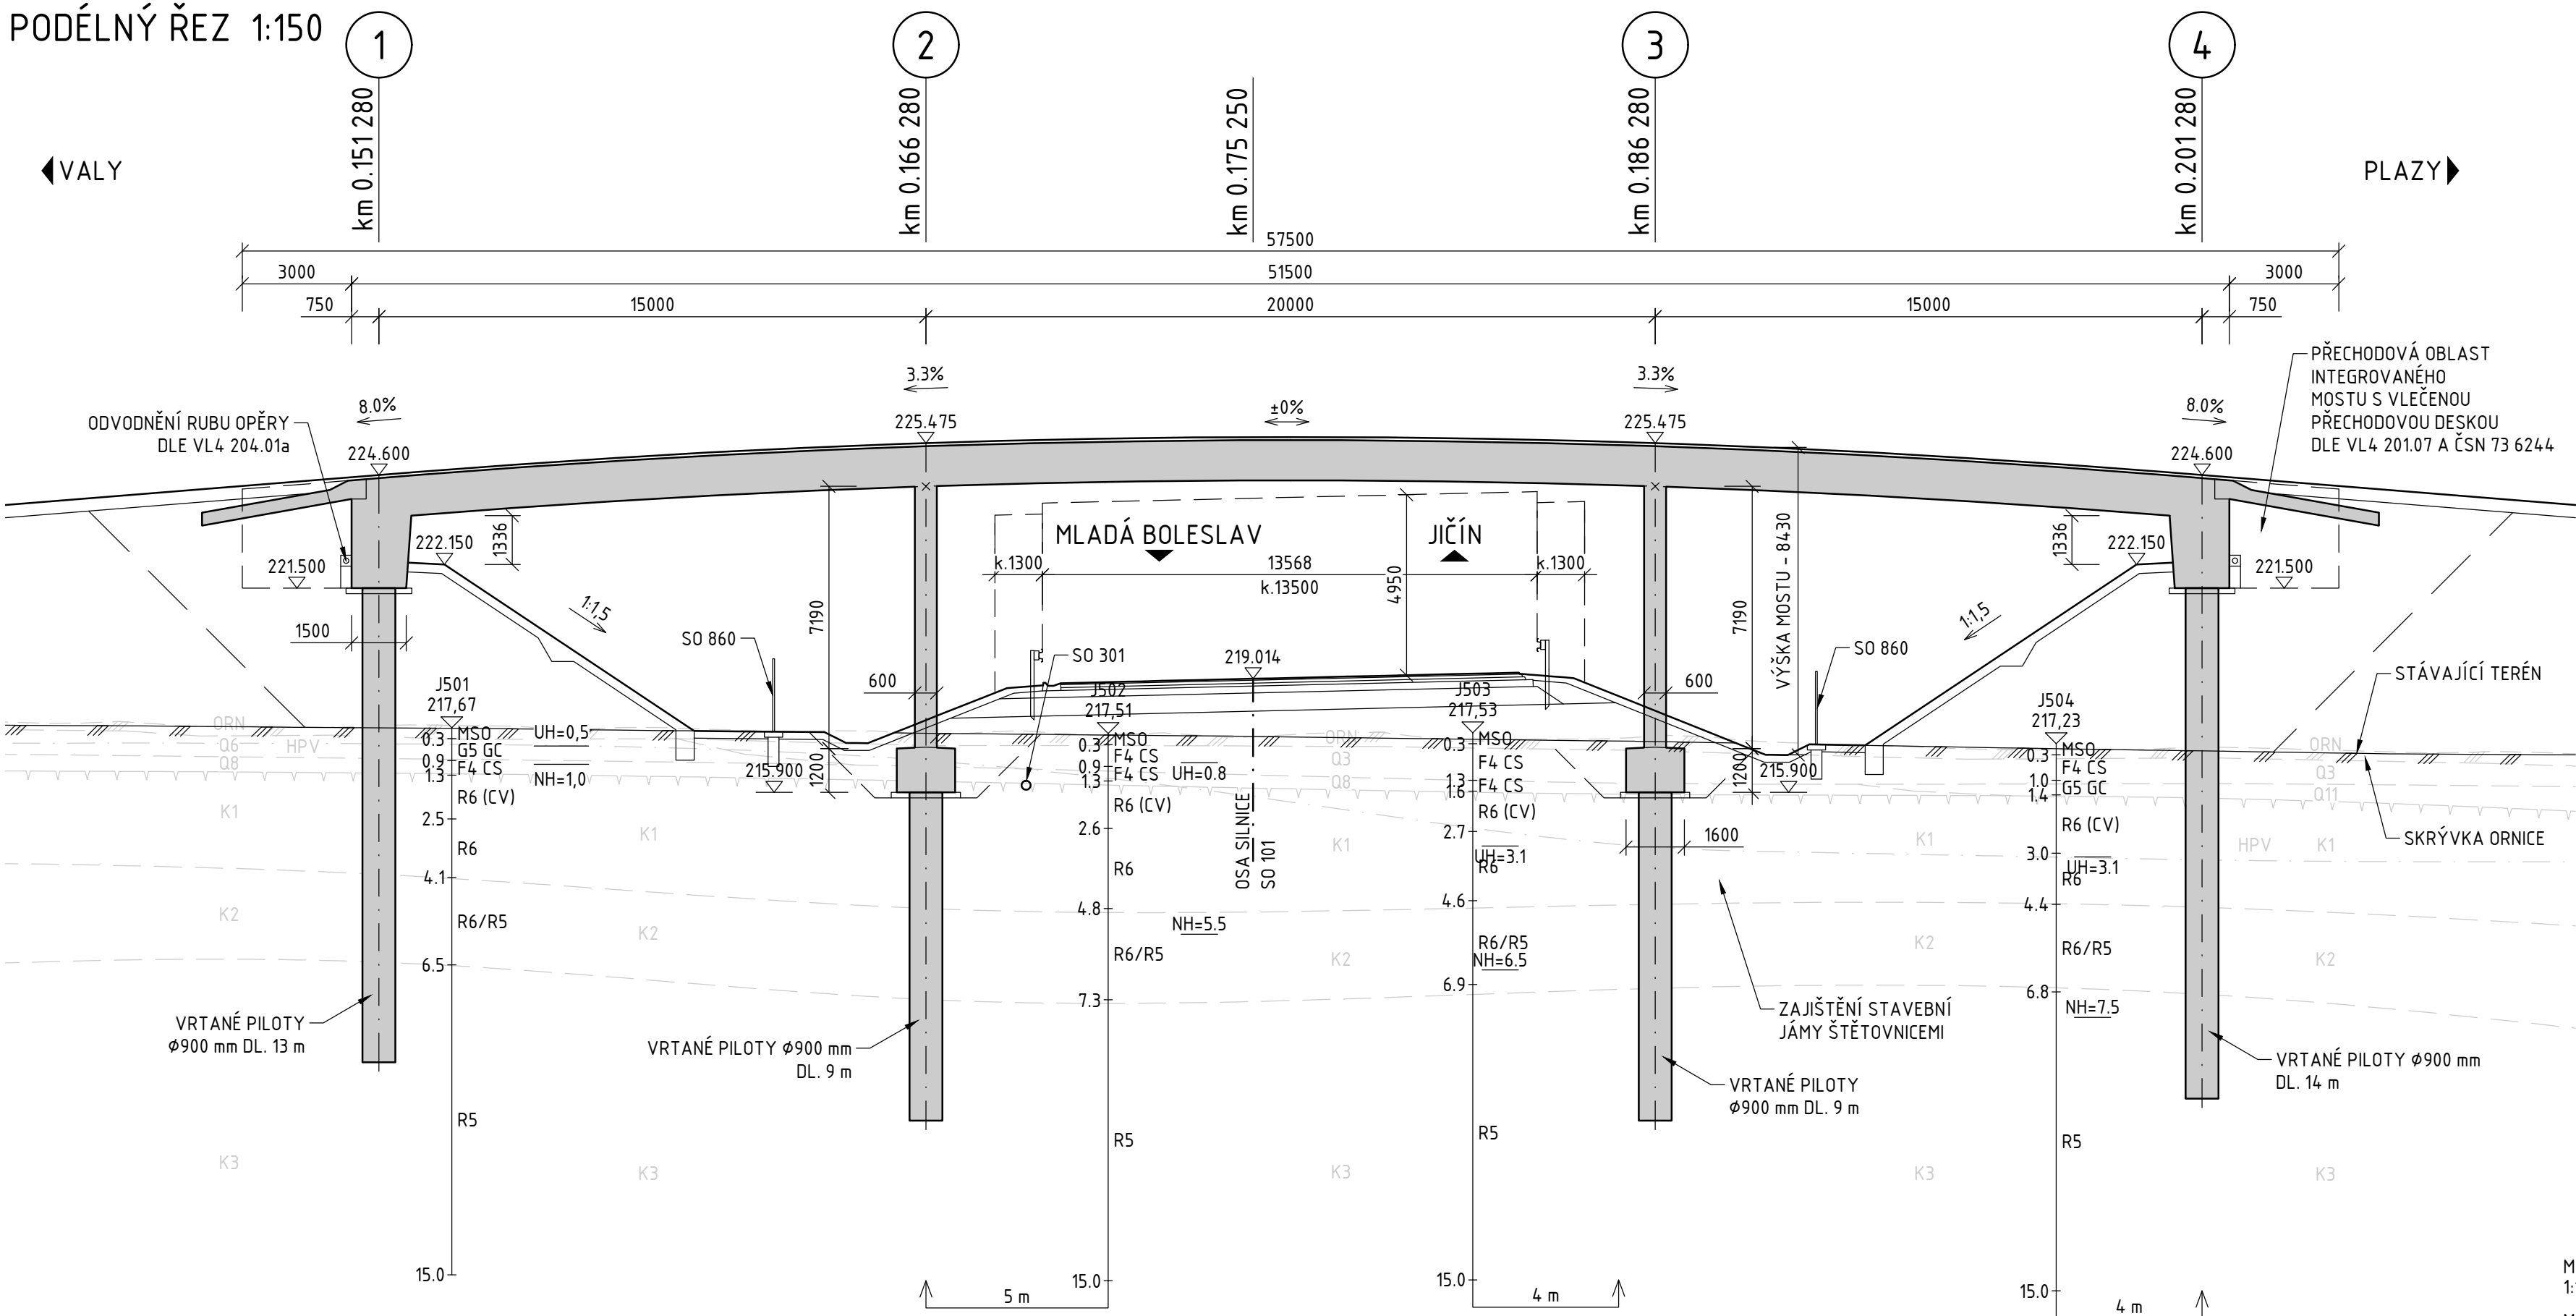

SMĚROVÉ VEDENÍ SO 130

STANIČENÍ	Y	X	PARAMETR
0.034 095	699387.863	1011284.316	PŘÍMÁ
0.328 270	699448.308	1011572.214	

VÝŠKOVÉ VEDENÍ SO 130

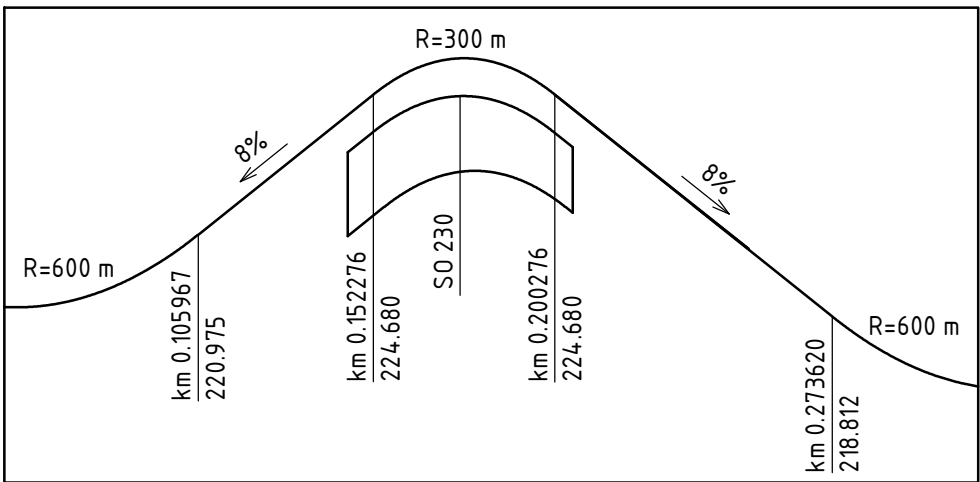

Souřadnicový systém: S-JTSK

Výškový systém: Bpv

SO 230 NADJEZD V km 1,713

Objednatel:



Ředitelství silnic a dálnic s. p.
Čerčanská 203/12, Krč, 140 00 Praha 4



Valbek, spol. s r.o.
Vaňurova 505/17
460 07 Liberec 3



Vypracoval: ING. A. HERASHCHANKA
Zodp. projektant: ING. A. HERASHCHANKA
Tech. kontrola: ING. I. BELDA
Akce: I/16 MLADÁ BOLESLAV - MARTINOVICE

Zak. číslo: 21-L113-001
Datum: 02/2025
Stupeň: PDPS
Počet formátů: 8 x A4
Měřítko: 1 : 150, 50
Č. přílohy: Paré

Zhotovitel:

Příloha: PŮDORYS, PODÉLNÝ ŘEZ
VZOROVÝ PŘÍČNÝ ŘEZ

102