



PILÍŘ 2
ŘEZ A-A 1:75

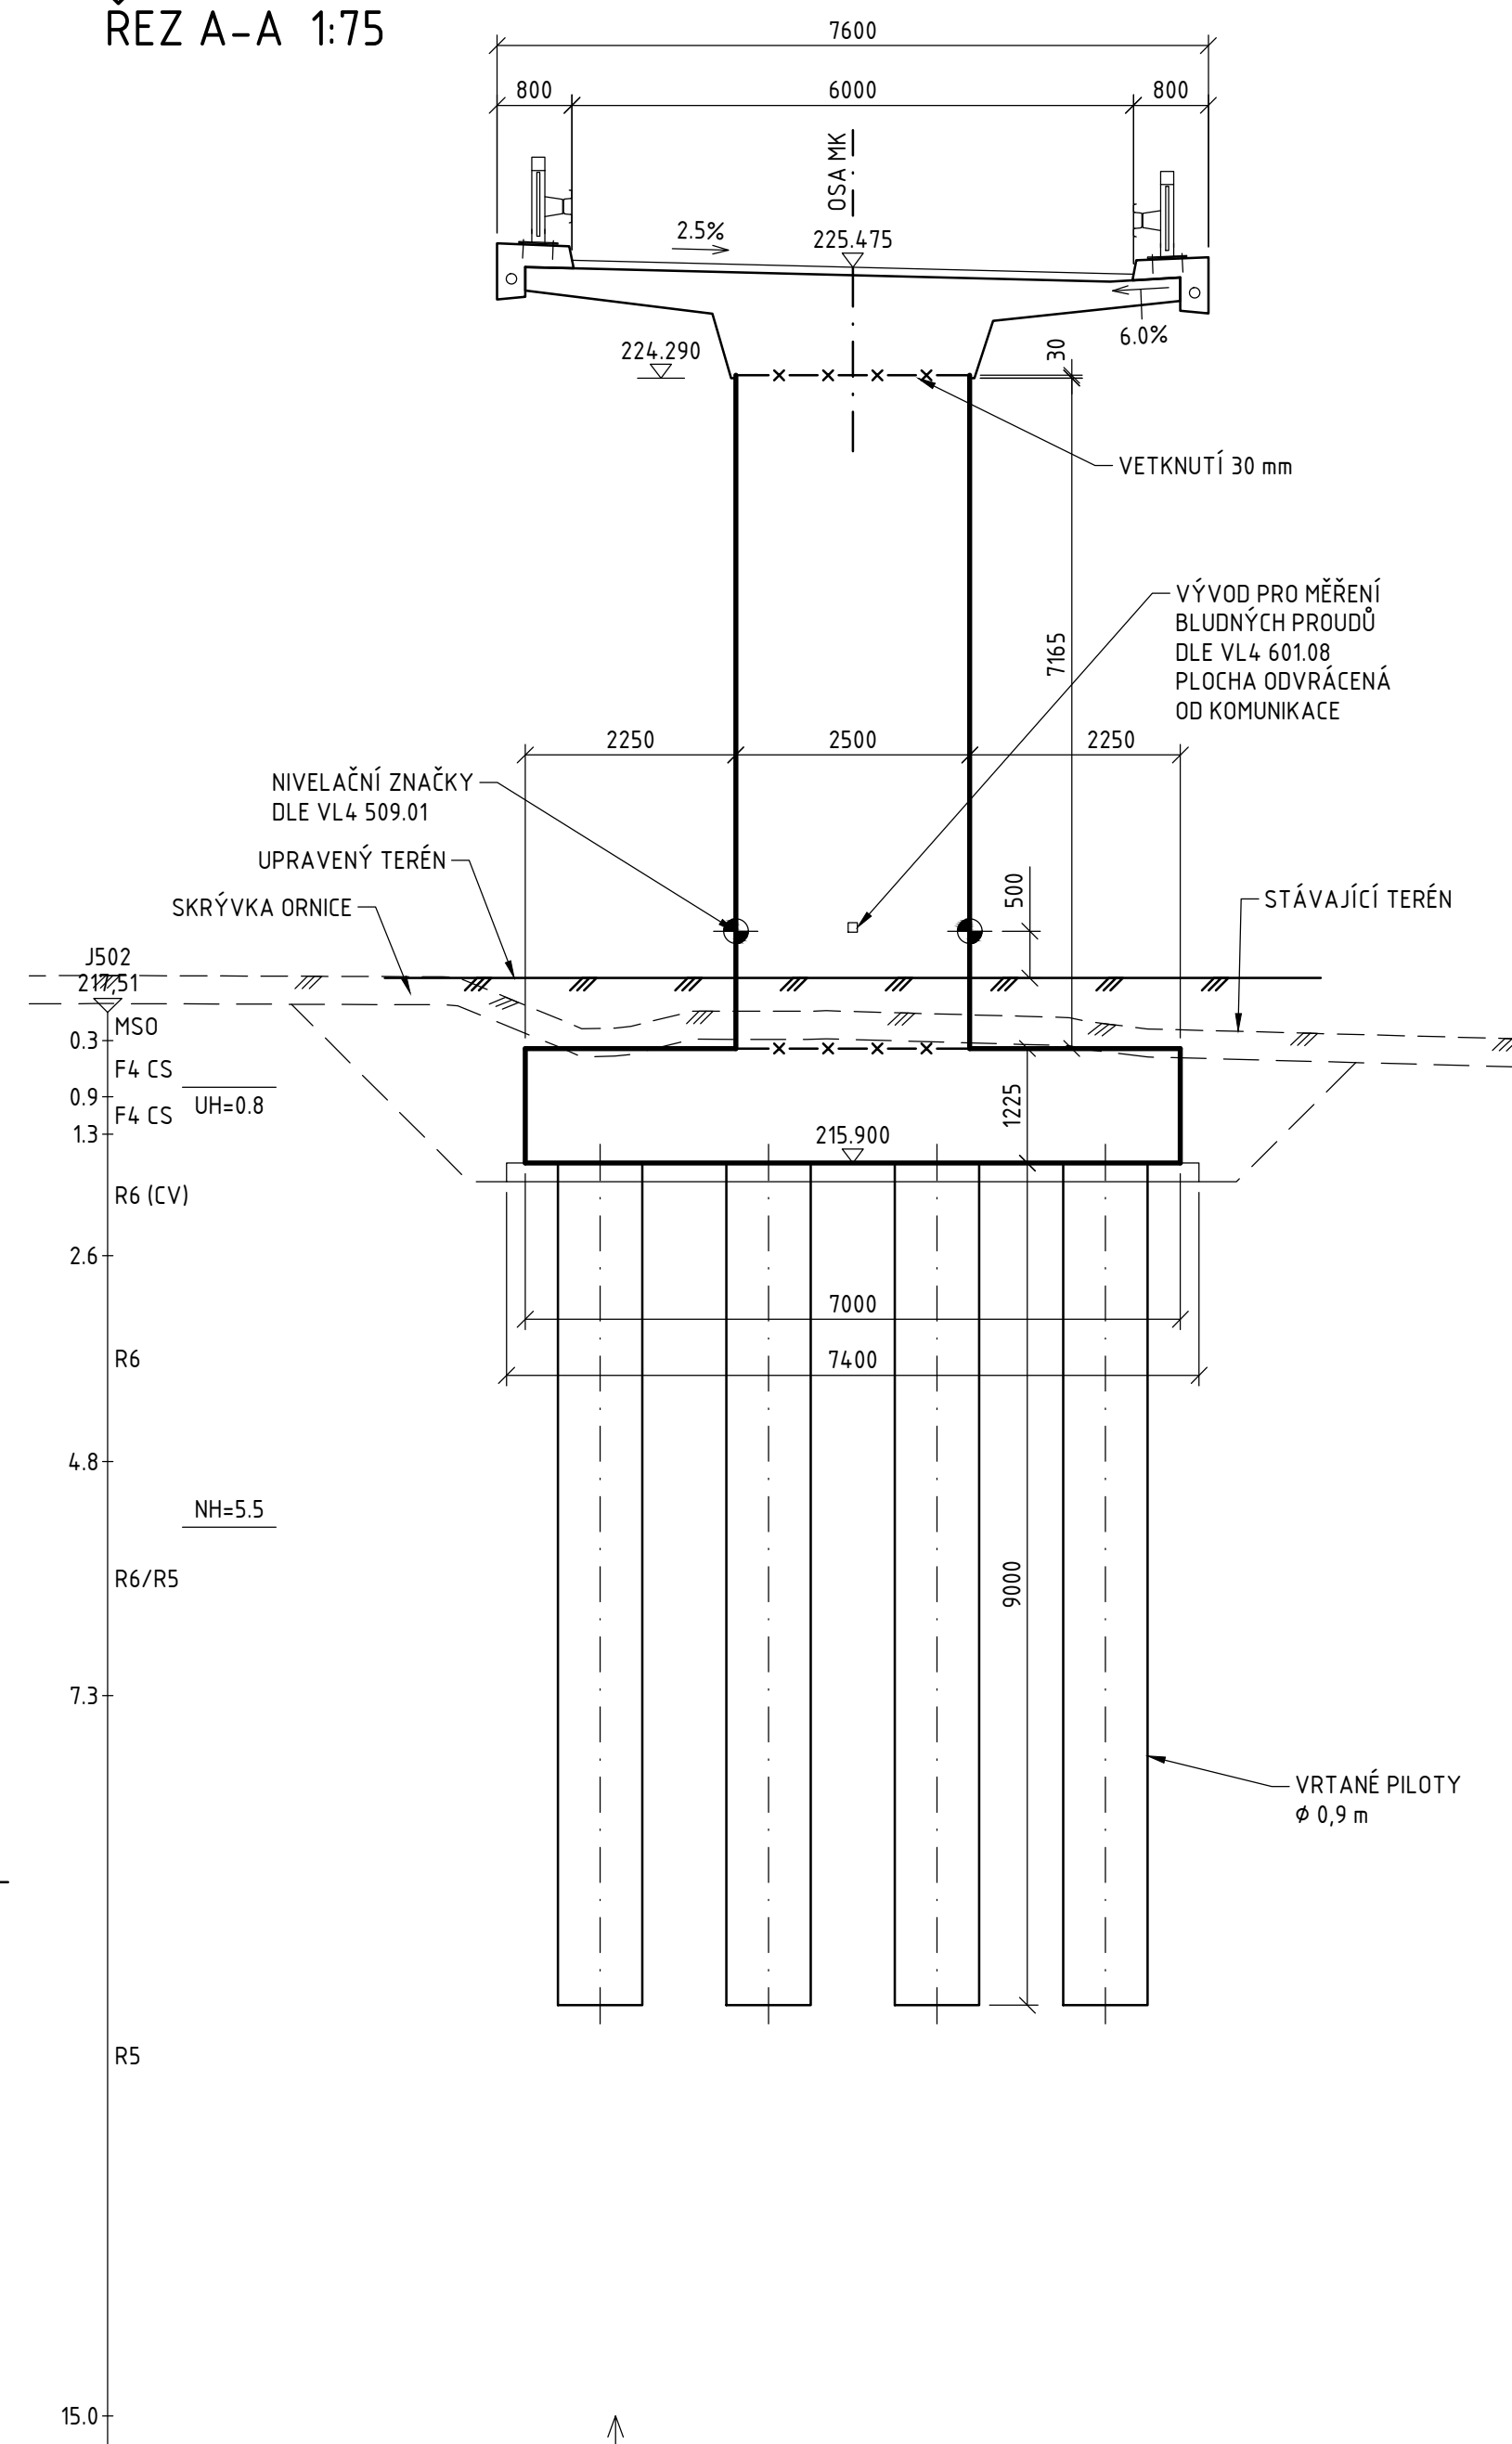


PILÍŘ 3
ŘEZ A-A 1:75

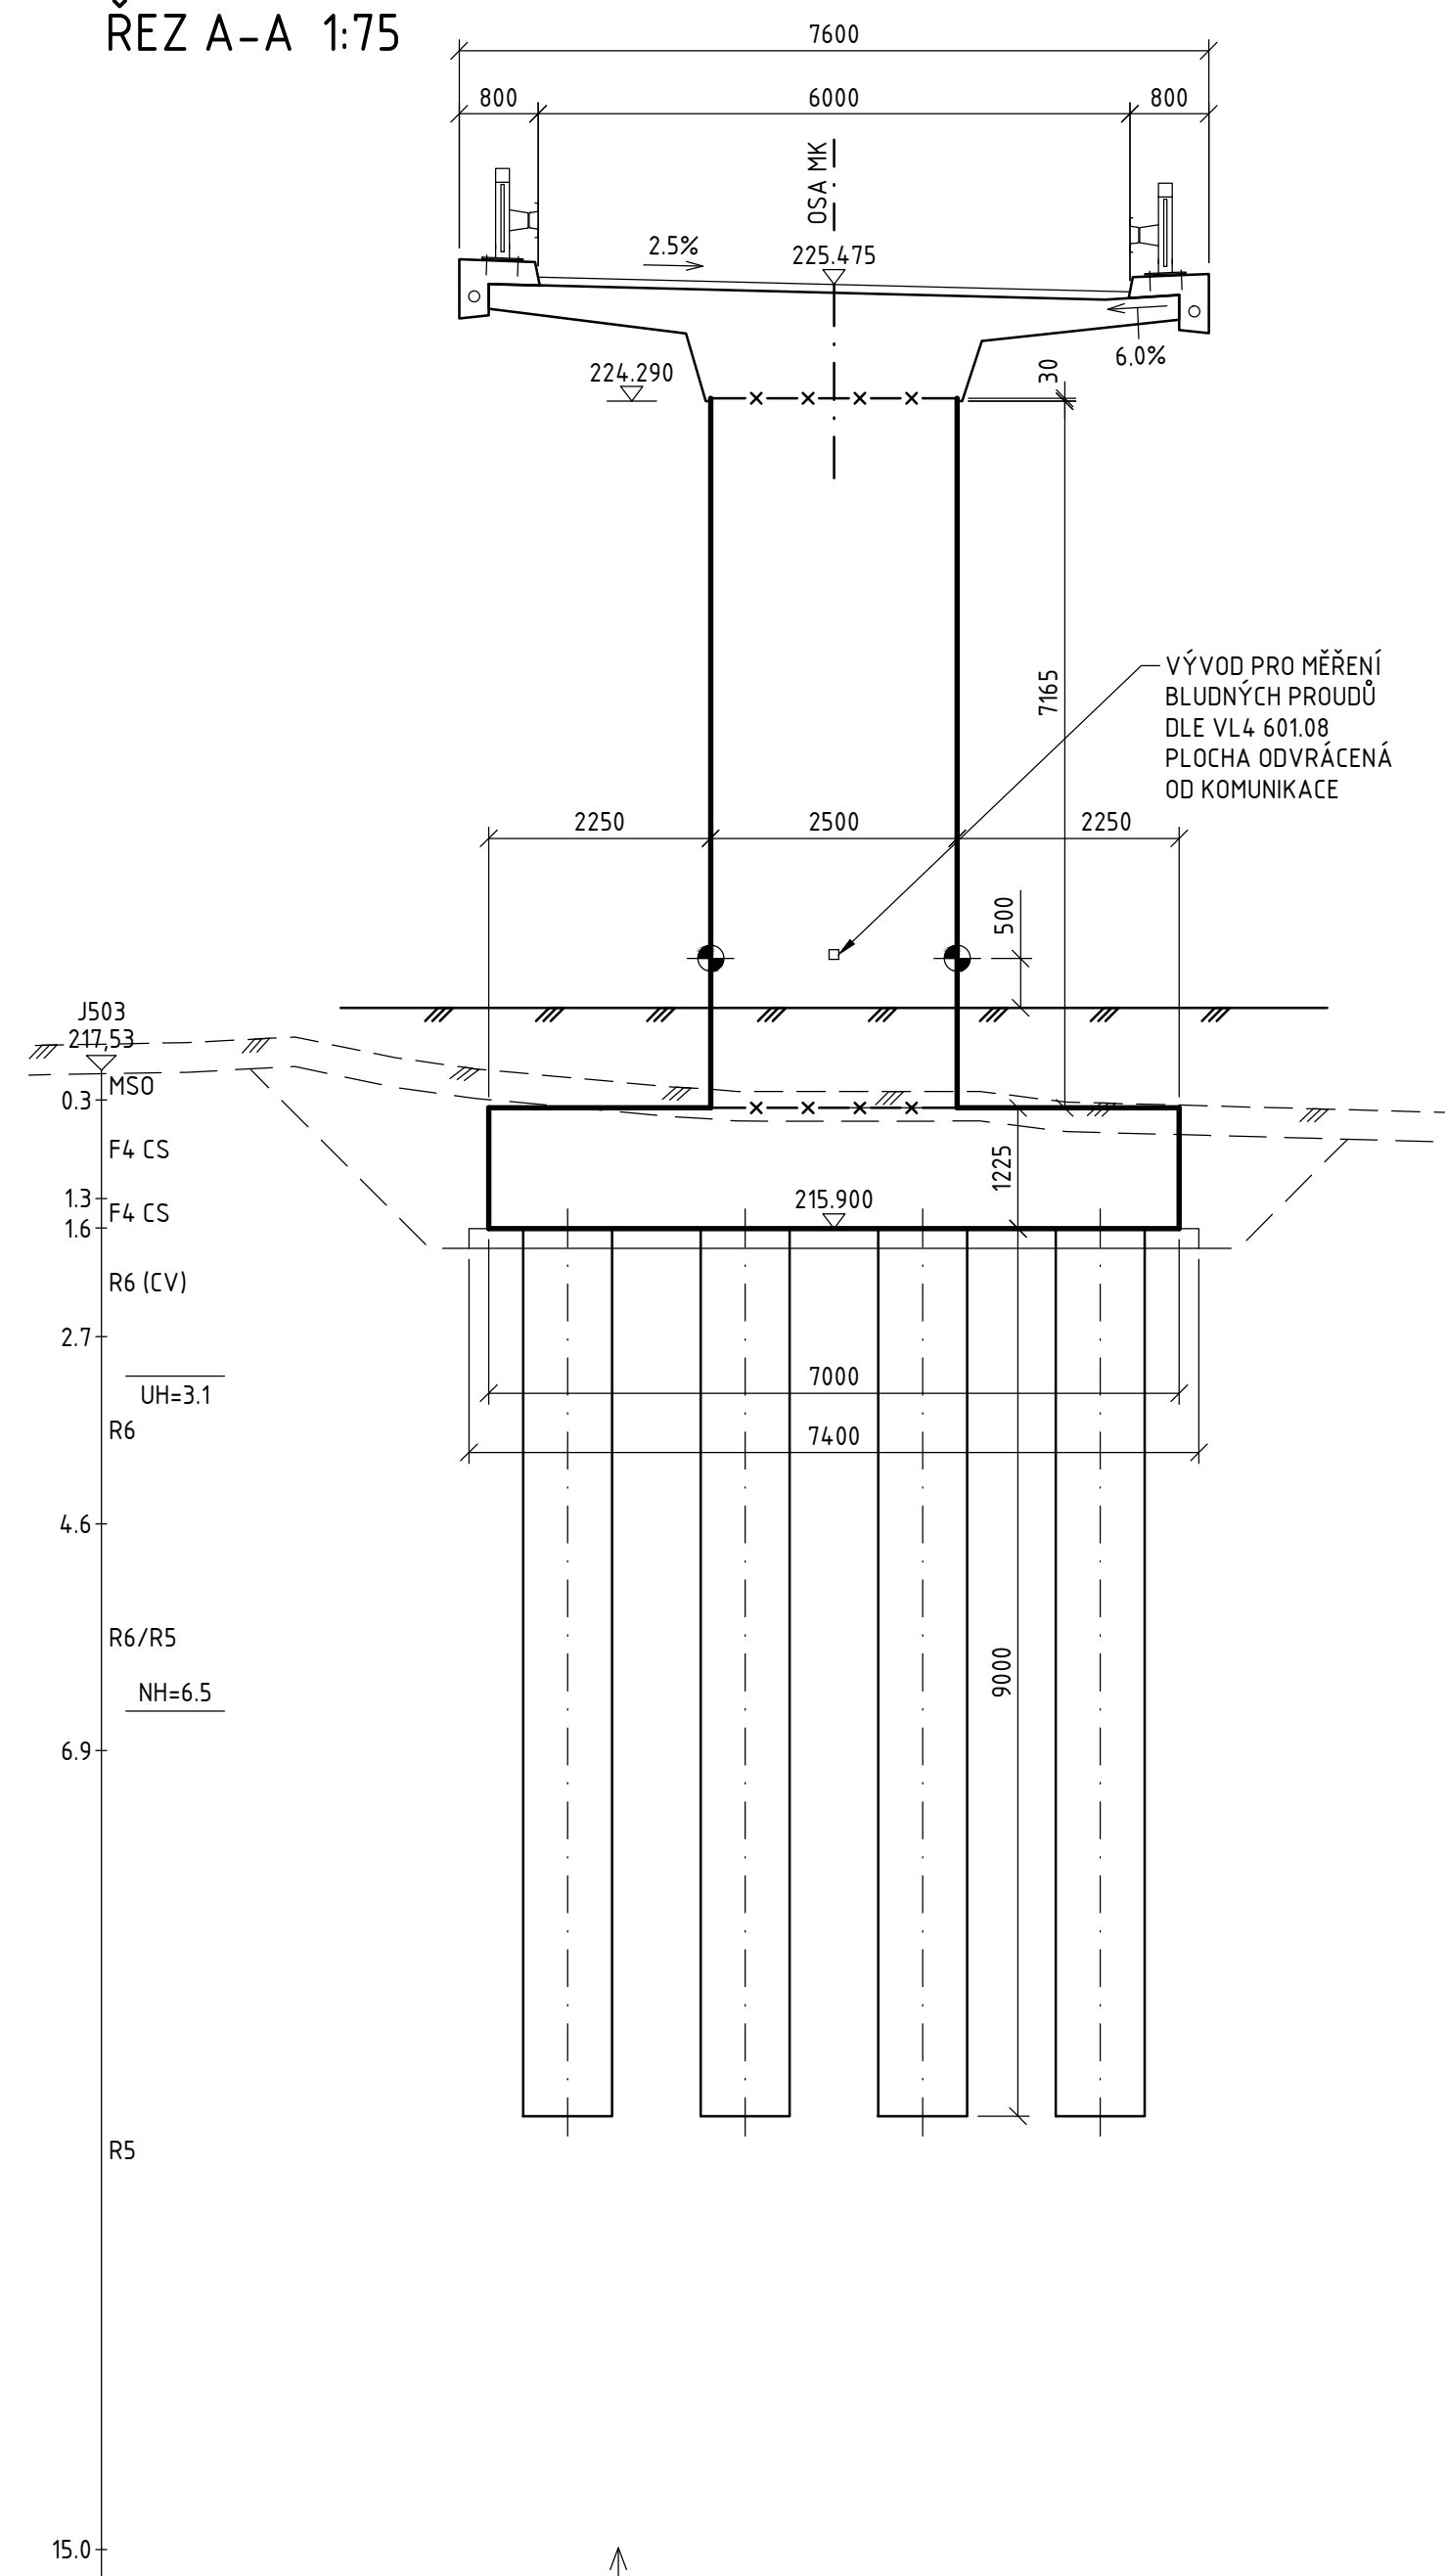


POHLED 1 1:75

KŘÍDLO 1

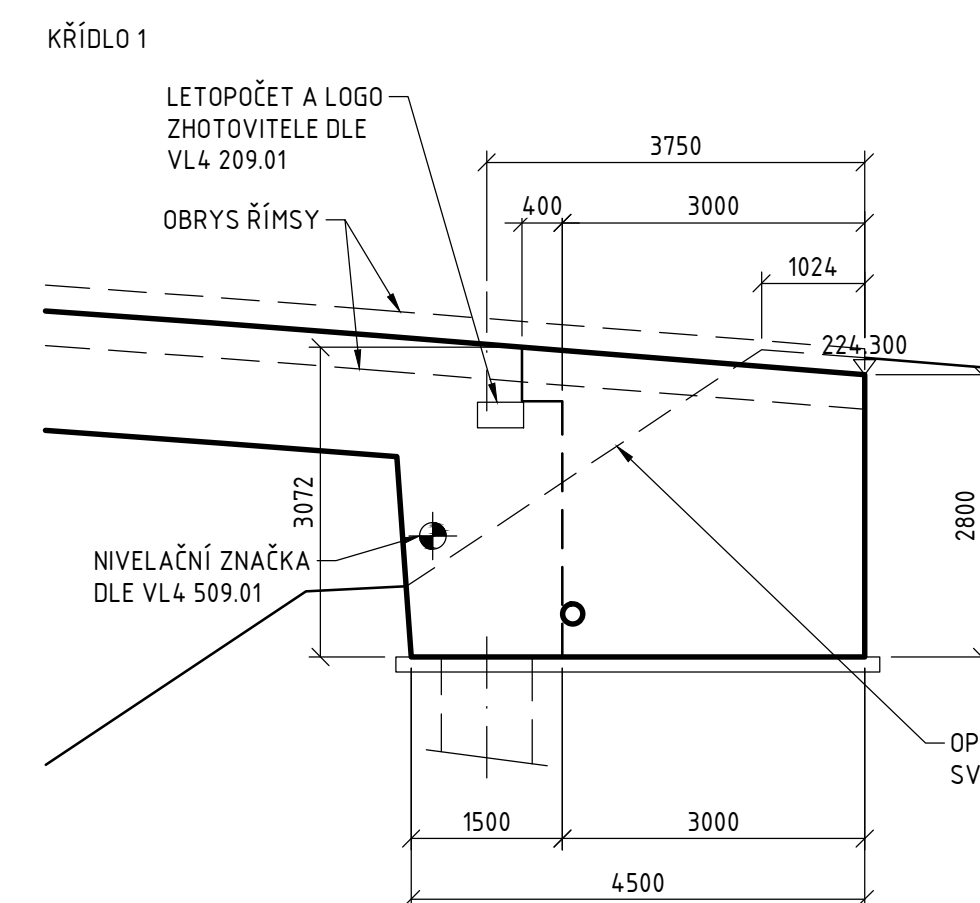


POHLED 2 1:75

KŘÍDLO 2

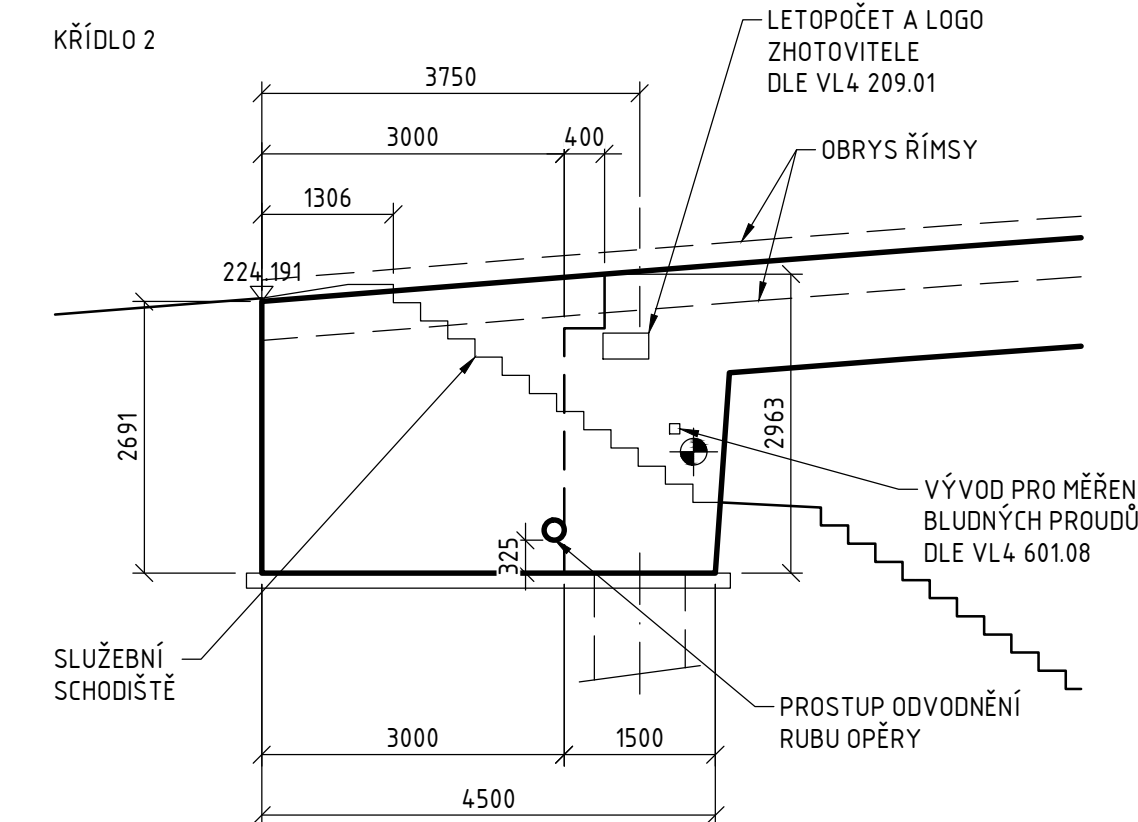


POHLED 3 1:75

KŘÍDLO 3

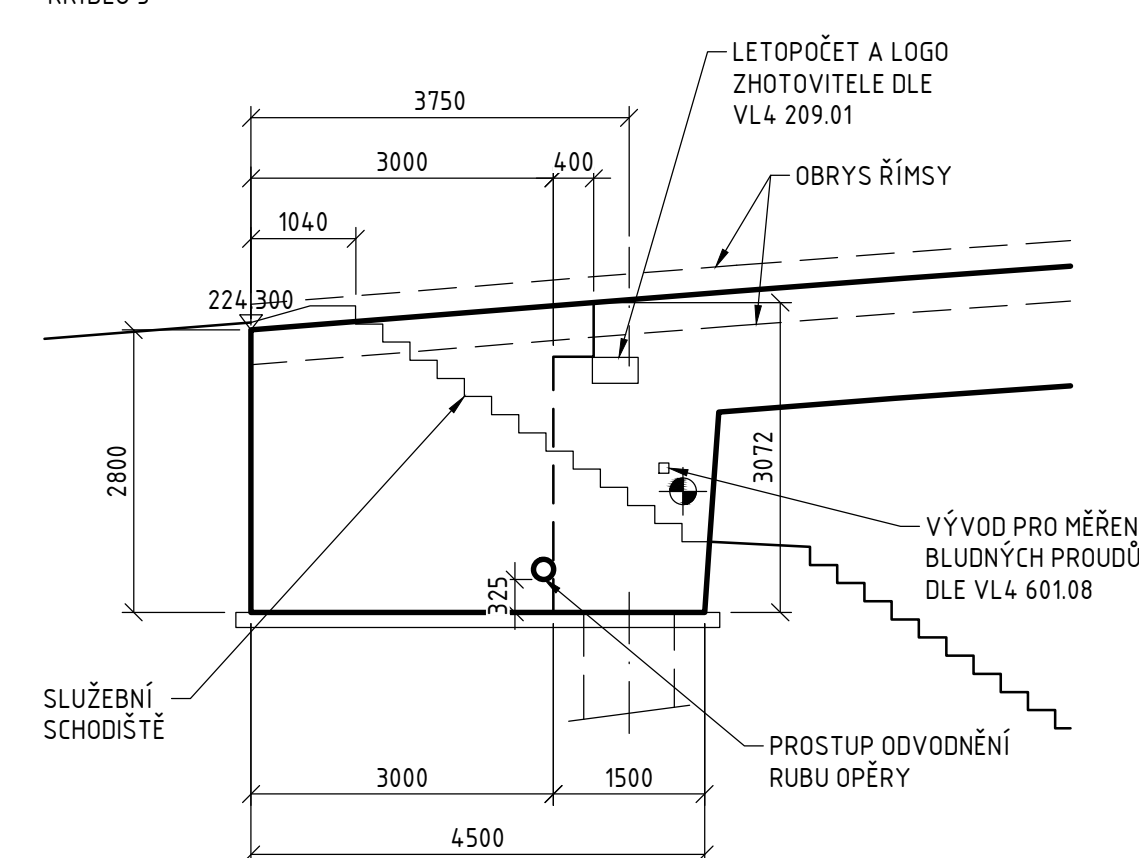


POHLED 4 1:75


KŘÍDLO 4

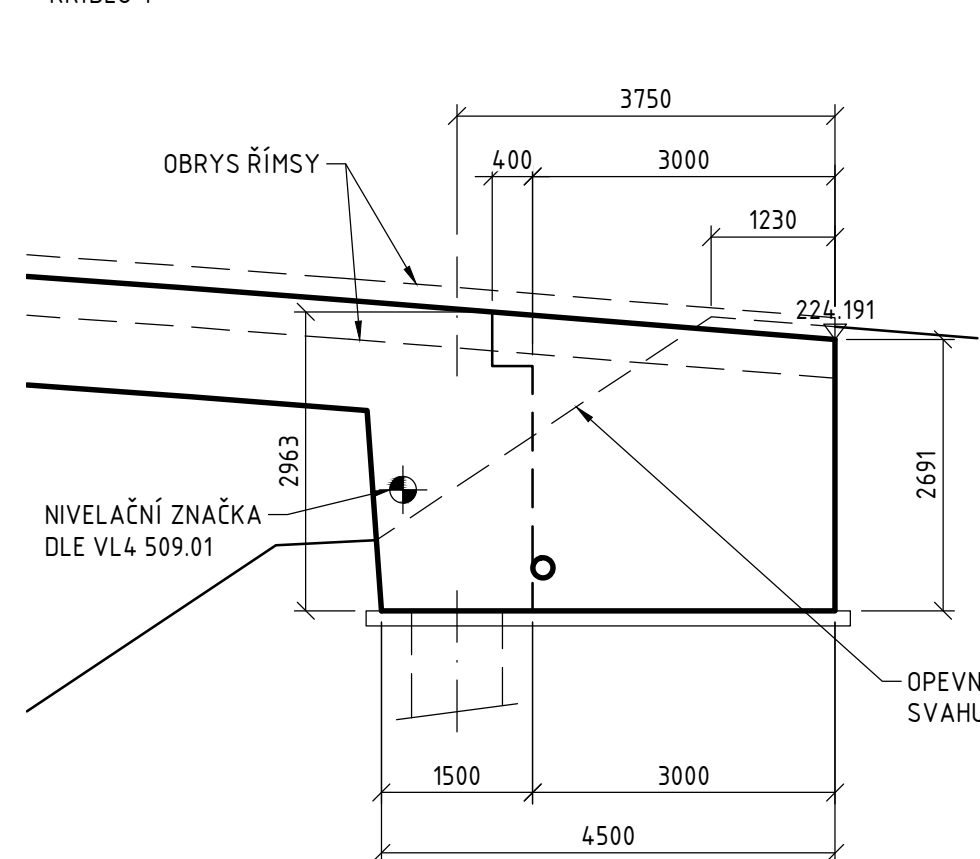


PILÍŘ 2
ŘEZ B - B 1:75

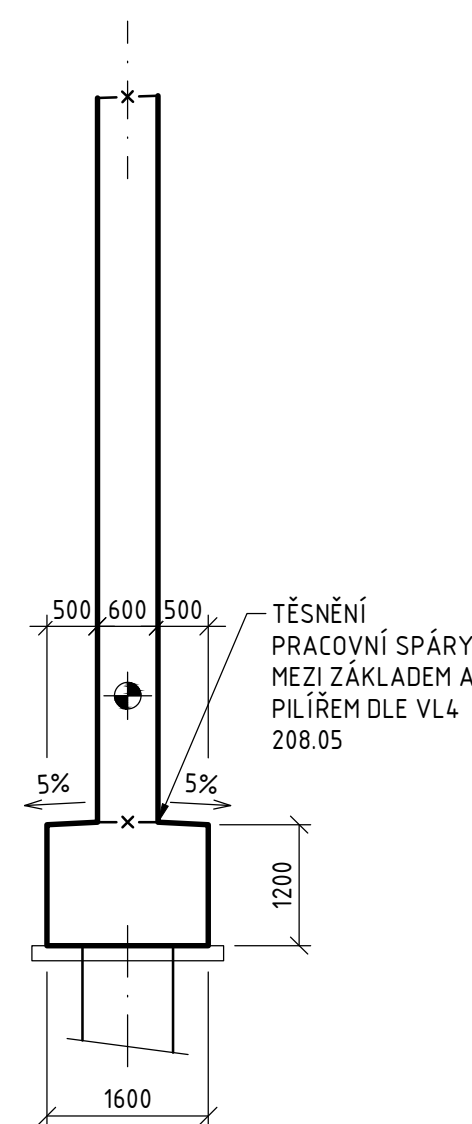


PILÍŘ 3
ŘEZ B – B 1:75

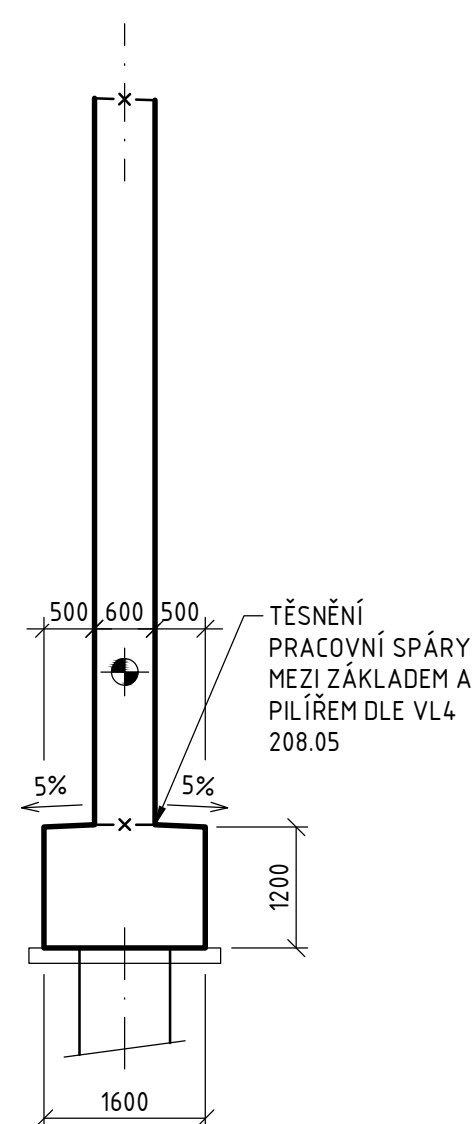


PILÍŘE 2, 3
PŮDORYS ZÁKLADU 1:75

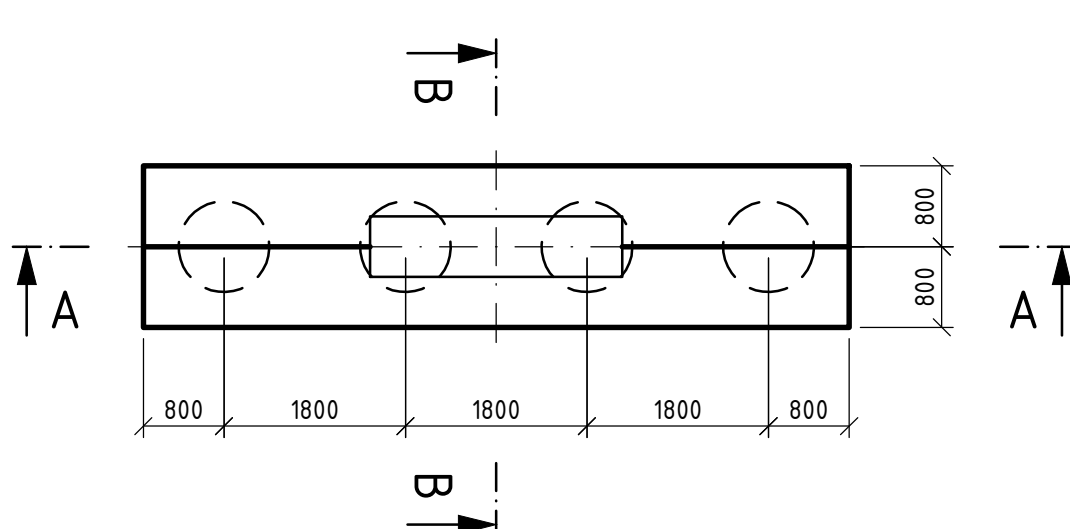


PILÍŘE 2, 3
ŘEZ STOJKOU 1:50

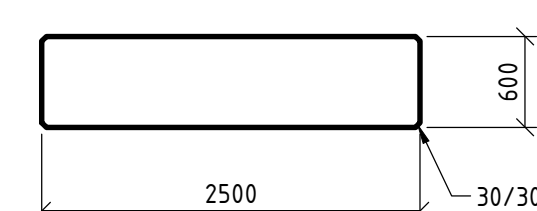


ŘEZ KŘÍDLEM 1
1:75

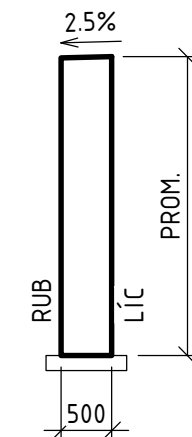



ŘEZ KŘÍDLEM 2
1:75

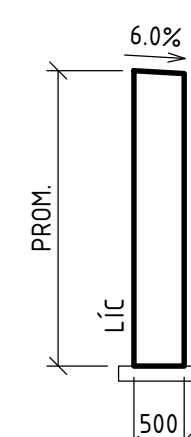

ŘEZ KŘÍDLEM 3
1:75

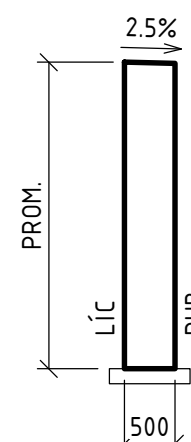

ŘEZ KŘÍDLEM 4
1:75

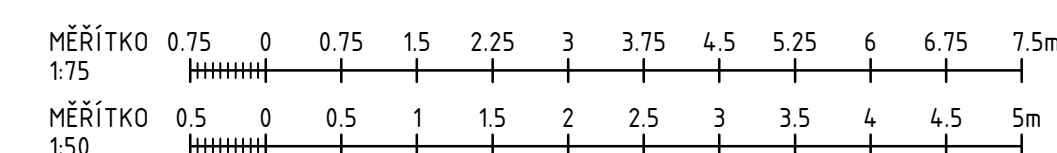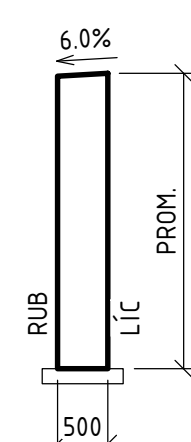

POZNÁMKY

- NEDÍLNOU SOUČÁSTÍ VÝKRESU JSOU TECHNICKÉ SPECIFIKACE A POZNÁMKY UVEDENÉ NA VÝKRESE TECHNICKÝCH SPECIFIKACÍ A POZNÁMEK;

Souřadnicový systém: S-JTSK
Výškový systém: Bpv

SO 230 NADJEZD V km 1,713


Objednatel:



Ředitelství silnic a dálnic s. p.
Čerčanská 2023/12, Krč, 140 00 Praha 4



Valbek, spol. s r.o.
Vaňurova 505/17
460 07 Liberec 3

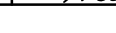	Vypracoval	D. MALIK		Zak. číslo	21-L14-0013
	Zodp. projektant	ING. A. HERASCHCHANKA		Datum	02/2025
	Tech. kontrola	ING. I. BELDA		Stupeň	PDPS
	Akce			Počet formátů	8 x A4
	I/16 MLADÁ BOLESLAV - MARTINOVICE			Měřítko	1 : 75, 50
				Č. přílohy	Paré
Zhotovitel: Valbek, spol. s r.o. Václavova 305/17 460 07 Liberec 3	Příloha	PRÍČNÉ REZY, HLUBINNÉ ZALOŽENÍ 1(2), TVAR SPODNÍ STAVBY			201