



TVAR ŘÍMS

PŮDORYS 1:100

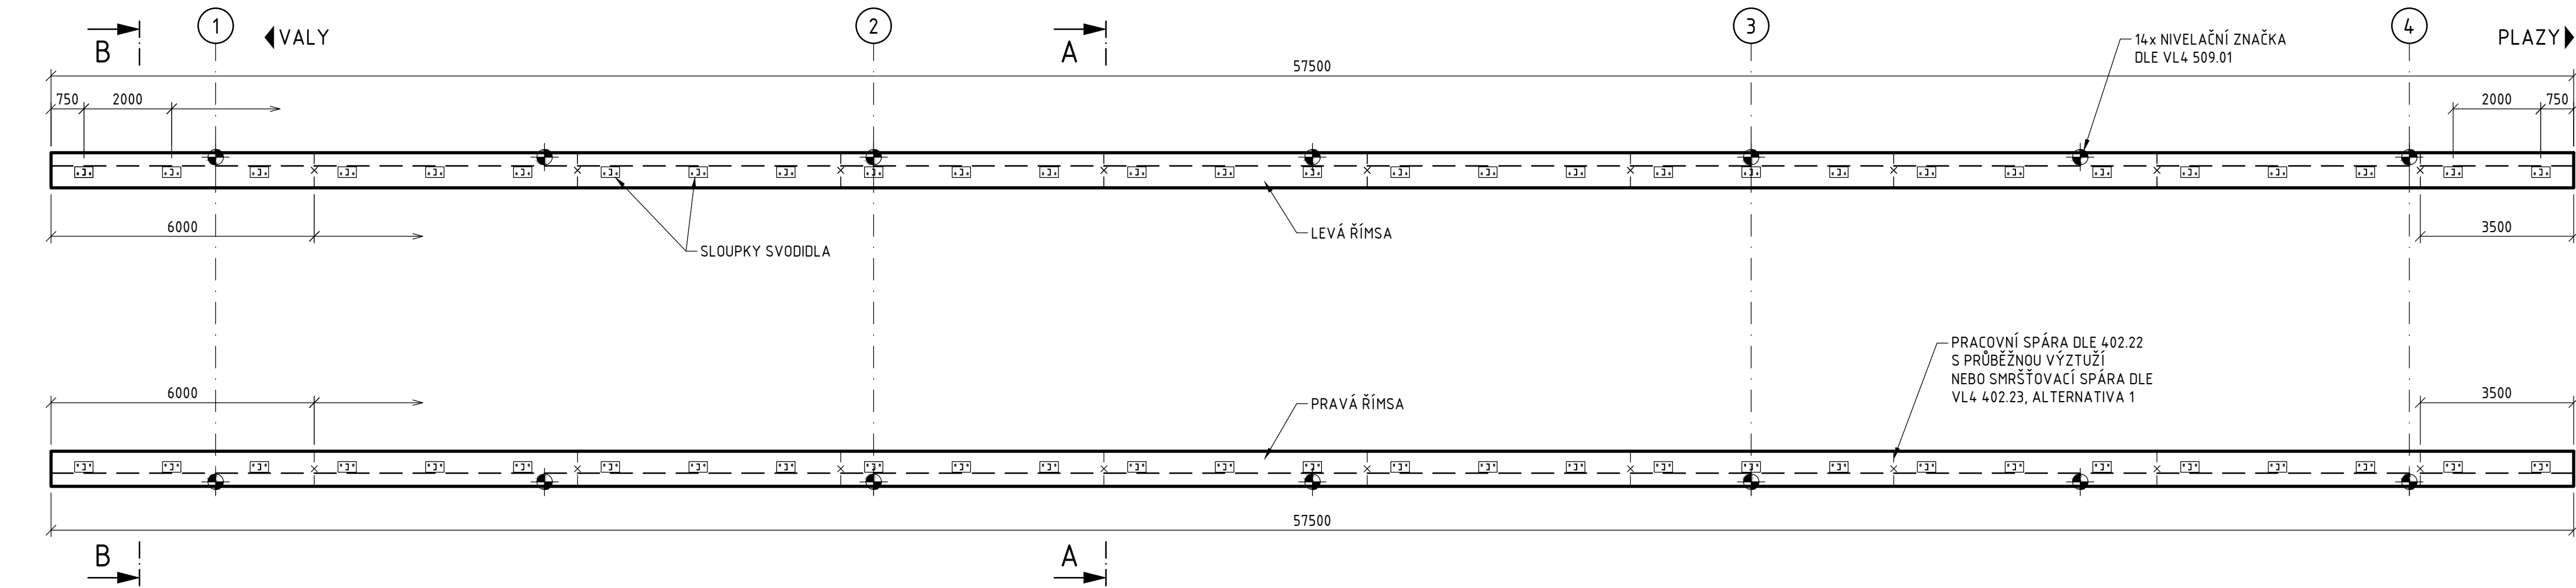

ŘEZ A-A 1:20

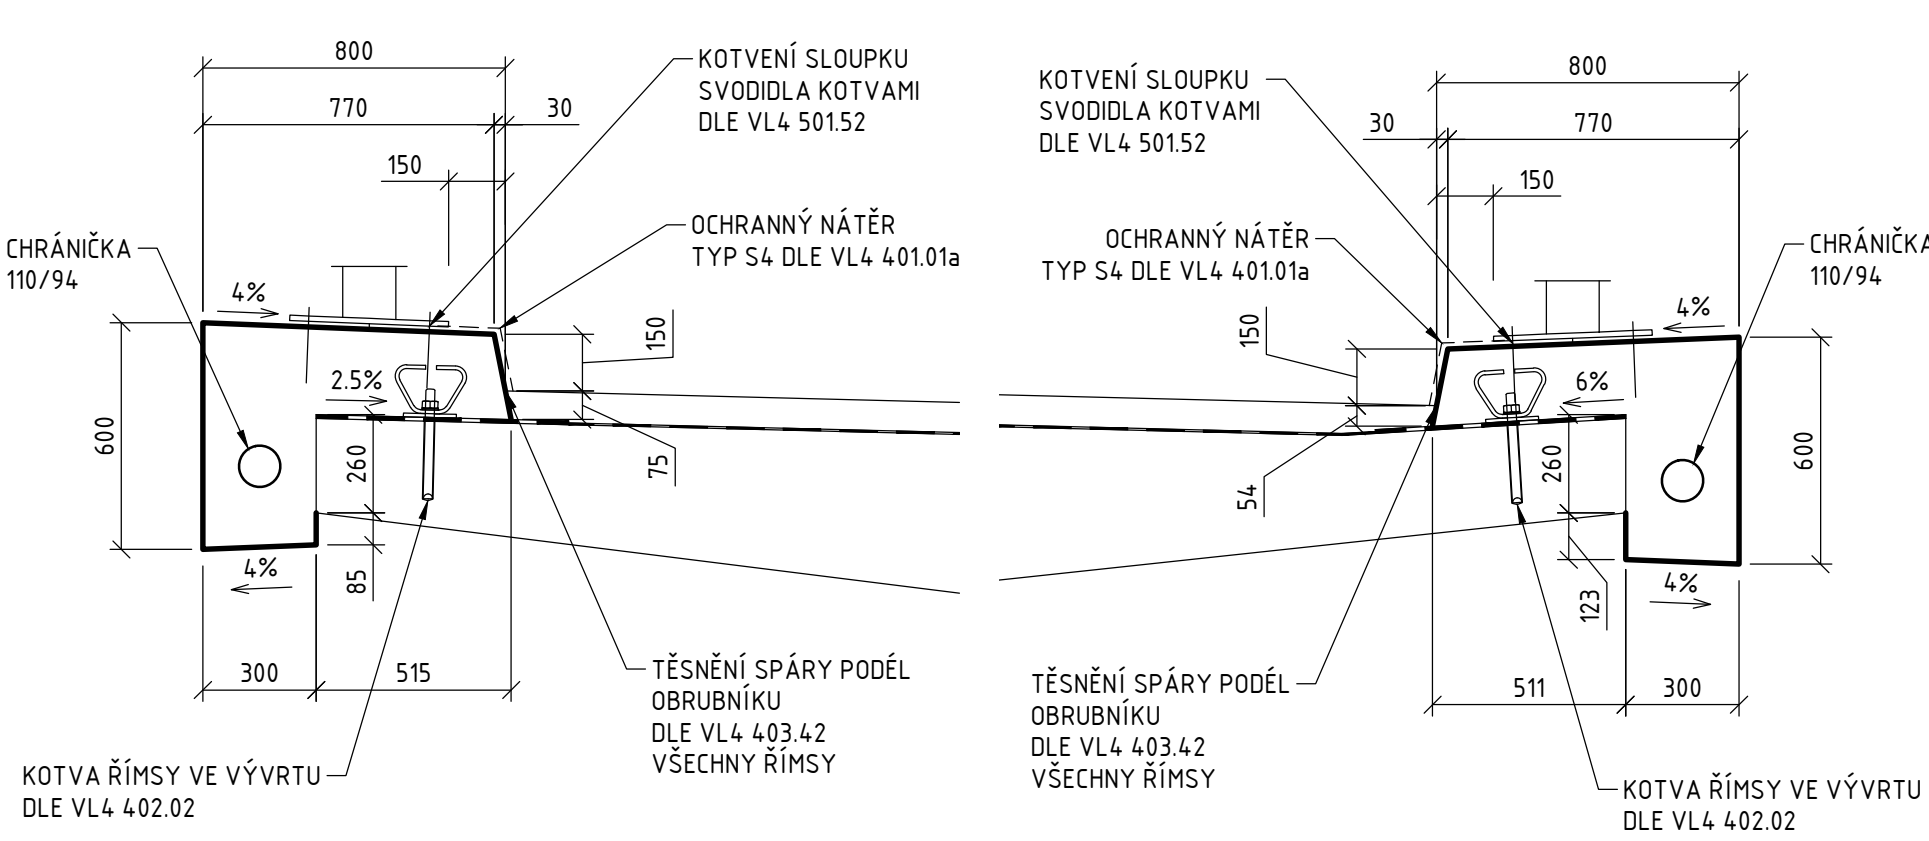

ŘEZ B-B 1:20



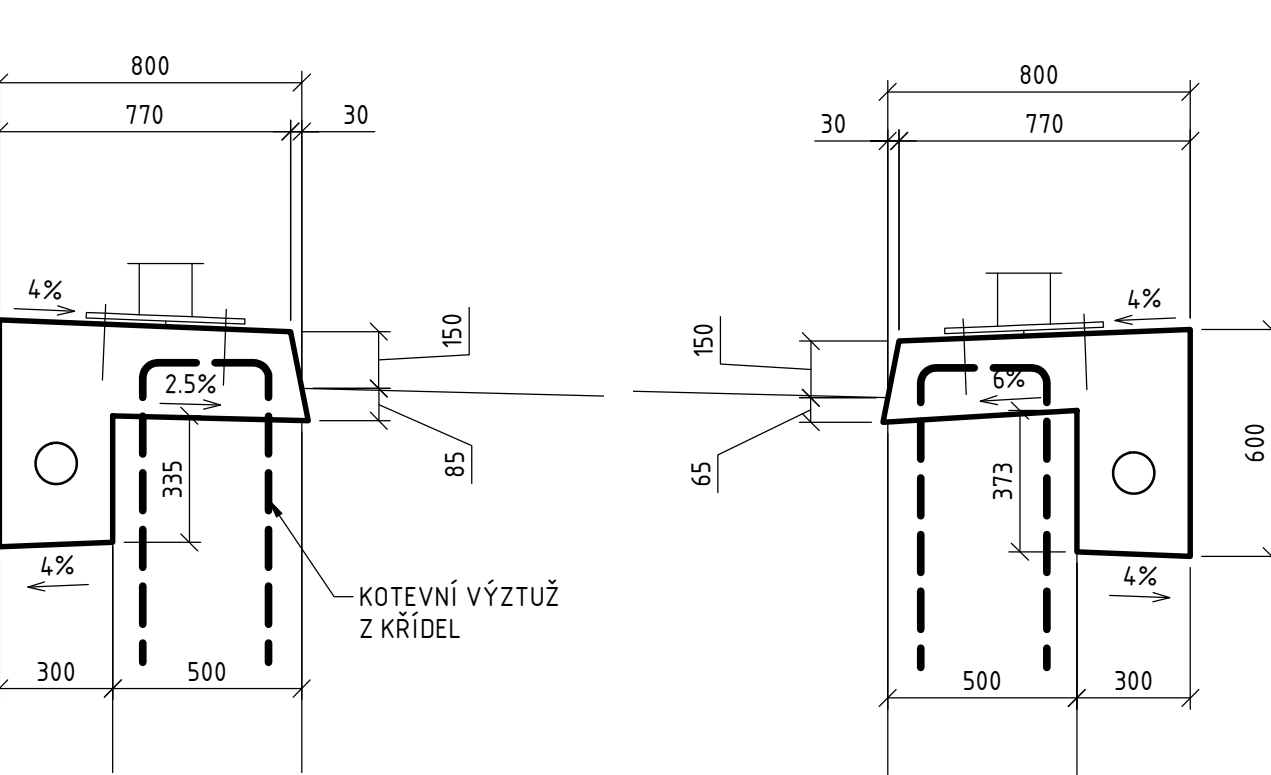


SCHÉMA ODVODNĚNÍ

PODÉLNÝ ŘEZ 1:100

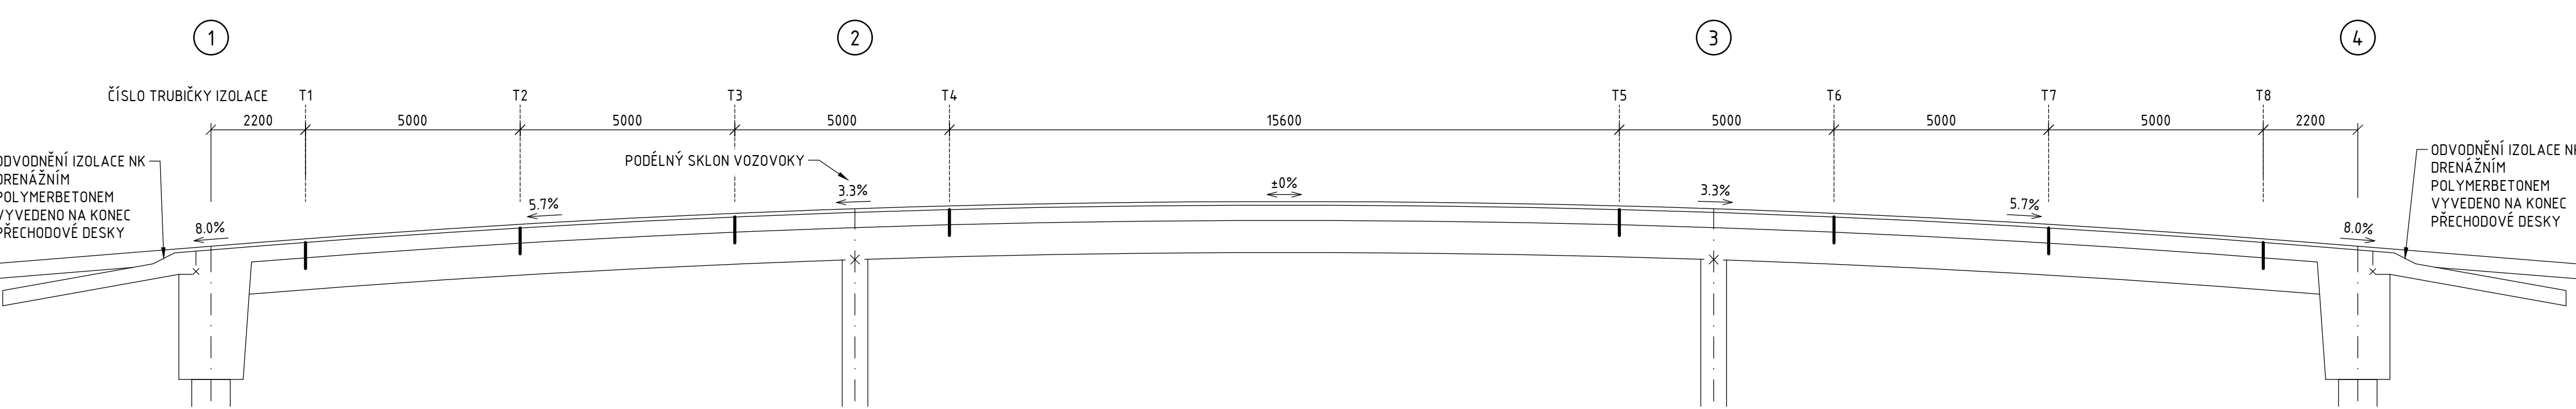

PŘÍČNÝ ŘEZ 1:50

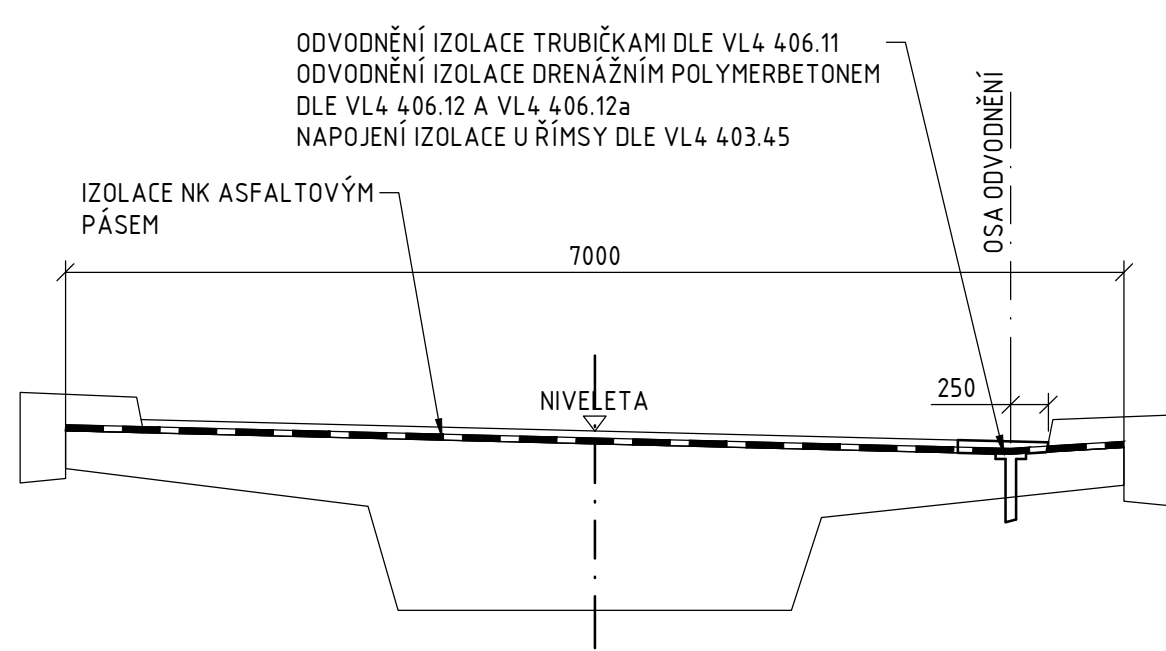

POZNÁMKY



- NEDÍLNOU SOUČÁSTÍ VÝKRESU JSOU TECHNICKÉ SPECIFIKACE A POZNÁMKY UVEDENÉ NA VÝKRESE TECHNICKÝCH SPECIFIKACÍ A POZNÁMEK;

Souřadnicový systém: S-JTSK
Výškový systém: Bpv

SO 230 NADJEZD V km 1,713

Objednatel: **ŘEDITELSTVÍ SILNIC A DÁLNIC**
Ředitelství silnic a dálnic s. p.
Čerčanská 2023/12, Krč, 140 00 Praha 4

Valbek, spol. s r.o.
Vaňurova 505/17
460 07 Liberec 3

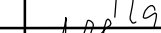 	Vypracoval	D. MALÍK		Zak. číslo	21-L113-001	
	Zodp. projektant	ING. A. HERASHCHANKA		Datum	02/2025	
	Tech. kontrola	ING. I. BELDA		Stupeň	PDPS	
	Akce	I/16 MLADÁ BOLESLAV - MARTINOVICE			Počet formátů	8 x A4
	Zhotovitel: Valbek, spol. s r.o. Vaňurova 505/17 460 07 Liberec 3	Příloha	TVAR ŘÍMS, SCHÉMA ODVODNĚNÍ	Měřítko	1 : 100, 50, 20	Paré
Č. přílohy						
				203		

