




PŮDORYS 1:150

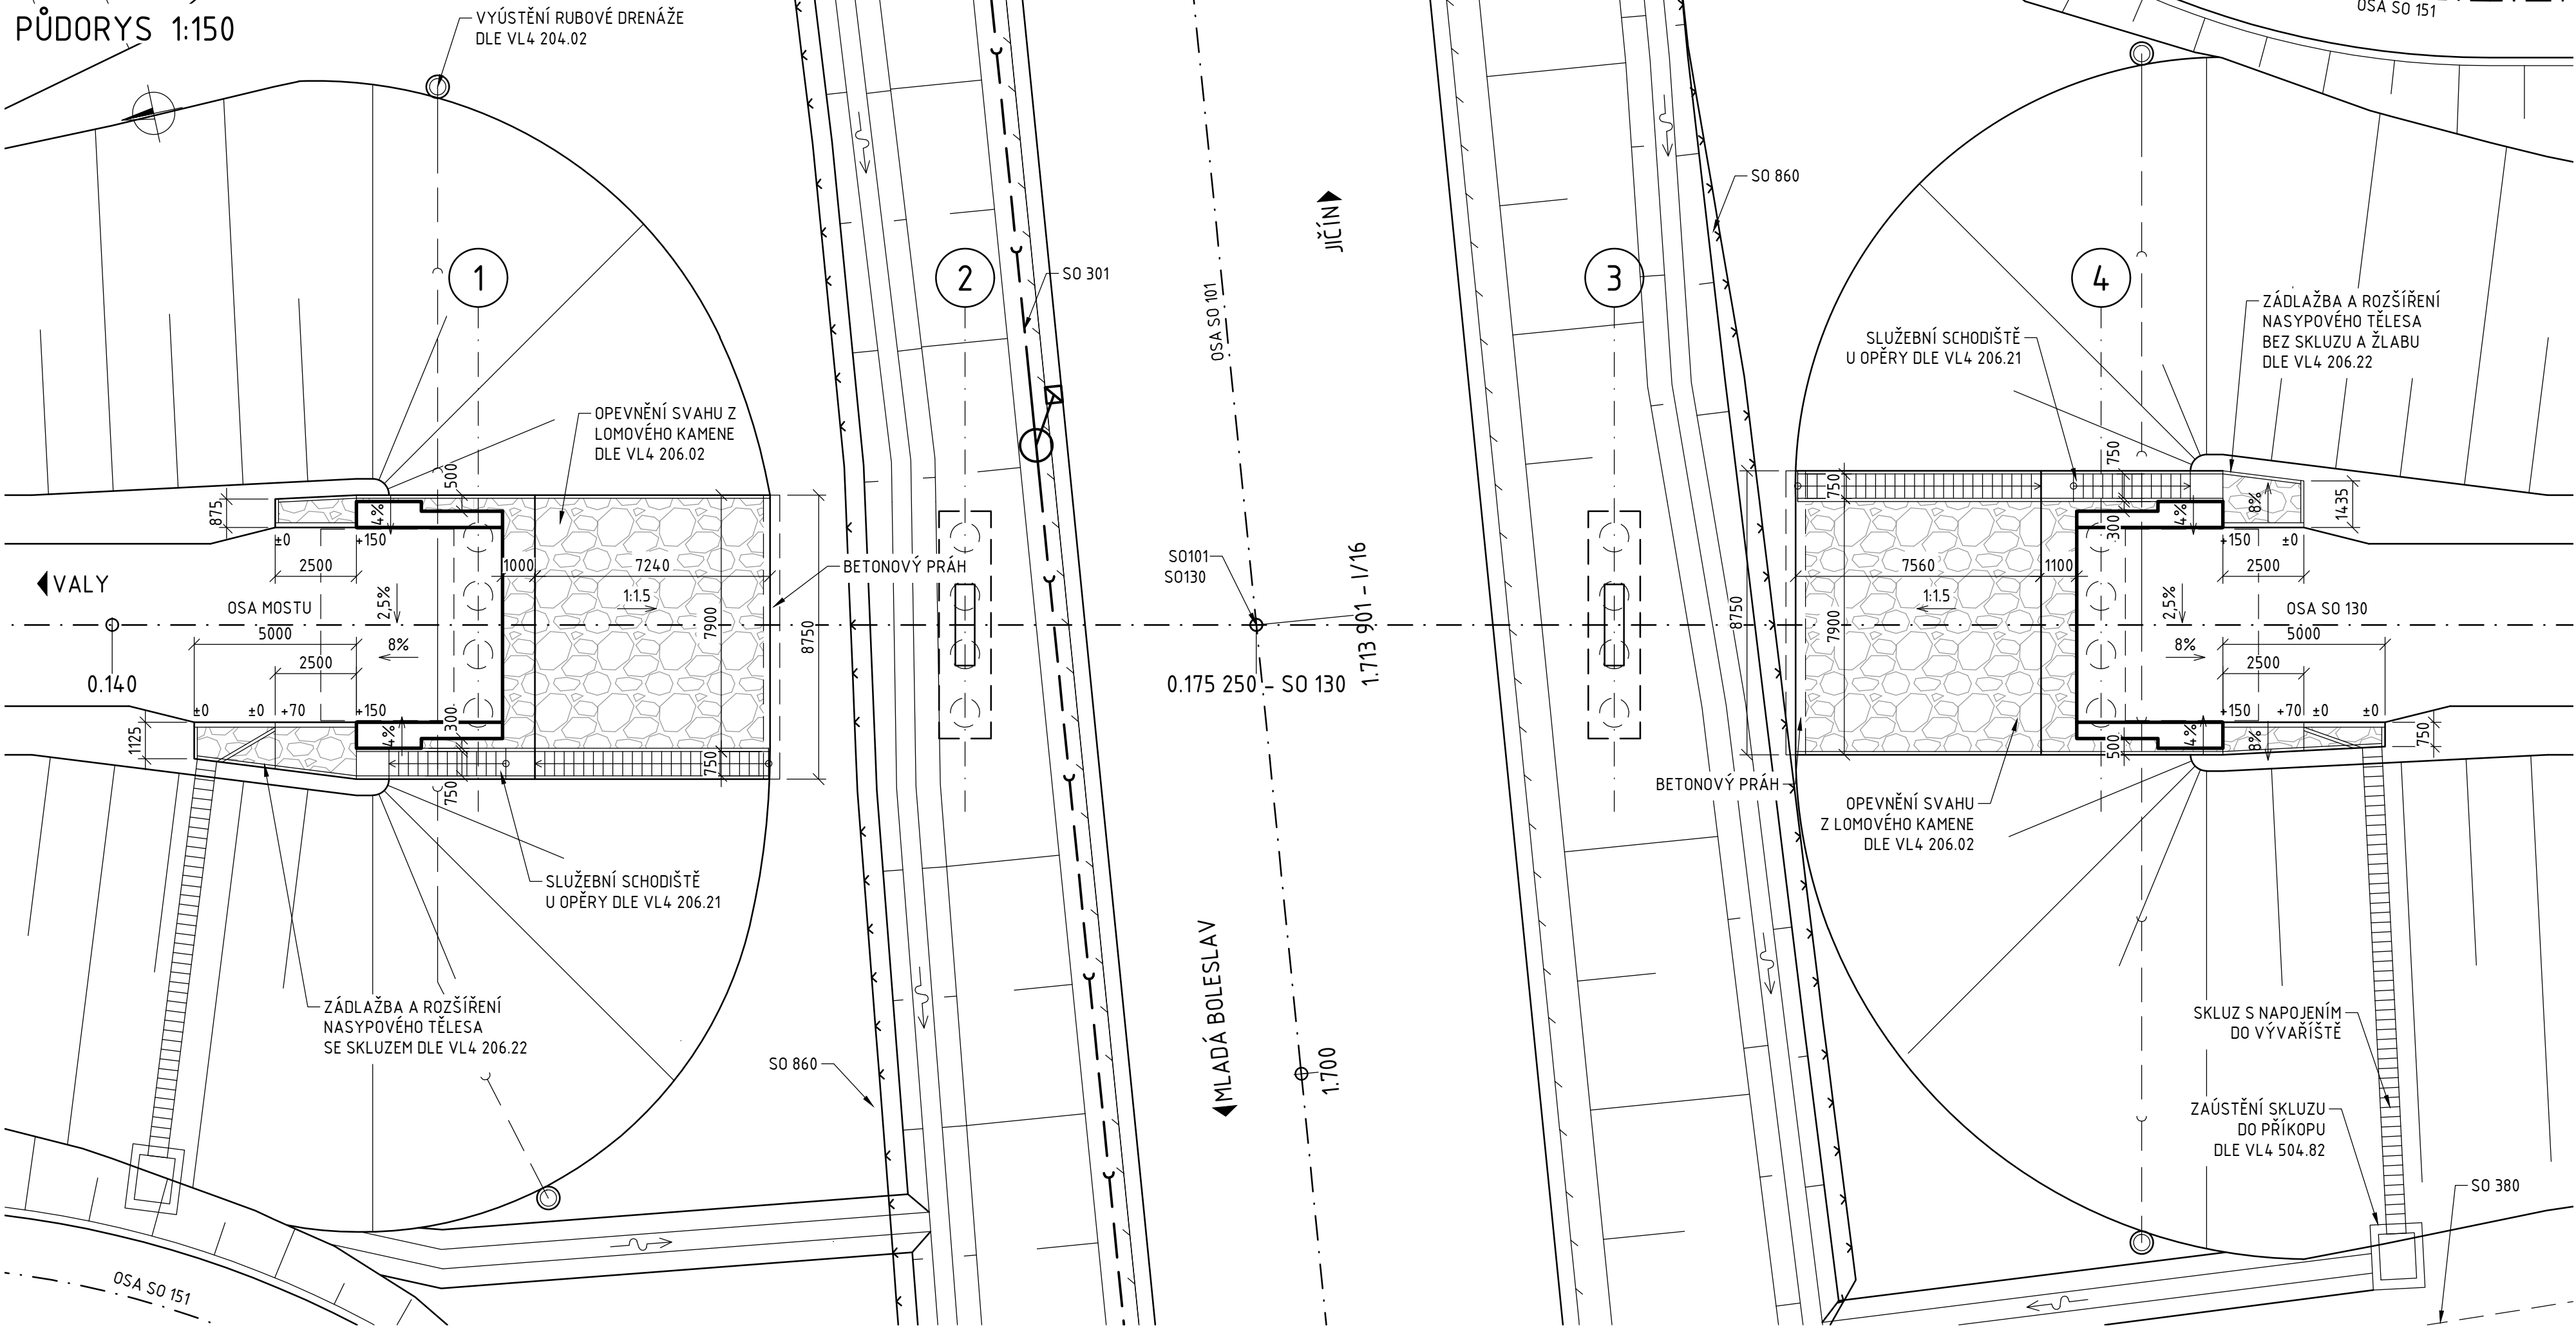


OPEVNĚNÍ SVAHU OPĚRY 1 1:75

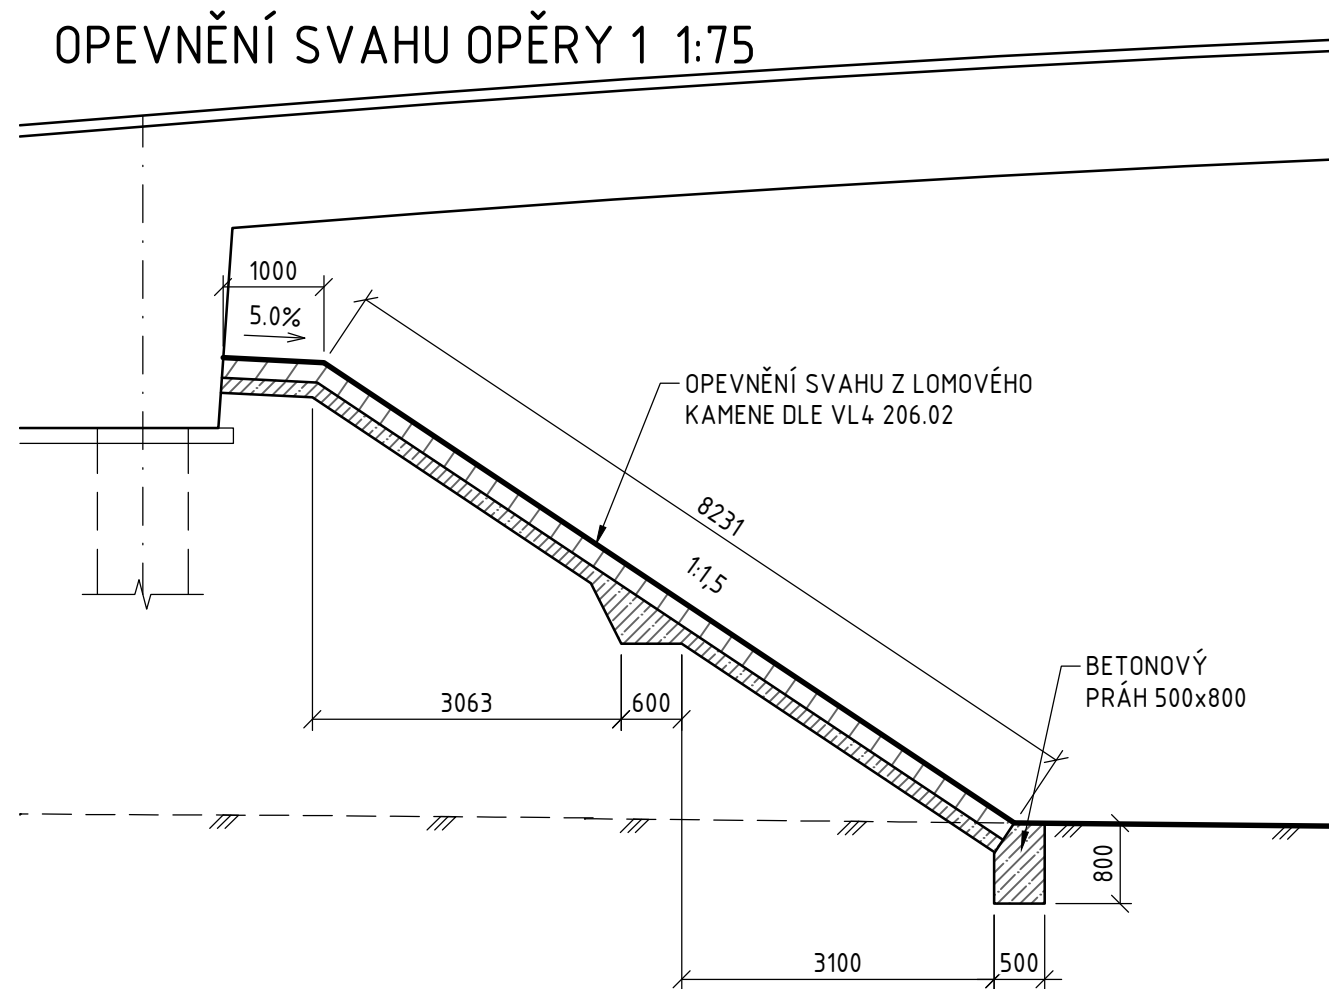


OPEVNĚNÍ SVAHU OPĚRY 4 1:75

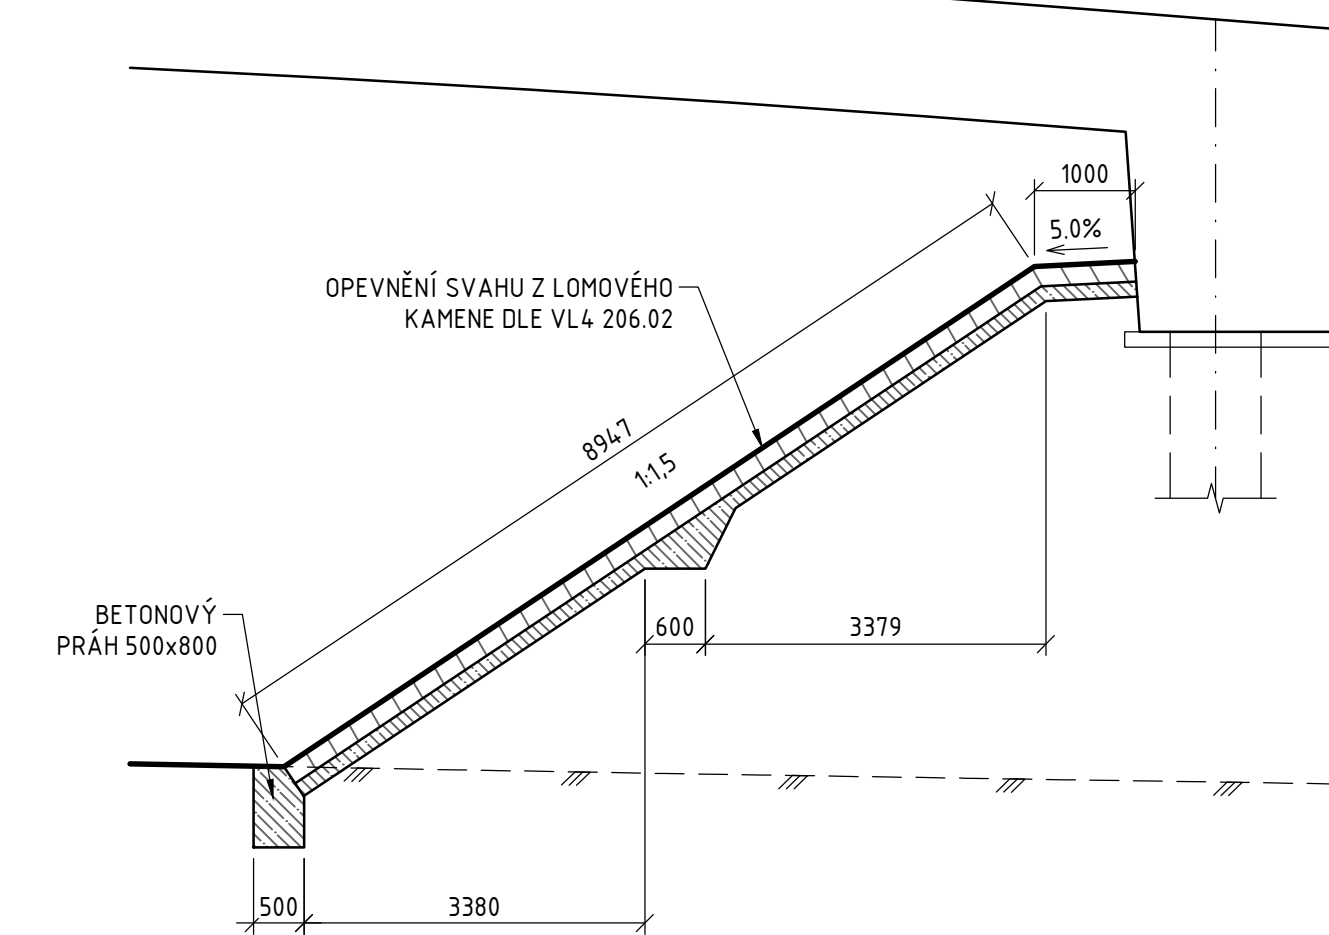

SLUŽEBNÍ SCHODIŠTĚ U OPĚRY 1 1:75

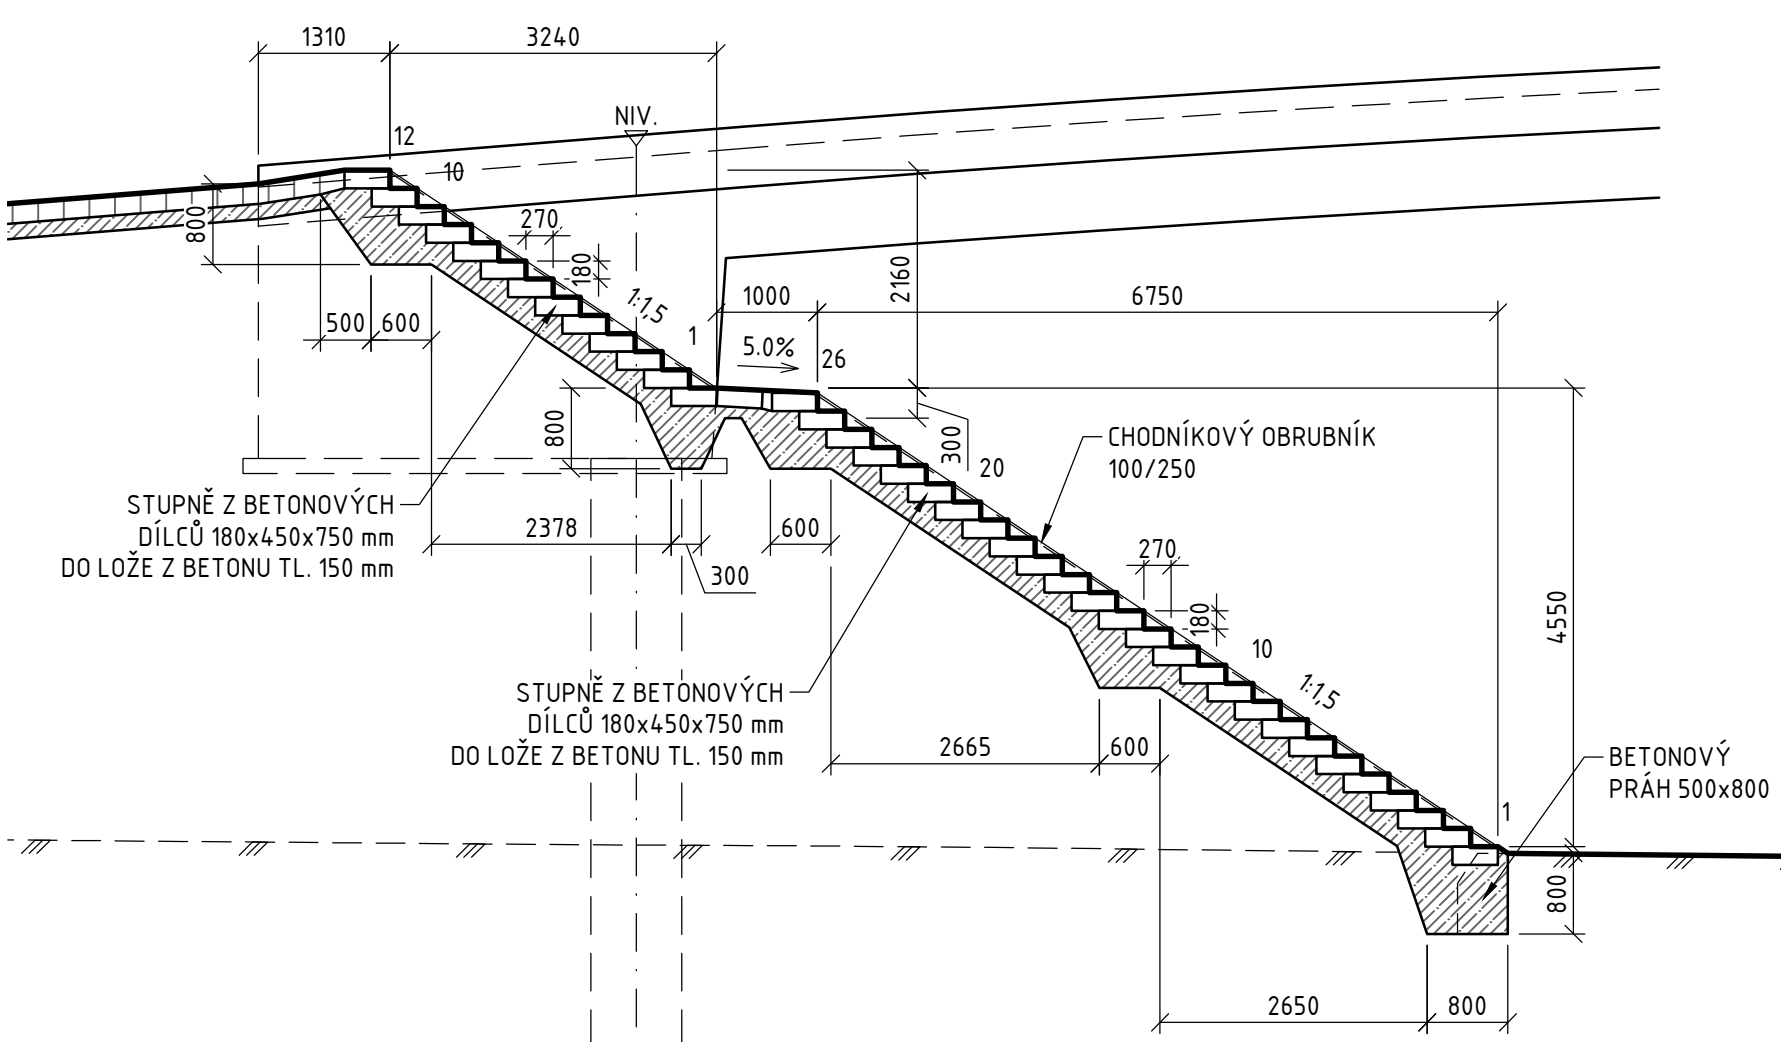


SLUŽEBNÍ SCHODIŠTĚ U OPĚRY 4 1:75

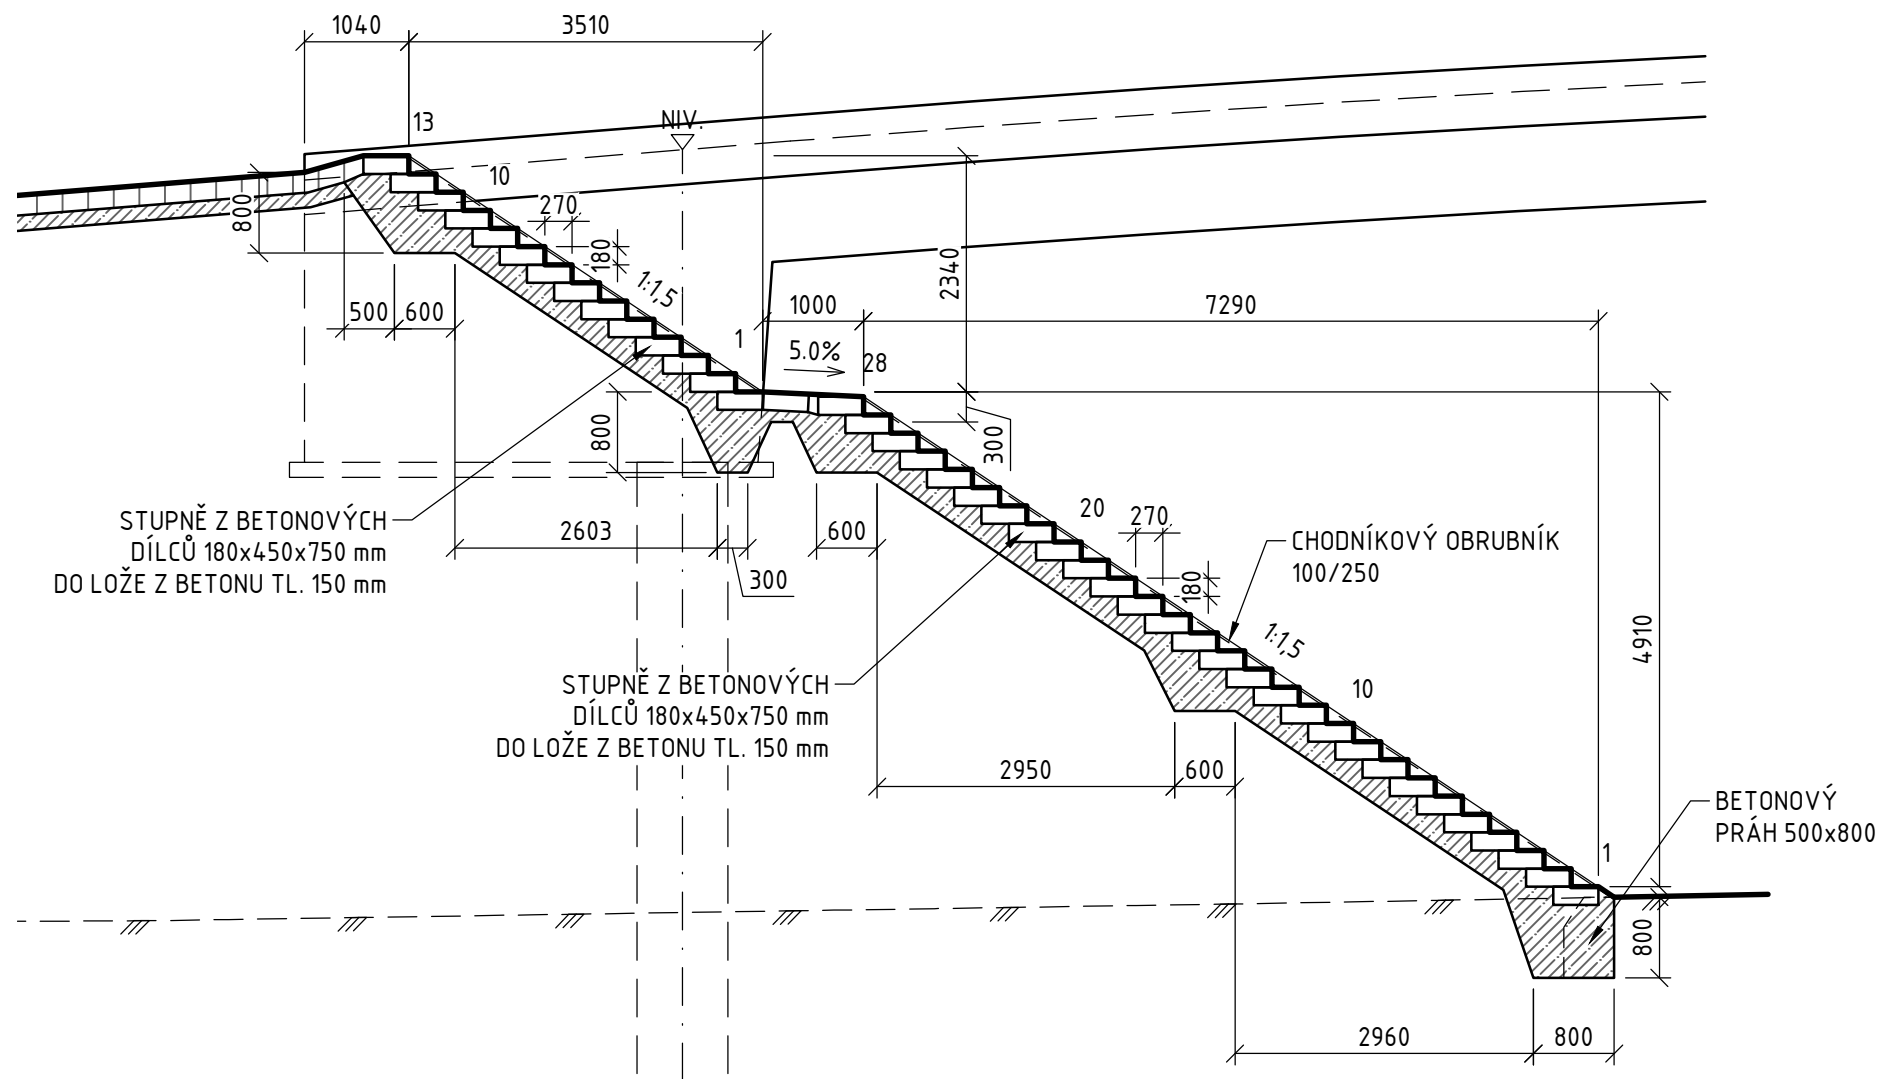

POZNÁMKY

- NEDÍLNOU SOUČÁSTÍ VÝKRESU JSOU TECHNICKÉ SPECIFIKACE A POZNÁMKY UVEDENÉ NA VÝKRESE TECHNICKÝCH SPECIFIKACÍ A POZNÁMEK;

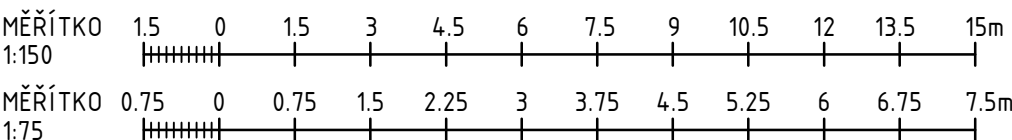

Souřadnicový systém: S-JTSK
Výškový systém: Bpv

SO 230 NADJEZD V km 1,713

Objednatel:



Ředitelství silnic a dálnic s. p.
Čerčanská 2023/12, Krč, 140 00 Praha 4



Valbek, spol. s r.o.
Vaňurova 505/17
460 07 Liberec 3



Vypracoval	ING. A. HERASHCHANKA	Zak. číslo	21-L113-001
Zodp. projektant	ING. A. HERASHCHANKA	Datum	02/2025
Tech. kontrola	ING. I. BELDA	Stupeň	PDPS
Akce	I/16 MLADÁ BOLESLAV - MARTINOVICE	Počet formátů	8 x A4
		Měřítko	1 : 150, 75
		Č. přílohy	Paré
Zhotovitel:	Příloha		
Valbek, spol. s r.o. Vaňurova 505/17 460 07 Liberec 3	ÚPRAVY POD MOSTEM, SLUŽEBNÍ SCHODIŠTĚ	205	