

SCHÉMA VÝZTUŽE ZÁKLADŮ PILÍŘŮ

ŘEZ A-A 1:50 POHLED 1 1:50


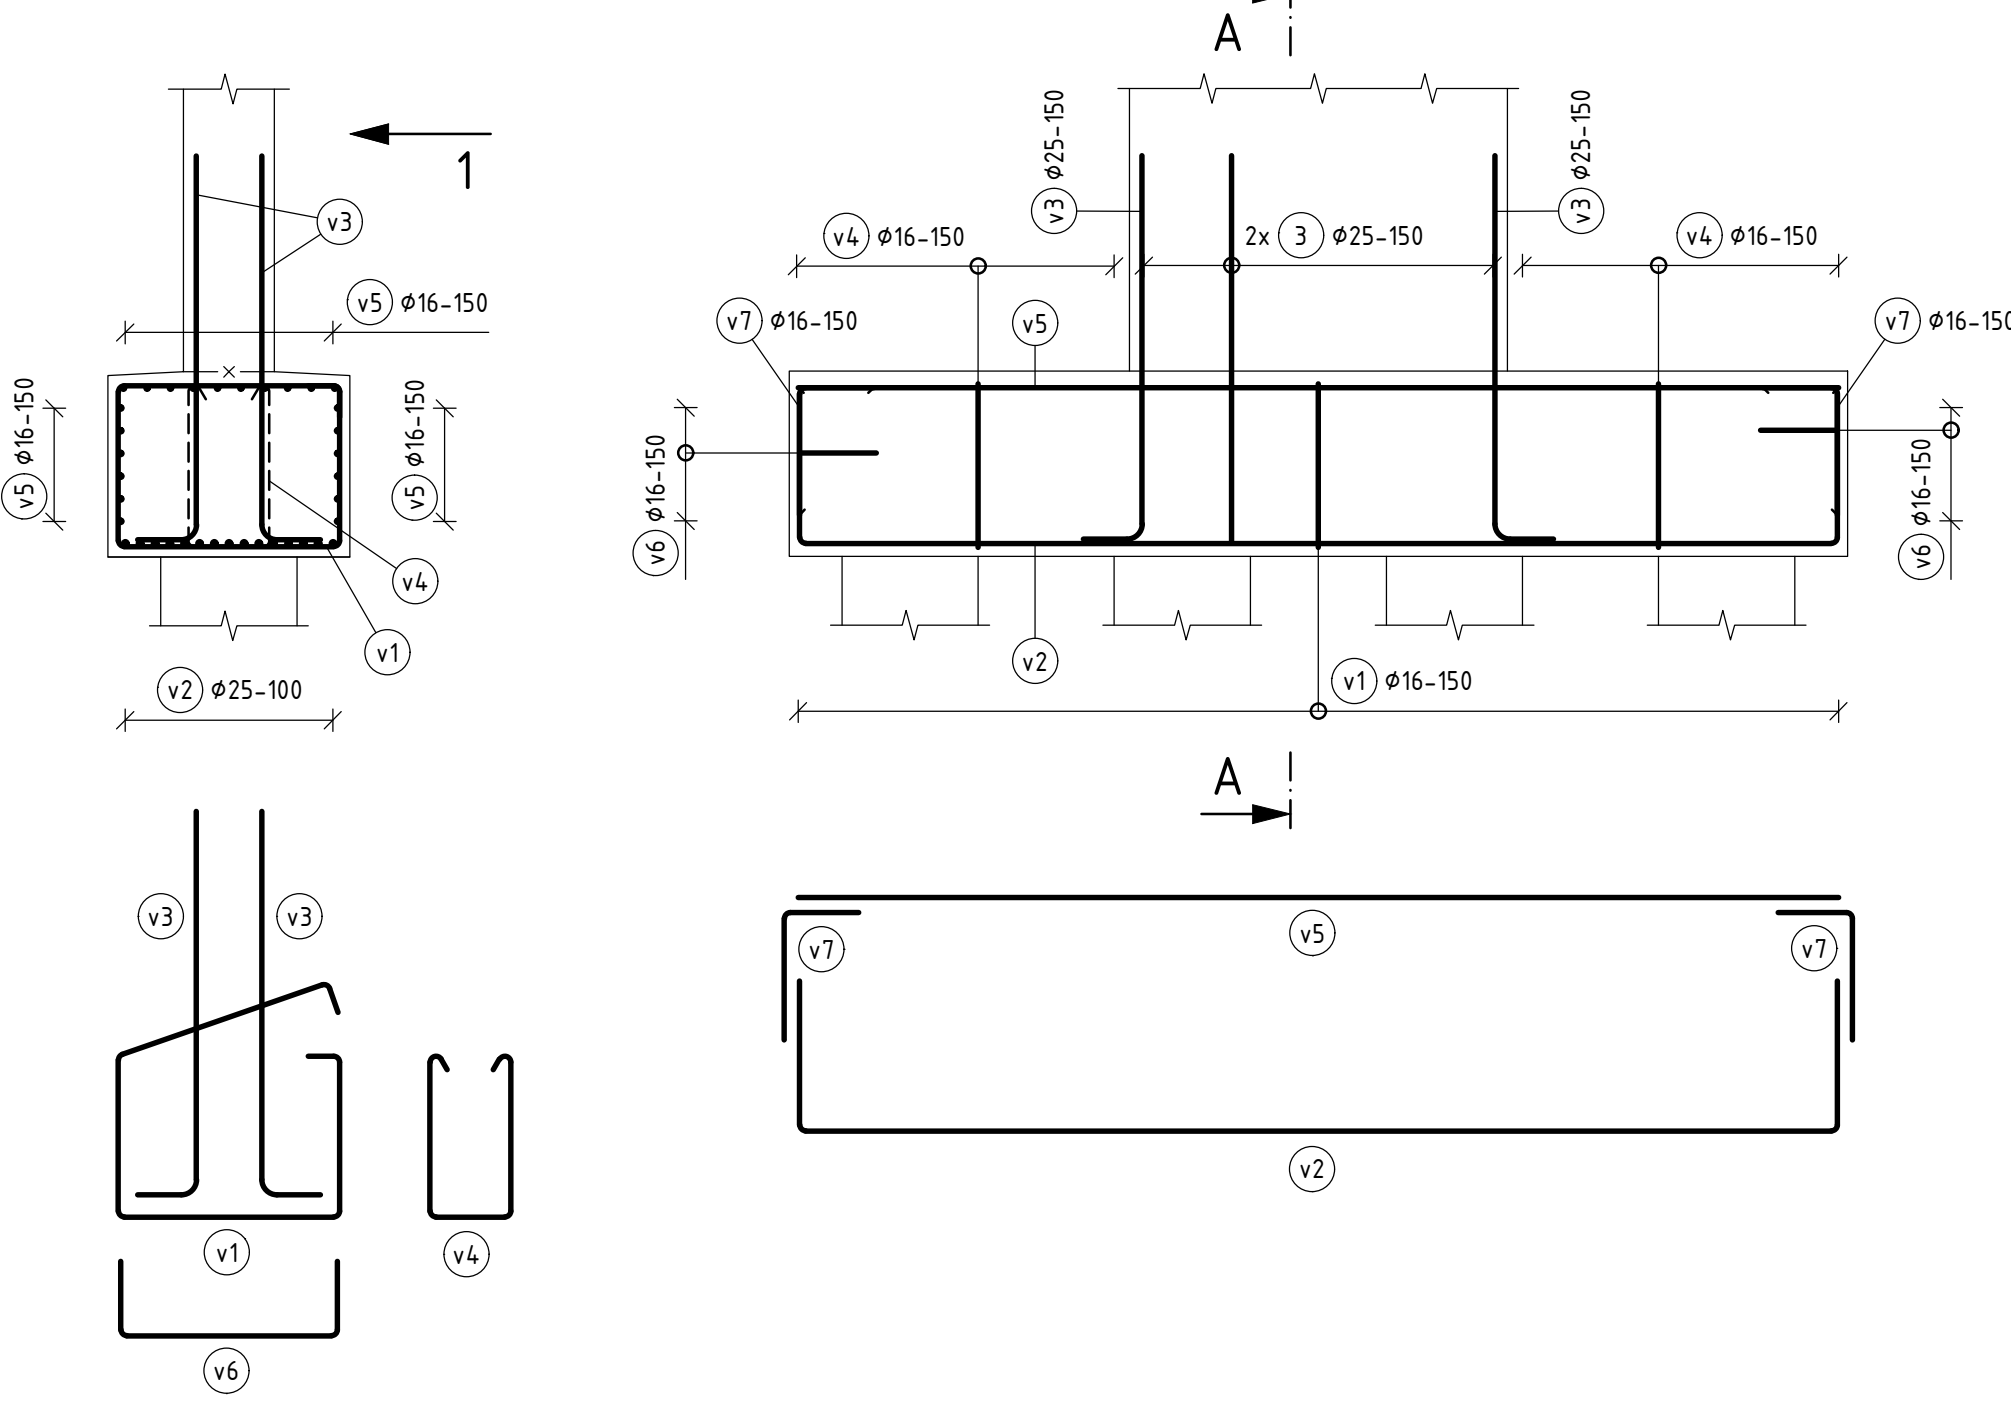


SCHÉMA VÝZTUŽE NK

VÝZTUŽ V PODÉLNÉM SMĚRU 1:100

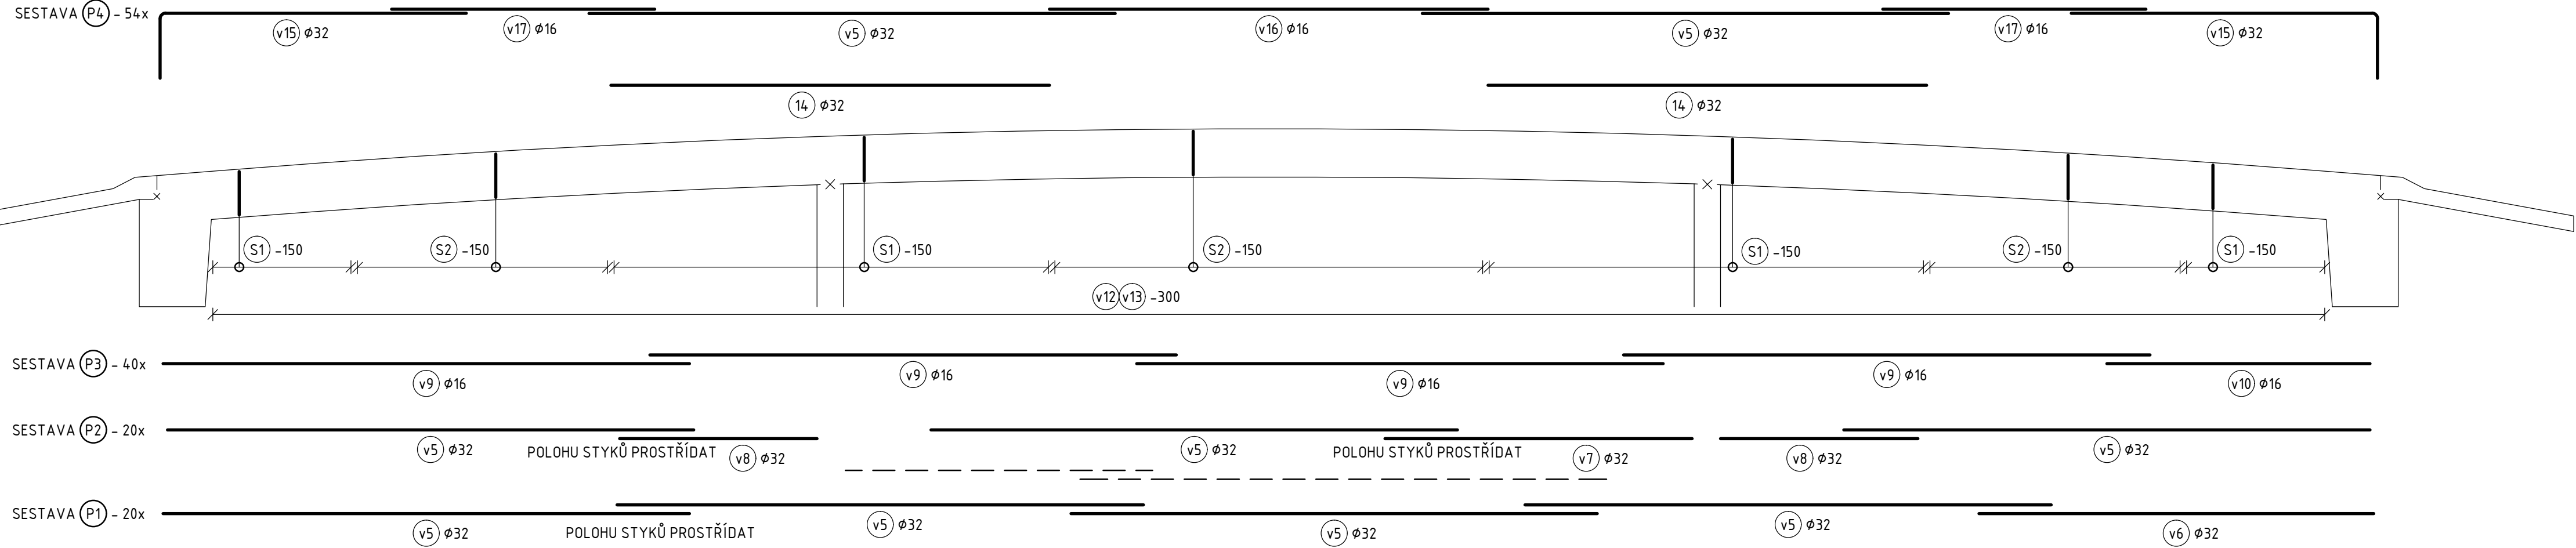

PŘÍČNÝ ŘEZ NK NAD PODPĚROU 1:35

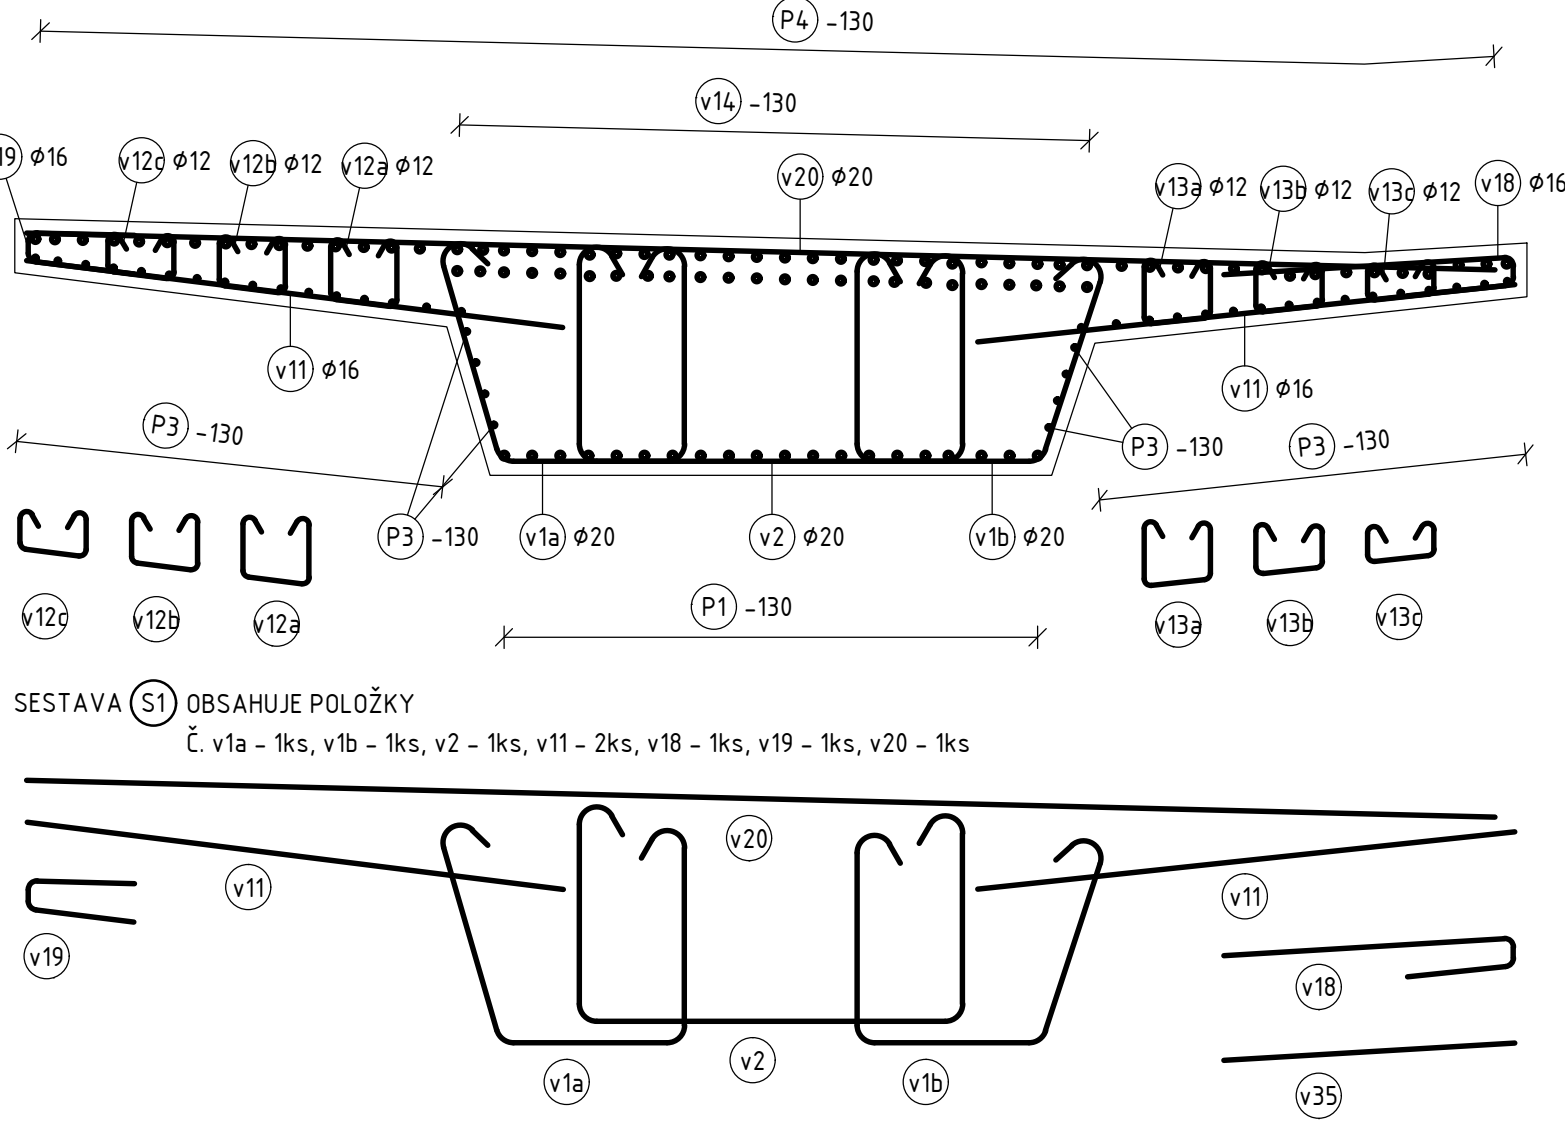


SCHÉMA VÝZTUŽE DŘÍKŮ PILÍŘŮ

ŘEZ A-A 1:50 ŘEZ B-B 1: 25



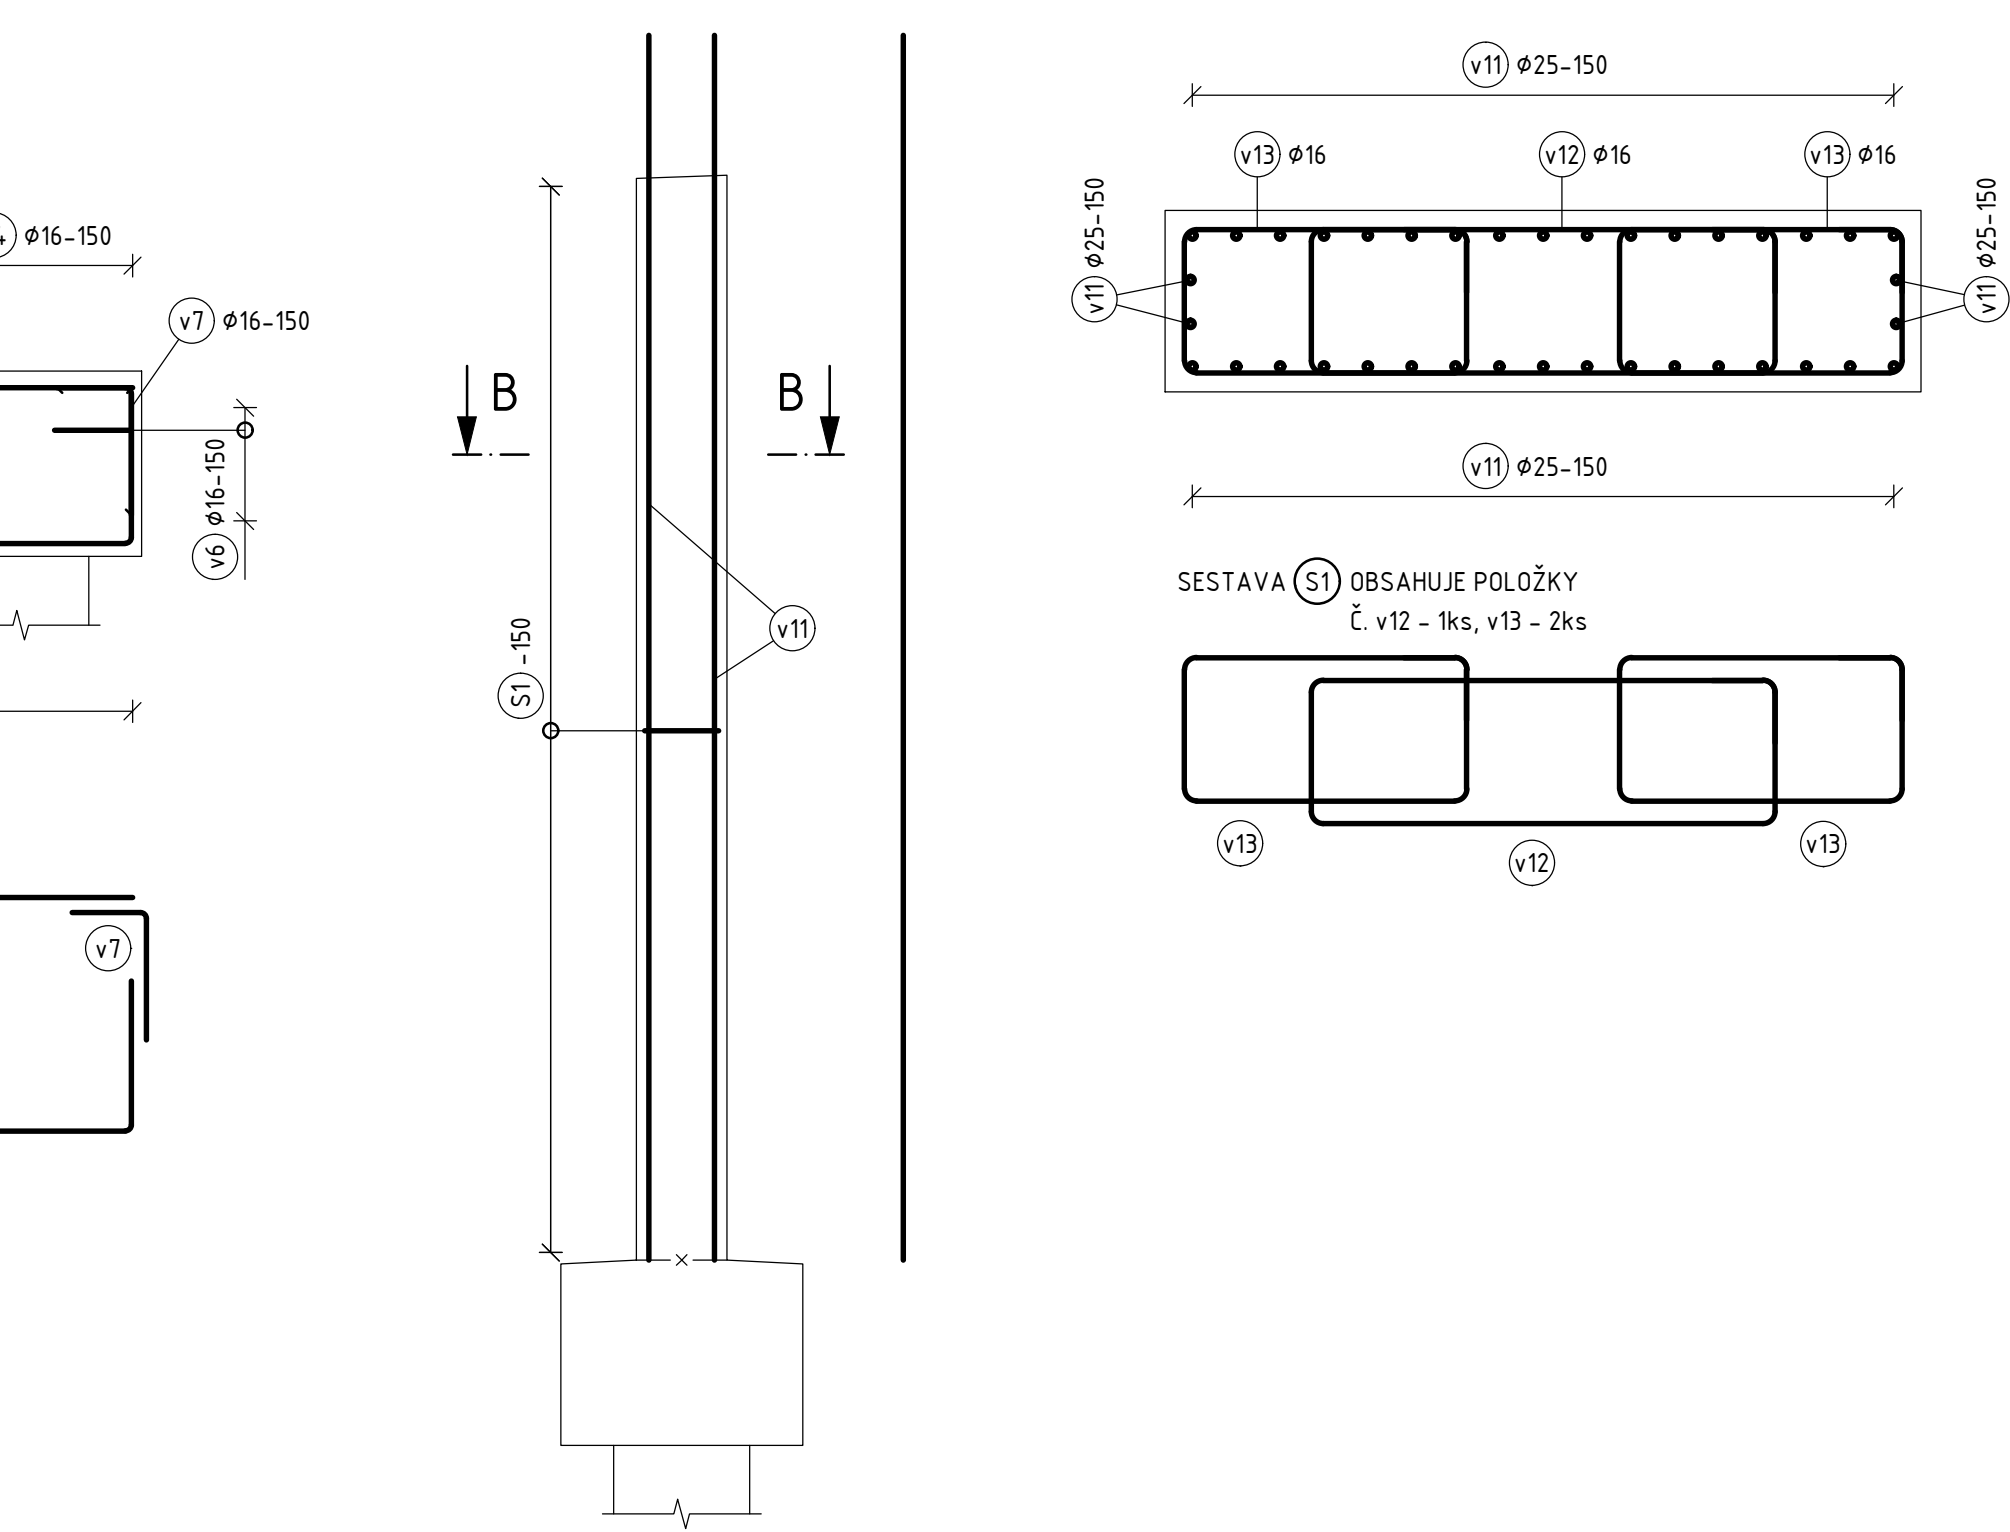


SCHÉMA VÝZTUŽE KONCOVÉHO PŘÍČNÍKU


PŘÍČNÝ ŘEZ OPĚROU 4 1:35

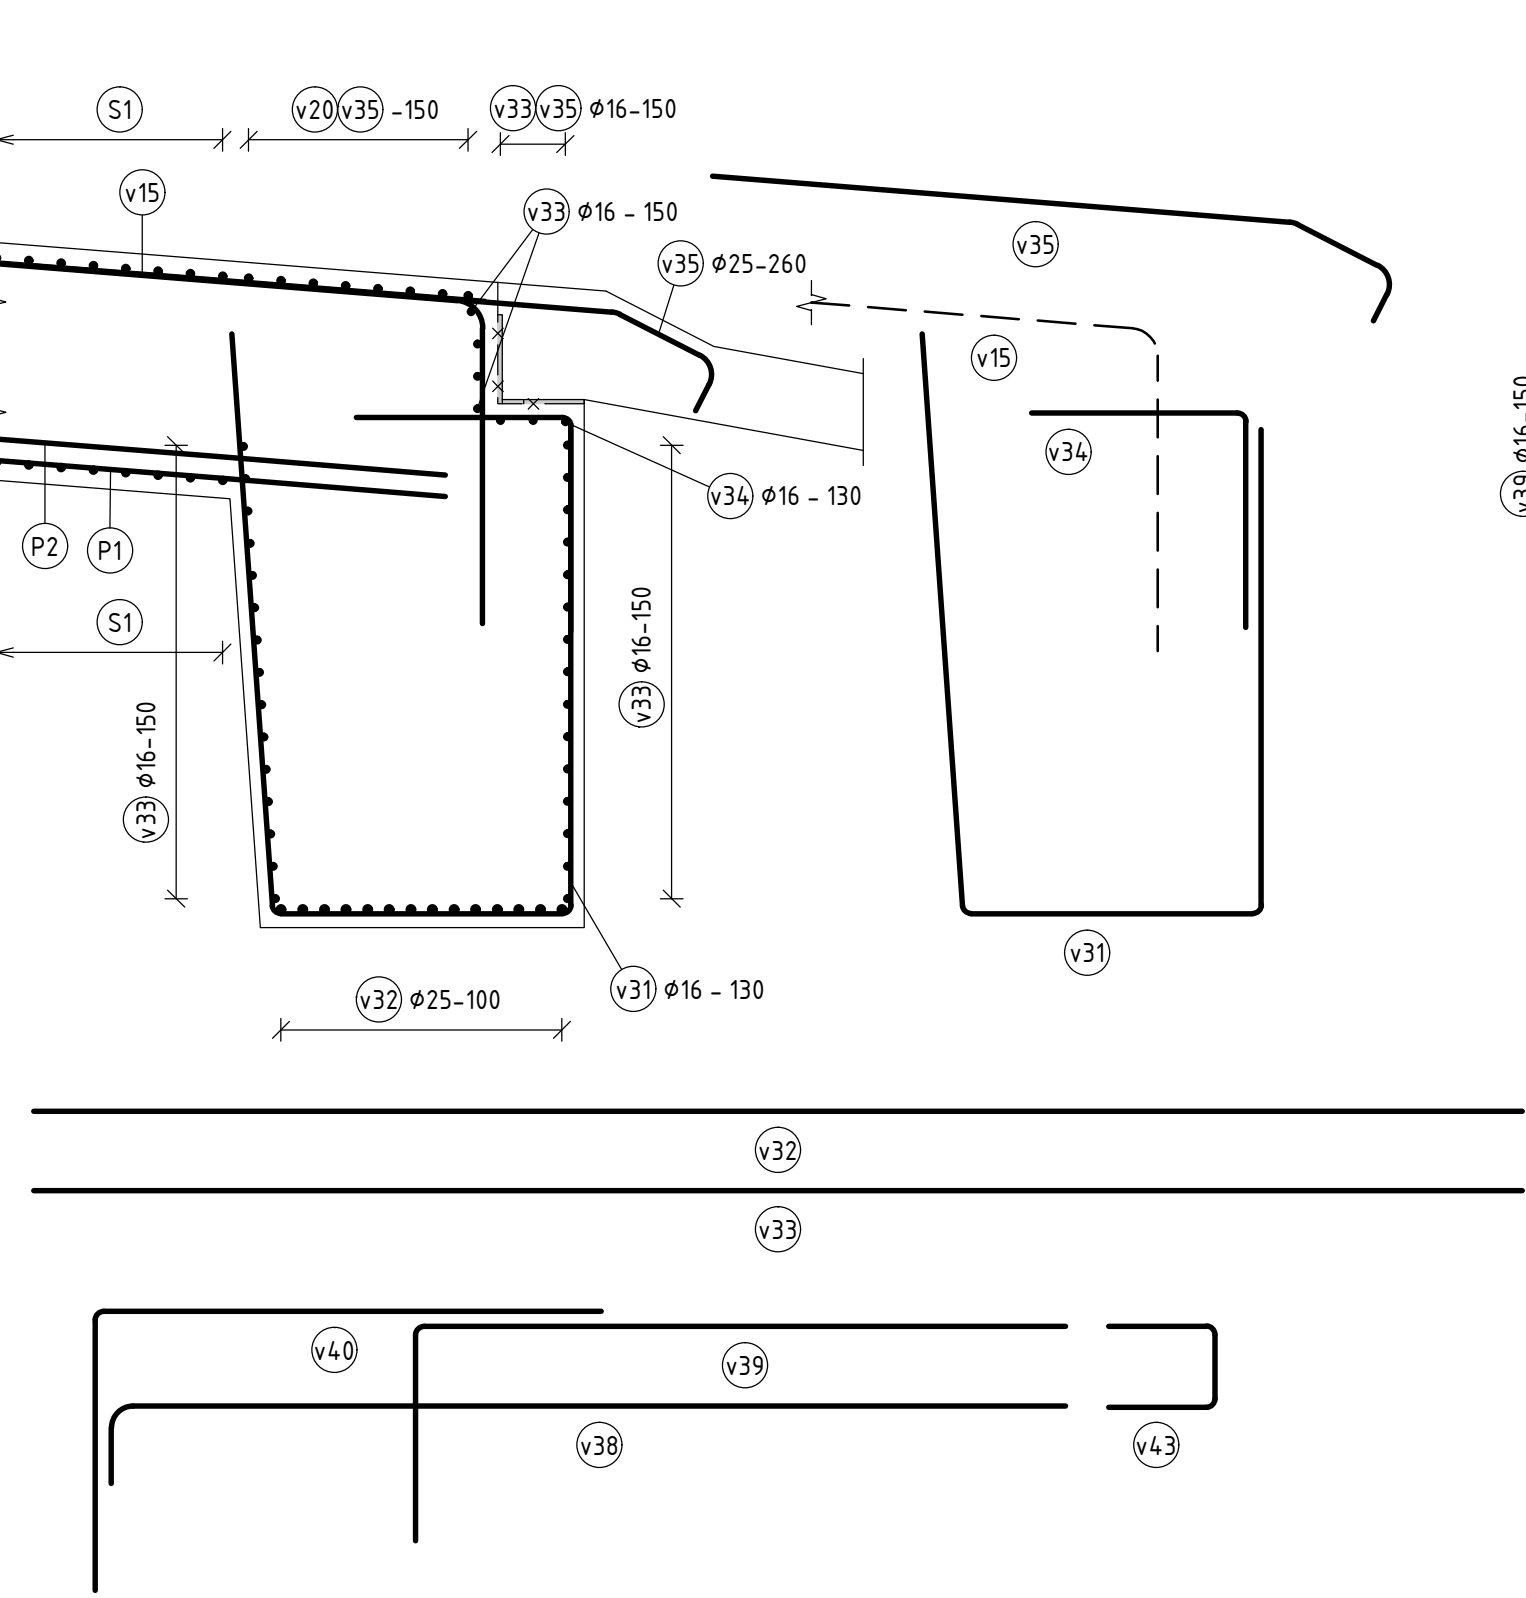

PŘÍČNÝ ŘEZ KŘÍDLEM 1:35

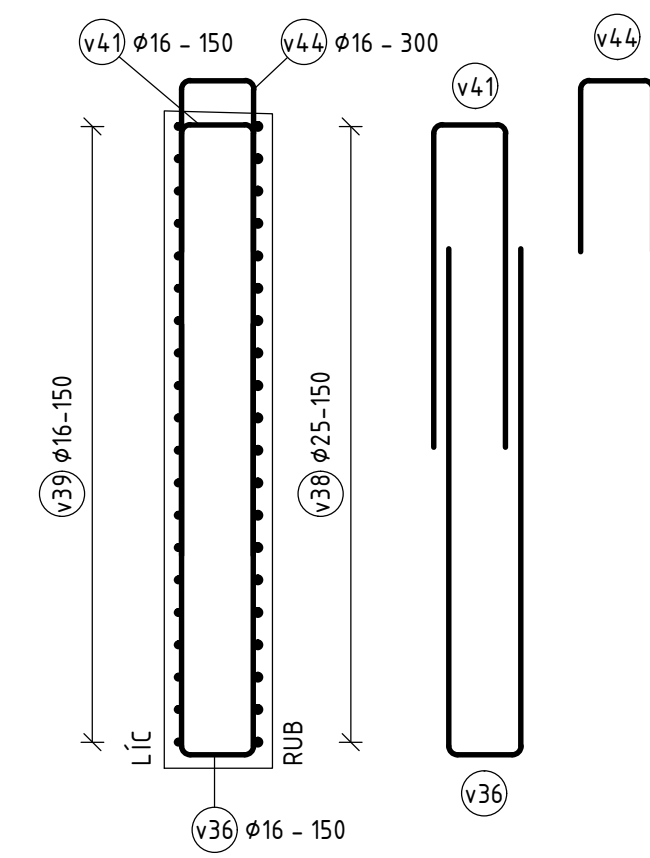

PŘÍČNÝ ŘEZ NK V POLI 1:35

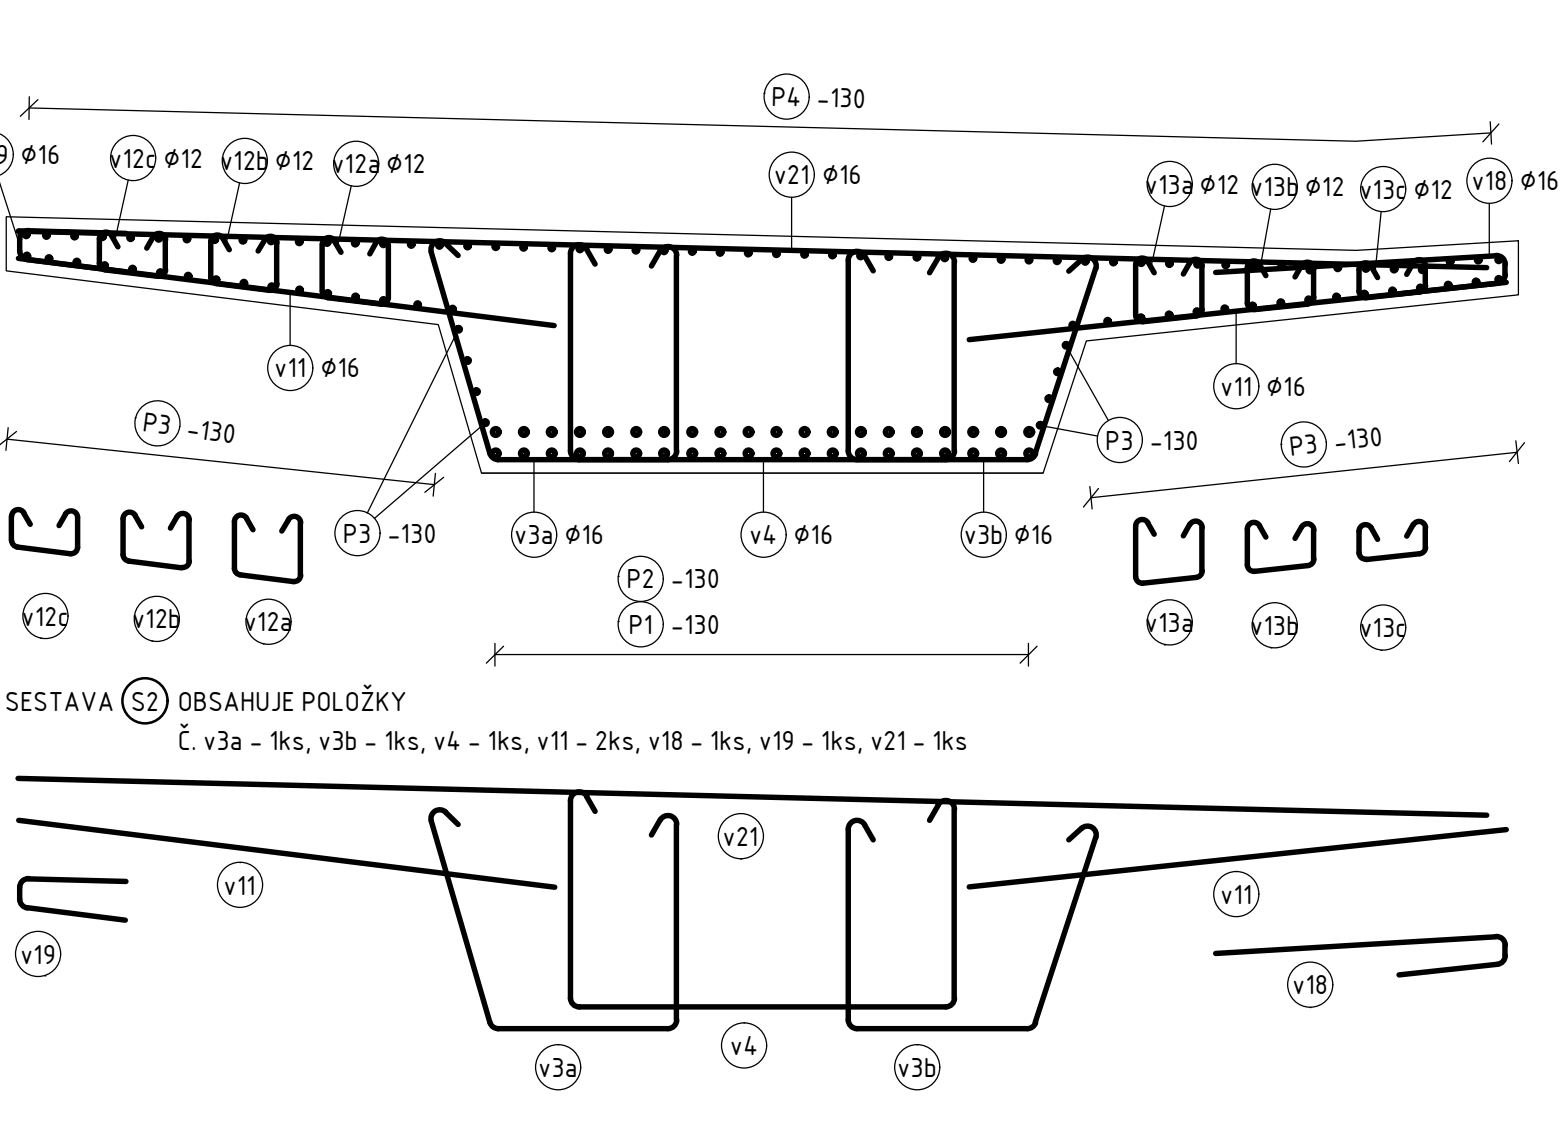

TABULKA SPOTŘEB BETONÁŘSKÉ VÝZTUŽE	MNOŽSTVÍ VÝZTUŽE V %	MNOŽSTVÍ VÝZT.V kg/m3
VÝZTUŽ PILOT Z OCELI 10S05, B500B		
PILOTY POD OPĚRAMI, D 900 mm	2.99 %	235.0
PILOTY POD PILÍŘI, D 900 mm	0.83%	65.0
VÝZTUŽ ZÁKLADŮ Z OCELI 10S05, B500B		
ZÁKLADY POD PILÍŘI	1.66 %	130.0
VÝZTUŽ MOSTNÍCH PILÍŘŮ A STATIV Z OCELI 10S05, B500B		
DŘÍKY PILÍŘŮ	2.42%	190.0
VÝZTUŽ MOSTNÍ TRÁMOVÉ KONSTRUKCE Z OCELI 10S05, B500B	2.61%	205.0
VÝZTUŽ ŘÍMS Z OCELI 10S05, B500B	1.78 %	140.0
VÝZTUŽ PŘECHODOVÝCH DESEK MOSTNÍCH OPĚR Z OCELI 10S05, B500B	1.78 %	140.0

Souřadnicový systém: S-JTSK Výškový systém: Bpv		SO 230 NADJEZD V km 1,713	
Objednatel:		Ředitelství silnic a dálnic s. p. Čerčanská 2023/12, Krč, 140 00 Praha 4	
Valbek		Valbek, spol. s r.o. Vaňurova 505/17 460 07 Liberec 3	
Zhotovitel: Valbek, spol. s r.o. Vaňurova 505/17 460 07 Liberec 3	Příloha	I/16 MLADÁ BOLESLAV - MARTINOVICE	301