


SITUACE
M 1 : 1000

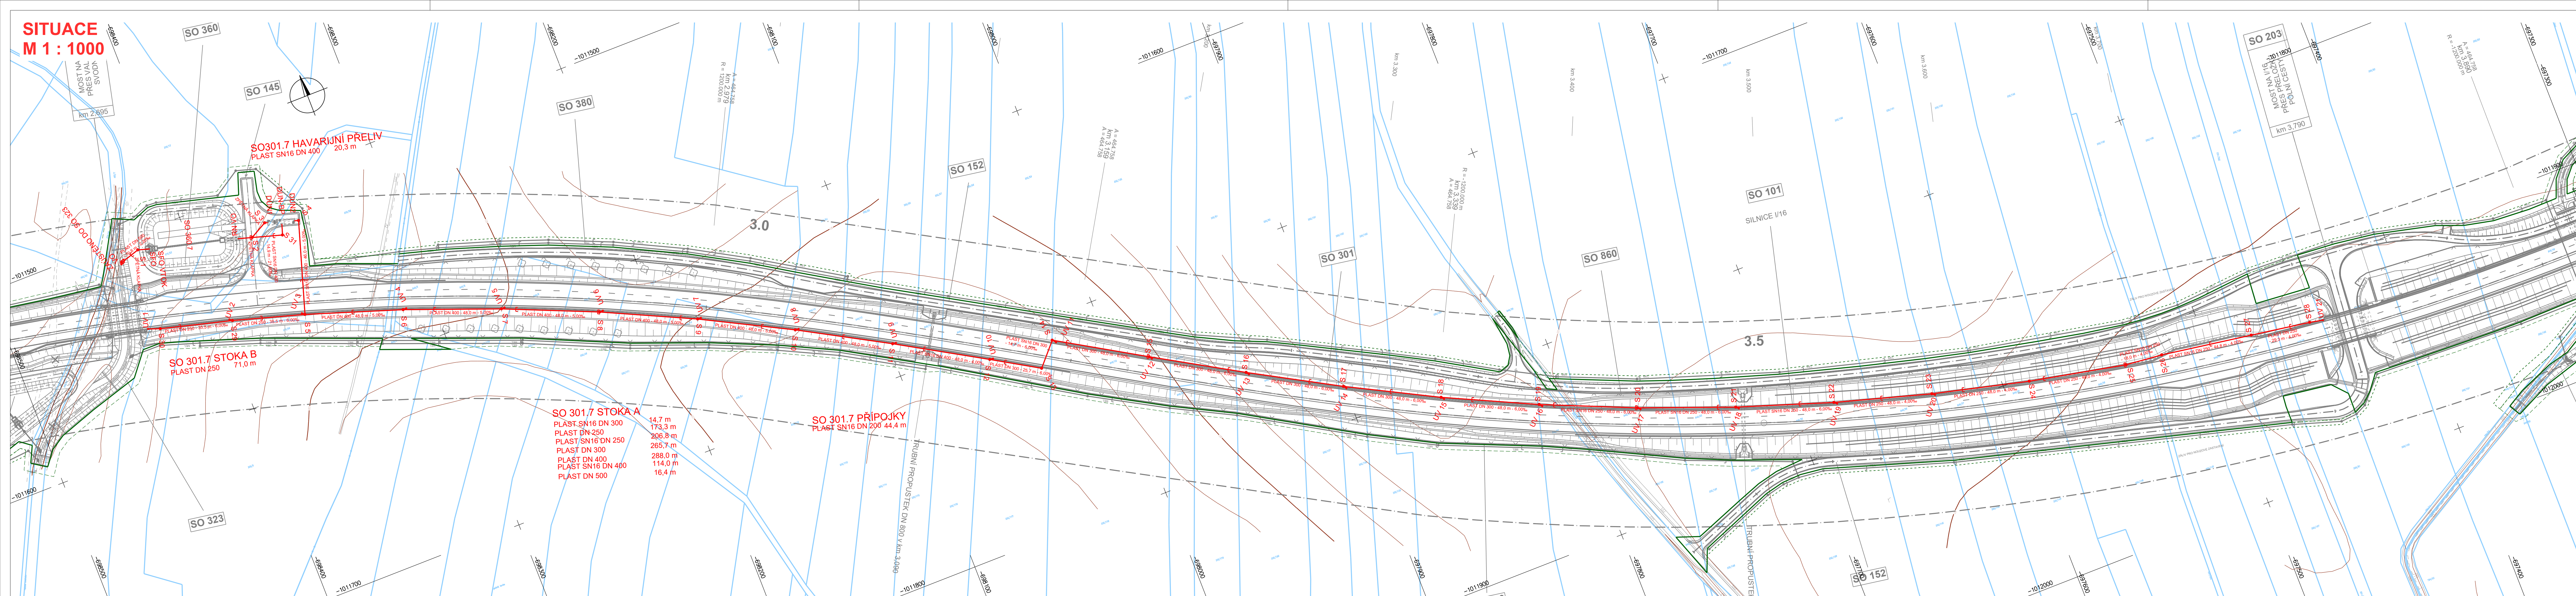

LEGENDA:

STÁVAJÍCÍ IS - INFORMATIVNÍ ZÁKRES

- VODOVOD
- KANALIZACE
- DEŠŤOVÁ KANALIZACE
- IS_Kanalizac_splaskov
- IS_Kanalizace_jednotn
- SDĚLOVACÍ VEDENÍ
- SDĚLOVACÍ VEDENÍ NADZEMNÍ
- PODZEMNÍ SDĚLOVACÍ VEDENÍ
- PLYNOVOD - NTL
- PLYNOVOD - STL
- PLYNOVOD - VTL
- NADZEMNÍ VEDENÍ NN
- NADZEMNÍ VEDENÍ VN
- NADZEMNÍ VEDENÍ VVN
- PODZEMNÍ VEDENÍ NN
- PODZEMNÍ VEDENÍ VN
- SILOVÉ VEDENÍ PODZEMNÍ - SŽDC

Souřadnicový systém: S-JTSK
Výškový systém: Bpv

SO 301 Odvodnění I/16

Objednatel:



Ředitelství silnic a dálnic s. p.
Čerčanská 2023/12, Krč, 140 00 Praha 4

Zhotovitel:



Valbek, spol. s r.o.
Vaňurova 505/17
460 07 Liberec 3

	Vypracoval	ING. J. VANCL	Zak. číslo	21-L113-001
	Zodp. projektant	ING. J. VANCL	Datum	02/2025
	Tech. kontrola	ING. D. LANDA	Stupeň	PDPS
	Akce	I/16 MLADÁ BOLESLAV - MARTINOVICE	Počet formátů	7 x A4
Zhotovitel: Valbek, spol. s r.o. Vaňurova 505/17 460 07 Liberec 3	Příloha	SITUACE Č.7 - 301.7	Měřítko	1 : 1 000
			Č. přílohy	Paré

2.7