


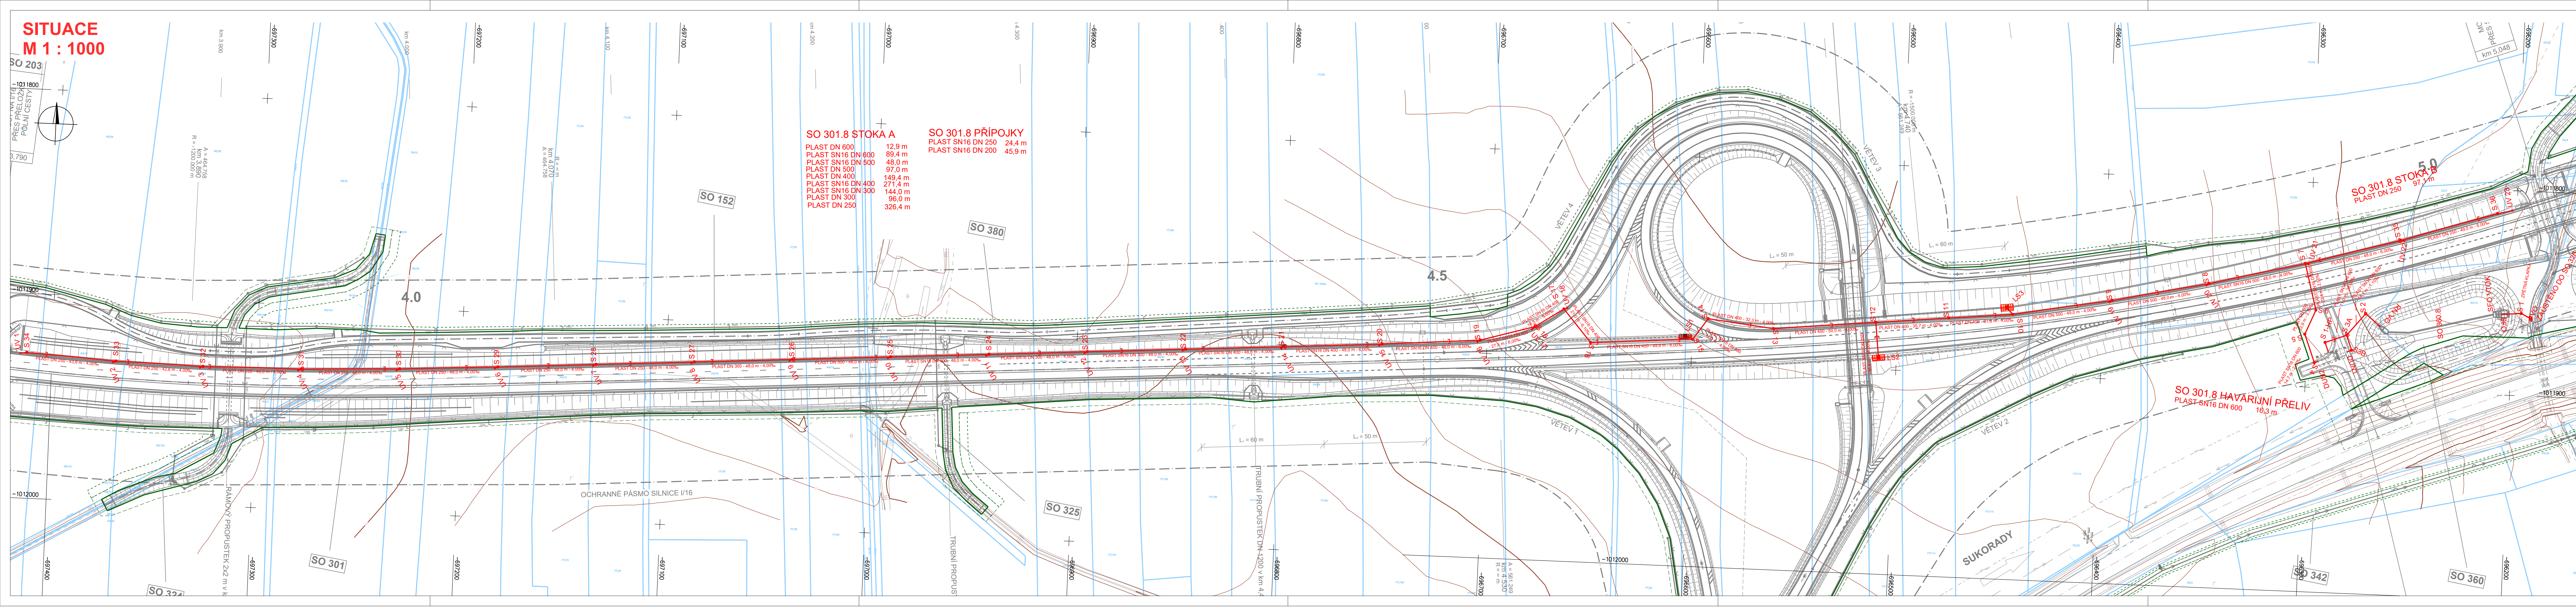

LEGENDA:

STÁVAJÍCÍ IS - INFORMATIVNÍ ZÁKRES

- VODOVOD
- KANALIZACE
- DEŠŤOVÁ KANALIZACE
- IS_Kanalizac_splaskov
- IS_Kanalizace_jednotn
- SDĚLOVACÍ VEDENÍ
- SDĚLOVACÍ VEDENÍ NADZEMNÍ
- PODZEMNÍ SDĚLOVACÍ VEDENÍ
- PLYNOVOD - NTL
- PLYNOVOD - STL
- PLYNOVOD - VT
- NADZEMNÍ VEDENÍ NN
- NADZEMNÍ VEDENÍ VN
- NADZEMNÍ VEDENÍ VVN
- PODZEMNÍ VEDENÍ NN
- PODZEMNÍ VEDENÍ VN
- SILOVÉ VEDENÍ PODZEMNÍ - SŽDC

Souřadnicový systém: S-JTSK
Výškový systém: Bpv

SO 301 Odvodnění I/16

Objednatel:



Ředitelství silnic a dálnic s. p.
Čerčanská 2023/12, Krč, 140 00 Praha 4

Zhotovitel:



Valbek, spol. s r.o.
Vaňurova 505/17
460 07 Liberec 3

	Vypracoval	ING. J. VANCL		Zak. číslo	21-L113-001		
	Zodp. projektant	ING. J. VANCL		Datum	02/2025		
	Tech. kontrola	ING. D. LANDA		Stupeň	PDPS		
	Akce	I/16 MLADÁ BOLESLAV - MARTINOVICE			Počet formátů	7 x A4	
 Zhotovitel: Valbek, spol. s r.o. Vaňurova 505/17 460 07 Liberec 3	Příloha				SITUACE Č.8 - 301.8	Měřítko	1 : 1 000
						Č. přílohy	Paré
		2.8					