



SMĚROVÉ POMĚRY

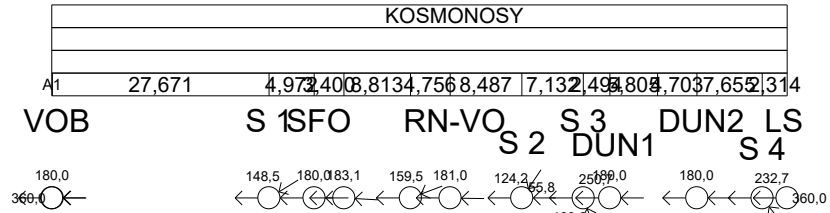


VZDÁLENOSTI ŠACHET	
A1	0,411
SKLON (‰) - DĚLKA (m)	
B1	787,7, 0,09
B2	18,8, 5,97
B3	4,5, 12,71
B4	118,0, 5,26
PROFIL (mm) - MATERIÁL - DĚLKA (m)	
C1	VO
C2	300, PLAST SN16, 21,11
C3	OLK, 11,51
C4	300, PLAST SN16, 11,97
KAPACITNÍ PRŮTOK (l/s) - RYCHLOST (m/s)	
D1	7,21, 3,67
D2	288,50, 2,30
D3	SFO
D4	RN
D5	RN
NÁVRHOVÝ PRŮTOK (l/s) - RYCHLOST (m/s)	
E1	43,800, 7,341
E2	43,800, 1,639
E3	43,800, 0,544
E4	43,800, 0,545
E5	43,800, 2,832

SMĚROVÉ POMĚRY

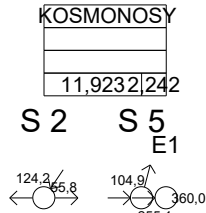


SKLON (‰) - DÉLKA (m)	
A1	17,0, 12,92
A2	-5,0, 3,24
PROFIL (mm) - MATERIÁL - DÉLKA (m)	
B1	300, PLAST SN16, 16,17
KAPACITNÍ PRŮTOK (l/s) - RYCHLOST (m/s)	
C1	127,94, 1,81
C2	69,11, 0,98
NÁVRHOVÝ PRŮTOK (l/s) - RYCHLOST (m/s)	
D1	43,800
D2	43,800
OZNAČENÍ ŠACHET	
E1	DUN-BP

[1:1000/100]

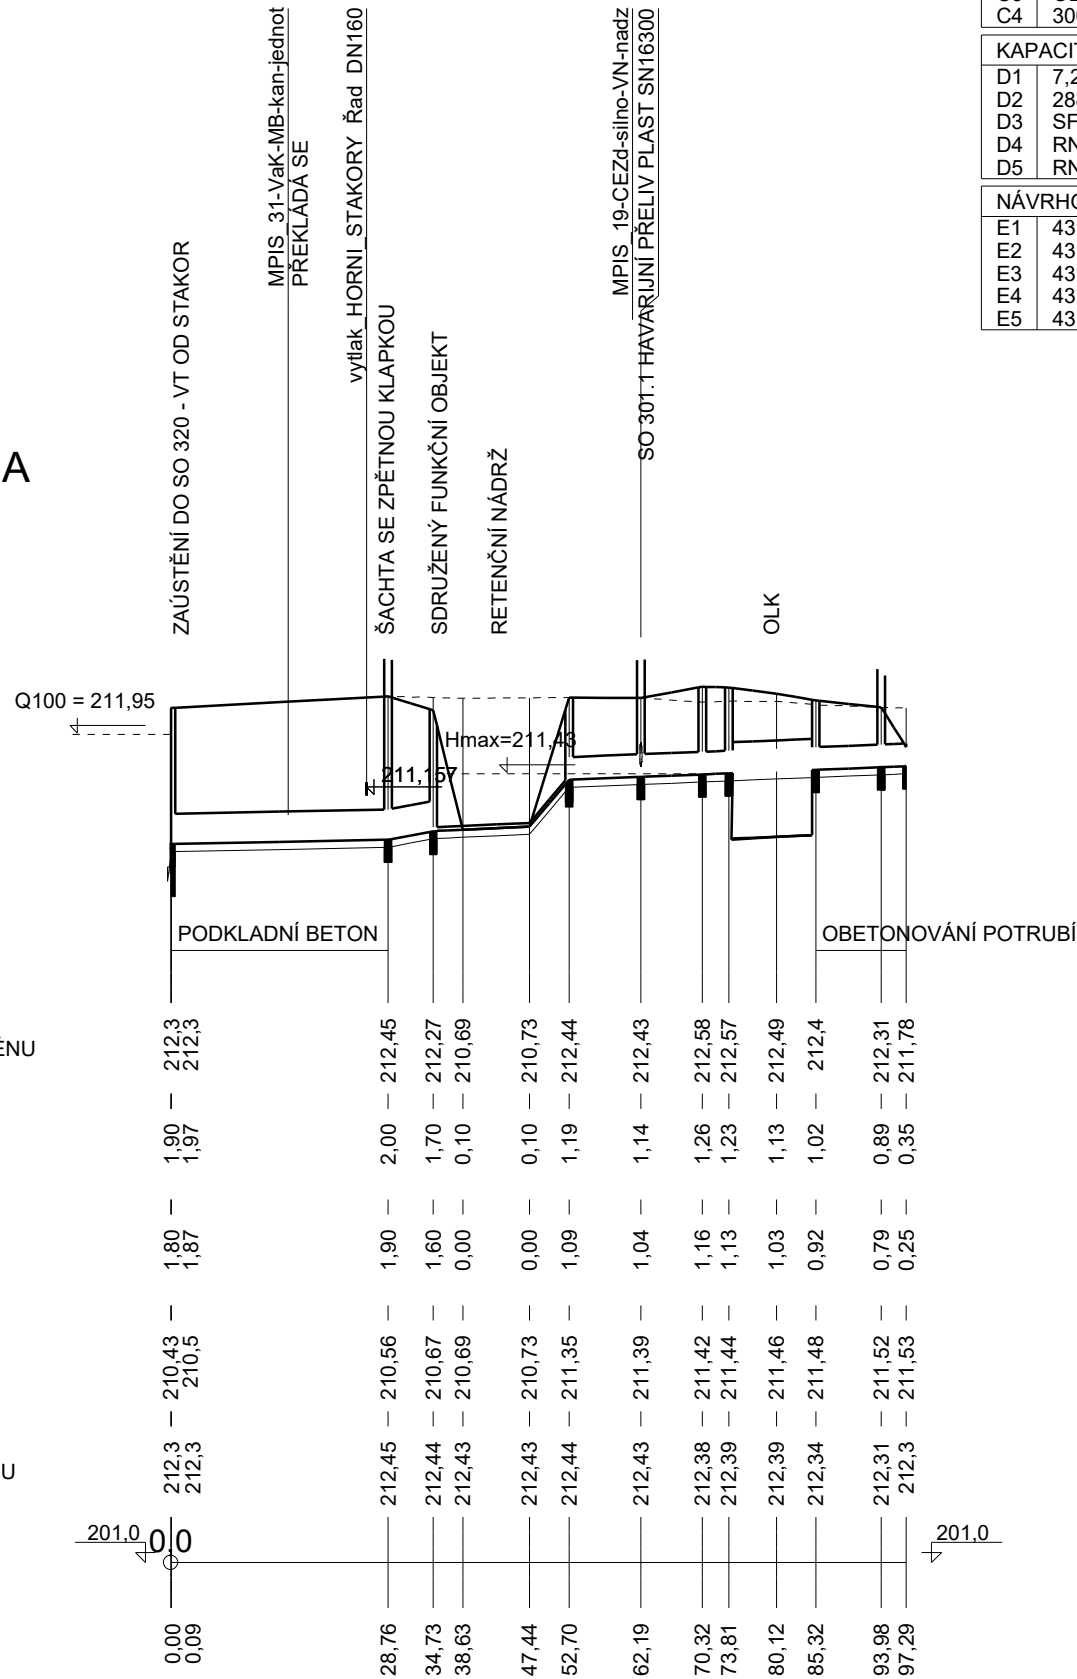

SKLON (‰) - DĚLKA (m)	B1	2,0	28,67	B2	B3	B4	4,0	44,66	
PROFIL (mm) - MATERIÁL - DĚLKA (m)	C1	400	PLAST SN16	34,64	RN	17,97	C2	C3	C4
KAPACITNÍ PRŮTOK (l/s) - RYCHLOST (m/s)	D1	93,58	0,74	D2	D3	D4	D5	62,05	0,88
NÁVRHOVÝ PRŮTOK (l/s) - RYCHLOST (m/s)	E1	43,800	0,700	E2	E3	E4	E5	43,800	0,933

[1:1000/100]

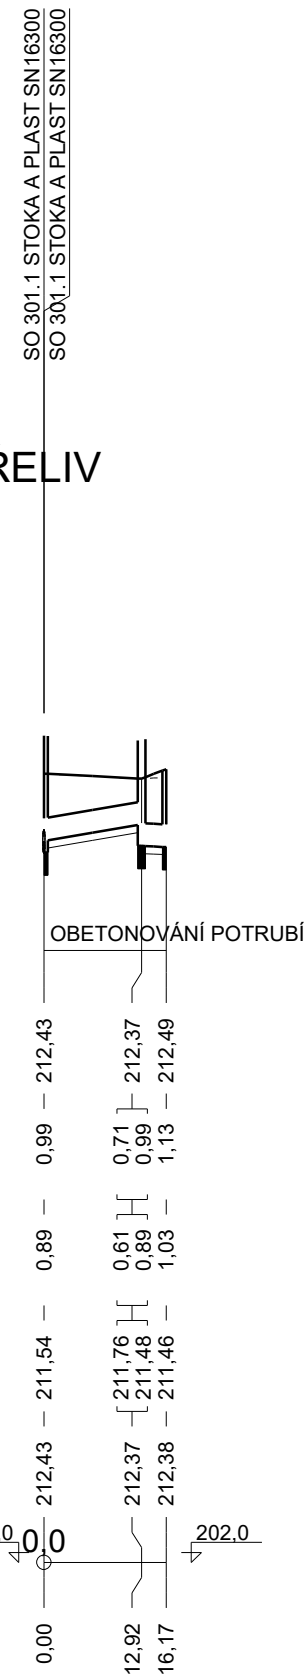

SKLON (‰) - DÉLKA (m)	A1	A2
PROFIL (mm) - MATERIÁL - DÉLKA (m)	B1	
KAPACITNÍ PRŮTOK (l/s) - RYCHLOST (m/s)	C1	C2
NÁVRHOVÝ PRŮTOK (l/s) - RYCHLOST (m/s)	D1	D2

SO 301 Odvodnění I/16

Objednatel:

ŘEDITELSTVÍ SILNIC A DÁLNIC

Čerčanská 2023/12, Krč, 140 00 Praha 4

Zhotovitel:



Vaňurova 505/17
460 07 Liberec 3

	Vypracoval	ING. J. VANCL		Zak. číslo	21-L113-001
	Zodp. projektant	ING. J. VANCL		Datum	02/2025
	Tech. kontrola	ING. D. LANDA		Stupeň	PDPS
	Akce I/16 MLADÁ BOLESLAV - MARTINOVICE			Počet formátů	3 x A4
Zhotovitel: Valbek, spol. s r.o. Vaňurova 505/17 460 07 Liberec 3	Příloha PODÉLNÝ PROFIL Č. 1 - 301.1			Měřítko	1 : 1 000 / 100
				Č. přílohy	Paré
				3.1	