

KATASTRÁLNÍ ÚZEMÍ
ČÍSLO PARCELY - NÁZEV ULICE
DRUH POVRCHU
VZDÁLENOSTI ŠACHET

SMĚROVÉ POMĚRY

301.5 STOKA A
[1:1000/100]

KÓTA UPRAVENÉHO TERÉNU

HLOUBKA VÝKOPU

HLOUBKA DNA POTRUBÍ


KÓTA DNA POTRUBÍ

KÓTA PŮVODNÍHO TERÉNU

STANIČENÍ[km]

STANIČENÍ [m]

SKLON (‰) - DÉLKA (m)
PROFIL (mm) - MATERIÁL - DÉLKA (m)
KAPACITNÍ PRŮTOK (l/s) - RYCHLOST (m/s)
NÁVRHOVÝ PRŮTOK (l/s) - RYCHLOST (m/s)

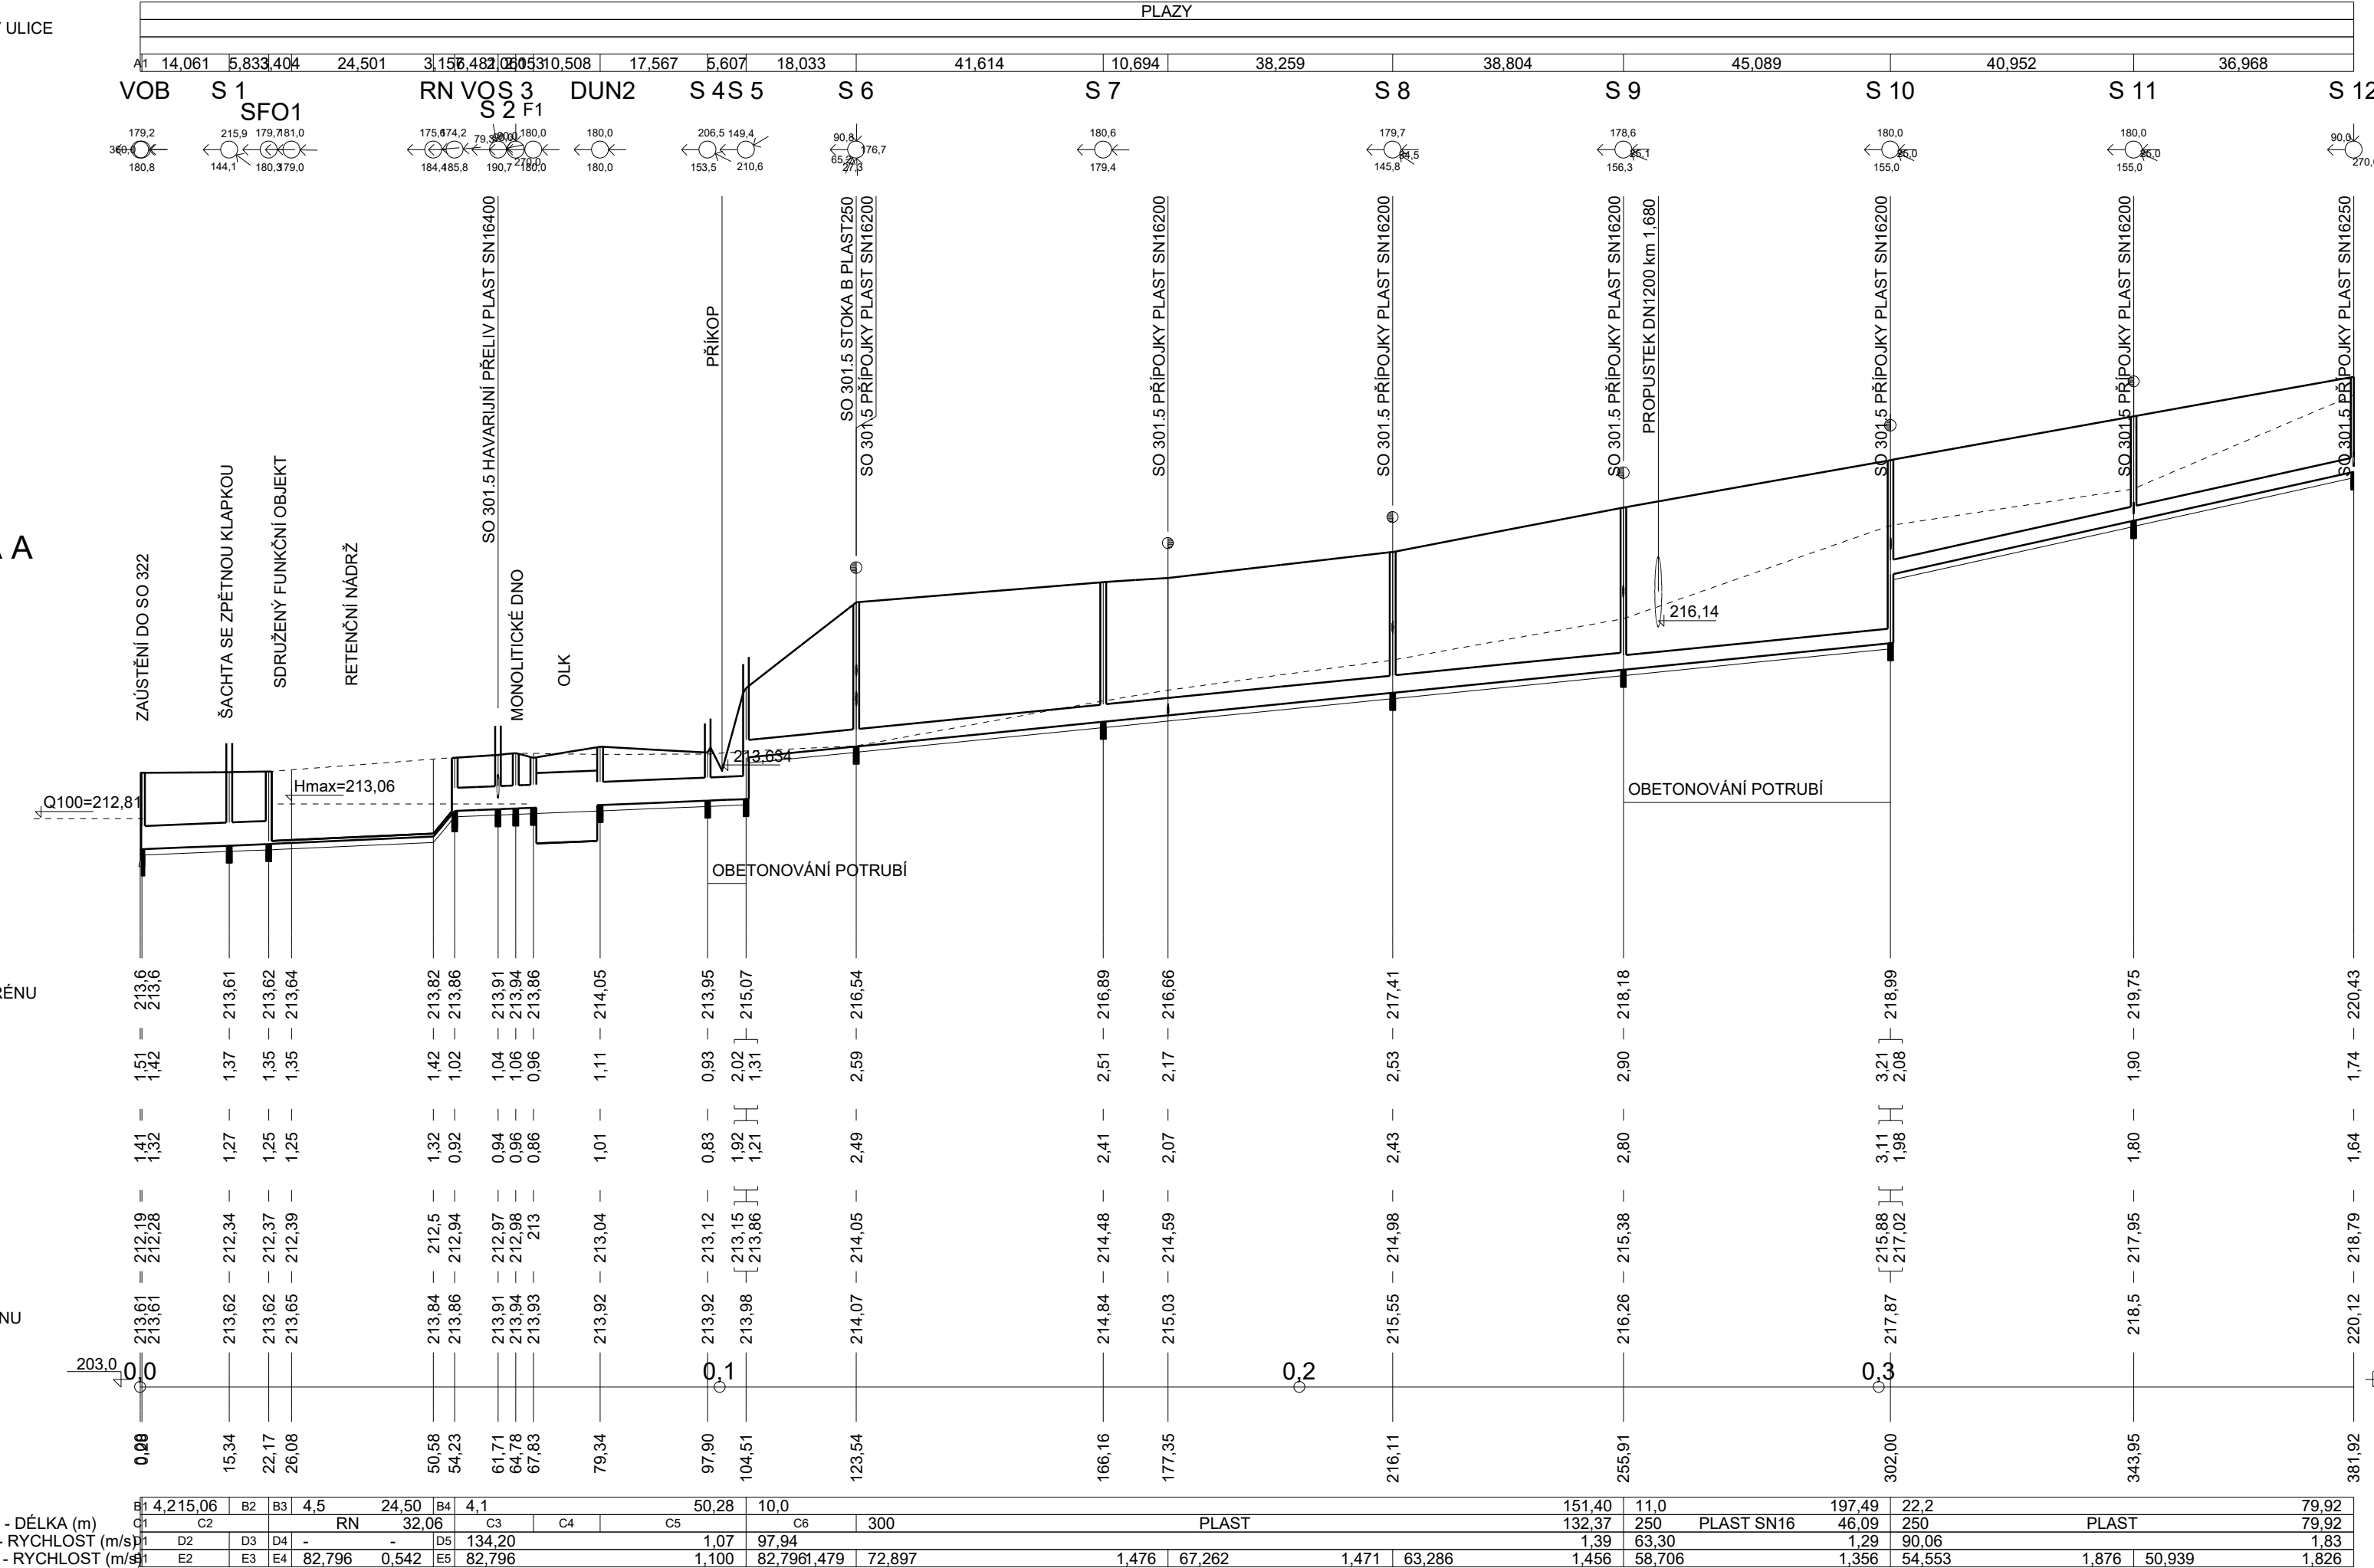

VZDÁLENOSTI ŠACHET	
A1	0,223
SKLON (‰) - DÉLKA (m)	
B1	324,6, 0,28
B2	4,0, 6,83
B3	5,1, 3,90
B4	120,3, 3,66
PROFIL (mm) - MATERIÁL - DÉLKA (m)	
C1	VO
C2	400, PLAST, 21,89
C3	400, PLAST SN16, 13,60
C4	OLK
C5	400, PLAST SN16, 25,17
C6	300, PLAST SN16, 19,03
KAPACITNÍ PRŮTOK (l/s) - RYCHLOST (m/s)	
D1	VO
D2	135,15, 1,08
D3	132,49, 1,05
D4	OLK
D5	RN
NÁVRHOVÝ PRŮTOK (l/s) - RYCHLOST (m/s)	
E1	82,796, 4,708
E2	82,796, 1,105
E3	82,796, 1,092
E4	82,796, 0,580
E5	82,796, 2,861
OZNAČENÍ ŠACHET	
F1	DUN1

KATASTRÁLNÍ ÚZEMÍ
ČÍSLO PARCELY - NÁZEV ULICE
DRUH POVRCHU
VZDÁLENOSTI ŠACHET

SMĚROVÉ POMĚRY

301.5 STOKA B
[1:1000/100]

KÓTA UPRAVENÉHO TERÉNU

HLOUBKA VÝKOPU

HLOUBKA DNA POTRUBÍ


KÓTA DNA POTRUBÍ

KÓTA PŮVODNÍHO TERÉNU

STANIČENÍ[km]

STANIČENÍ [m]

SKLON (‰) - DÉLKA (m)
PROFIL (mm) - MATERIÁL - DÉLKA (m)
KAPACITNÍ PRŮTOK (l/s) - RYCHLOST (m/s)
NÁVRHOVÝ PRŮTOK (l/s) - RYCHLOST (m/s)

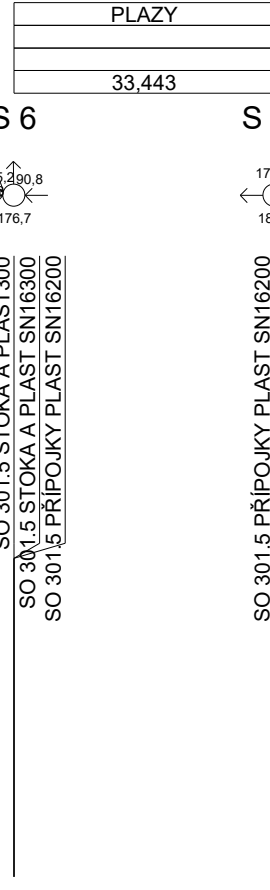

KATASTRÁLNÍ ÚZEMÍ
ČÍSLO PARCELY - NÁZEV ULICE
DRUH POVRCHU
VZDÁLENOSTI ŠACHET

SMĚROVÉ POMĚRY

301.5 HAVARIJNÍ PŘELIV
[1:1000/100]

KÓTA UPRAVENÉHO TERÉNU

HLOUBKA VÝKOPU

HLOUBKA DNA POTRUBÍ

KÓTA DNA POTRUBÍ

KÓTA PŮVODNÍHO TERÉNU

STANIČENÍ[km]

STANIČENÍ [m]

SKLON (‰) - DÉLKA (m)
PROFIL (mm) - MATERIÁL - DÉLKA (m)
KAPACITNÍ PRŮTOK (l/s) - RYCHLOST (m/s)
NÁVRHOVÝ PRŮTOK (l/s) - RYCHLOST (m/s)



SKLON (‰) - DÉLKA (m)	
A1	29,3, 9,36
A2	-5,0, 1,94
PROFIL (mm) - MATERIÁL - DÉLKA (m)	
B1	400, PLAST SN16, 11,30
KAPACITNÍ PRŮTOK (l/s) - RYCHLOST (m/s)	
C1	359,82, 2,86
C2	148,23, 1,18
NÁVRHOVÝ PRŮTOK (l/s) - RYCHLOST (m/s)	
D1	82,796
OZNAČENÍ ŠACHET	
E1	DUN-BP
E2	S 1-HP

Souřadnicový systém: S-JTSK
Výškový systém: Bpv

SO 301 Odvodnění I/16

Objednatel:



Ředitelství silnic a dálnic s. p.
Čerčanská 2023/12, Krč, 140 00 Praha 4

Zhotovitel:



Valbek, spol. s r.o.
Vaňurova 505/17
460 07 Liberec 3

	Vypracoval	ING. J. VANCL		Zak. číslo	21-L113-001	
	Zodp. projektant	ING. J. VANCL		Datum	02/2025	
	Tech. kontrola	ING. D. LANDA		Stupeň	PDPS	
	Akce			Počet formátů	6 x A4	
Zhotovitel: Valbek, spol. s r.o. Vaňurova 505/17 460 07 Liberec 3	I/16 MLADÁ BOLESLAV - MARTINOVICE			Měřítko	1 : 1 000 / 100	
				Č. přílohy	Paré	
	Příloha	PODÉLNÝ PROFIL Č. 5 - 301.5			3.5	