301.6 STOKA A
[1:1000/100]

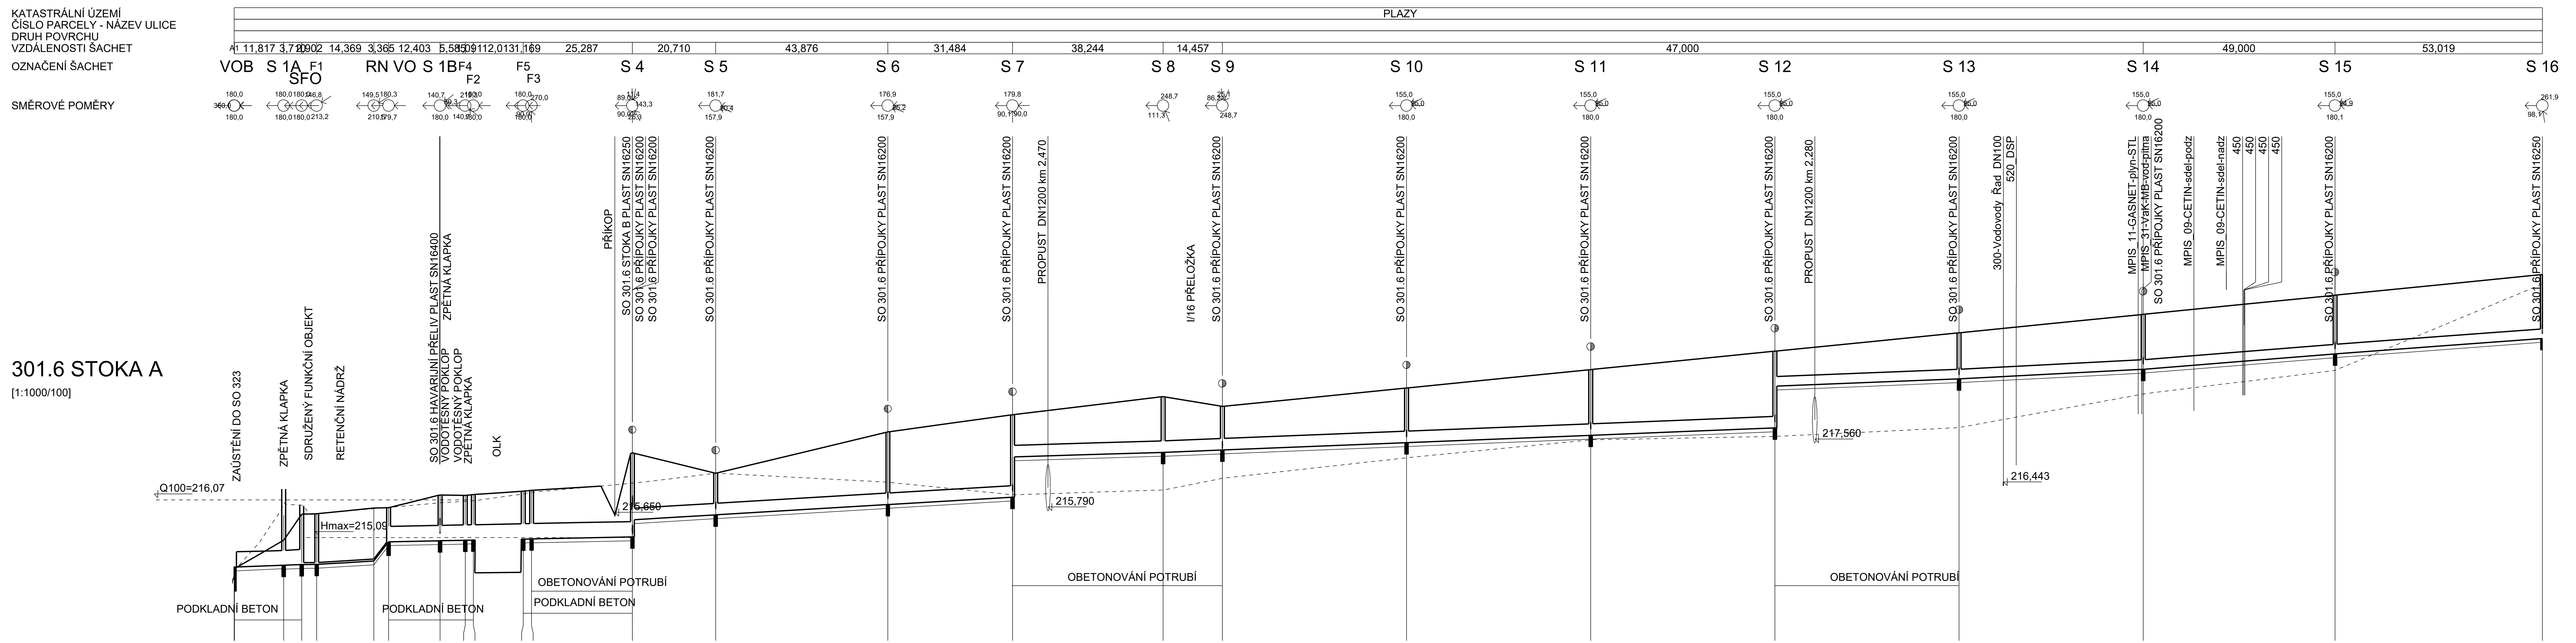
KATASTRÁLNÍ ÚZEMÍ
ČÍSLO PARCELY - NÁZEV ULICE
DRUH POVRCHU
VZDÁLENOSTI ŠACHET
OZNAČENÍ ŠACHET
SMĚROVÉ POMĚRY
PLAZY
A1 11,817 3,712,090 2 14,369 3,365 12,403 5,585 0,9112,013 1,169 25,287 20,710 43,876 31,484 38,244 14,457 47,000 49,000 53,019
VOB S 1A F1 SFO RN VO S 1B F4 F2 F5 F3 S 4 S 5 S 6 S 7 S 8 S 9 S 10 S 11 S 12 S 13 S 14 S 15 S 16
ZAÚSTĚNÍ DO SO 323
ZPĚTNÁ KLAPKA
SDRUŽENÝ FUNKČNÍ OBJEKT
RETENČNÍ NÁDRŽ
SO 301.6 HAVARIJNÍ PŘELIV PLAST SN16400
ZPĚTNÁ KLAPKA
VODOTĚSNÝ POKLOP
VODOTĚSNÝ POKLOP
ZPĚTNÁ KLAPKA
OLK
PŘÍKOP
SO 301.6 STOKA B PLAST SN16250
SO 301.6 PŘÍPOJKY PLAST SN16200
SO 301.6 PŘÍPOJKY PLAST SN16200
SO 301.6 PŘÍPOJKY PLAST SN16200
PROPUST DN1200 km 2,470
I/16 PŘELOŽKA
PROPUST DN1200 km 2,280
300-Vodovody Řad DN100 520 DSP
MPIS_11-GASNET-plyn-STL
MPIS_31-VaK-MB-vod-pitna
SO 301.6 PŘÍPOJKY PLAST SN16200
MPIS_09-CETIN-sdel-podz
MPIS_09-CETIN-sdel-nadz
450 450 450 450
SO 301.6 PŘÍPOJKY PLAST SN16250
Q100=216,07
Hmax=215,09
215,650
215,790
217,560
216,443
PODKLADNÍ BETON
PODKLADNÍ BETON
OBETONOVÁNÍ POTRUBÍ
PODKLADNÍ BETON
OBETONOVÁNÍ POTRUBÍ
OBETONOVÁNÍ POTRUBÍ

STANIČENÍ [m]	KÓTA UPRAVENÉHO TERÉNU	HLOUBKA VÝKOPU	HLOUBKA DNA POTRUBÍ	KÓTA DNA POTRUBÍ	KÓTA PŮVODNÍHO TERÉNU
0,00	214,25	0,06	0,00	214,25	214,23
0,11	214,28	0,10	-0,04	214,32	214,23
12,92	216,01	1,74	1,64	214,37	215,68
17,63	215,98	1,69	1,59	214,39	215,7
21,53	215,71	1,42	1,32	214,39	215,72
36,40	215,86	1,48	1,38	214,48	215,84
40,27	215,87	0,99	0,89	214,98	215,88
53,67	216,2	1,29	1,19	215,01	216
60,26	216,19	1,27	1,17	215,02	216,03
62,35	216,21	1,29	1,19	215,02	216,05
75,36	216,3	1,35	1,25	215,05	216,23
77,53	216,32	1,37	1,27	215,05	216,27
103,82	217,3	2,29 1,85	2,19 1,75	215,11 215,55	216,51
125,53	216,77	1,18	1,08	215,68	216,77
170,40	217,84	1,99	1,89	215,95	216,54
202,89	218,29	2,25 1,20	2,15 1,10	216,14 217,19	216,21
242,13	218,76	1,55	1,45	217,31	216,33
257,59	218,51	1,24	1,14	217,37	216,64
305,59	218,99	1,52	1,42	217,56	217,17
353,59	219,47	1,81	1,71	217,76	217,64
401,59	219,95	2,10 1,01	2,00 0,91	217,95 219,04	217,73
449,59	220,43	1,30	1,20	219,23	217,96
497,59	220,91	1,53	1,43	219,48	218,83
547,59	221,41	1,63	1,53	219,88	219,45
601,61	221,95	1,77	1,67	220,28	221,7

STANIČENÍ[km] 205,0 0,0 0,1 0,2 0,3 0,4 0,5 0,6 205,0

SKLON (‰) - DÉLKA (m): B1 3,7 17,53 | B2 6,114,87 | B3 2,0 63,55 | 6,0 66,59 | 5,9 32,48 | 3,0 39,24 | 4,0 207,46 | 5,2 48,00 | 8,0 50,00 | 7,4 54,02
PROFIL (mm) - MATERIÁL - DÉLKA (m): C1 C2 | RN 22,64 | C3 | C4 | C5 | 300 PLAST 99,07 | 300 PLAST SN16 102,70 | 300 PLAST 96,00 | 250 PLAST SN16 48,00 | 250 PLAST 152,02
KAPACITNÍ PRŮTOK (l/s) - RYCHLOST (m/s): D1 127,921,02 | D2 - - | D3 93,44 0,74 | 75,76 1,07 | 75,15 1,06 | 53,43 0,76 | 61,77 0,87 | 38,04 0,77 | 43,32 0,88 | 54,07 1,10 | 52,01 1,06
NÁVRHOVÝ PRŮTOK (l/s) - RYCHLOST (m/s): E1 E2 | E3 E4 | E5 76,795 0,795 | 59,515 1,144 | 54,957 1,140 | 50,959 1,128 | 47,278 0,803 | E6 | 42,513 0,928 | 37,749 0,897 | 32,984 0,851 | 28,219 0,825 | 23,461 0,864 | 18,512 0,992 | 13,260 0,870

VZDÁLENOSTI ŠACHET	
A1	0,394

SKLON (‰) - DÉLKA (m)	
B1	660,5, 0,11
B2	1,2, 3,90
B3	129,4, 3,87

PROFIL (mm) - MATERIÁL - DÉLKA (m)	
C1	VO
C2	400, PLAST, 17,53
C3	400, PLAST SN16, 22,08
C4	OLK
C5	400, PLAST SN16, 28,46

KAPACITNÍ PRŮTOK (l/s) - RYCHLOST (m/s)	
D1	VO
D2	RN
D3	RN

NÁVRHOVÝ PRŮTOK (l/s) - RYCHLOST (m/s)	
E1	76,795, 6,722
E2	76,795, 1,037
E3	76,795, 0,272
E4	76,795, 0,631
E5	76,795, 2,967
E6	47,278, 0,932

OZNAČENÍ ŠACHET	
F1	SFO VTOK
F2	DUN1
F3	S 3
F4	S 2
F5	DUN2

301.6 STOKA B
[1:1000/100]

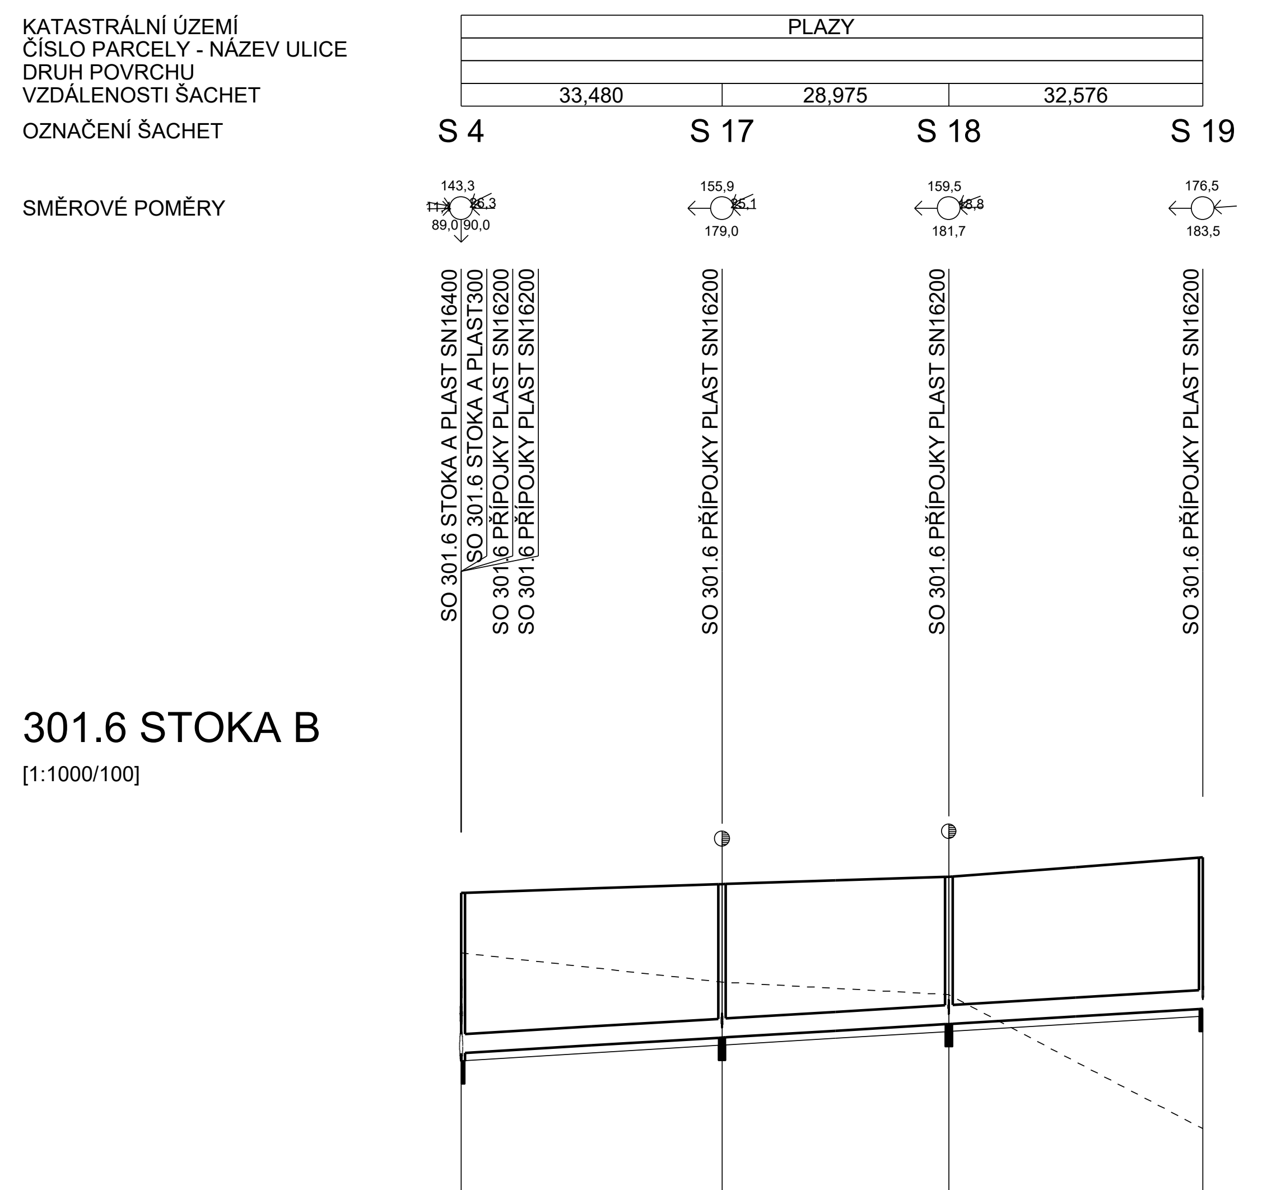
KATASTRÁLNÍ ÚZEMÍ
ČÍSLO PARCELY - NÁZEV ULICE
DRUH POVRCHU
VZDÁLENOSTI ŠACHET
OZNAČENÍ ŠACHET
SMĚROVÉ POMĚRY
PLAZY
33,480 28,975 32,576
S 4 S 17 S 18 S 19
SO 301.6 STOKA A PLAST SN16400
SO 301.6 STOKA A PLAST300
SO 301.6 PŘÍPOJKY PLAST SN16200
SO 301.6 PŘÍPOJKY PLAST SN16200
SO 301.6 PŘÍPOJKY PLAST SN16200
SO 301.6 PŘÍPOJKY PLAST SN16200
SO 301.6 PŘÍPOJKY PLAST SN16200

STANIČENÍ [m]	KÓTA UPRAVENÉHO TERÉNU	HLOUBKA VÝKOPU	HLOUBKA DNA POTRUBÍ	KÓTA DNA POTRUBÍ	KÓTA PŮVODNÍHO TERÉNU
0,00	217,3	2,22	2,12	215,18	216,51
34,48	217,41	2,13	2,03	215,39	216,12
64,46	217,51	2,05	1,95	215,57	215,95
98,03	217,77	2,10	2,00	215,77	214,18

STANIČENÍ[km] 205,0 0,0 205,0

SKLON (‰) - DÉLKA (m): 6,0 98,03
PROFIL (mm) - MATERIÁL - DÉLKA (m): 250 PLAST SN16 34,48 | 250 PLAST 63,55
KAPACITNÍ PRŮTOK (l/s) - RYCHLOST (m/s): 46,66 0,95
NÁVRHOVÝ PRŮTOK (l/s) - RYCHLOST (m/s): 10,679 0,757 | 7,057 0,678 | 3,502 0,579

301.6 HAVARIJNÍ PŘELIV
[1:1000/100]

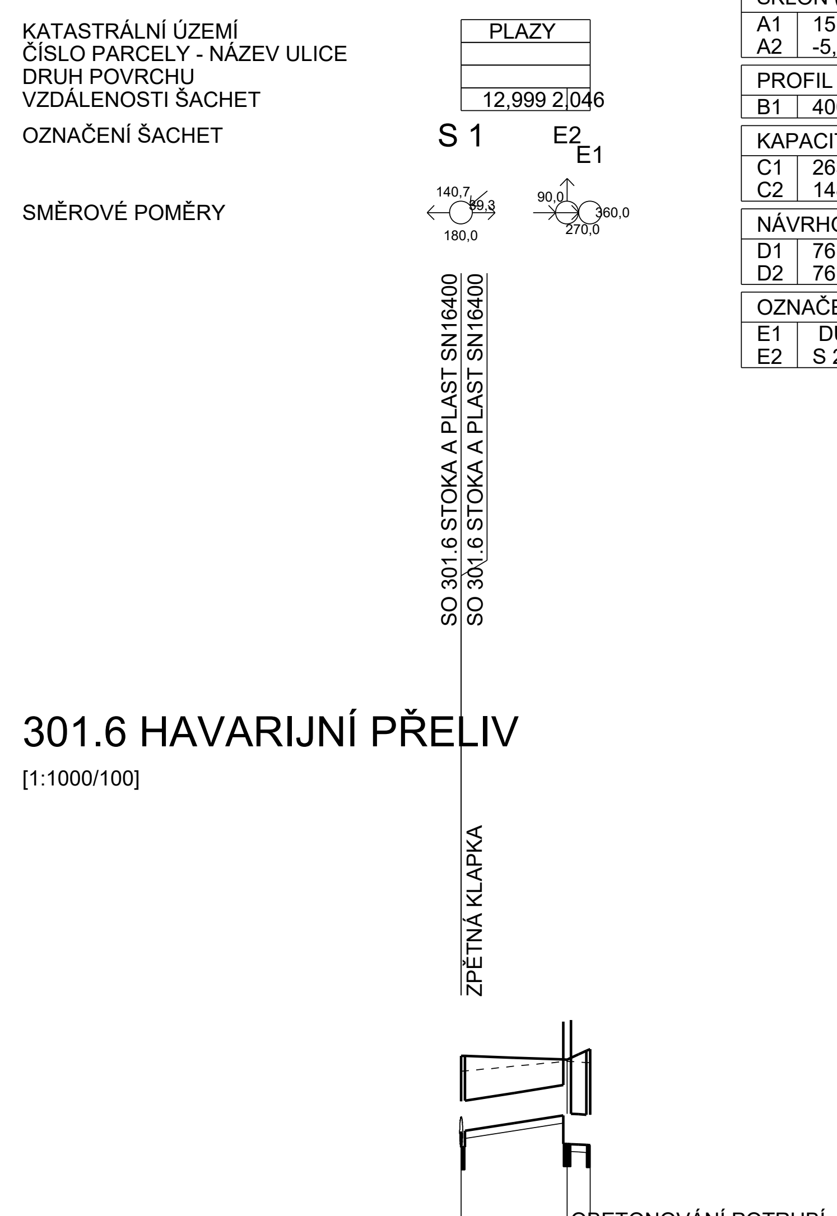
KATASTRÁLNÍ ÚZEMÍ
ČÍSLO PARCELY - NÁZEV ULICE
DRUH POVRCHU
VZDÁLENOSTI ŠACHET
OZNAČENÍ ŠACHET
SMĚROVÉ POMĚRY
PLAZY
12,999 2,046
S 1 E2 E1
SO 301.6 STOKA A PLAST SN16400
SO 301.6 STOKA A PLAST SN16400
ZPĚTNÁ KLAPKA
OBETONOVÁNÍ POTRUBÍ

STANIČENÍ [m]	KÓTA UPRAVENÉHO TERÉNU	HLOUBKA VÝKOPU	HLOUBKA DNA POTRUBÍ	KÓTA DNA POTRUBÍ	KÓTA PŮVODNÍHO TERÉNU
0,00	216,2	1,10	1,00	215,2	216
14,00	216,15	0,83 1,21	0,73 1,11	215,42 215,04	216,13
17,05	216,29	1,37	1,27	215,02	216,11

STANIČENÍ[km] 206,0 0,0 206,0

SKLON (‰) - DÉLKA (m): A1 | A2
PROFIL (mm) - MATERIÁL - DÉLKA (m): B1
KAPACITNÍ PRŮTOK (l/s) - RYCHLOST (m/s): C1 | C2
NÁVRHOVÝ PRŮTOK (l/s) - RYCHLOST (m/s): D1 | D2

SKLON (‰) - DÉLKA (m)	
A1	15,7, 14,00
A2	-5,0, 3,05

PROFIL (mm) - MATERIÁL - DÉLKA (m)	
B1	400, PLAST SN16, 17,05

KAPACITNÍ PRŮTOK (l/s) - RYCHLOST (m/s)	
C1	263,45, 2,10
C2	148,23, 1,18

NÁVRHOVÝ PRŮTOK (l/s) - RYCHLOST (m/s)	
D1	76,795
D2	76,795

OZNAČENÍ ŠACHET	
E1	DUN-BP
E2	S 20

Souřadnicový systém: S-JTSK
Výškový systém: Bpv

SO 301 Odvodnění I/16

Objednatel:
Ředitelství silnic a dálnic s. p.
Čerčanská 2023/12, Krč, 140 00 Praha 4

Zhotovitel:
Valbek, spol. s r.o.
Vaňurova 505/17
460 07 Liberec 3

Vypracoval	ING. J. VANCL	**Zak. číslo**	21-LI13-001
Zodp. projektant	ING. J. VANCL	**Datum**	02/2025
Tech. kontrola	ING. D. LANDA	**Stupeň**	PDPS
Akce	**I/16 MLADÁ BOLESLAV - MARTINOVICE**	**Počet formátů**	7 x A4
		Měřítko	1 : 1 000 / 100
		Č. přílohy	Paré
Příloha	PODÉLNÝ PROFIL Č. 6 - 301.6	**3.6**	

Zhotovitel:
Valbek, spol. s r.o.
Vaňurova 505/17
460 07 Liberec 3