301.9 STOKA A

[1:1000/100]

KATASTRÁLNÍ ÚZEMÍ
ČÍSLO PARCELY - NÁZEV ULICE
DRUH POVRCHU
VZDÁLENOSTI ŠACHET
OZNAČENÍ ŠACHET
SMĚROVÉ POMĚRY
SUKORADY
VOB
S 1
SFO
RN2
S 2
S 3A
S 5
S 6
S 7
S 8
S 9
S 10
S 11
S 12
S 13
S 14
S 15
S 16
S 17
S 18
S 19
S 20
S 21
S 22
S 23
S 24
S 25
S 26
S 27
S 28
S 29
S 30
S 31
S 32
S 33
S 34
S 35
S 36A
S 36B
S 37
S 38
S 39
S 40
S 41
S 42
ZAÚSTĚNÍ DO SO 326
ŠACHTA SE ZPĚTNOU KLAPKOU
SDRUŽENÝ FUNKČNÍ OBJEKT
RETENČNÍ NÁDRŽ
OLK
PŘÍKOP
Q100=217,58
Hmax=218,88
221,659
224,600
225,496
223,766
230,099
MPIS_19-CEZd-silno-VN-nadz
KÓTA UPRAVENÉHO TERÉNU
HLOUBKA VÝKOPU
HLOUBKA DNA POTRUBÍ
KÓTA DNA POTRUBÍ
KÓTA PŮVODNÍHO TERÉNU
STANIČENÍ[km]
STANIČENÍ [m]
SKLON (‰) - DÉLKA (m)
PROFIL (mm) - MATERIÁL - DÉLKA (m)
KAPACITNÍ PRŮTOK (l/s) - RYCHLOST (m/s)
NÁVRHOVÝ PRŮTOK (l/s) - RYCHLOST (m/s)
PLAST SN16
PLAST

VZDÁLENOSTI ŠACHET	
A1	-0,197
SKLON (‰) - DÉLKA (m)	
B1	297,3, 0,30
B2	4,0, 3,67
B3	117,7, 11,98
PROFIL (mm) - MATERIÁL - DÉLKA (m)	
C1	VO
C2	500, PLAST SN16, 20,20
C3	500, PLAST SN16, 29,23
C4	400, PLAST SN16, 24,69
KAPACITNÍ PRŮTOK (l/s) - RYCHLOST (m/s)	
D1	VO
D2	SFO
D3	RN
NÁVRHOVÝ PRŮTOK (l/s) - RYCHLOST (m/s)	
E1	196,490, 4,505
E2	196,490, 1,286
E3	196,490, 0,510
E4	196,490, 2,829
OZNAČENÍ ŠACHET	
F1	DUN2
F2	S 4
F3	S3B
F4	DUN3

301.9 STOKA B

[1:1000/100]

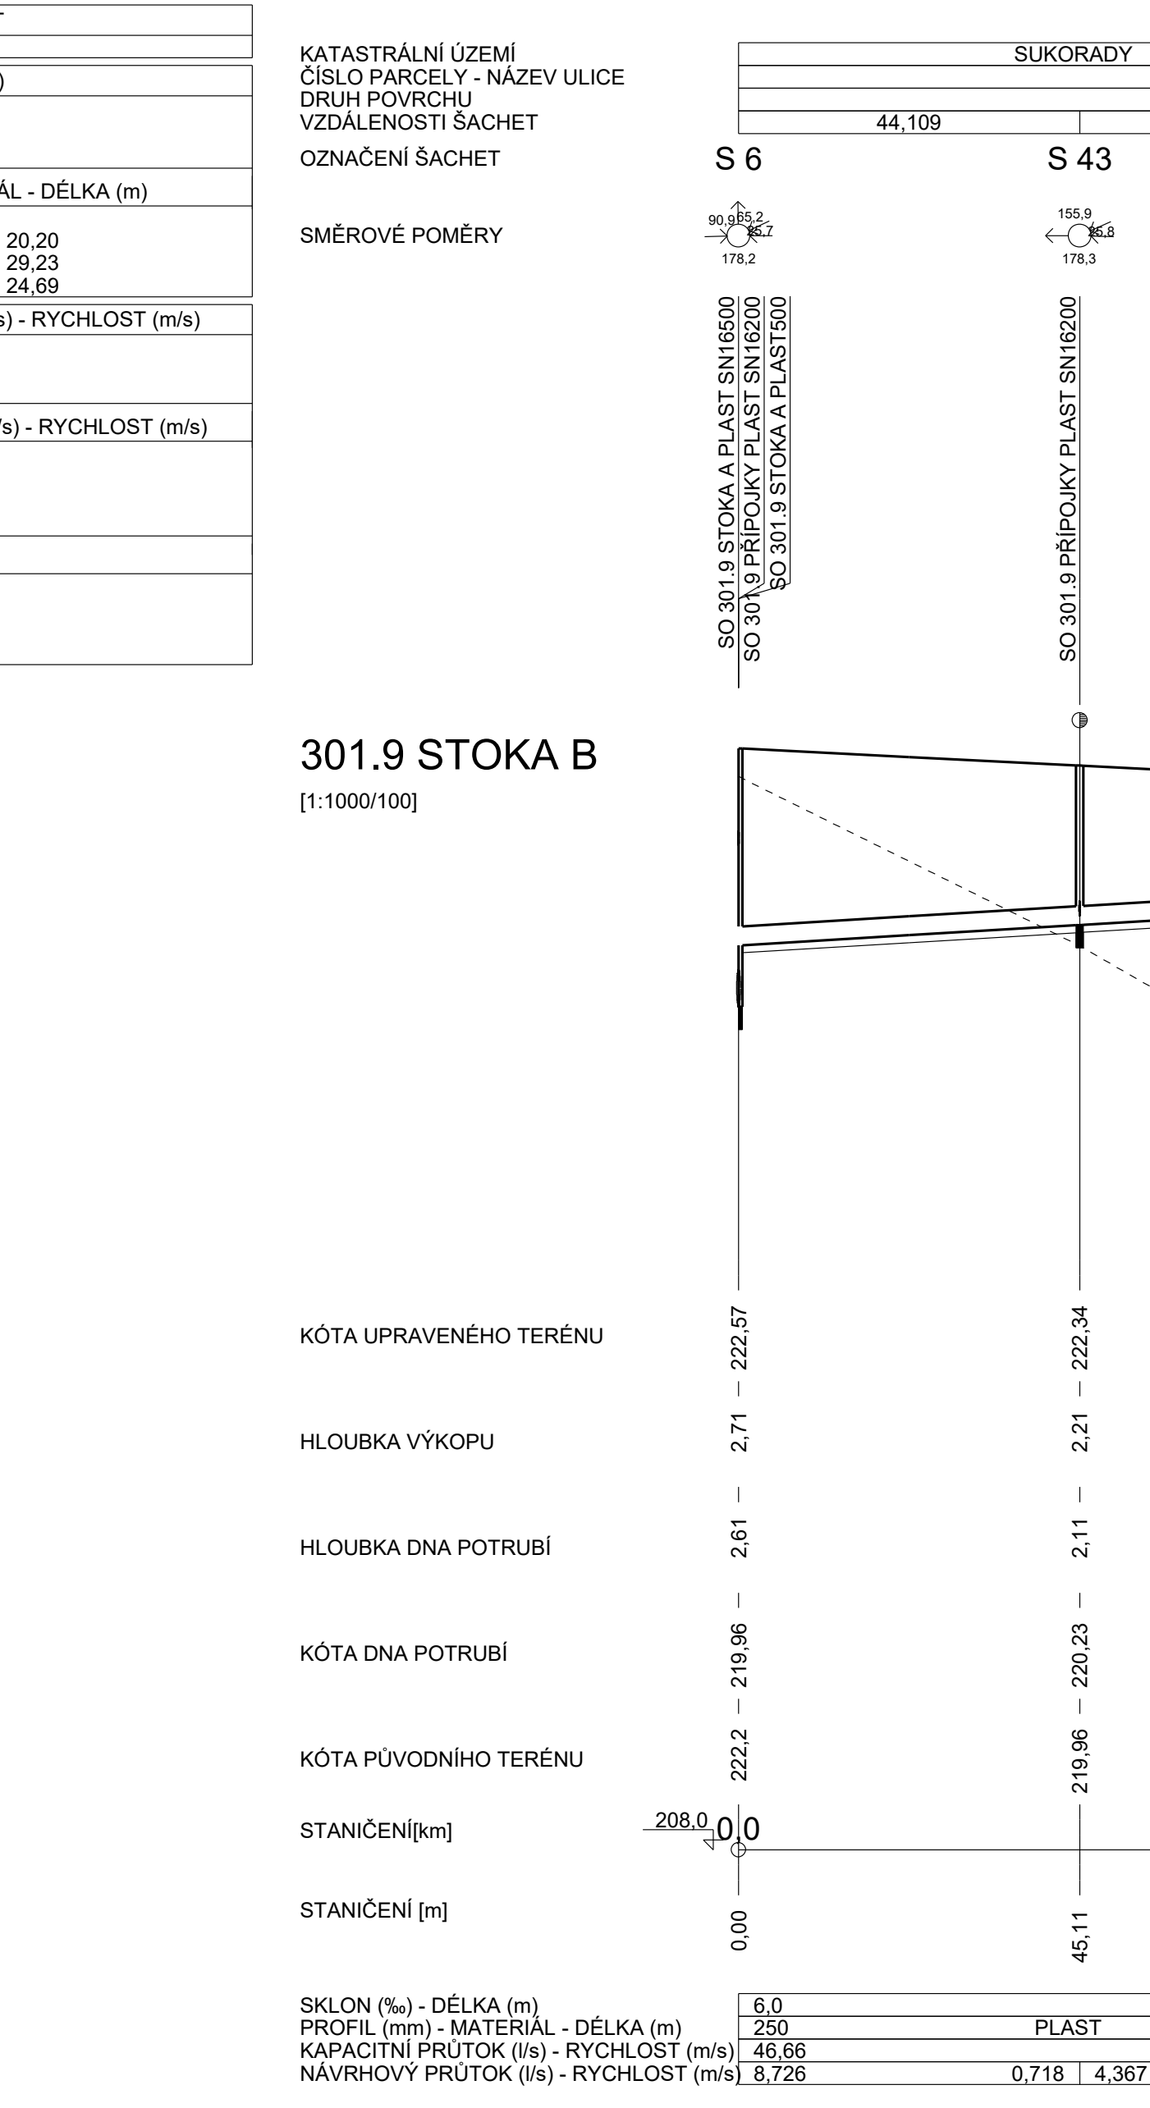
KATASTRÁLNÍ ÚZEMÍ
ČÍSLO PARCELY - NÁZEV ULICE
DRUH POVRCHU
VZDÁLENOSTI ŠACHET
OZNAČENÍ ŠACHET
SMĚROVÉ POMĚRY
SUKORADY
S 6
S 43
S 44
KÓTA UPRAVENÉHO TERÉNU
HLOUBKA VÝKOPU
HLOUBKA DNA POTRUBÍ
KÓTA DNA POTRUBÍ
KÓTA PŮVODNÍHO TERÉNU
STANIČENÍ[km]
STANIČENÍ [m]
SKLON (‰) - DÉLKA (m)
PROFIL (mm) - MATERIÁL - DÉLKA (m)
KAPACITNÍ PRŮTOK (l/s) - RYCHLOST (m/s)
NÁVRHOVÝ PRŮTOK (l/s) - RYCHLOST (m/s)
PLAST

301.9 STOKA C

[1:1000/100]

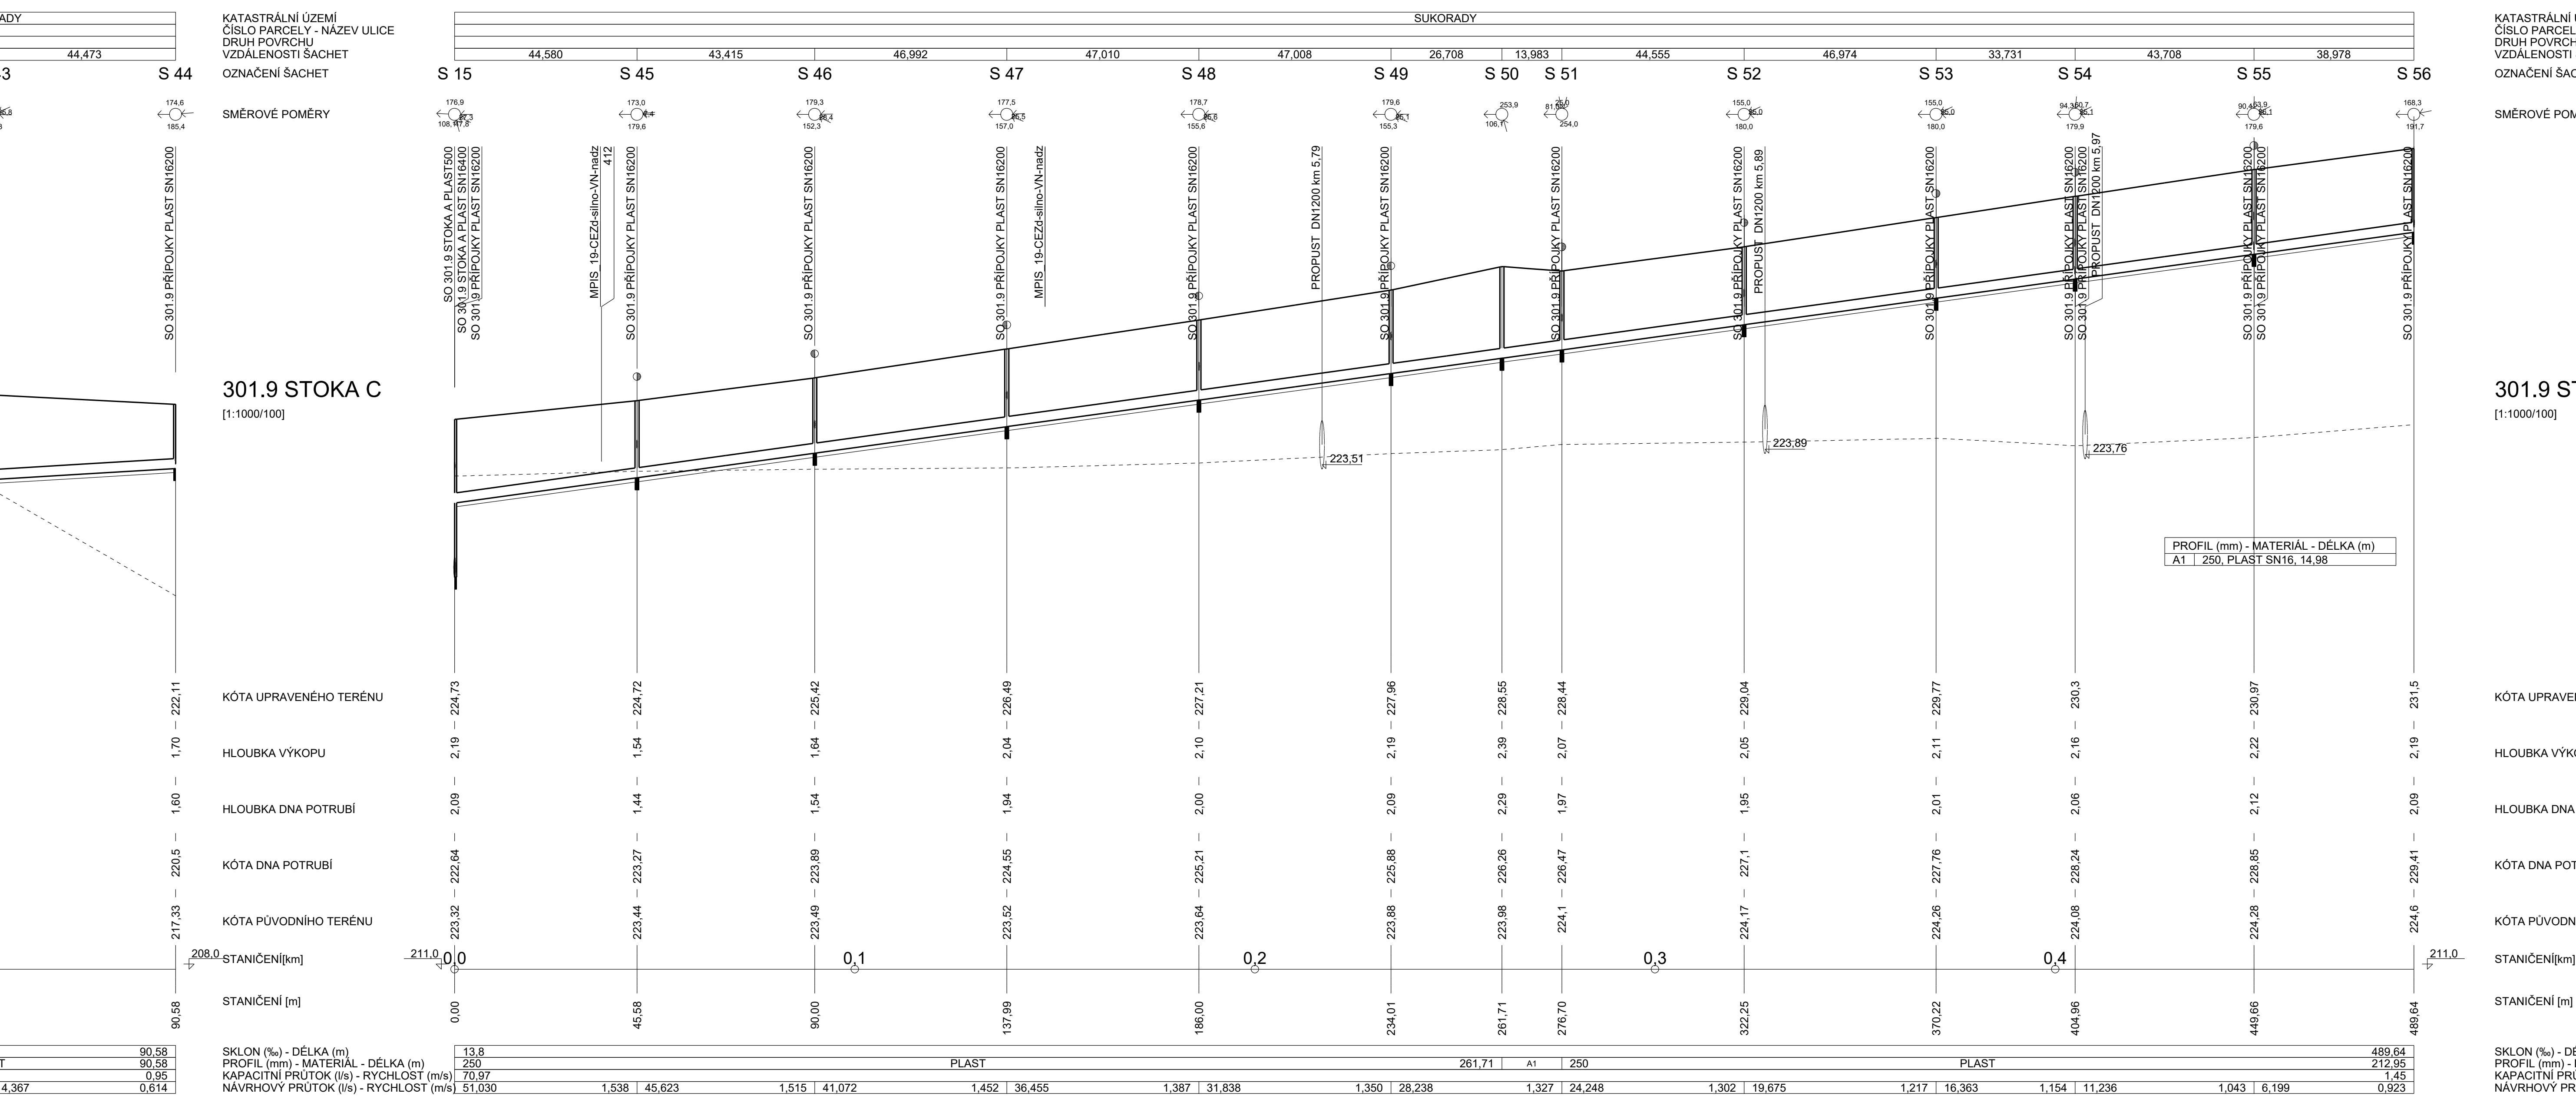
KATASTRÁLNÍ ÚZEMÍ
ČÍSLO PARCELY - NÁZEV ULICE
DRUH POVRCHU
VZDÁLENOSTI ŠACHET
OZNAČENÍ ŠACHET
SMĚROVÉ POMĚRY
SUKORADY
S 15
S 45
S 46
S 47
S 48
S 49
S 50
S 51
S 52
S 53
S 54
S 55
S 56
PROPUST DN1200 km 5,79
PROPUST DN1200 km 5,88
PROPUST DN1200 km 5,97
223,51
223,89
223,76
KÓTA UPRAVENÉHO TERÉNU
HLOUBKA VÝKOPU
HLOUBKA DNA POTRUBÍ
KÓTA DNA POTRUBÍ
KÓTA PŮVODNÍHO TERÉNU
STANIČENÍ[km]
STANIČENÍ [m]
SKLON (‰) - DÉLKA (m)
PROFIL (mm) - MATERIÁL - DÉLKA (m)
KAPACITNÍ PRŮTOK (l/s) - RYCHLOST (m/s)
NÁVRHOVÝ PRŮTOK (l/s) - RYCHLOST (m/s)
PLAST

PROFIL (mm) - MATERIÁL - DÉLKA (m)	
A1	250, PLAST SN16, 14,98

301.9 STOKA D

[1:1000/100]

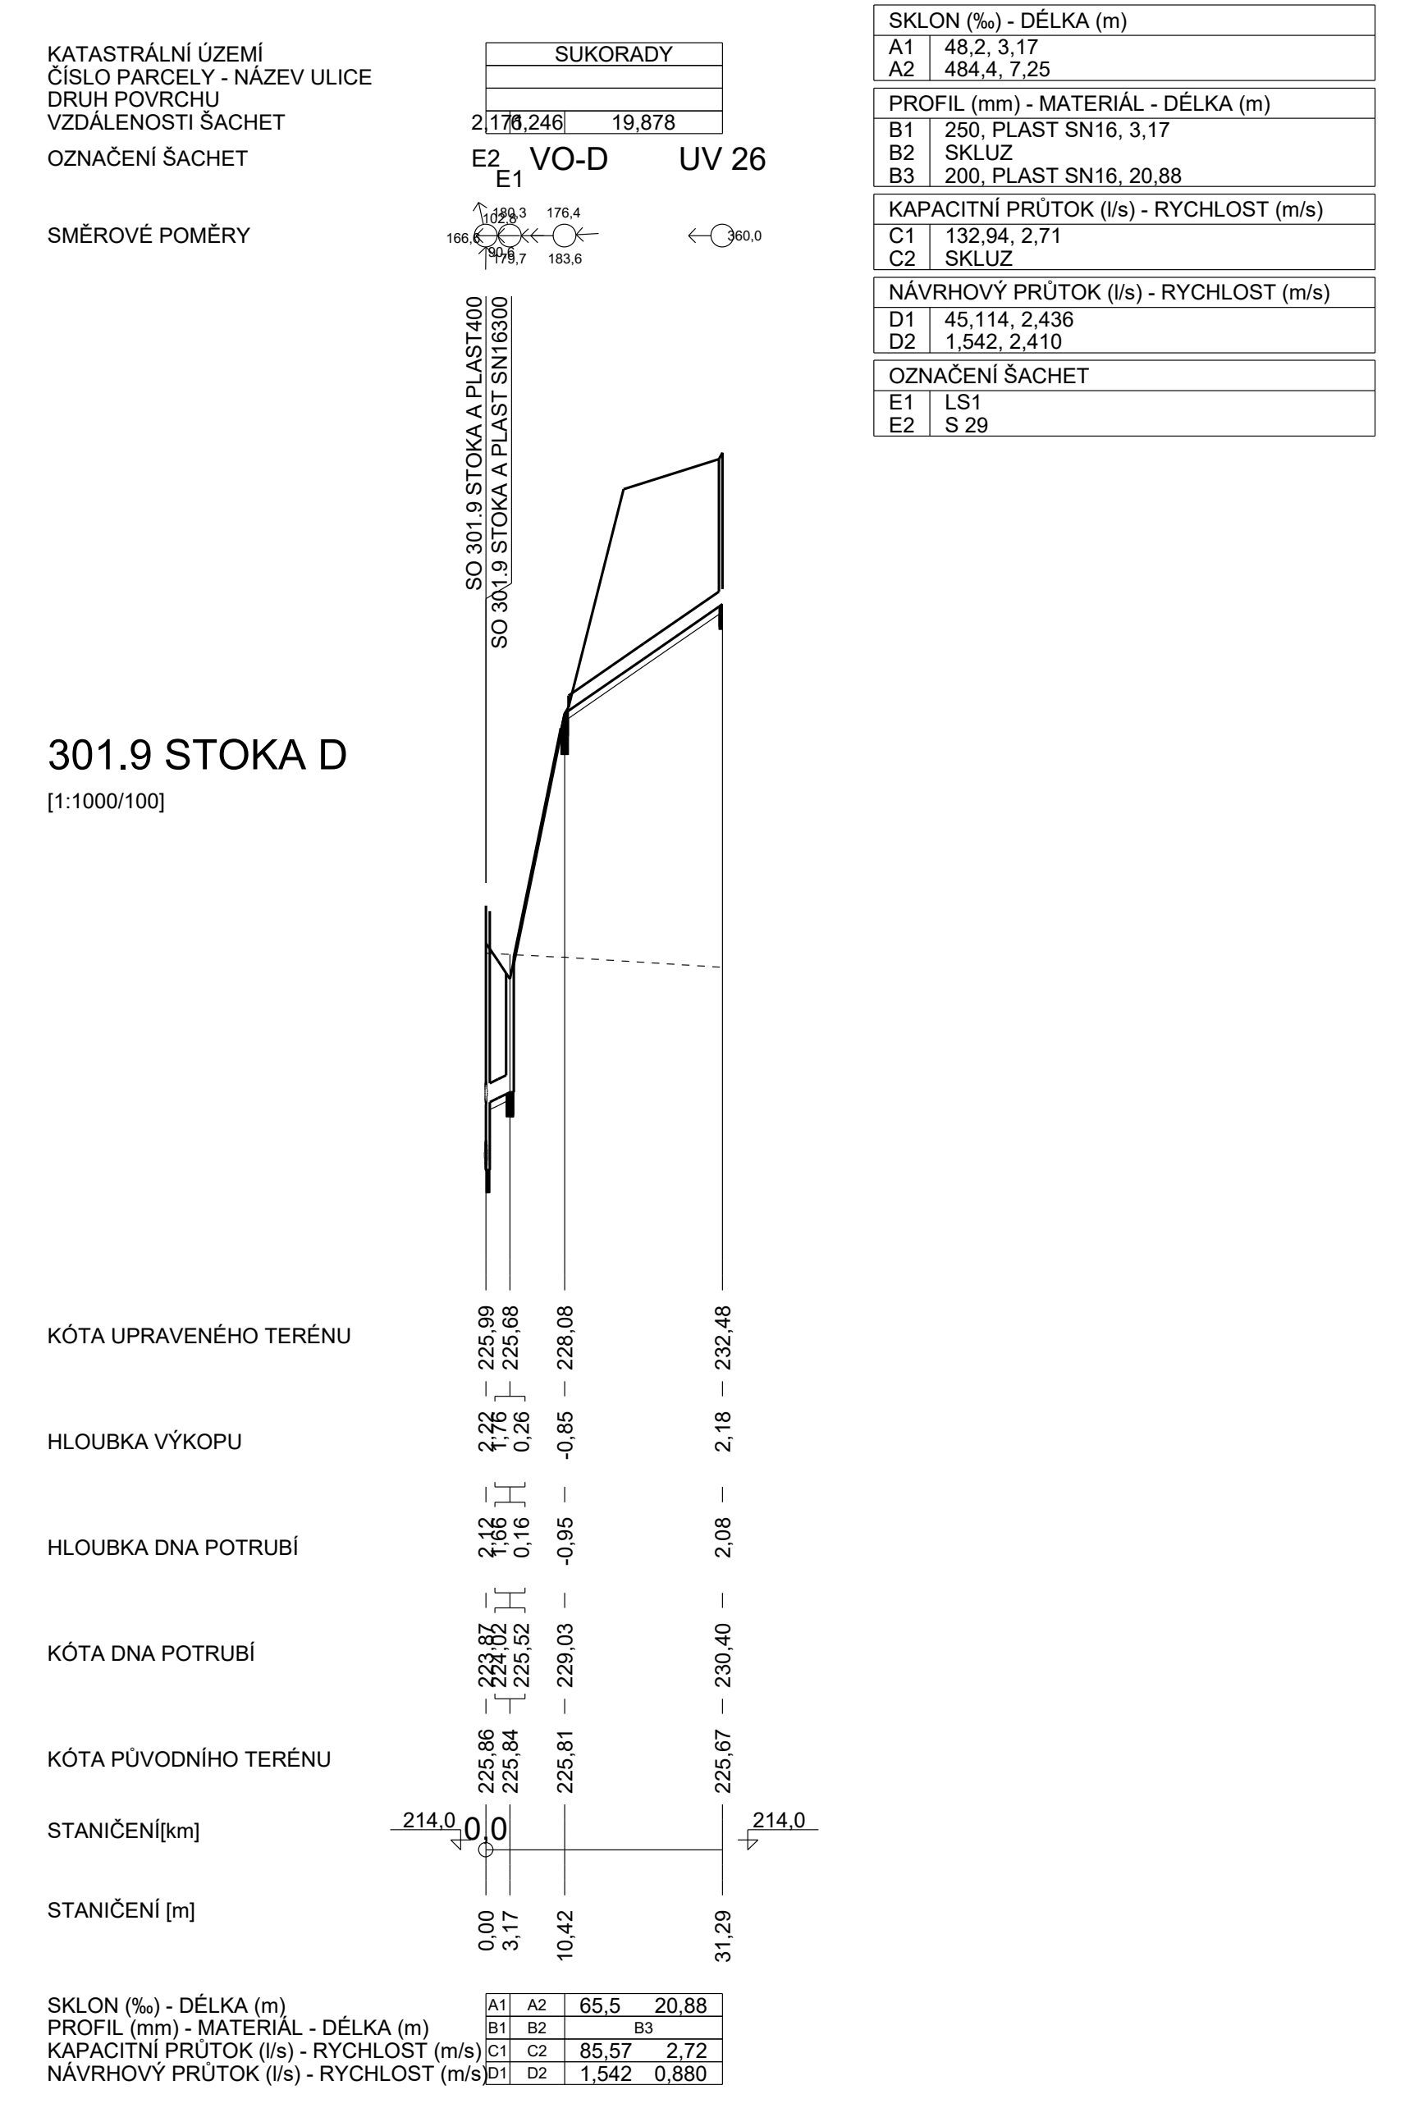
KATASTRÁLNÍ ÚZEMÍ
ČÍSLO PARCELY - NÁZEV ULICE
DRUH POVRCHU
VZDÁLENOSTI ŠACHET
OZNAČENÍ ŠACHET
SMĚROVÉ POMĚRY
SUKORADY
E2
E1
VO-D
UV 26
KÓTA UPRAVENÉHO TERÉNU
HLOUBKA VÝKOPU
HLOUBKA DNA POTRUBÍ
KÓTA DNA POTRUBÍ
KÓTA PŮVODNÍHO TERÉNU
STANIČENÍ[km]
STANIČENÍ [m]
SKLON (‰) - DÉLKA (m)
PROFIL (mm) - MATERIÁL - DÉLKA (m)
KAPACITNÍ PRŮTOK (l/s) - RYCHLOST (m/s)
NÁVRHOVÝ PRŮTOK (l/s) - RYCHLOST (m/s)

SKLON (‰) - DÉLKA (m)	
A1	48,2, 3,17
A2	484,4, 7,25
PROFIL (mm) - MATERIÁL - DÉLKA (m)	
B1	250, PLAST SN16, 3,17
B2	SKLUZ
B3	200, PLAST SN16, 20,88
KAPACITNÍ PRŮTOK (l/s) - RYCHLOST (m/s)	
C1	132,94, 2,71
C2	SKLUZ
NÁVRHOVÝ PRŮTOK (l/s) - RYCHLOST (m/s)	
D1	45,114, 2,436
D2	1,542, 2,410
OZNAČENÍ ŠACHET	
E1	LS1
E2	S 29

301.9 HAVARIJNÍ PŘELIV

[1:1000/100]

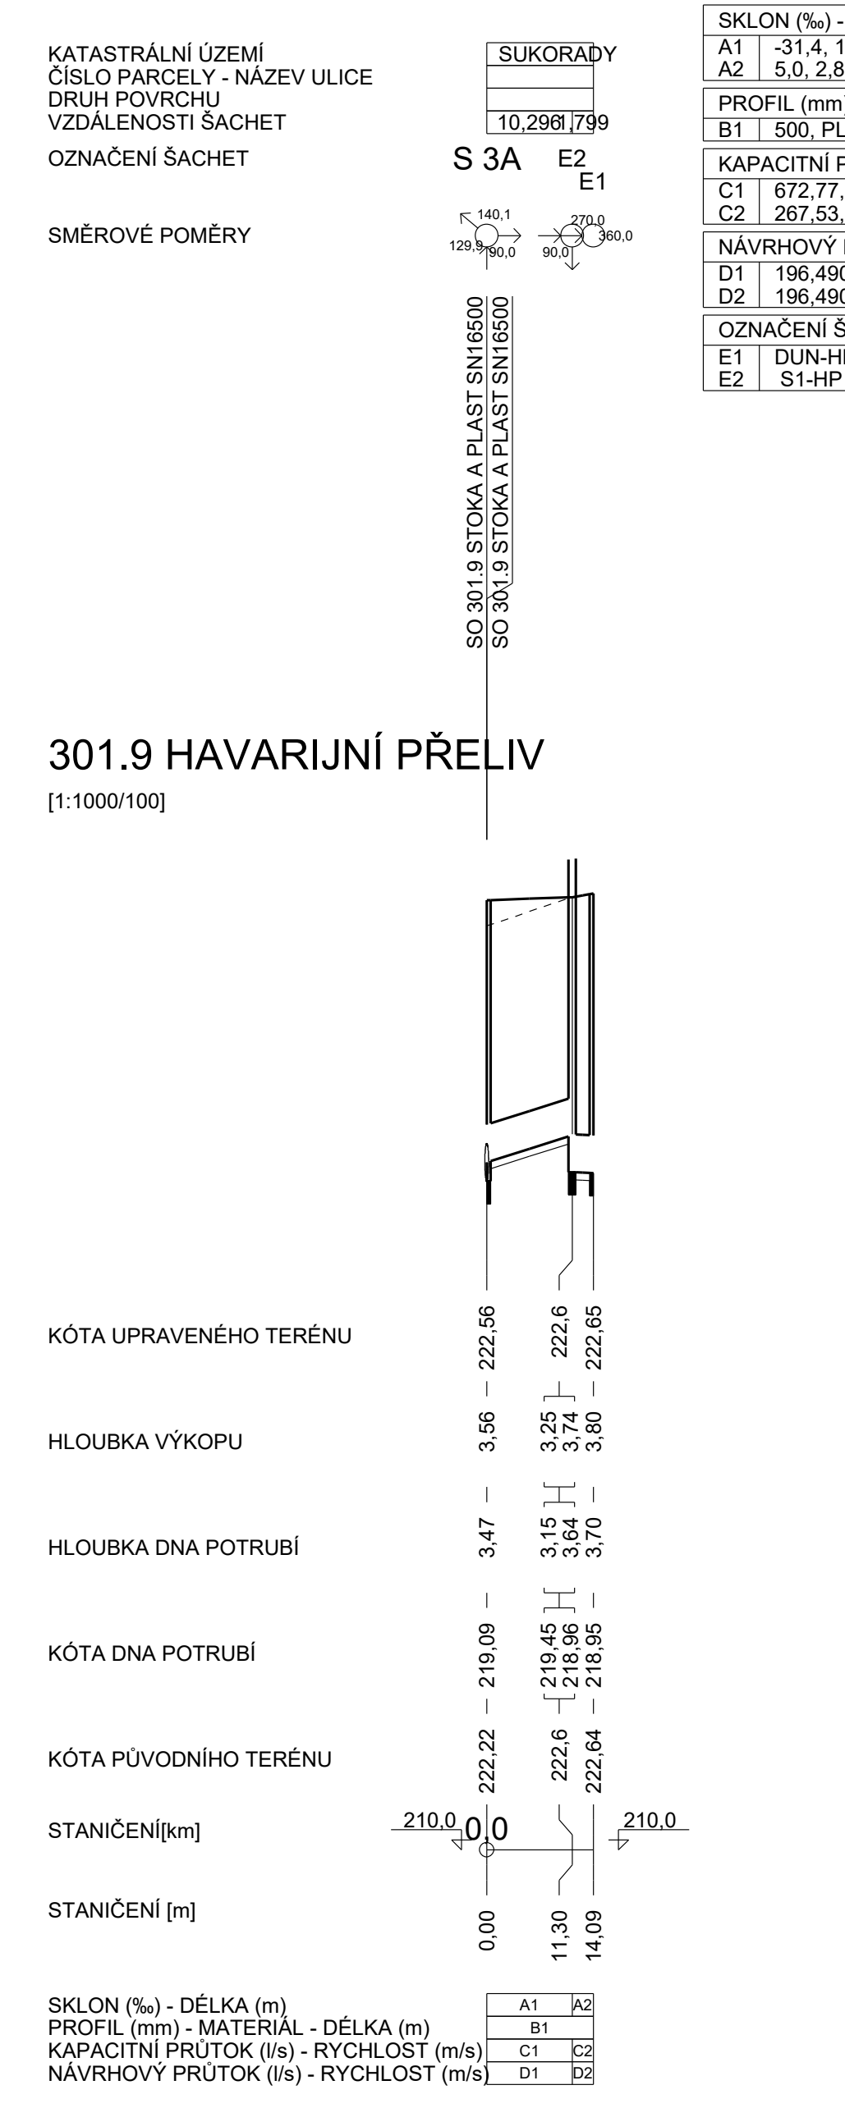
KATASTRÁLNÍ ÚZEMÍ
ČÍSLO PARCELY - NÁZEV ULICE
DRUH POVRCHU
VZDÁLENOSTI ŠACHET
OZNAČENÍ ŠACHET
SMĚROVÉ POMĚRY
SUKORADY
S 3A
E2
E1
KÓTA UPRAVENÉHO TERÉNU
HLOUBKA VÝKOPU
HLOUBKA DNA POTRUBÍ
KÓTA DNA POTRUBÍ
KÓTA PŮVODNÍHO TERÉNU
STANIČENÍ[km]
STANIČENÍ [m]
SKLON (‰) - DÉLKA (m)
PROFIL (mm) - MATERIÁL - DÉLKA (m)
KAPACITNÍ PRŮTOK (l/s) - RYCHLOST (m/s)
NÁVRHOVÝ PRŮTOK (l/s) - RYCHLOST (m/s)

SKLON (‰) - DÉLKA (m)	
A1	-31,4, 11,30
A2	5,0, 2,80
PROFIL (mm) - MATERIÁL - DÉLKA (m)	
B1	500, PLAST SN16, 14,09
KAPACITNÍ PRŮTOK (l/s) - RYCHLOST (m/s)	
C1	672,77, 3,43
C2	267,53, 1,36
NÁVRHOVÝ PRŮTOK (l/s) - RYCHLOST (m/s)	
D1	196,490
D2	196,490
OZNAČENÍ ŠACHET	
E1	DUN-HP
E2	S1-HP

Souřadnicový systém: S-JTSK
Výškový systém: Bpv

SO 301 Odvodnění I/16

Objednatel:
ŘEDITELSTVÍ SILNIC A DÁLNIC
Ředitelství silnic a dálnic s. p.
Čerčanská 2023/12, Krč, 140 00 Praha 4

Zhotovitel:
Valbek
Valbek, spol. s r.o.
Vaňurova 505/17
460 07 Liberec 3

Vypracoval	ING. J. VANCL			Zak. číslo	21-LI13-001
Zodp. projektant	ING. J. VANCL			Datum	02/2025
Tech. kontrola	ING. D. LANDA			Stupeň	PDPS
Akce				Počet formátů	16 x A4
I/16 MLADÁ BOLESLAV - MARTINOVICE				Měřítko	1 : 1 000 / 100
				Č. přílohy	Paré
Příloha				3.9	
PODÉLNÝ PROFIL Č. 9 - 301.9					

Zhotovitel:
Valbek, spol. s r.o.
Vaňurova 505/17
460 07 Liberec 3