



VZOROVÝ ŘEZ ŠACHTOU NA TRUBNÍCH STOKÁCH DN 250-600, 800

ZÁKLADNÍ SESTAVA

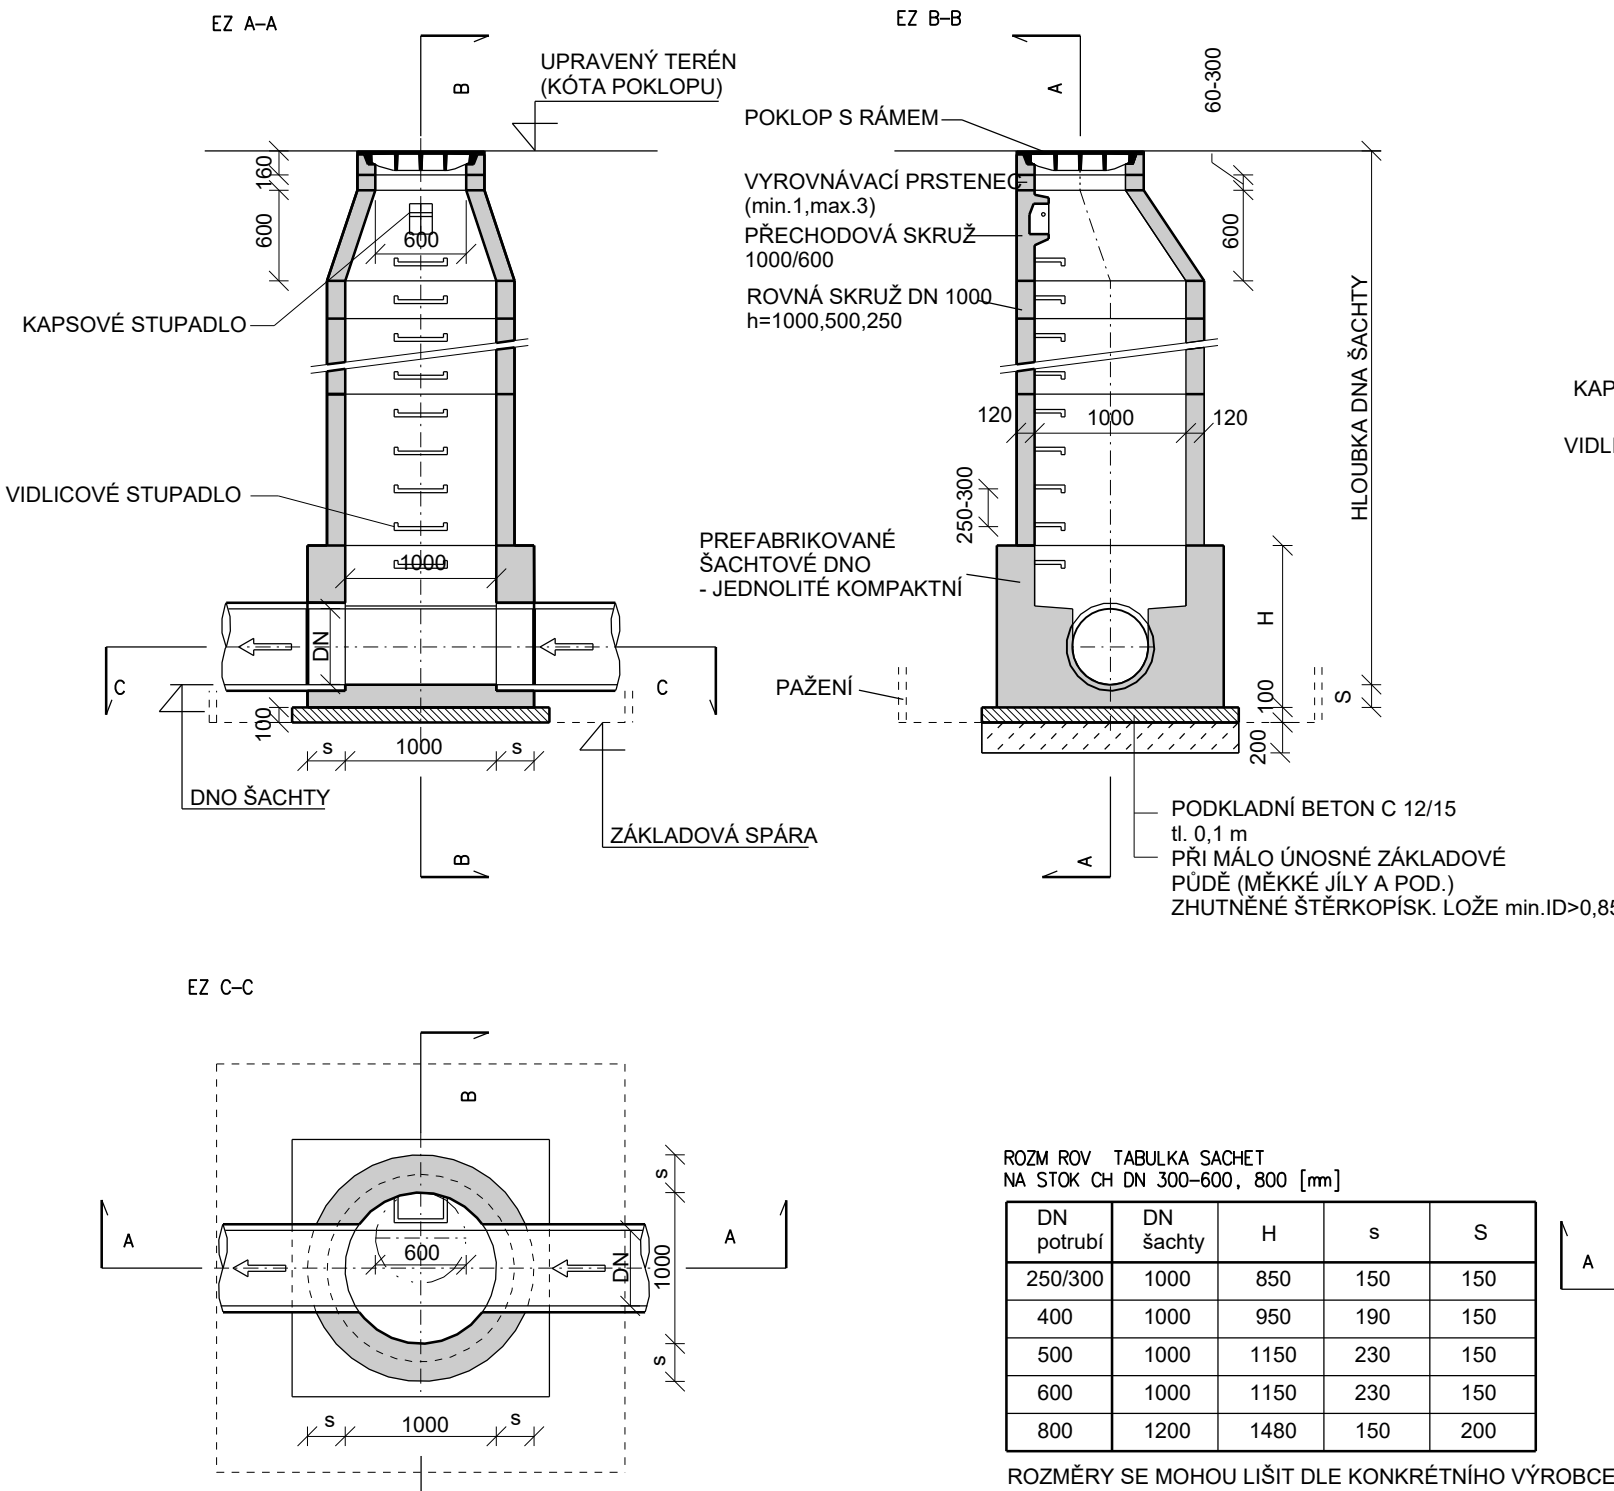


VZOROVÝ ŘEZ ŠACHTOU NA STOKÁCH DN 800, DN 1000

ZÁKLADNÍ SESTAVA

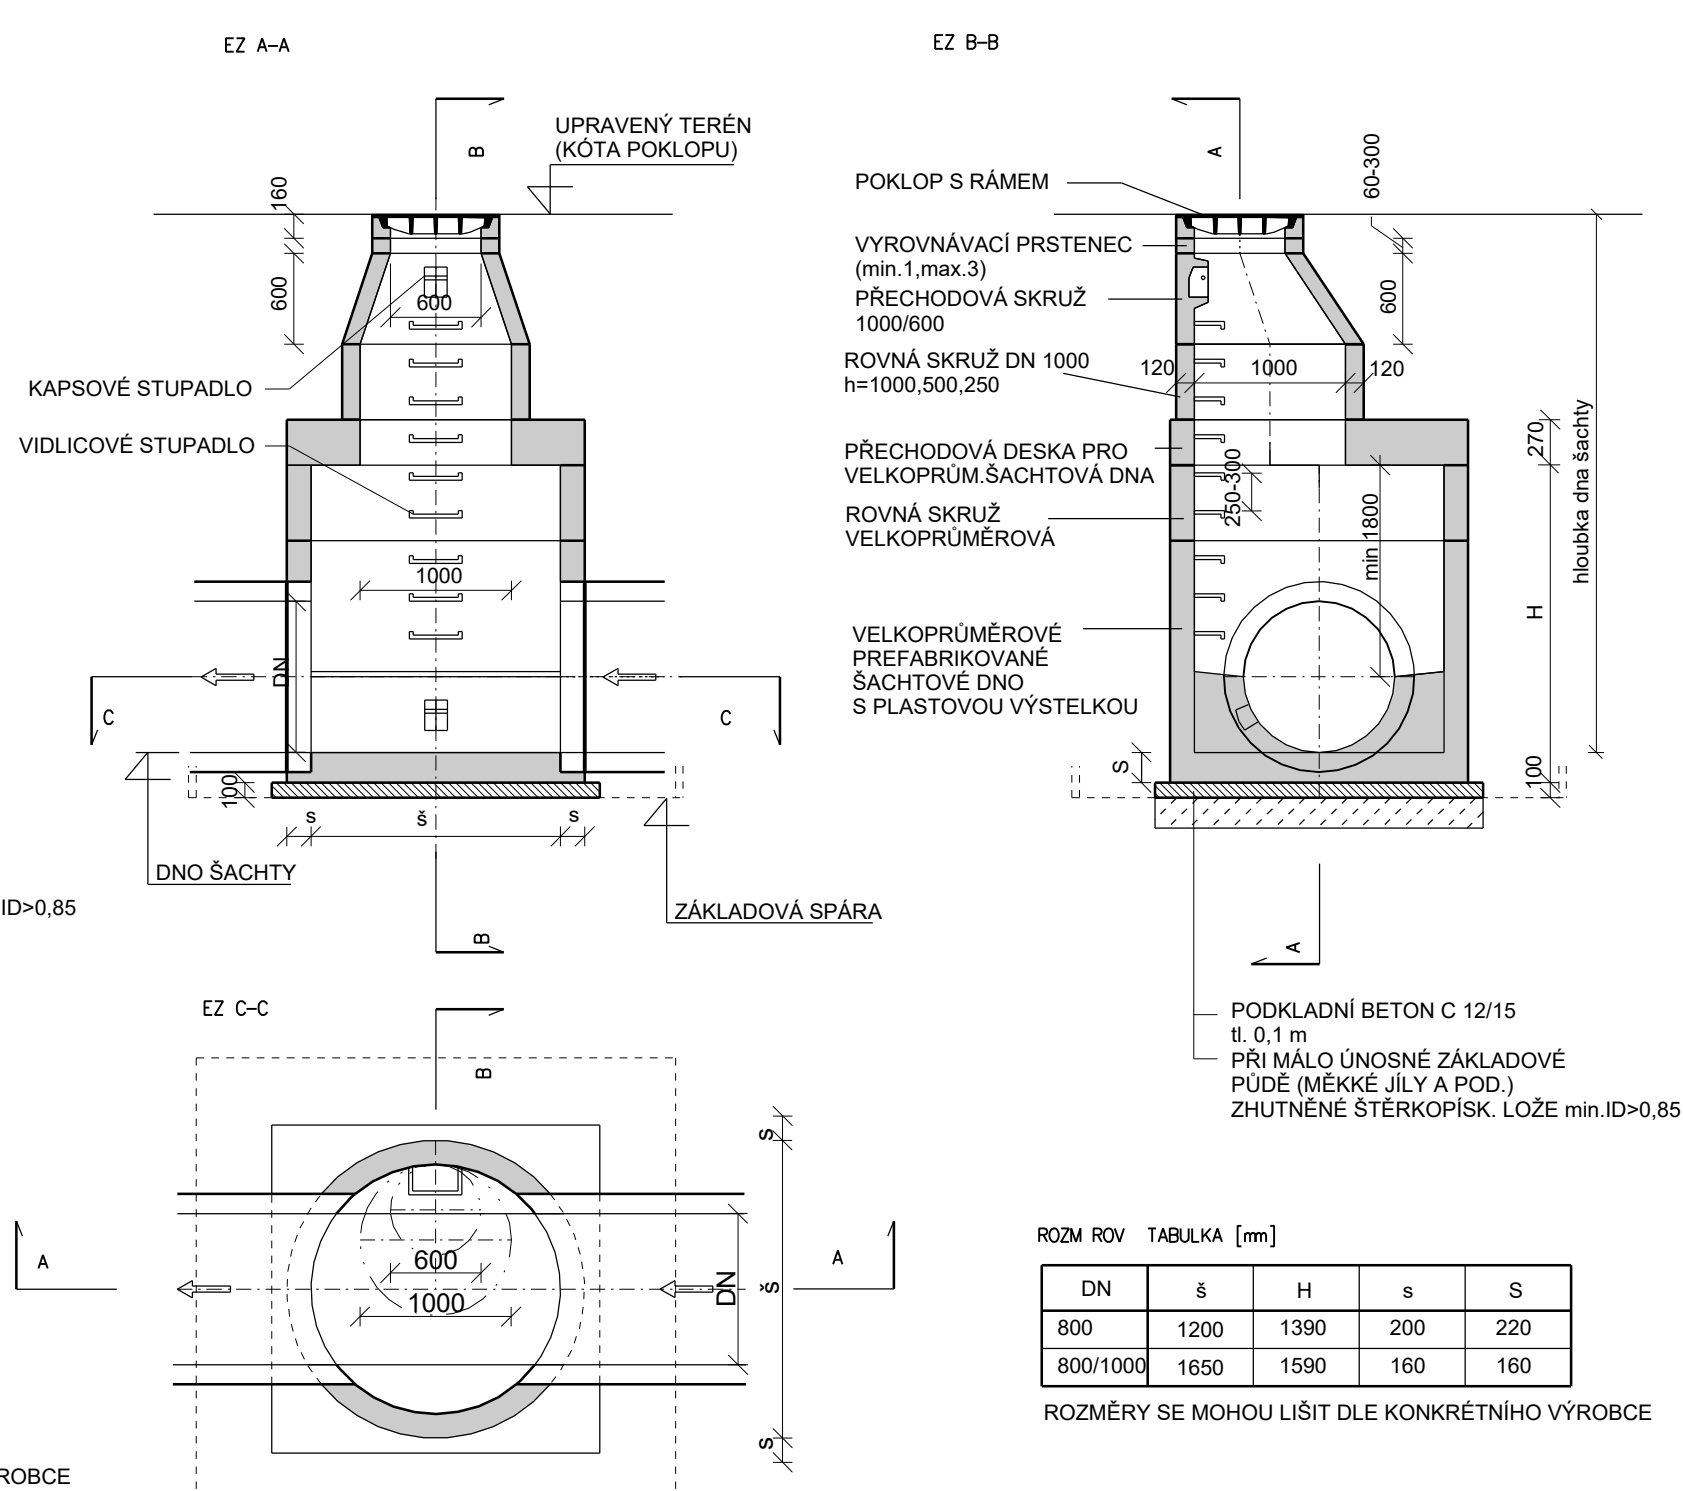


VZOROVÝ ŘEZ ŠACHTOU SE ZPĚTNOU KLAPKOU NA TRUBNÍCH STOKÁCH DO DN 600

M 1:50

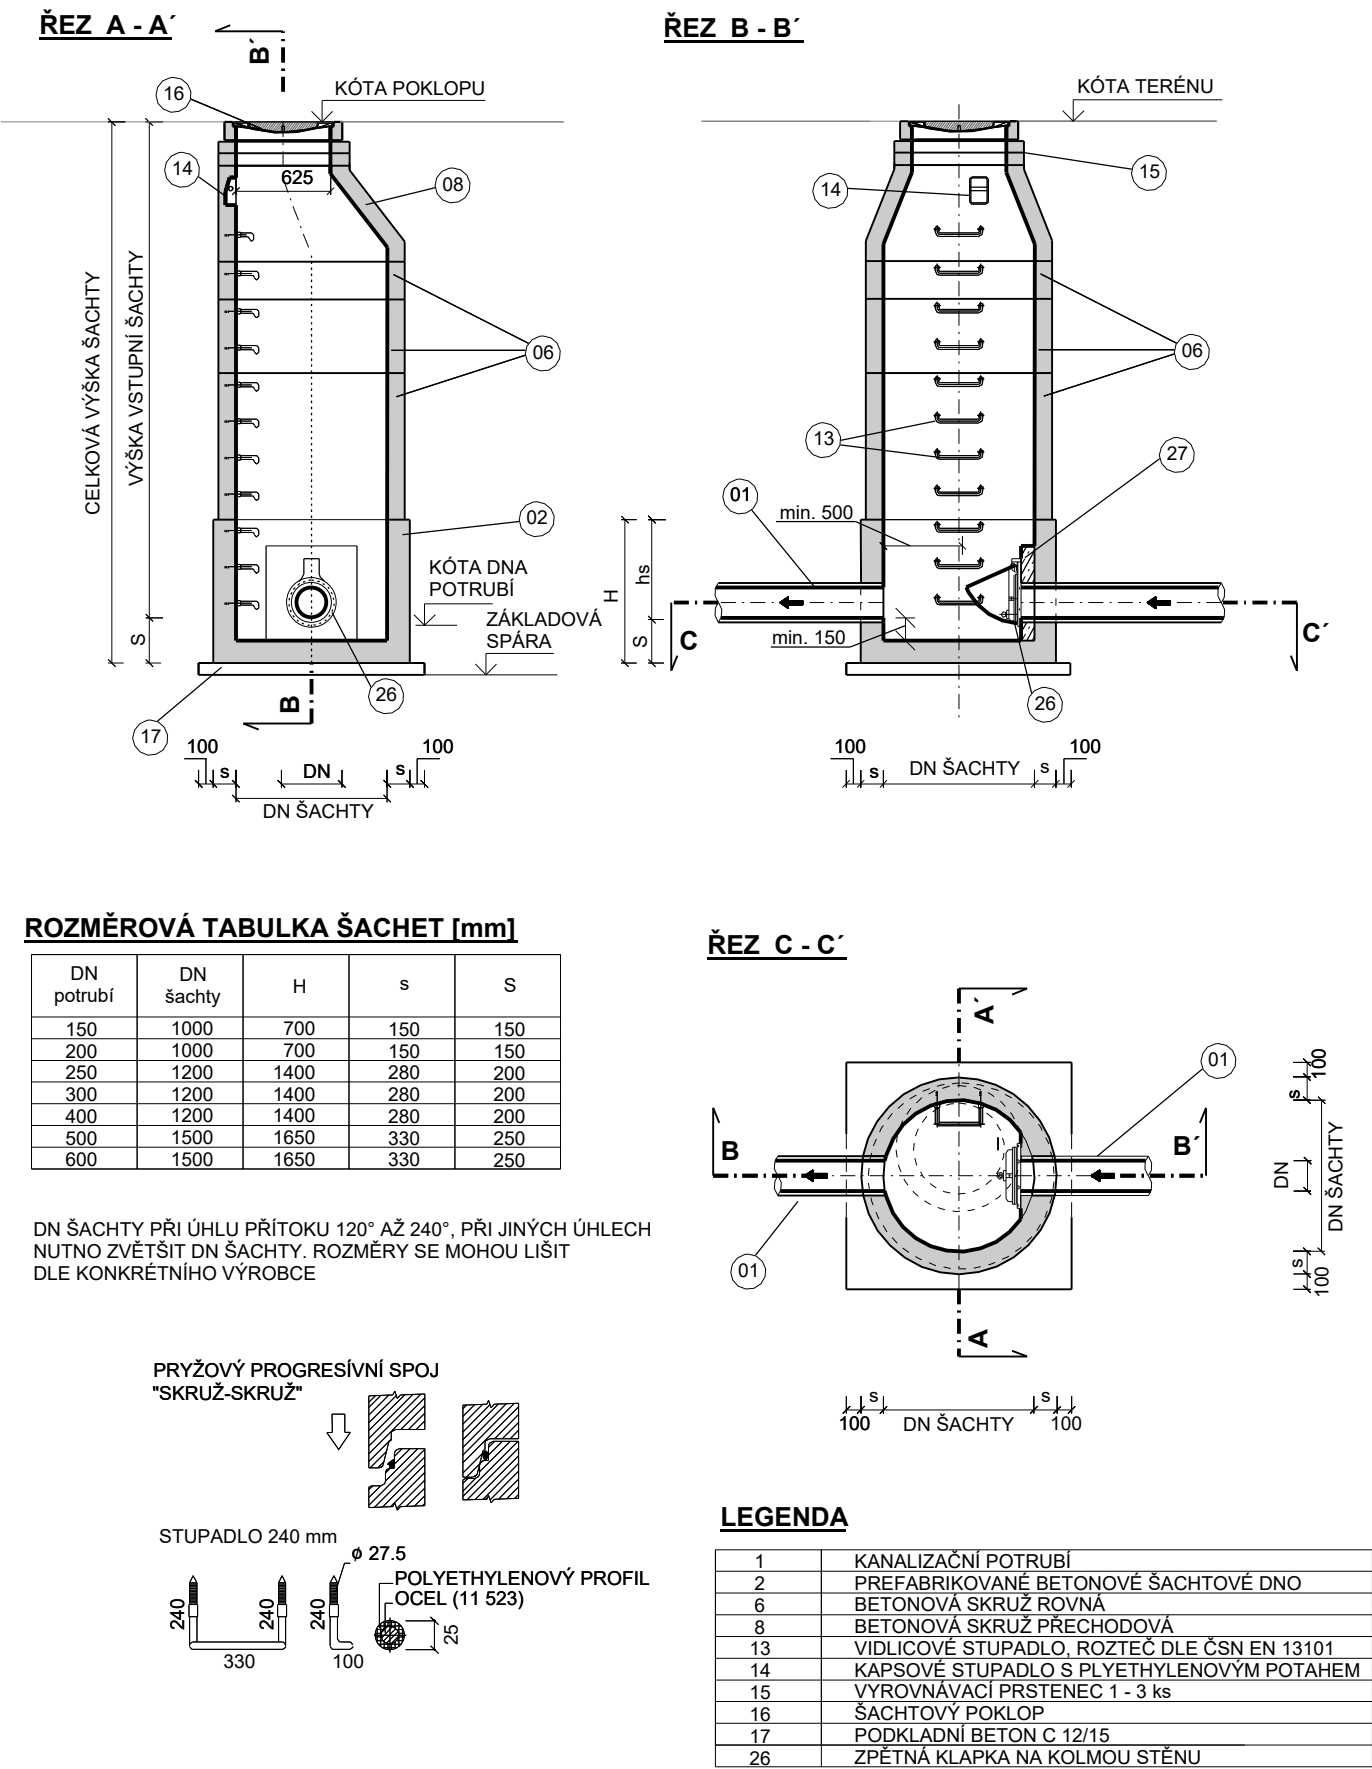


SPADIŠTĚ NA POTRUBÍ DN 250+600 Z BET. PREFABRIKÁTŮ

-SE SVISLÝM POTRUBÍM (U STOK PŘECHÁZEJÍCÍCH ŽÁREZY, KDE SE PŘEDPOKLÁDÁ STÁLÝ PŘÍTOK Z DRENÁŽÍ)

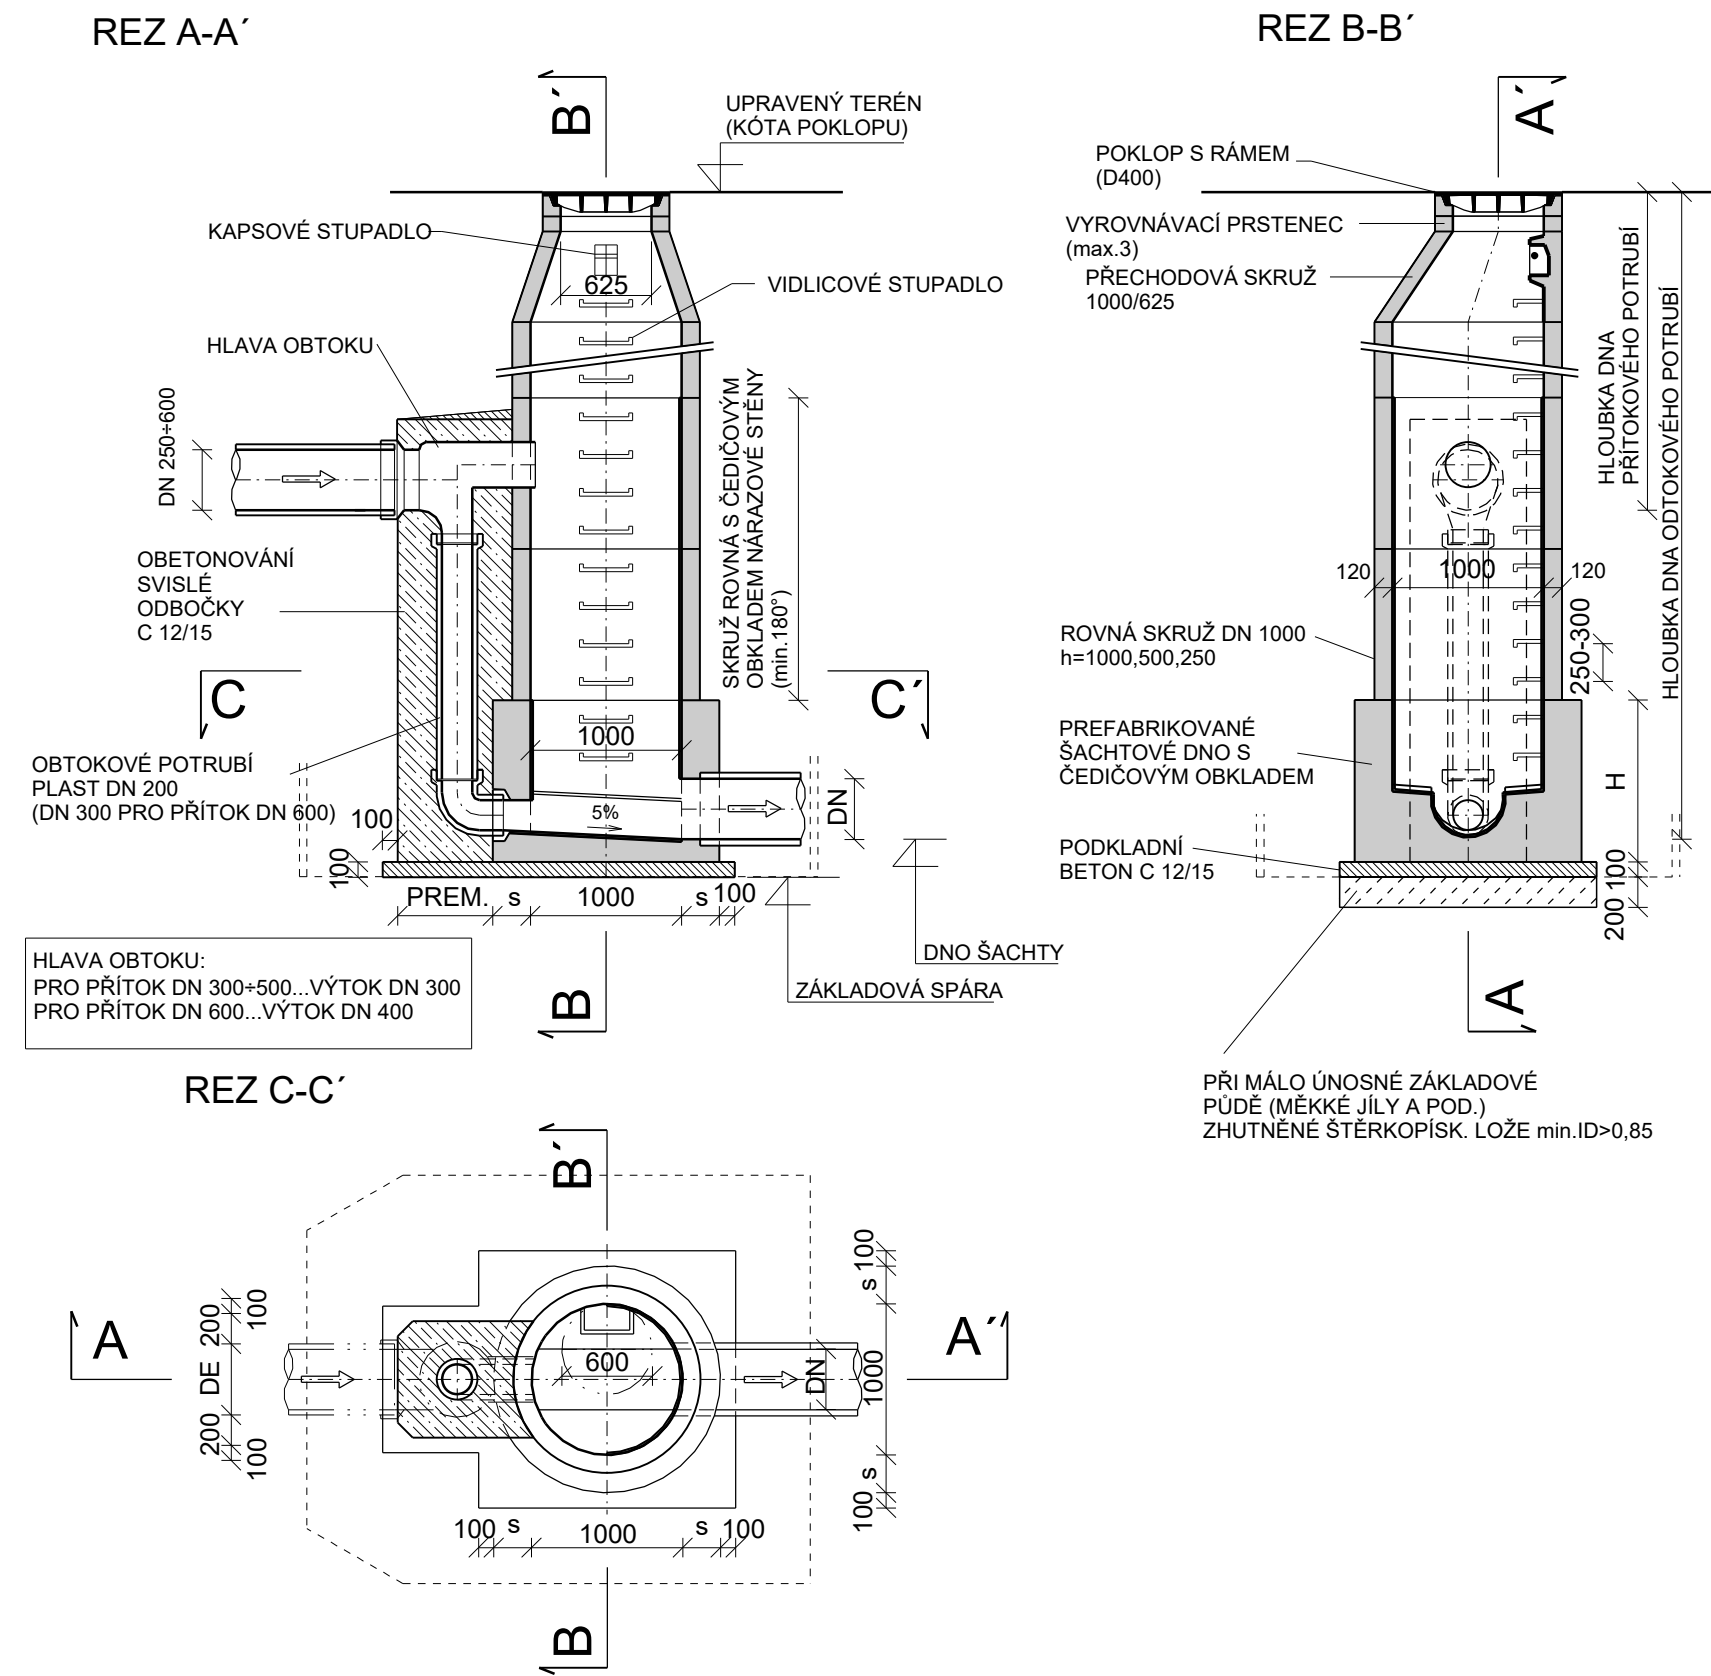


SPADIŠTĚ NA POTRUBÍ DN 250+500 Z BET. PREFABRIKÁTŮ


-BEZ SVISLÉHO POTRUBÍ (U STOK NA POTRUBÍ DN 250-DN 600, KDE SE NEPŘEDPOKLÁDÁ TRVALÝ PŘÍTOK Z DRENÁŽÍ)

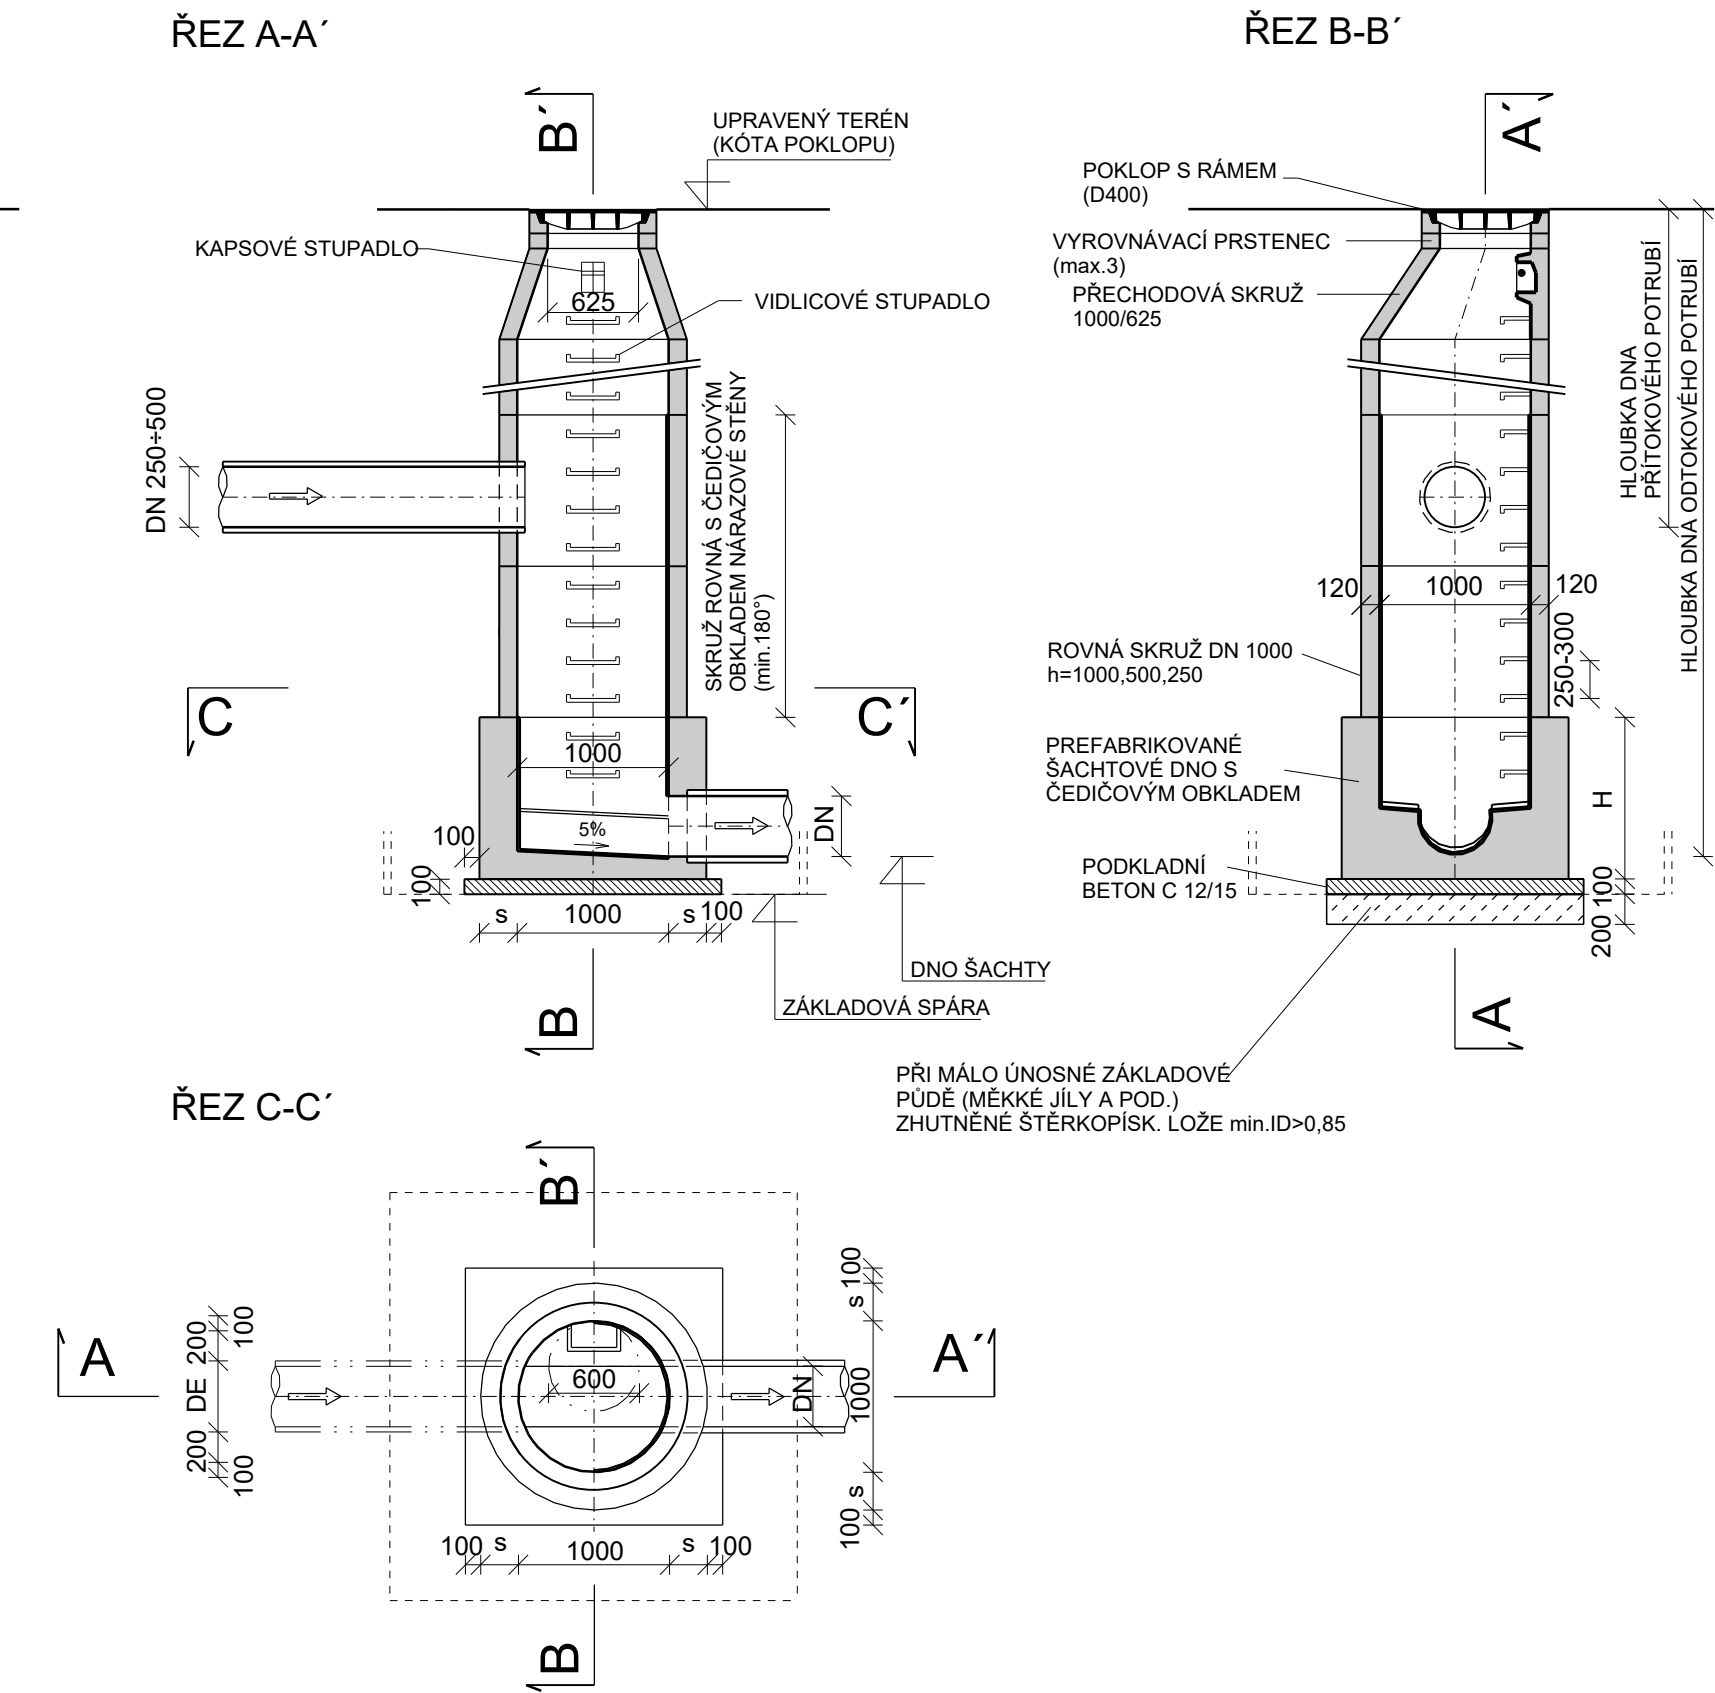

ÚPRAVA VSTUPU ŠACHTY VE VOLNÉM TERÉNU:

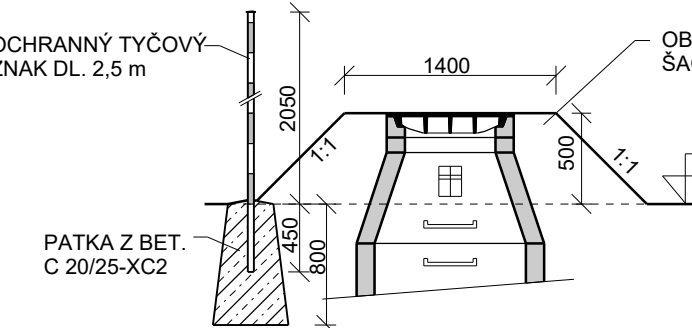

ÚPRAVA VSTUPU ŠACHTY V KRAJINICÍ:

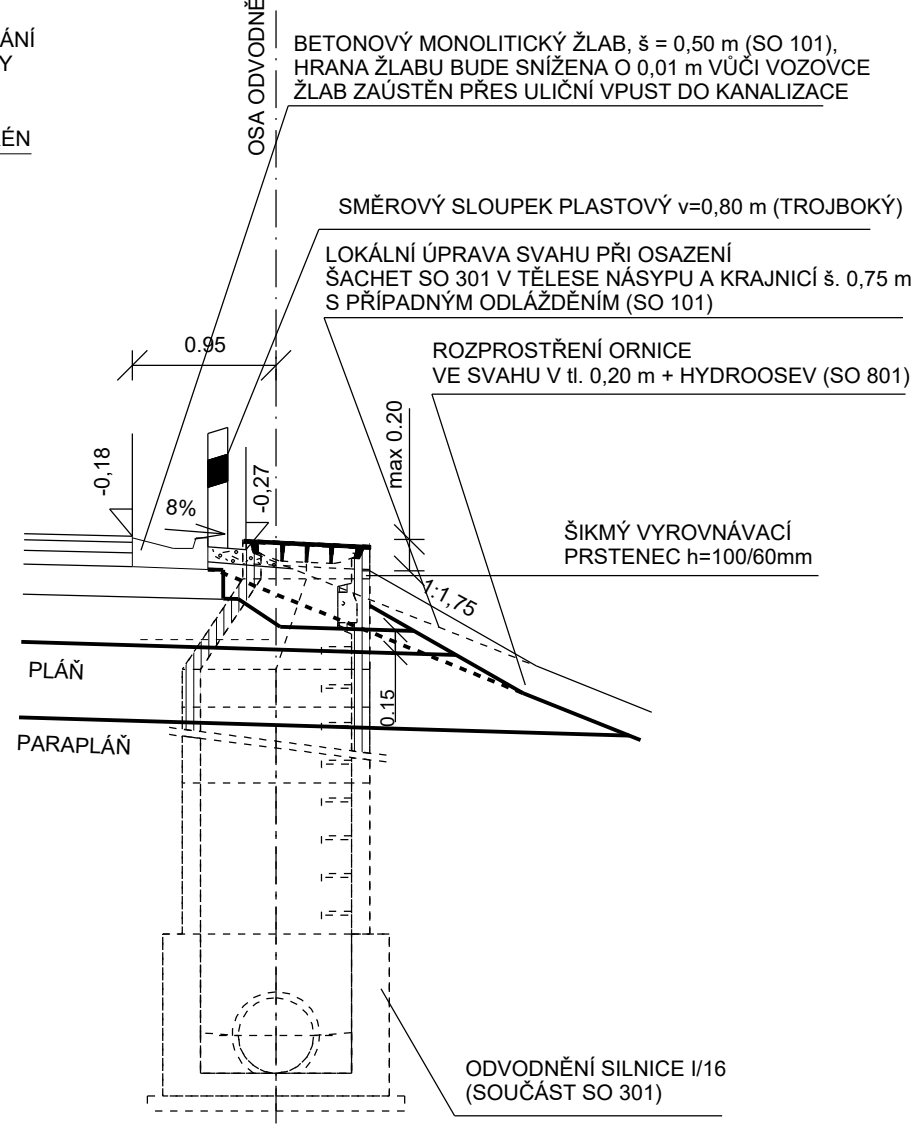

POZNÁMKA:
-SPADIŠTĚ - BETONOVÉ, PREFABRIKOVANÉ DNO S OBKLADEM Z ČEDIČE
-NARÁZOVÁ STĚNA ROVNĚŽ S OBKLADEM Z ČEDIČE V ZAHLBOVÁNÍ MIN. 180"
-PRO NAPLOUENÍ KANALIZAČNÍHO POTRUBÍ DO ŠACHTOVÝCH DEN POUŽÍVAT ŠACHTOVÉ VLOŽKY NEBO VODOTĚSNÉ ŠACHTOVÉ VSTUPY, KTERÉ BUDOU ZABUDOVÁNY JIŽ PŘI VÝROBĚ
-VRTÁNÍ DODATEČNÝCH OTVORŮ S REZERVOU TAK, ABY PO OSAZENÍ VLOŽKY BYL OTVOR VODOTĚSNĚ ZAPLOUČEN (SANAČNÍ MALTA, DOSTAČNÝ TĚL NEBO TĚSNÍCÍ PROFIL)
-PŘÍPOJKY - DO PREFABRIKOVANÝCH DEN NEBO DO ČISTÉ REZANÝCH OTVORŮ, DRENÁŽE DO ČISTÉ REZANÝCH OTVORŮ, VÝJIMEČNĚ NÁPOJENÍ POMOCÍ TVAROVEK PŘÍMO DO POTRUBÍ
-OKOLÍ POKLOPU UMÍSTĚNÝCH V KOMUNIKACI MUSÍ BÝT PEČLIVĚ HUTNĚNO
-SPOJ MEZI SKRUŽEMI A MEZI DNEM A VSTUPNÍM KOLÍNEM BUDOU OPATŘENY ELASTOMEROVÝM TĚSNĚNÍM
-VÝŠKA KYNETY V ŠACHTÁCH BUDE MIN. 1/2 DN POTRUBÍ
-VE VOLNÉM TERÉNU BUDE VSTUPNÍ KOLÍN VYTÁZEN CCA 0,5m NAD TERÉN, V ZEMĚDĚLSKÝCH KULTURÁCH - BUDE OZNAČEN OCHRANNÝM TYČOVÝM ZNAKEM

POKLOPY ŠACHT KANALIZACE - DLE ČSN EN 124 BEZ ODVĚTRÁNÍ
A) VE VOZOVCE A V PŘEJEZDECH SDP D400, Z TVÁRNĚ LITINY SE ZABEZPEČENÍM PROTI VYSKOČENÍ, S PANTEM A S BEZPEČNOSTNÍM ZÁMKEM-OBRTLIK-SPECIÁLNÍM PRO RSD. PRO RSD S NÁPÍSEM RSD ČR A S LOGEM.
B) POKLOPY MIMO VOZOVKU V SDP MIN. B125: NEKOVOVÝ POKLOP SE ZÁMKEM-OBRTLIK. V PŘÍPADĚ KOVOVÝCH POKLOPŮ ZABEZPEČIT PROTI ZCIZENÍ ZÁMKEM-OBRTLIK-SPECIÁLNÍM PRO RSD. PRO RSD S NÁPÍSEM RSD ČR A S LOGEM.
C) PRO POKLOPY MIMO HL. TRASU V ZELENÍ A15 + D400: (TRÍDA ZATÍŽENÍ DLE UVAŽOVANÉHO ZATÍŽENÍ) CELOTIHOVĚ S PANTEM NEBO NEKOVOVÉ. PRO RSD S NÁPÍSEM RSD ČR A S LOGEM. POKLOP. JSOU ŠACHTY ZVÝŠENY NAD ÚROVĚNĚ TERÉNU O 0,3-0,5 m. STACI POKLOPY NEKOVOVÉ TRÍDY A15. KOVOVÉ POKLOPY POUZE UZAMKYATELNĚ Z DŮVODU ZAMEZENÍ SNADNÉHO PŘÍSTUPU A ODCIZOVÁNÍ.
D) POKLOPY V PŘÍKRYCH SVAZÍCH (NAPŘ. NÁSPY) - LITINOVÉ OPATŘENY NEROZEABITELNÝM PANTEM PROTI ZCIZENÍ S OTVÍRÁNÍM PŘES 90° (DOP. 120°), S SÁRETACÍ PŘI INSPEKČNÍ POLOZE, NEBO LEHKE NEKOVOVÉ- NAPŘ. DLE B), ALE S UNOSNOSTÍ NIŽÍ.
E) ZOHLÉDNIT A KONTROLOVAT: SMĚR OTVÍRÁNÍ U POKLOPŮ S PANTEM (POLOHA PANTU PROTI SMĚRU JÍZDY - PŘIJÍDEJÍCÍ AUTO DŮVĚŘÁ POKLOP), MANIPULAČNÍ PROSTOR VSTUPU DO ŠACHTY U SVOIDIDEL. U POKLOPŮ V ZÁSTAVĚ A SOUČASNĚ V KOMUNIKACI - BEZHLUČNOST.

-U SPADIŠTĚ A ŠACHT NA POTRUBÍ S VELKÝM SPÁDEM BUDOU POUŽITÝ POKLOPY S ODVĚTRÁNÍM

Souřadnicový systém: S-JTSK
Výškový systém: Bpv

SO 301 Odvodnění I/16

Objednatel:



Ředitelství silnic a dálnic s. p.
Čerčanská 2023/12, Krč, 140 00 Praha 4

Zhotovitel:



Valbek, spol. s r.o.
Vaňurova 505/17
460 07 Liberec 3

Valbek	Vypracoval Zodp. projektant Tech. kontrola Akce	ING. J. VANCL ING. J. VANCL ING. D. LANDA	<i>[Signature]</i> <i>[Signature]</i> <i>[Signature]</i>	Zak. číslo Datum Stupeň Počet formátů Měřítko Č. přílohy	21-L113-001 02/2025 PDPS 8 x A4 1 : 50 Paré
Zhotovitel: Valbek, spol. s r.o. Vaňurova 505/17 460 07 Liberec 3	Příloha	ŠACHTY, SPADIŠTĚ			5