


ULIČNÍ VPUST
-Z BETON. PREFABRIKOVANÝCH DÍLCŮ
-PRO OSAZENÍ DO CURB-KINGU
M 1:25


ŘEZ

PŘÍKLAD SKLADBY PREFABRIKÁTŮ UV:

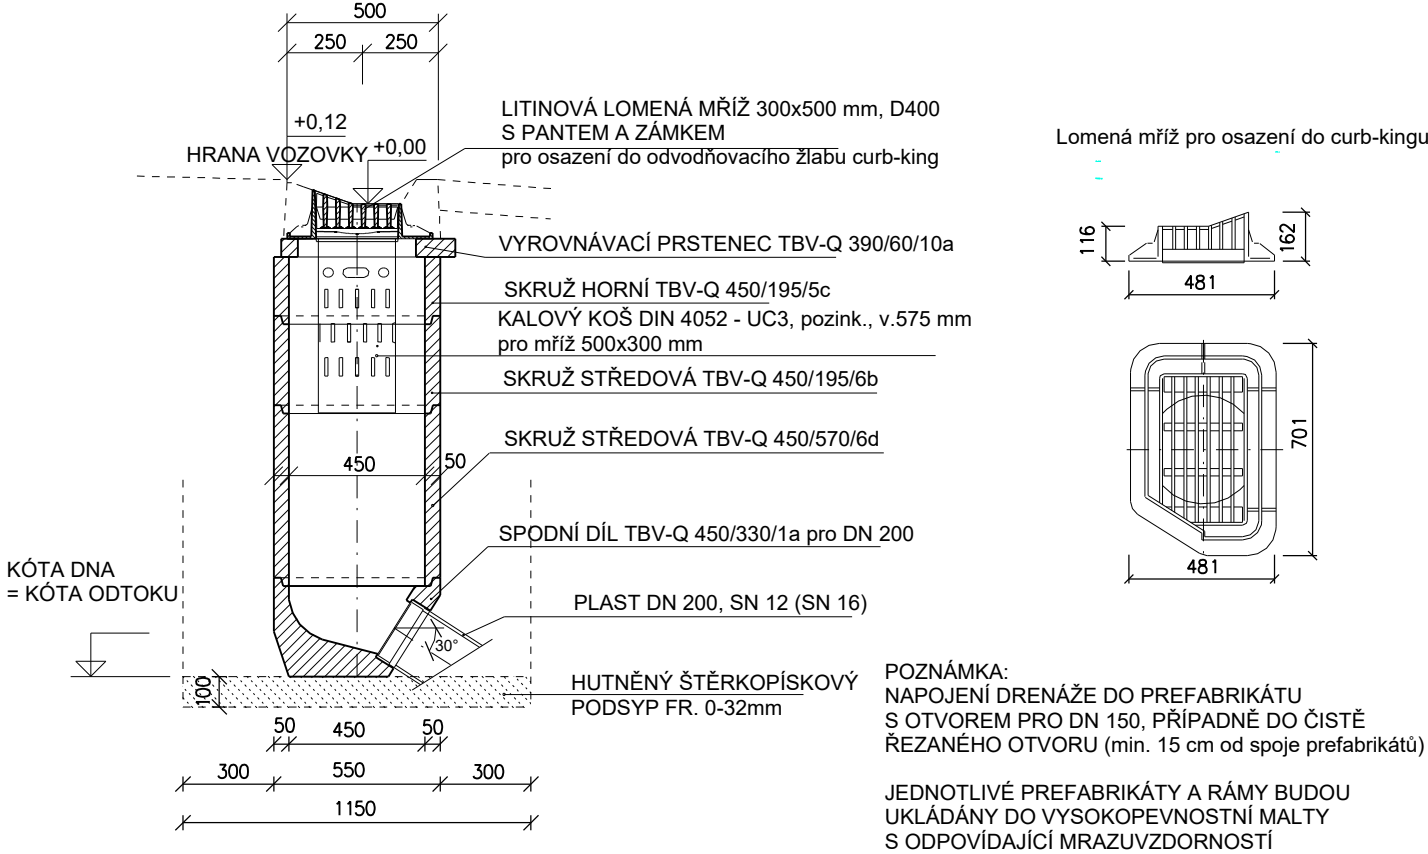

ODTOKOVÁ VPUST ŠŽ
-Z BETON. PREFABRIKOVANÝCH DÍLCŮ

PŘÍKLAD SKLADBY PRO ODTOKOVOU VPUSTĚ (OV)
ŠTĚRBINOVÉHO ŽLABU (ŠŽ):

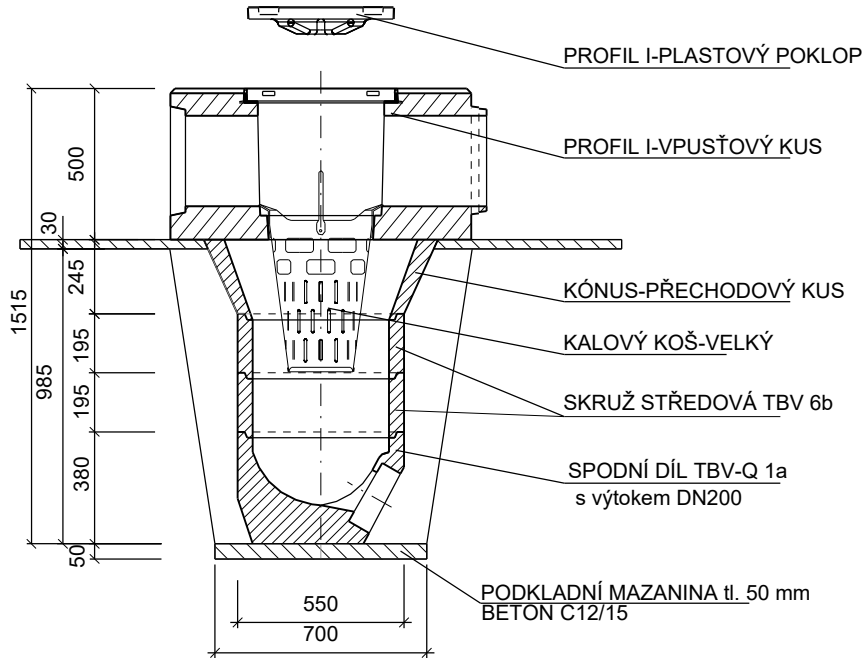

Souřadnicový systém: S-JTSK
Výškový systém: Bpv

SO 301 Odvodnění I/16

Objednatel:



Ředitelství silnic a dálnic s. p.
Čerčanská 2023/12, Krč, 140 00 Praha 4

Zhotovitel:



Valbek, spol. s r.o.
Vaňurova 505/17
460 07 Liberec 3

	Vypracoval	ING. J. VANCL		Zak. číslo	21-LI13-001
	Zodp. projektant	ING. J. VANCL		Datum	02/2025
	Tech. kontrola	ING. D. LANDA		Stupeň	PDPS
	Akce I/16 MLADÁ BOLESLAV - MARTINOVICE			Počet formátů	2 x A4
				Měřítko	1 : 25
Zhotovitel: Valbek, spol. s r.o. Vaňurova 505/17 460 07 Liberec 3	Příloha ULIČNÍ VPUSTI			Č. přílohy	Paré
				6	