



VÝUSTNÍ OBJEKT Č. 5
M 1 : 50

PŮDORYS

OPEVNĚNÍ SOUČÁSTÍ SO 322

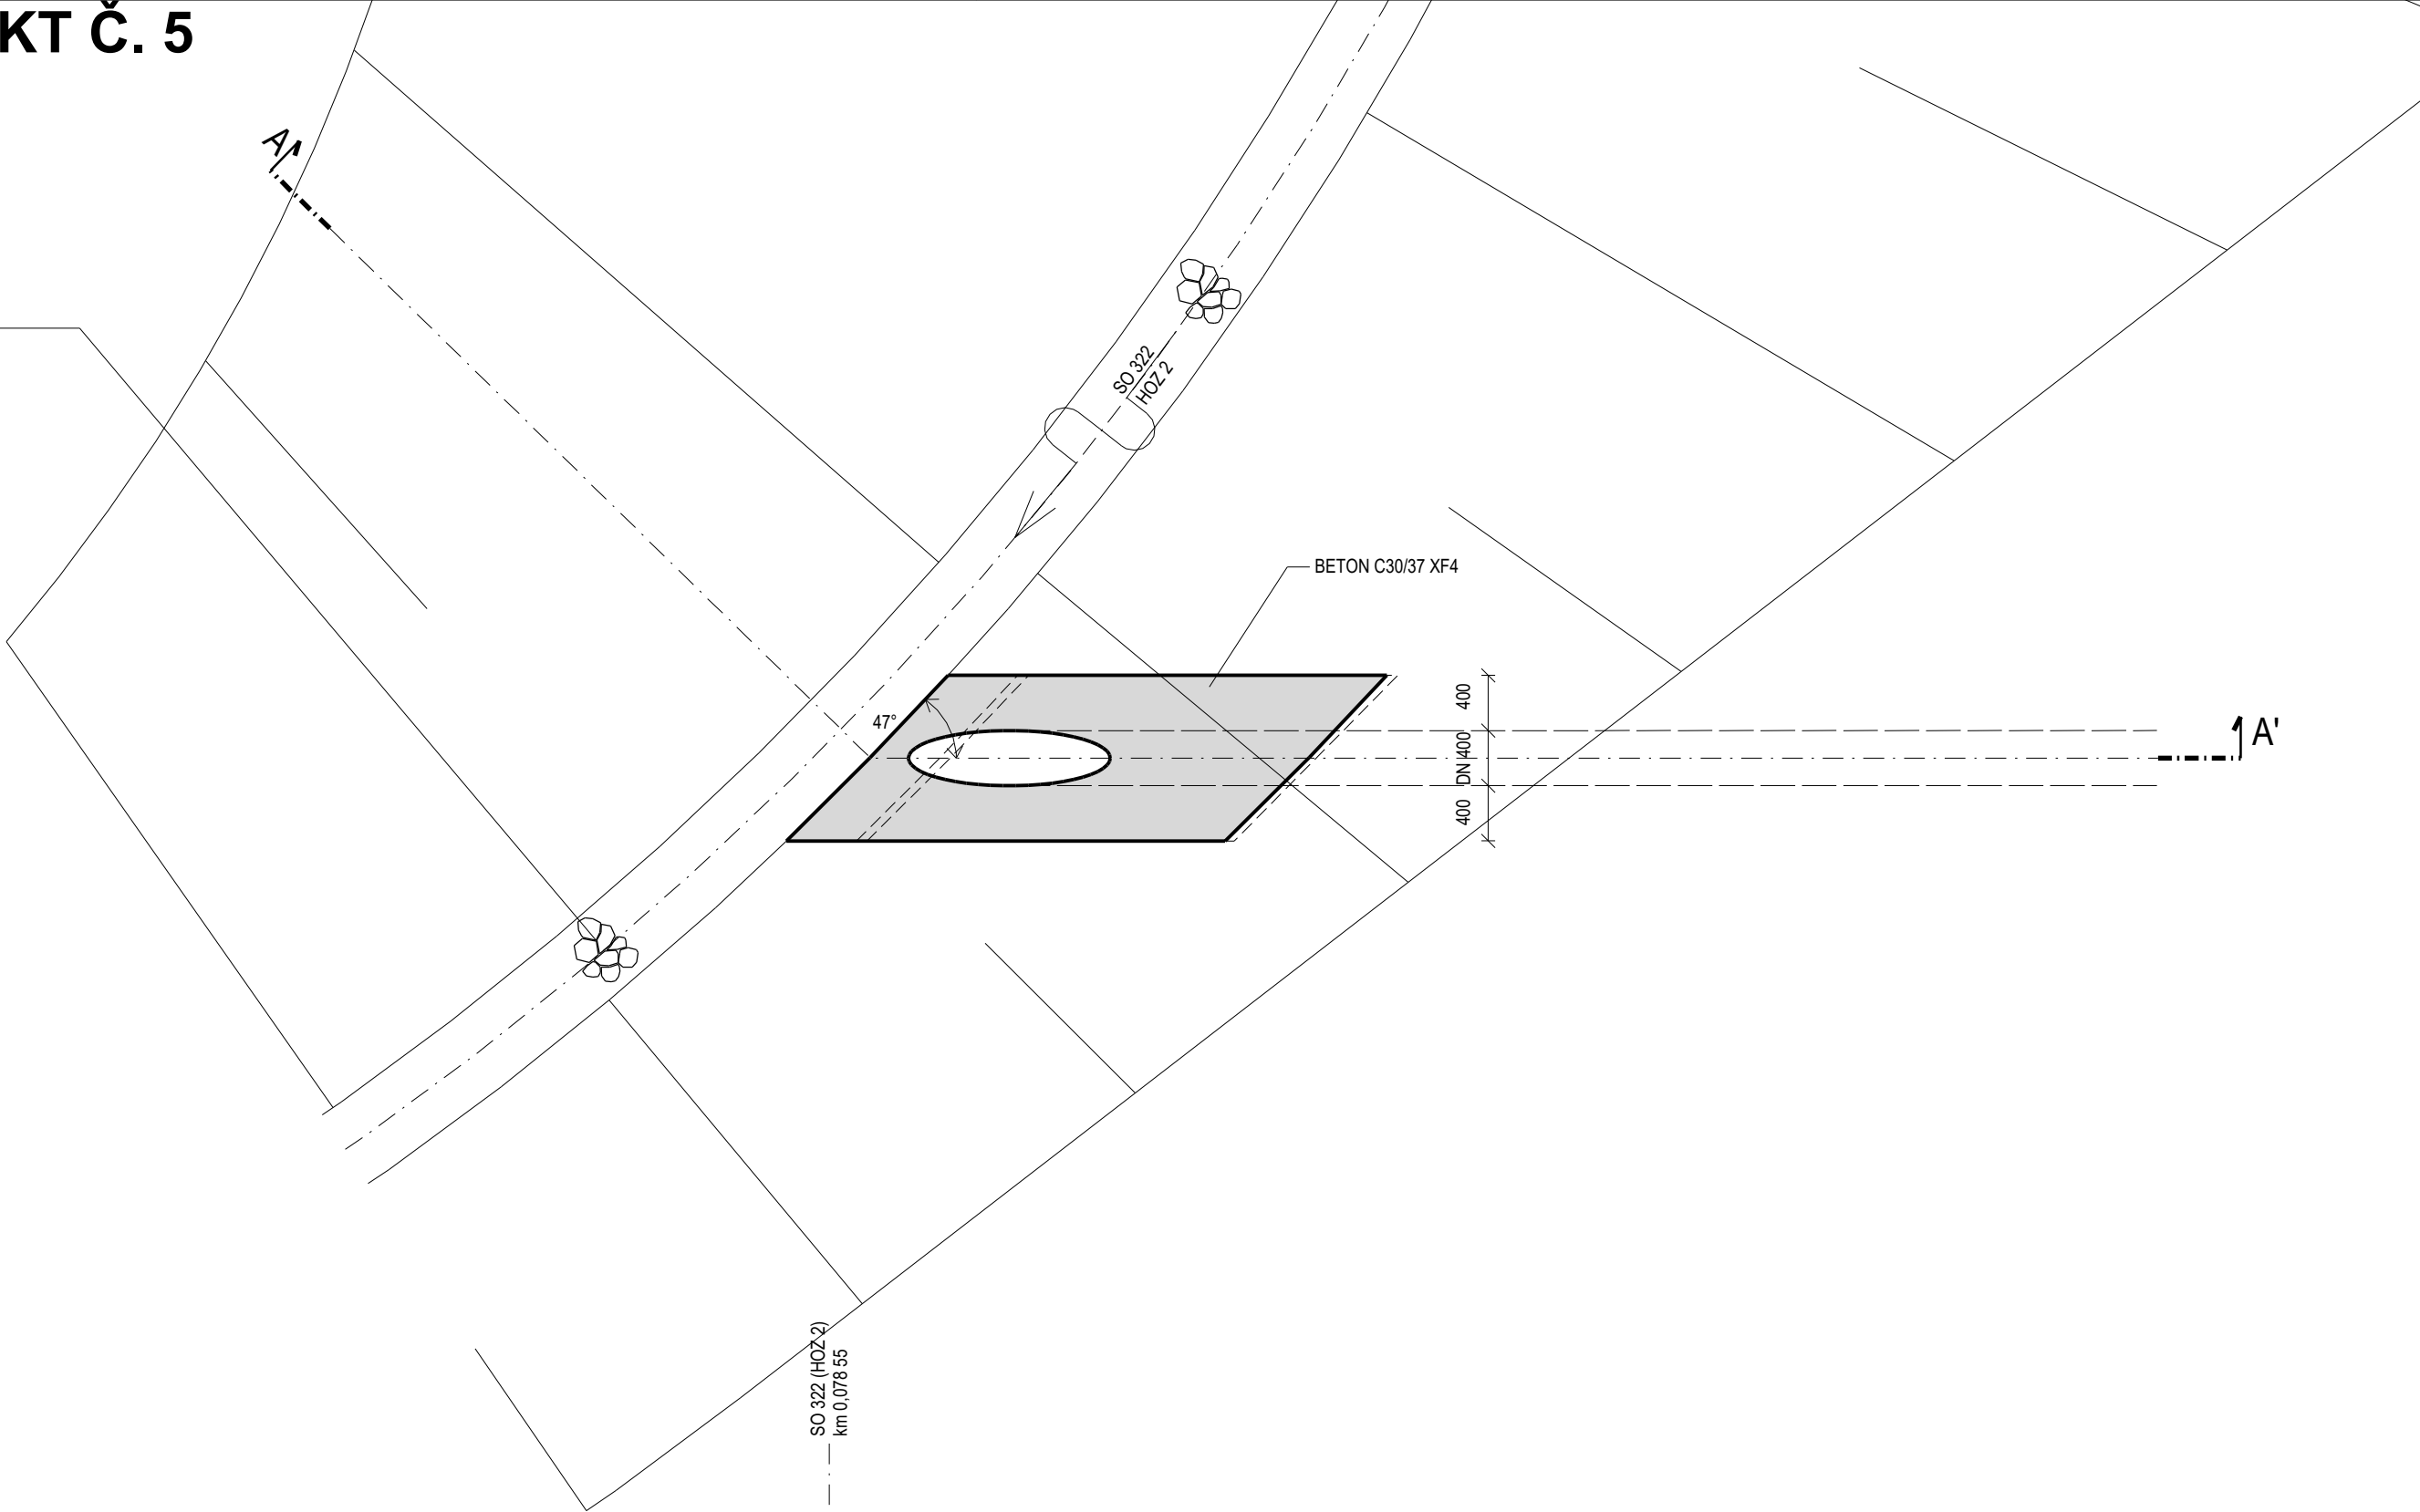

ŘEZ A - A'

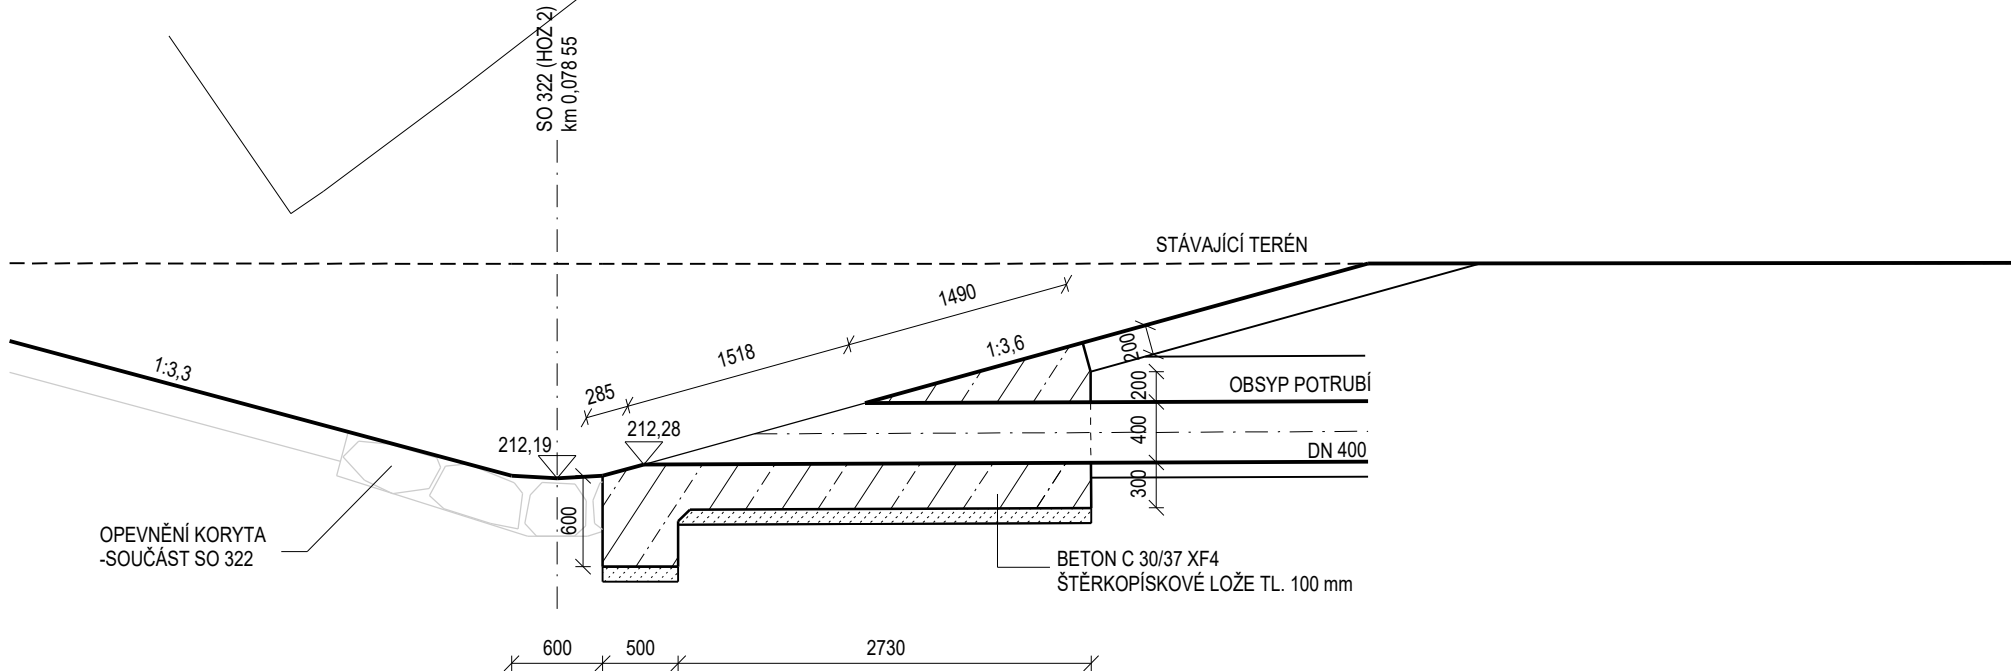

Souřadnicový systém: S-JTSK
Výškový systém: Bpv

SO 301 Odvodnění I/16

Objednatel:



ŘEDITELSTVÍ
SILNIC
A DÁLNIC

Ředitelství silnic a dálnic s. p.
Čerčanská 2023/12, Krč, 140 00 Praha 4

Zhotovitel:



Valbek, spol. s r.o.
Vaňurova 505/17
460 07 Liberec 3



Vypracoval
Zodp. projektant
Tech. kontrola

ING. V. JURÁNEK
ING. J. VANCL
ING. D. LANDA

Zak. číslo
Datum
Stupeň
Počet formátů
Měřítko
Č. přílohy

21-LI13-001
02/2025
PDPS
3 x A4
1:50
Paré

I/16 MLADÁ BOLESLAV - MARTINOVICE

Zhotovitel:

Valbek, spol. s r.o.
Vaňurova 505/17
460 07 Liberec 3

Příloha

VÝUSTNÍ OBJEKT Č.5 - 301.5

8.5