


# VÝUSTNÍ OBJEKT Č. 9

## M 1 : 50

# PŮDORYS

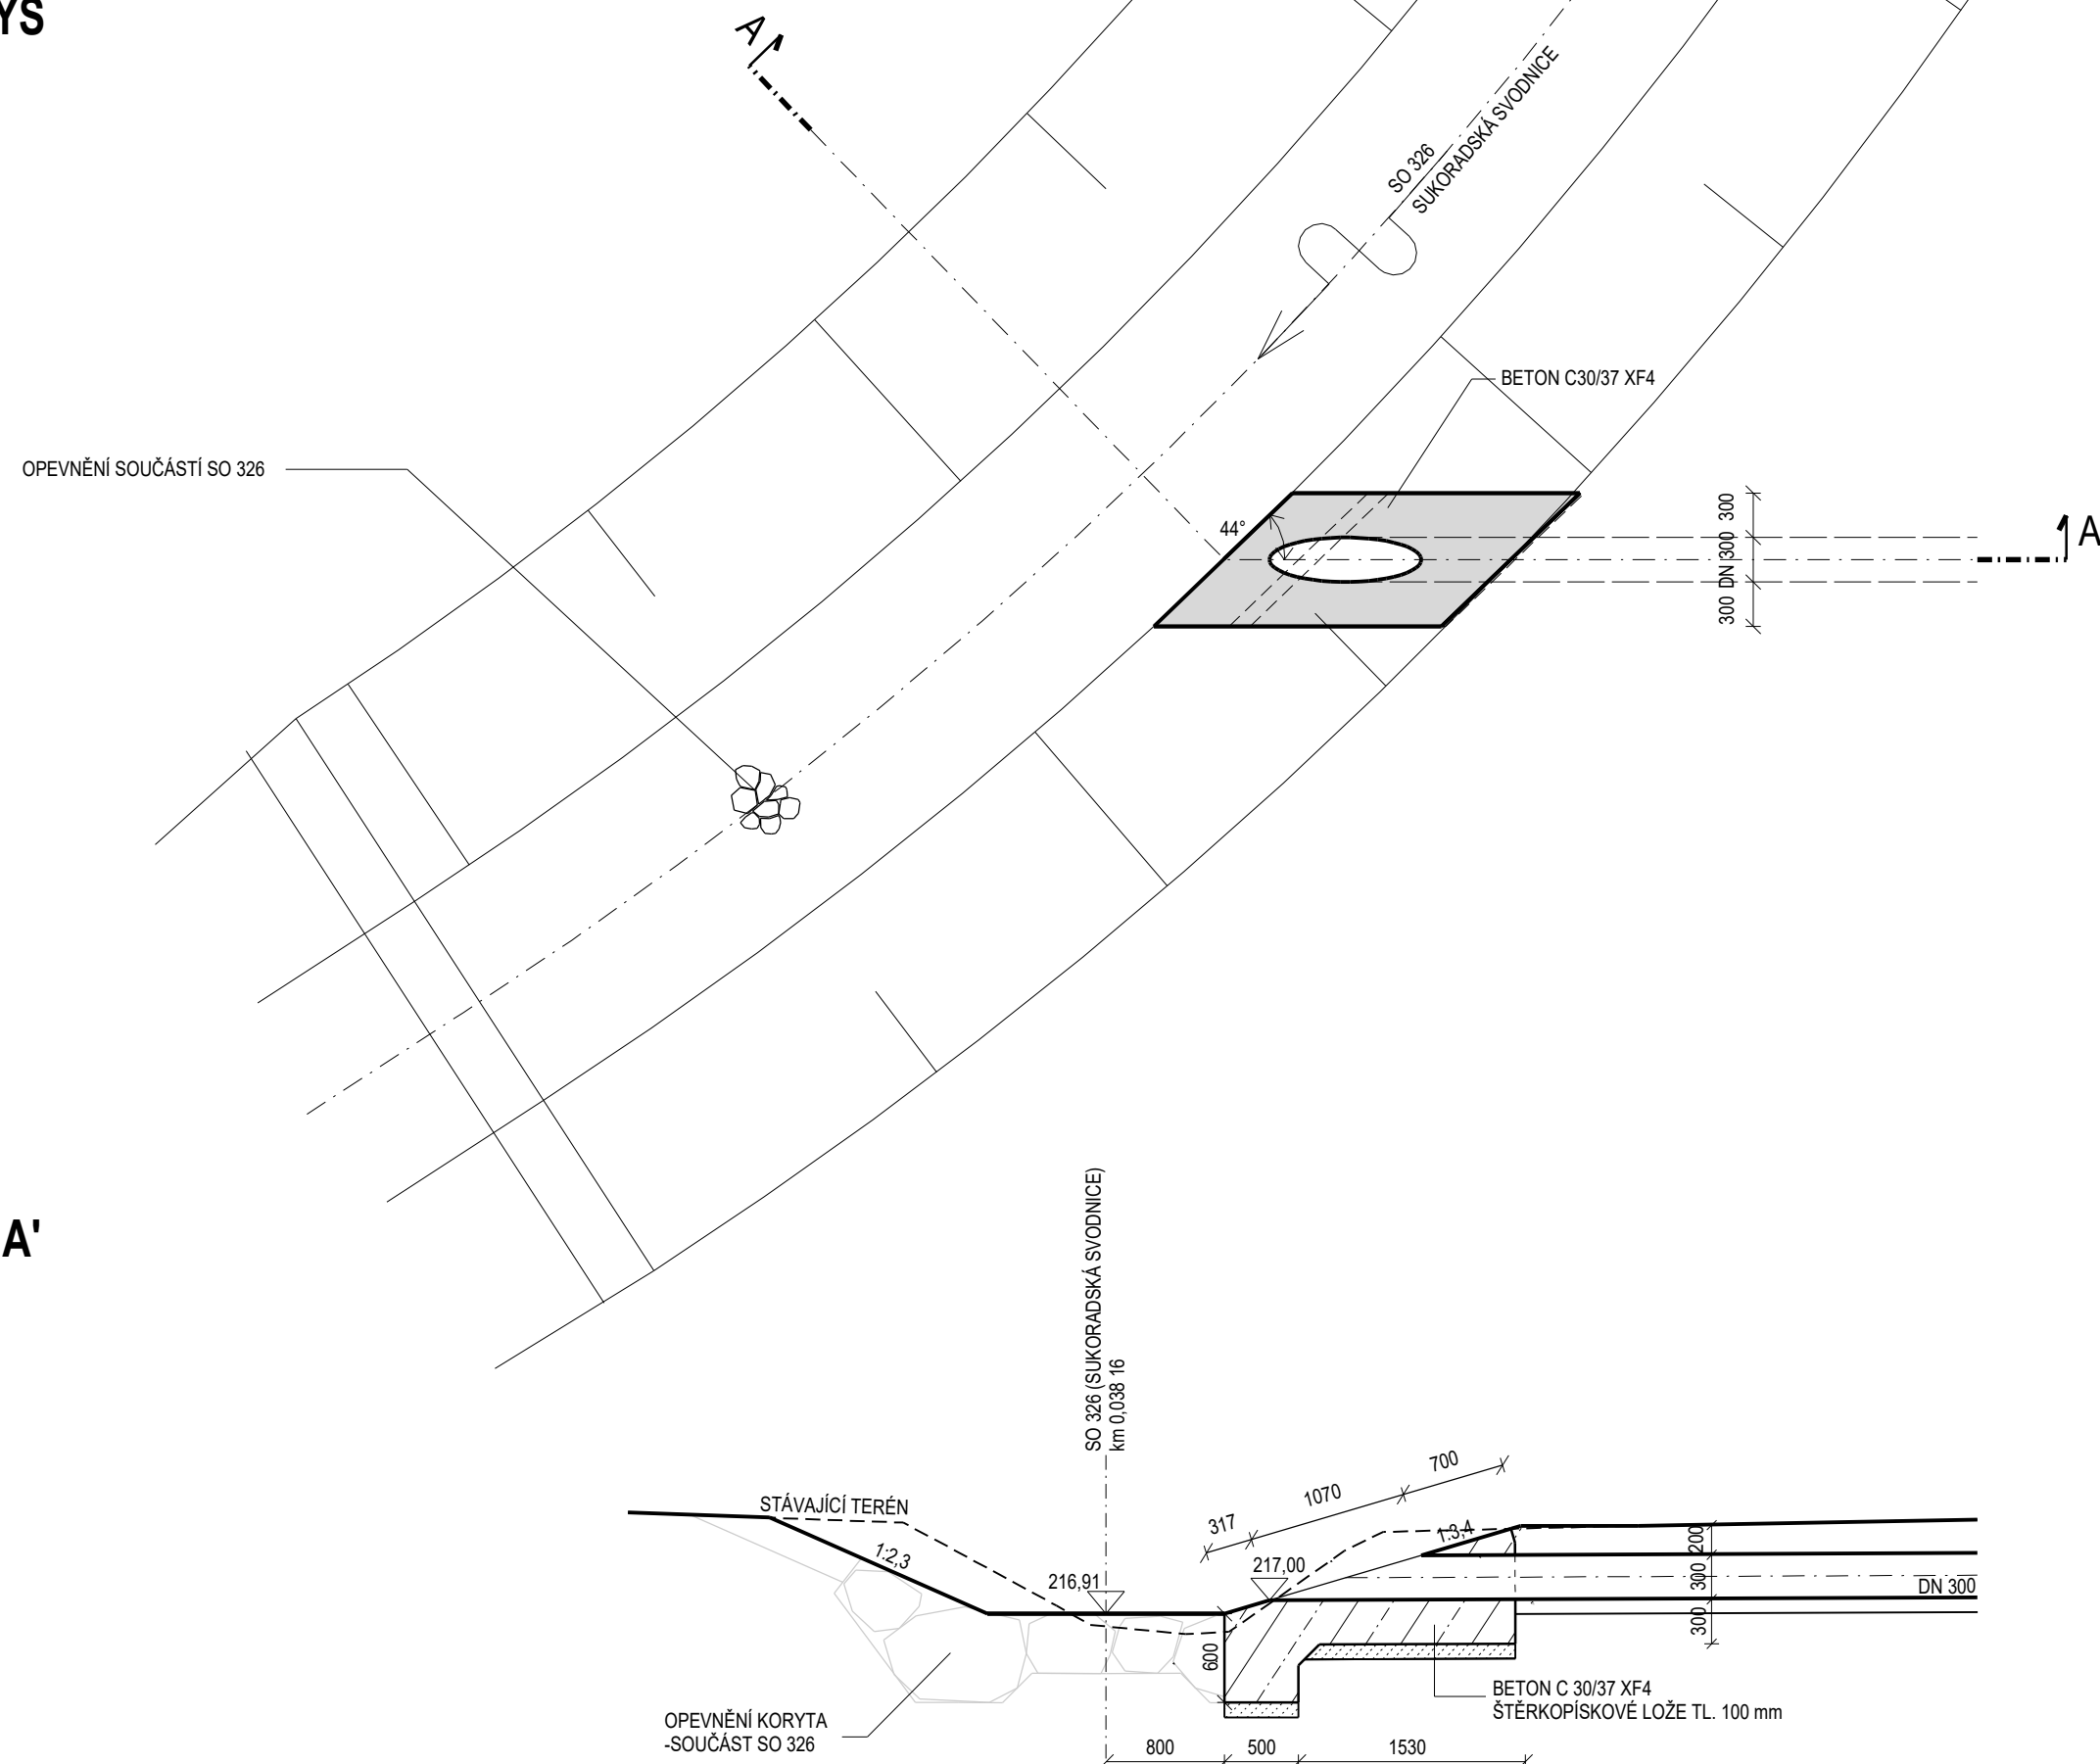

Souřadnicový systém: S-JTSK  
Výškový systém: Bpv

SO 301 Odvodnění I/16

**Objednatel:**



**ŘEDITELSTVÍ  
SILNIC  
A DÁLNIC**

**Ředitelství silnic a dálnic s. p.**  
Čerčanská 2023/12, Krč, 140 00 Praha 4

**Zhotovitel:**



**Valbek, spol. s r.o.**  
Vaňurova 505/17  
460 07 Liberec 3

|                                                                                       |                                                  |                 |                                                                                       |                      |             |
|---------------------------------------------------------------------------------------|--------------------------------------------------|-----------------|---------------------------------------------------------------------------------------|----------------------|-------------|
|  | <b>Vypracoval</b>                                | ING. V. JURÁNEK |  | <b>Zak. číslo</b>    | 21-LI13-001 |
|                                                                                       | <b>Zodp. projektant</b>                          | ING. J. VANCL   |  | <b>Datum</b>         | 02/2025     |
|                                                                                       | <b>Tech. kontrola</b>                            | ING. D. LANDA   |  | <b>Stupeň</b>        | PDPS        |
|                                                                                       | <b>Akce</b>                                      |                 |                                                                                       | <b>Počet formátů</b> | 3 x A4      |
| <b>Zhotovitel:</b><br>Valbek, spol. s r.o.<br>Vaňurova 505/17<br>460 07 Liberec 3     | <b>Příloha</b><br><br>VÝUSTNÍ OBJEKT Č.9 - 301.9 |                 |                                                                                       | <b>Měřítka</b>       | 1:50        |
|                                                                                       |                                                  |                 |                                                                                       | <b>Č. přílohy</b>    | Paré        |
|                                                                                       |                                                  |                 |                                                                                       | <b>8.9</b>           |             |
|                                                                                       |                                                  |                 |                                                                                       |                      |             |