


SO 301 ODVODNĚNÍ I/16

SPOJNÁ ŠACHTA


PŮDORYS

M 1:25

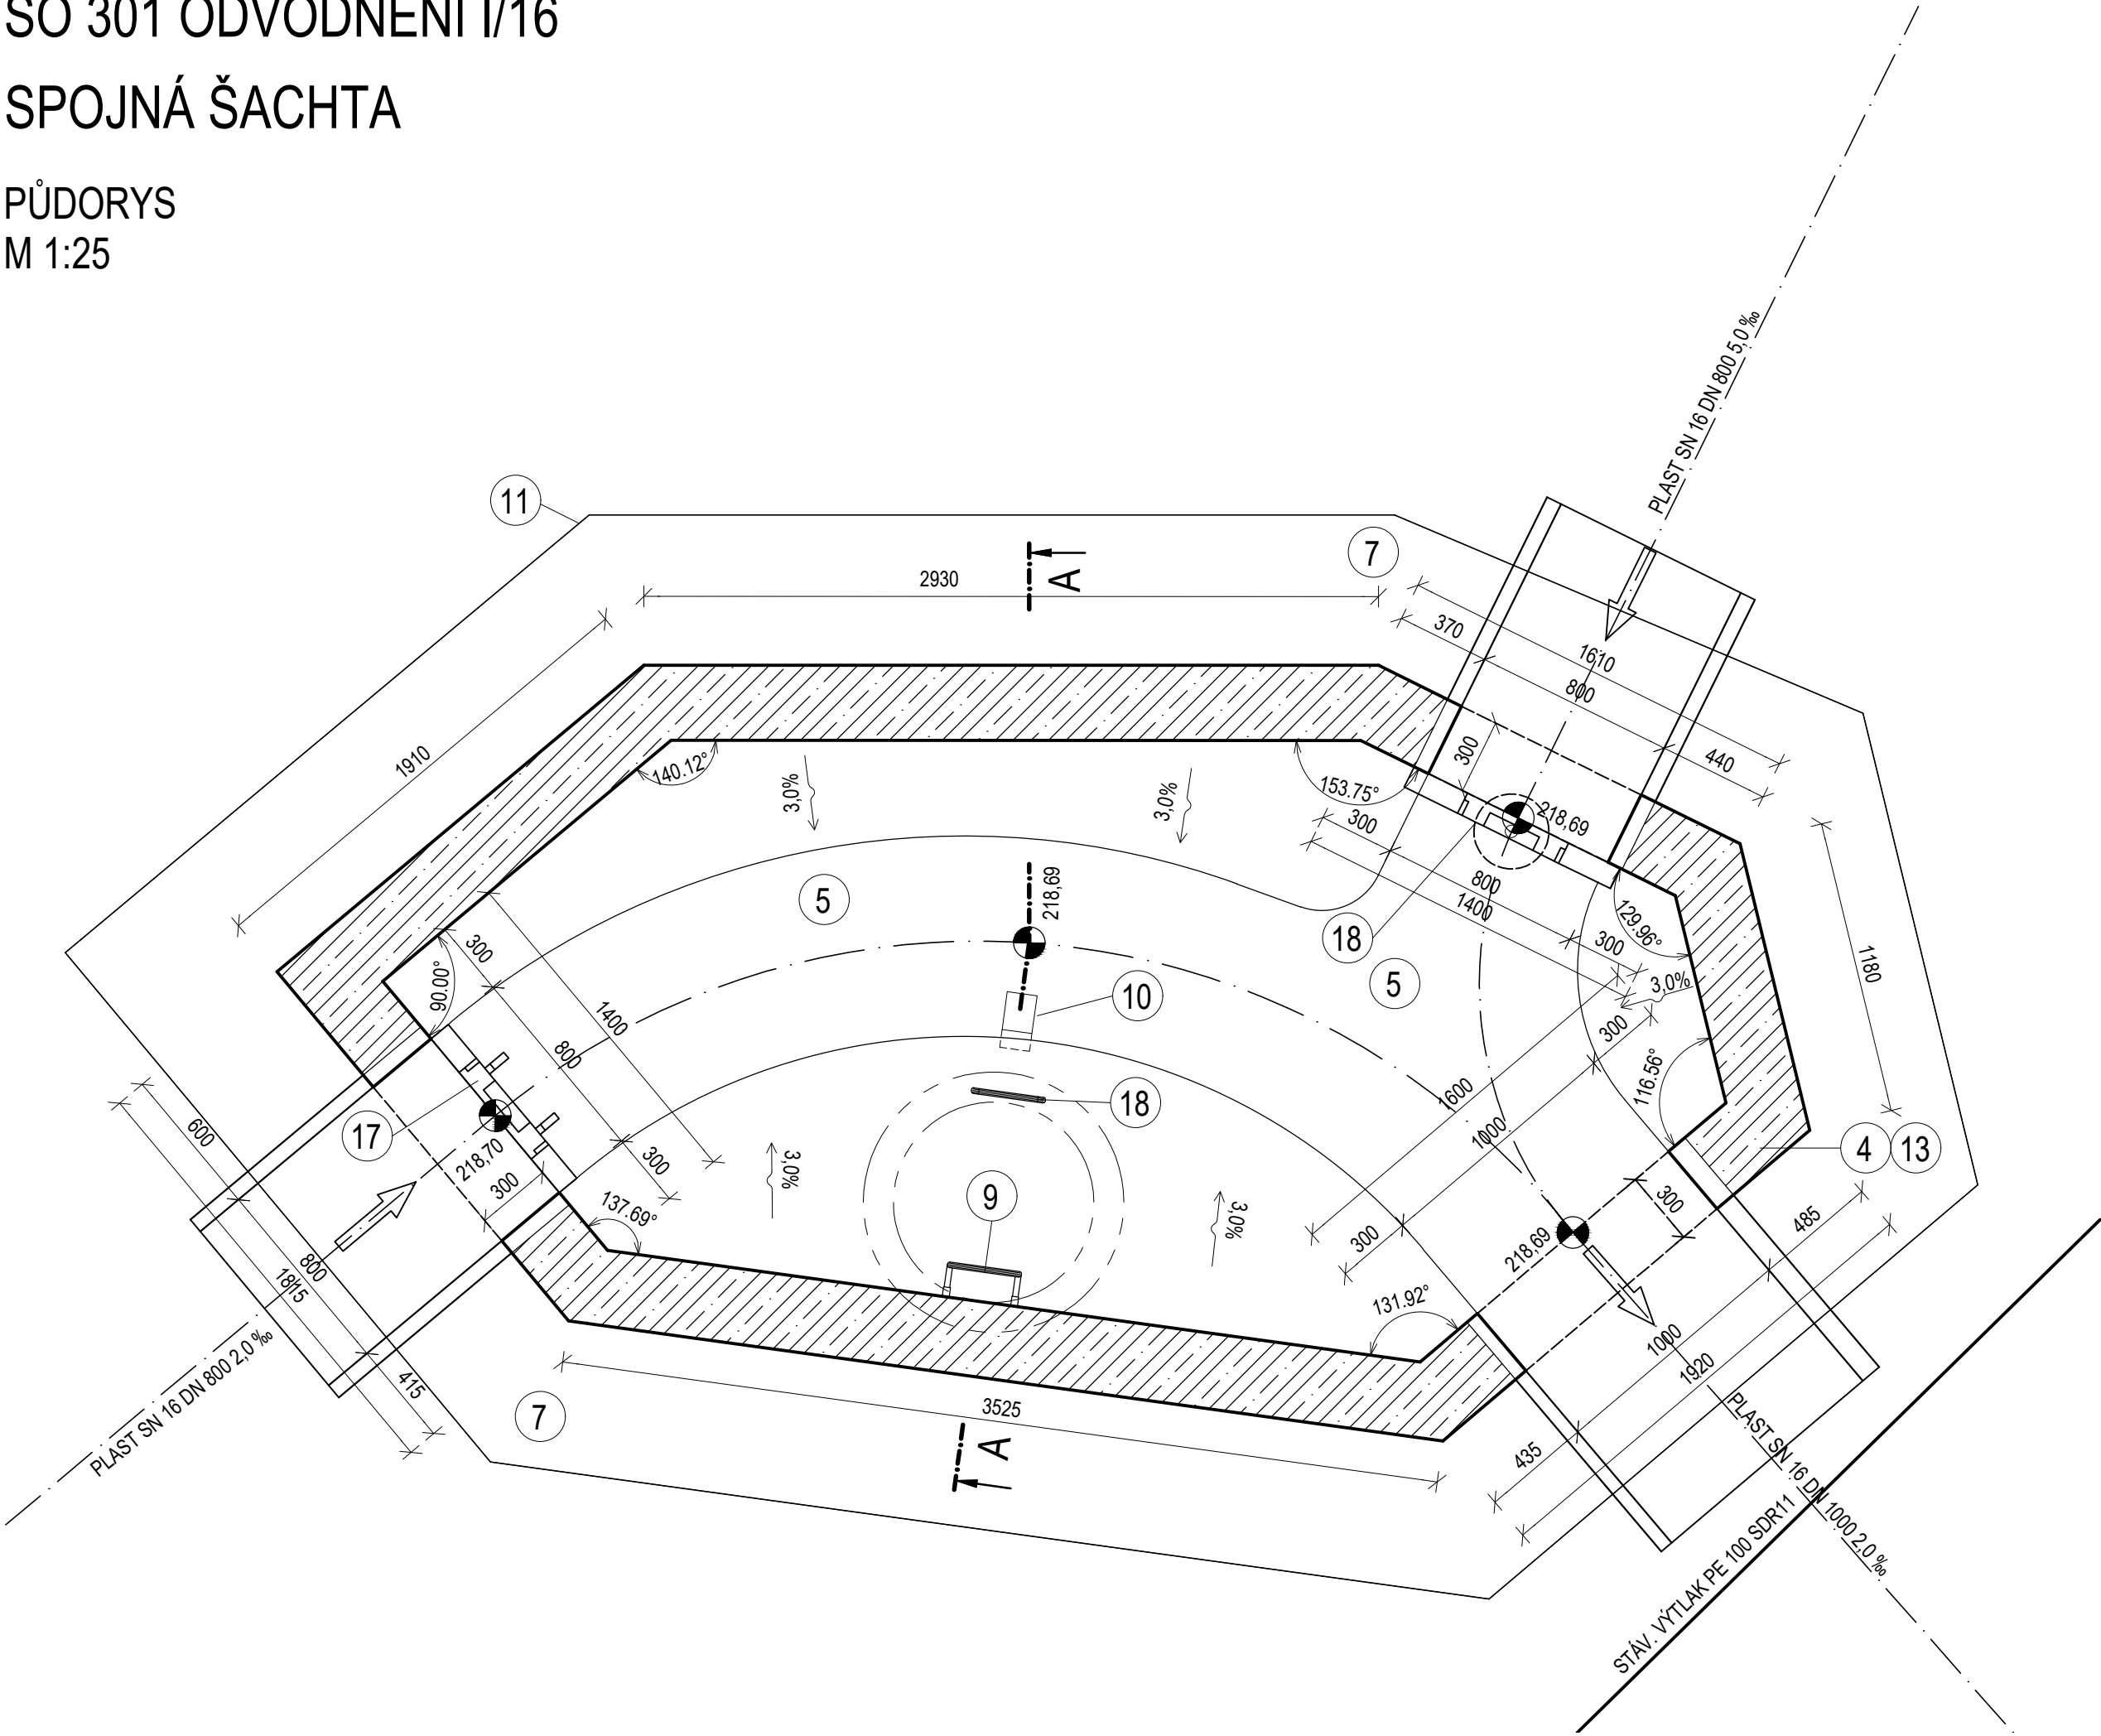

ŘEZ A-A

M 1:25

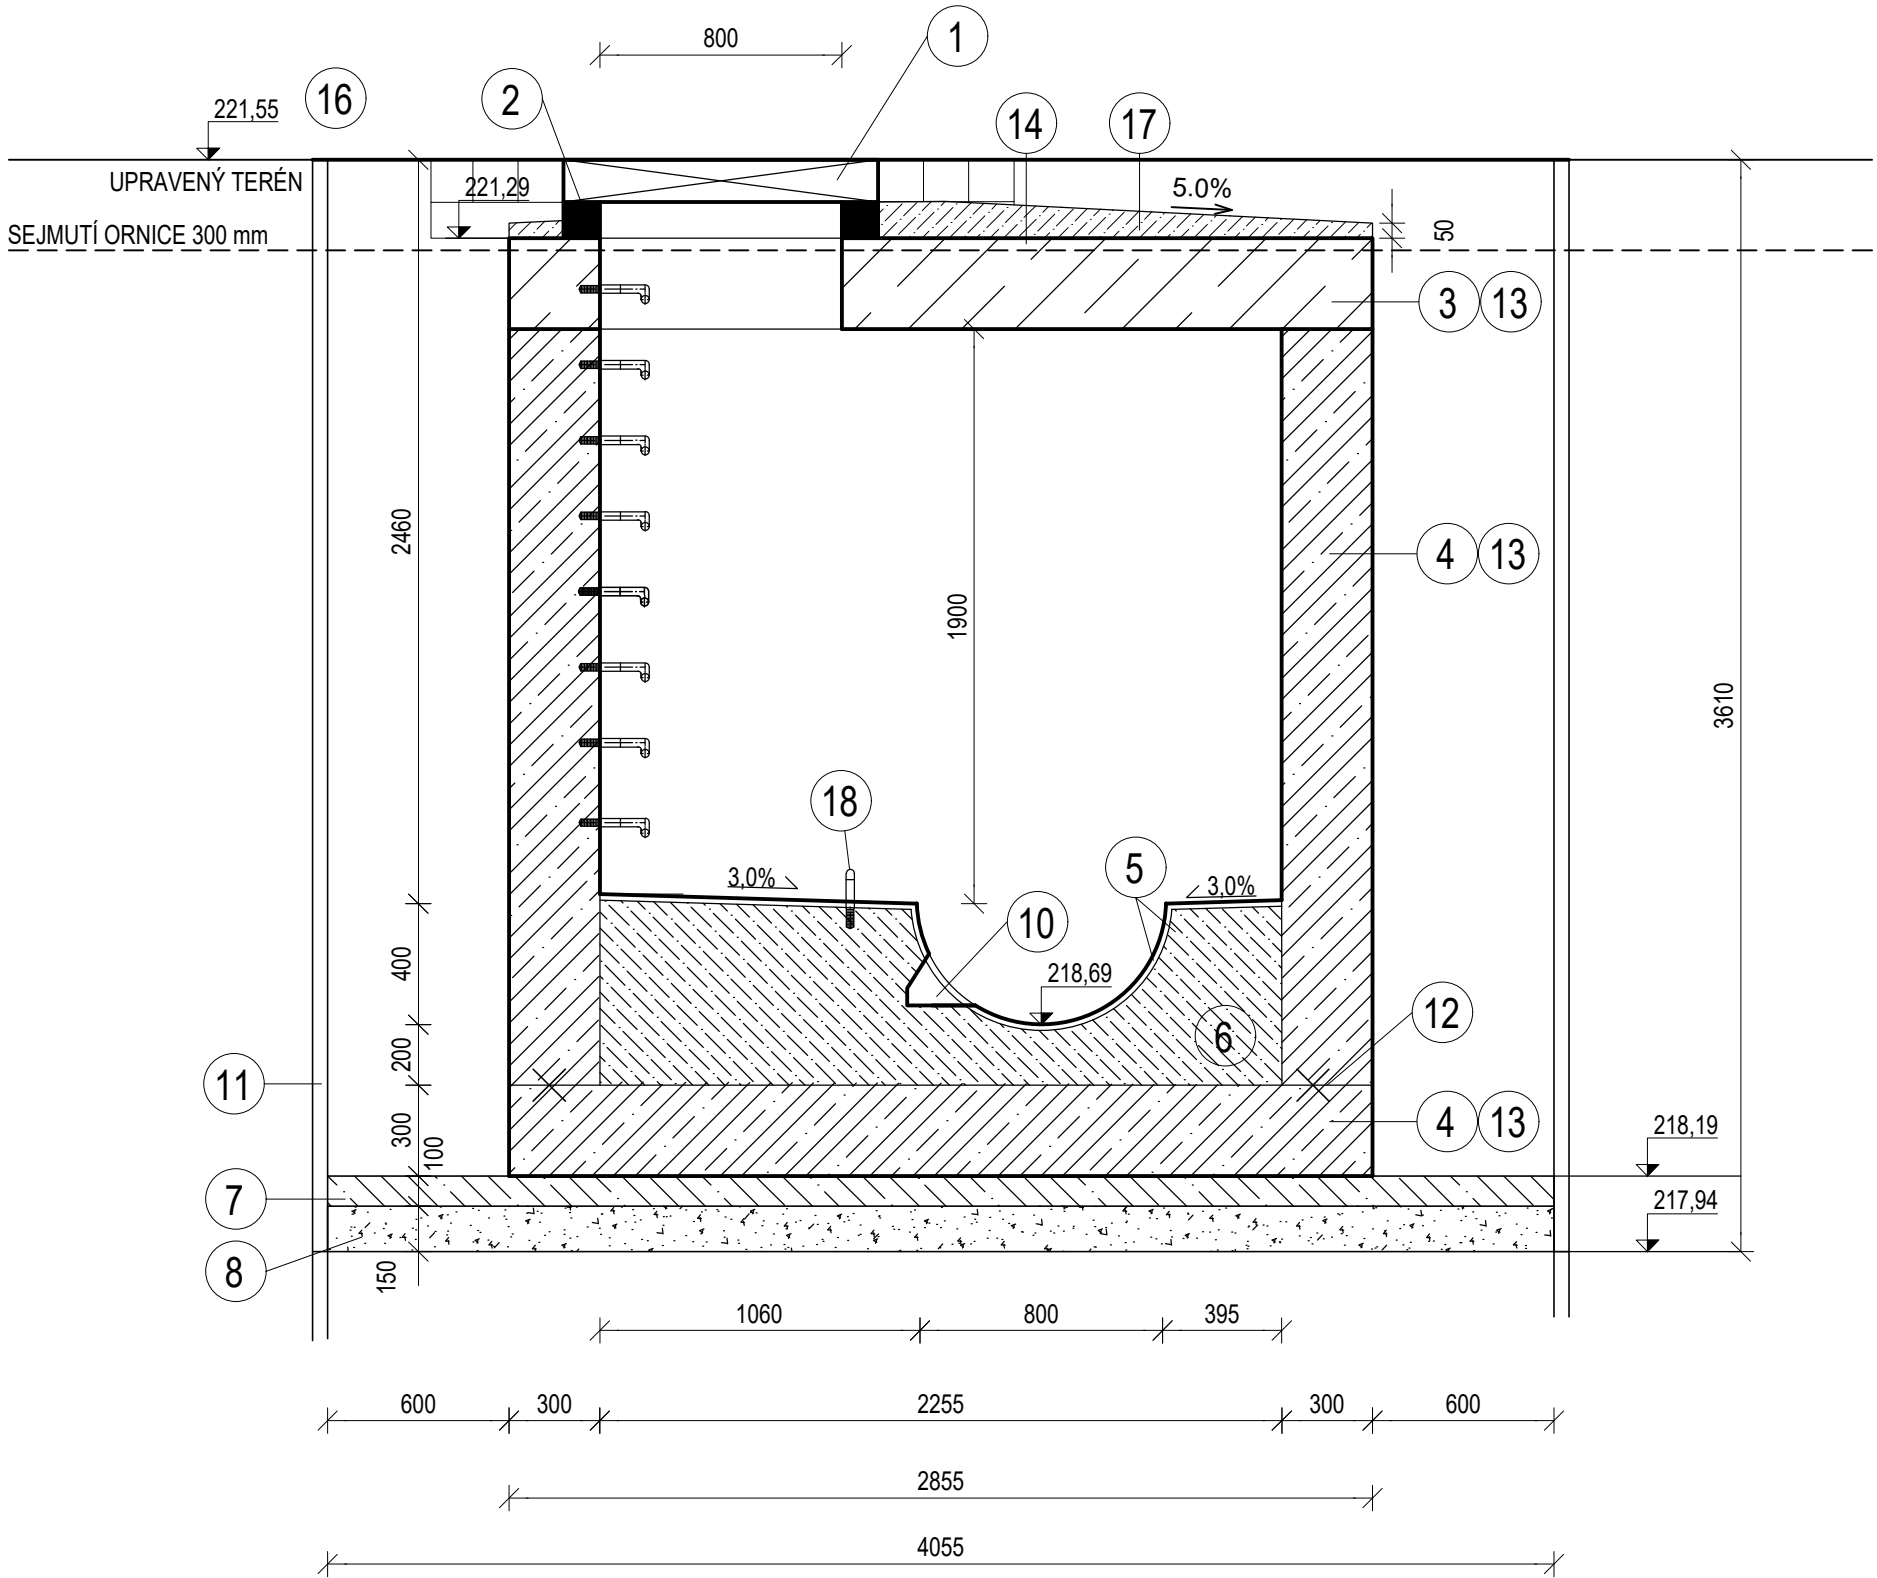

LEGENDA	
1	ŠACHTOVÝ POKLOP NEKOVÝ BEZ ODVĚTRÁNÍ, DN 800, DLE ČSN EN 124, TŘ. ZATÍŽENÍ B125
2	VYROVNÁVACÍ PRSTENEC DN 800 DLE ČSN EN 1917
3	ZÁKRYTOVÁ DESKA - PREFABRIKOVANÁ NEBO MONOLITICKÁ, STAVEBNÍ VÝŠKA 300 mm
4	ŠACHTOVÉ DNO A STĚNY - ŽB, BETON C 30/37 XF4, XD3, XA1, TL.300 mm
5	OPEVNĚNÍ DNA - KYNETA (DO 1/2 DN) A NÁSTUPNICE - OBKLAD Z TAVENÉHO ČEDIČE
6	TVRZENÝ BETON C 30/37 XF4
7	PODKLADNÍ BETON C12/15, TL. 100 mm
8	HUTNĚNÝ ŠTĚRKOPÍŠKOVÝ PODSYP TL. 0,15 m, FR. 0-16 mm
9	VIDLICOVÉ STUPADLO S POLYETHYLENOVÝM POTAHEM VE VZD. 0,25-0,35 m
10	KAPSOVÉ STUPADLO S POLYETHYLENOVÝM POTAHEM
11	PAŽENÍ
12	VODOU BOBTNÁJÍCÍ PÁSEK K TĚSNĚNÍ PRACOVNÍCH SPAR A PROSTUPŮ
13	IZOLACE PROTI ZEMNÍ VLHKOSTI SIVSLÁ (1x PENETR. NÁTĚR + 2x ASFALTOVÝ NÁTĚR)
14	IZOLACE PROTI ZEMNÍ VLHKOSTI VODOROVNÁ (1xPENETRAČNÍ NÁTĚR + 2x ASFALTOVÉ NATAVOVACÍ PÁSY + 1x OCHRANNÁ GEOTEXTILIE min 500 g/m²)
15	ZÁSYP ZEMINOU VHDNOU KE ZHUTNĚNÍ
16	BET. MAZANINA VE SPÁDU NA STROPU ŠACHTY, C20/25-XF2, tl. min. 50 mm
17	ZPĚTNÁ KLAPOKA DN800 PE-HD, NA KOLMOU BETONOVOU STĚNU
18	MADLO
19	HRADÍTKO KOLMO NA STĚNU DN800 + OVLÁDACÍ TYČ A ŠOUPÁTKOÝ POKLOP S ODLÁŽDĚNÍM - SOUČÁST SO 312

Souřadnicový systém: S-JTSK
Výškový systém: Bpv

SO 301 Odvodnění I/16

Objednatel:



Ředitelství silnic a dálnic s. p.
Čerčanská 2023/12, Krč, 140 00 Praha 4



Valbek, spol. s r.o.
Vaňurova 505/17
460 07 Liberec 3

	Vypracoval	ING. V. JURÁNEK		Zak. číslo	21-L113-001
	Zodp. projektant	ING. J. VANCL		Datum	02/2025
	Tech. kontrola	ING. D. LANDA		Stupeň	PDPS
	Akce I/16 MLADÁ BOLESLAV - MARTINOVICE			Počet formátů	4 x A4
Měřítko				1 : 25	
Č. přílohy				Paré	
Zhotovitel: Valbek, spol. s r.o. Vaňurova 505/17 460 07 Liberec 3	Příloha SPOJNÁ ŠACHTA			9	