
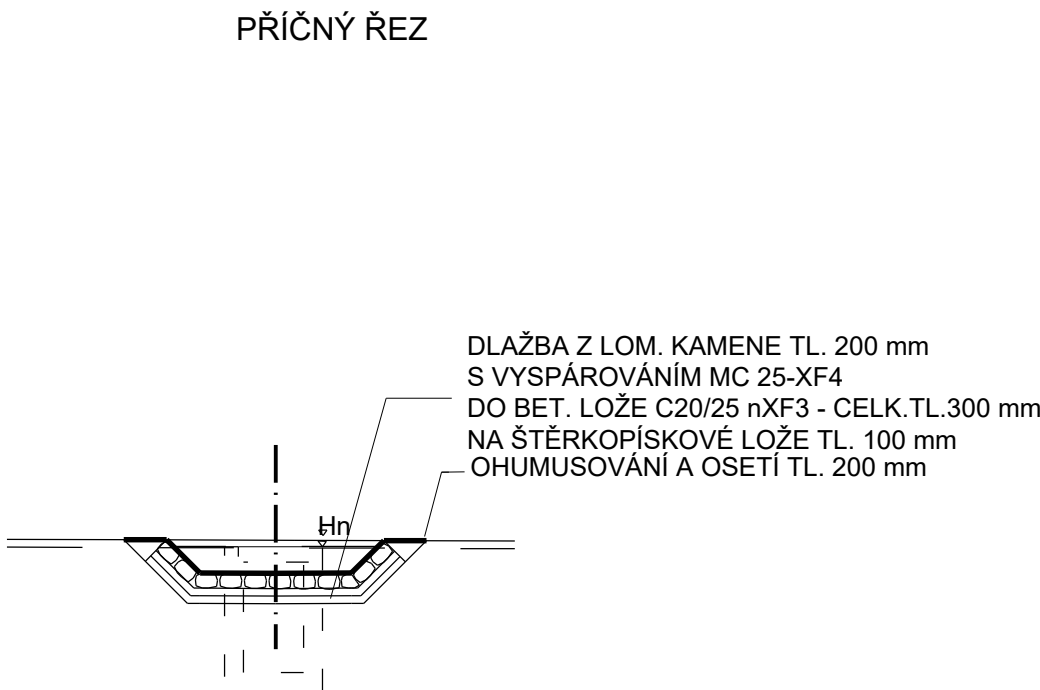


DISPOZIČNÍ VÝKRES Č.1

M 1 : 100

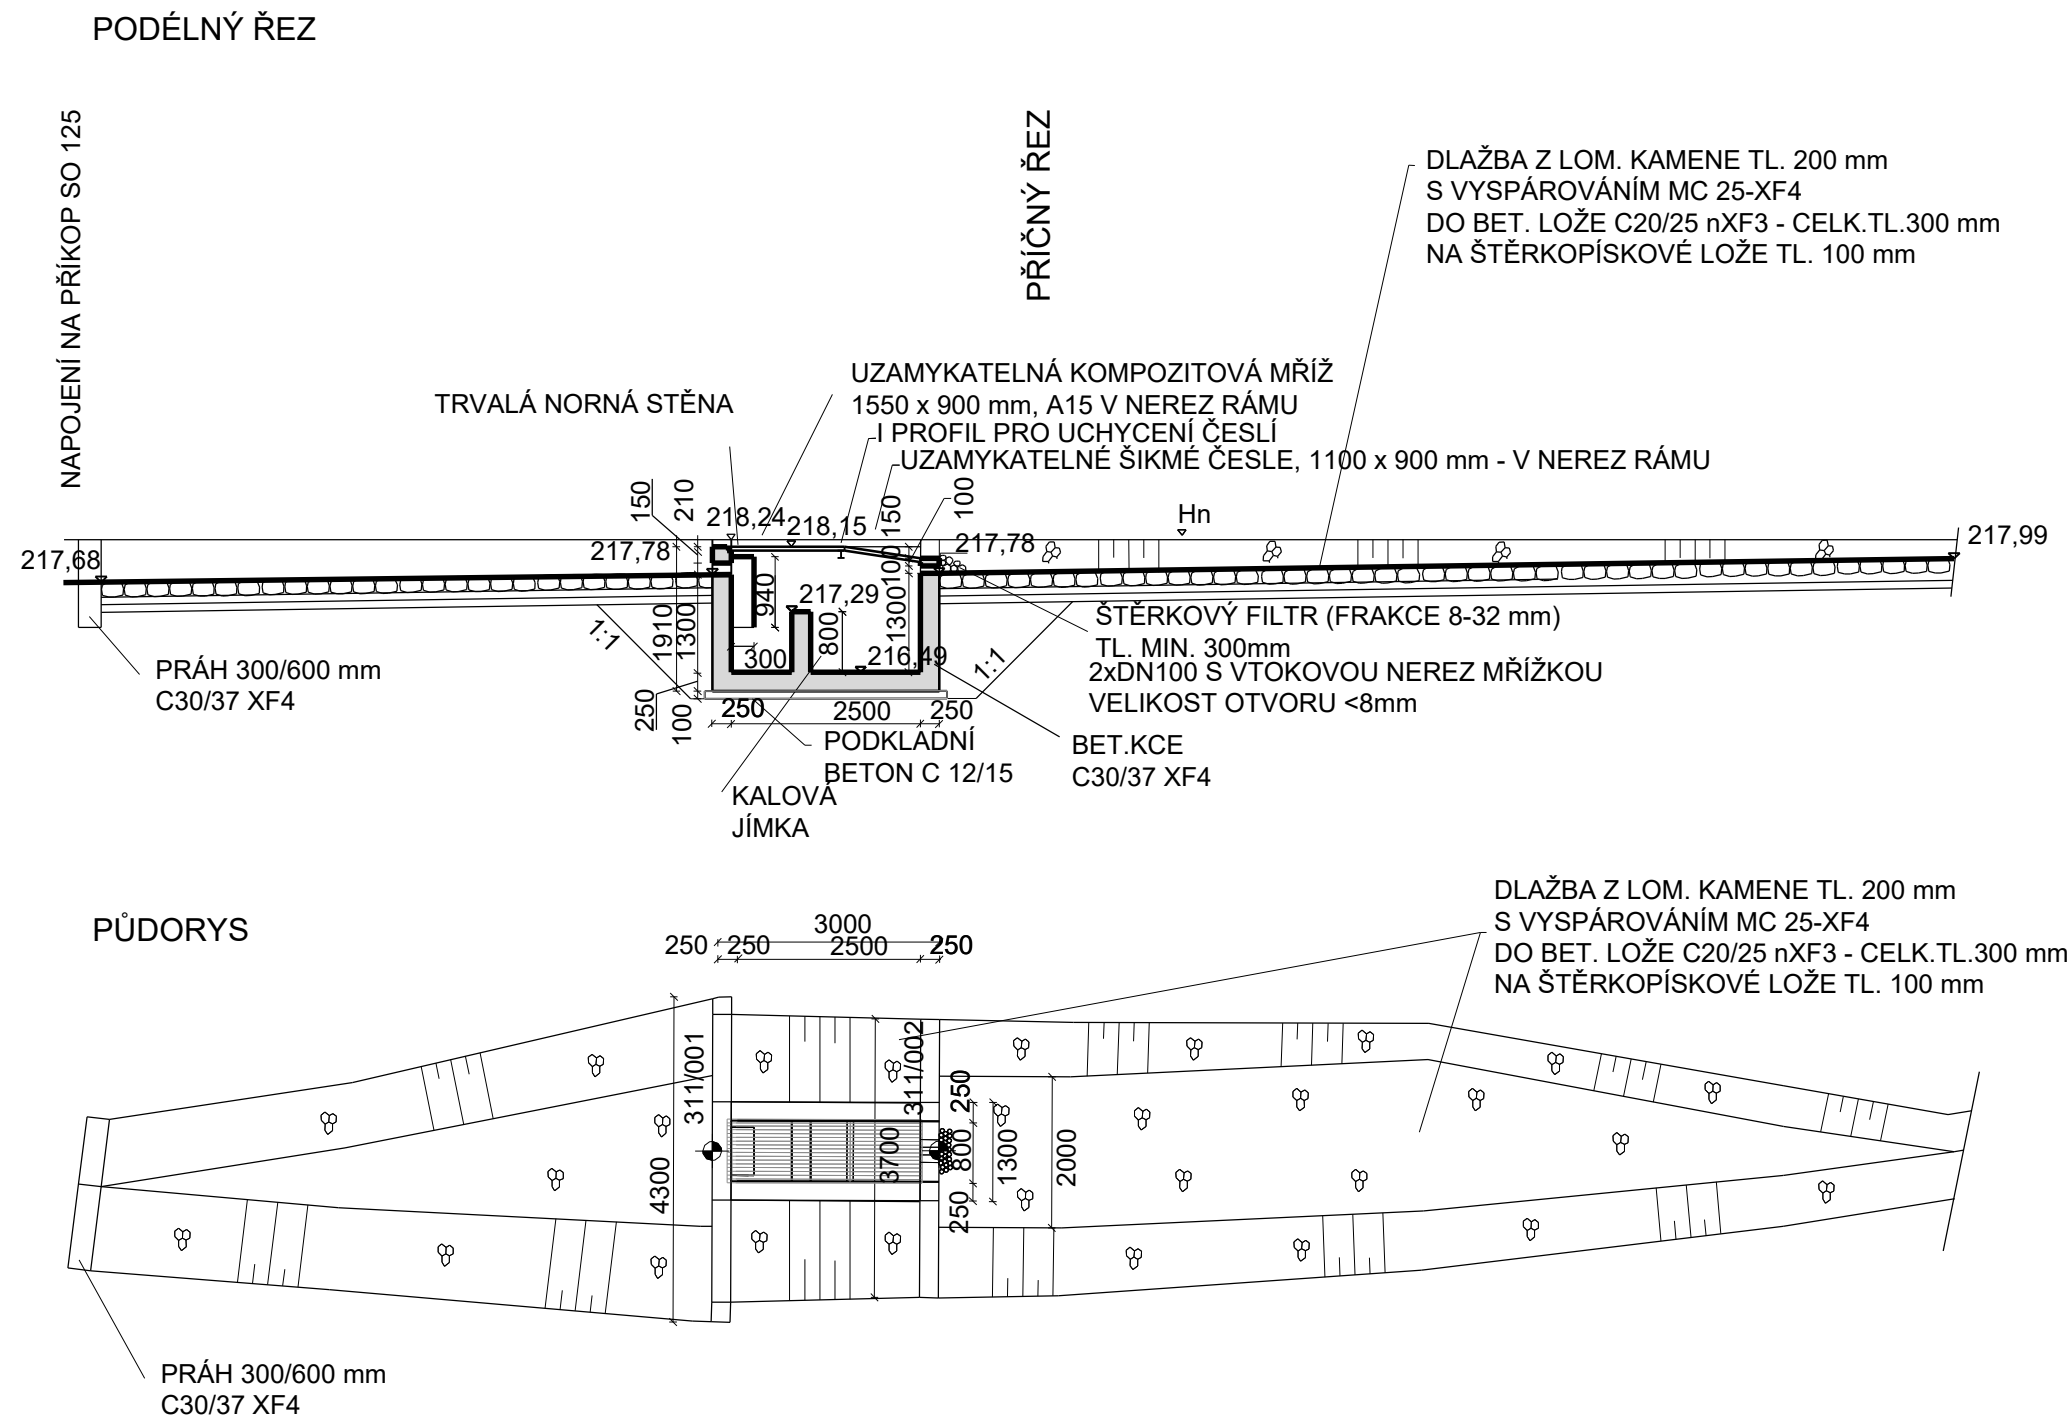

POZNÁMKA:
BETONOVÉ KONSTRUKCE VE STYKU
SE ZEMINOU OPATŘIT NÁTĚREM
1 x NPe, 2 x Na + 1 x GEOTEXTILIE
MINIMÁLNÍ KRYTÍ 45 mm
JMENOVITÉ KRYTÍ 50 mm
BETON STĚN C30/37 - XF4
OČEL B500 B St KARI SÍŤ
KOTOVANO V mm !
DLAŽBY Z KAMENE viz ČSN EN 13383-1 KÁMEN PRO VODNÍ STAVBY
HRANY BUDOU ZKOSENY 30/30 mm

Souřadnicový systém: S-JTSK
Výškový systém: Bpv

SO 311 Odvodnění MÚK Židněves

Objednatel:

ŘEDITELSTVÍ SILNIC A DÁLNIC

Ředitelství silnic a dálnic s. p.

Čerčanská 2023/12, Krč, 140 00 Praha 4

Zhotovitel:

**Valbek, spol. s r.o.**

Vaňurova 505/17
460 07 Liberec 3

	Vypracoval	ING. J. VANCL		Zak. číslo	21-L113-001
	Zodp. projektant	ING. J. VANCL		Datum	02/2025
	Tech. kontrola	ING. D. LANDA		Stupeň	PDPS
	Akce I/16 MLADÁ BOLESLAV - MARTINOVICE			Počet formátů	3 x A4
				Měřítko	1 : 100
Zhotovitel: Valbek, spol. s r.o. Vaňurova 505/17 460 07 Liberec 3	Příloha DISPOZIČNÍ VÝKRES NORNÉ STĚNY Č. 1			3.1	Č. přílohy Paré