
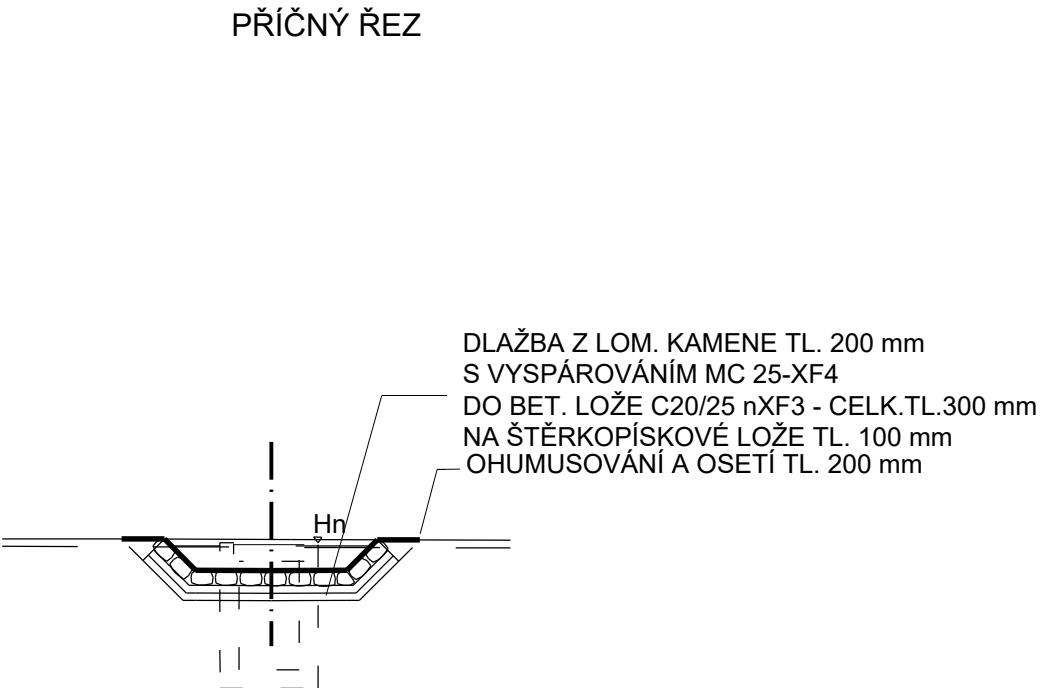


DISPOZIČNÍ VÝKRES Č.2
M 1 : 100

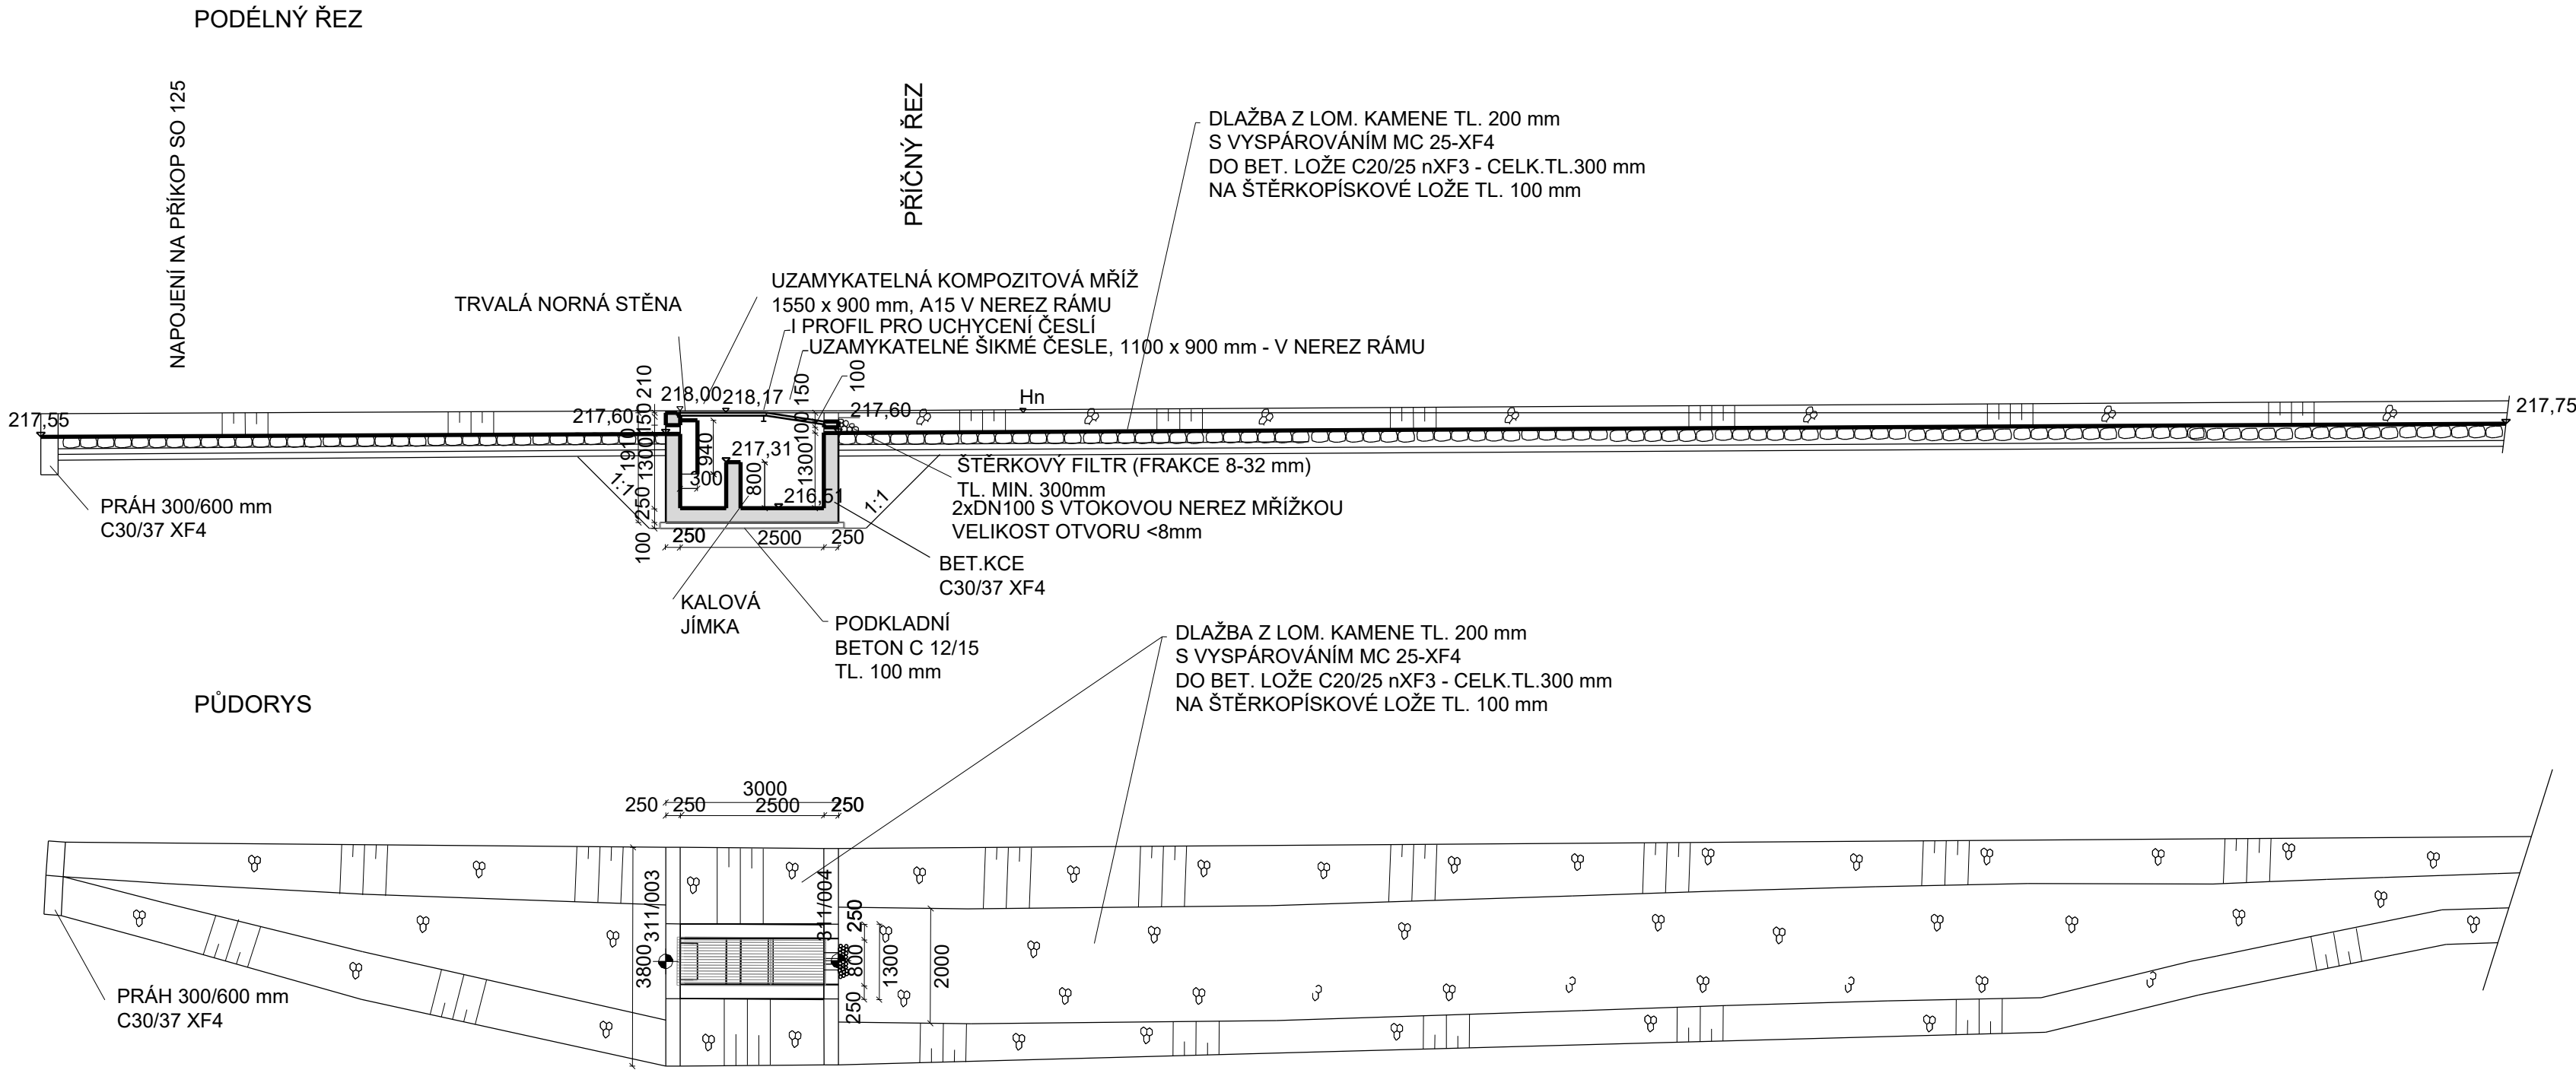

Souřadnicový systém: S-JTSK
Výškový systém: Bpv

SO 311 Odvodnění MÚK Židněves

Objednatel:



**ŘEDITELSTVÍ
SILNIC
A DÁLNIC**

Ředitelství silnic a dálnic s. p.

Čerčanská 2023/12, Krč, 140 00 Praha 4

Zhotovitel:



Valbek

Valbek, spol. s r.o.

Vaňurova 505/17
460 07 Liberec 3

	Vypracoval	ING. J. VANCL		Zak. číslo	21-L113-001	
	Zodp. projektant	ING. J. VANCL		Datum	02/2025	
	Tech. kontrola	ING. D. LANDA		Stupeň	PDPS	
	Akce			Počet formátů	4 x A4	
Zhotovitel: Valbek, spol. s r.o. Vaňurova 505/17 460 07 Liberec 3	I/16 MLADÁ BOLESLAV - MARTINOVICE			Měřitko	1 : 100	
				Č. přílohy	Paré	
	Příloha	DISPOZIČNÍ VÝKRES NORNÉ STĚNY Č. 2			3.2	