


SITUACE
M 1 : 1000

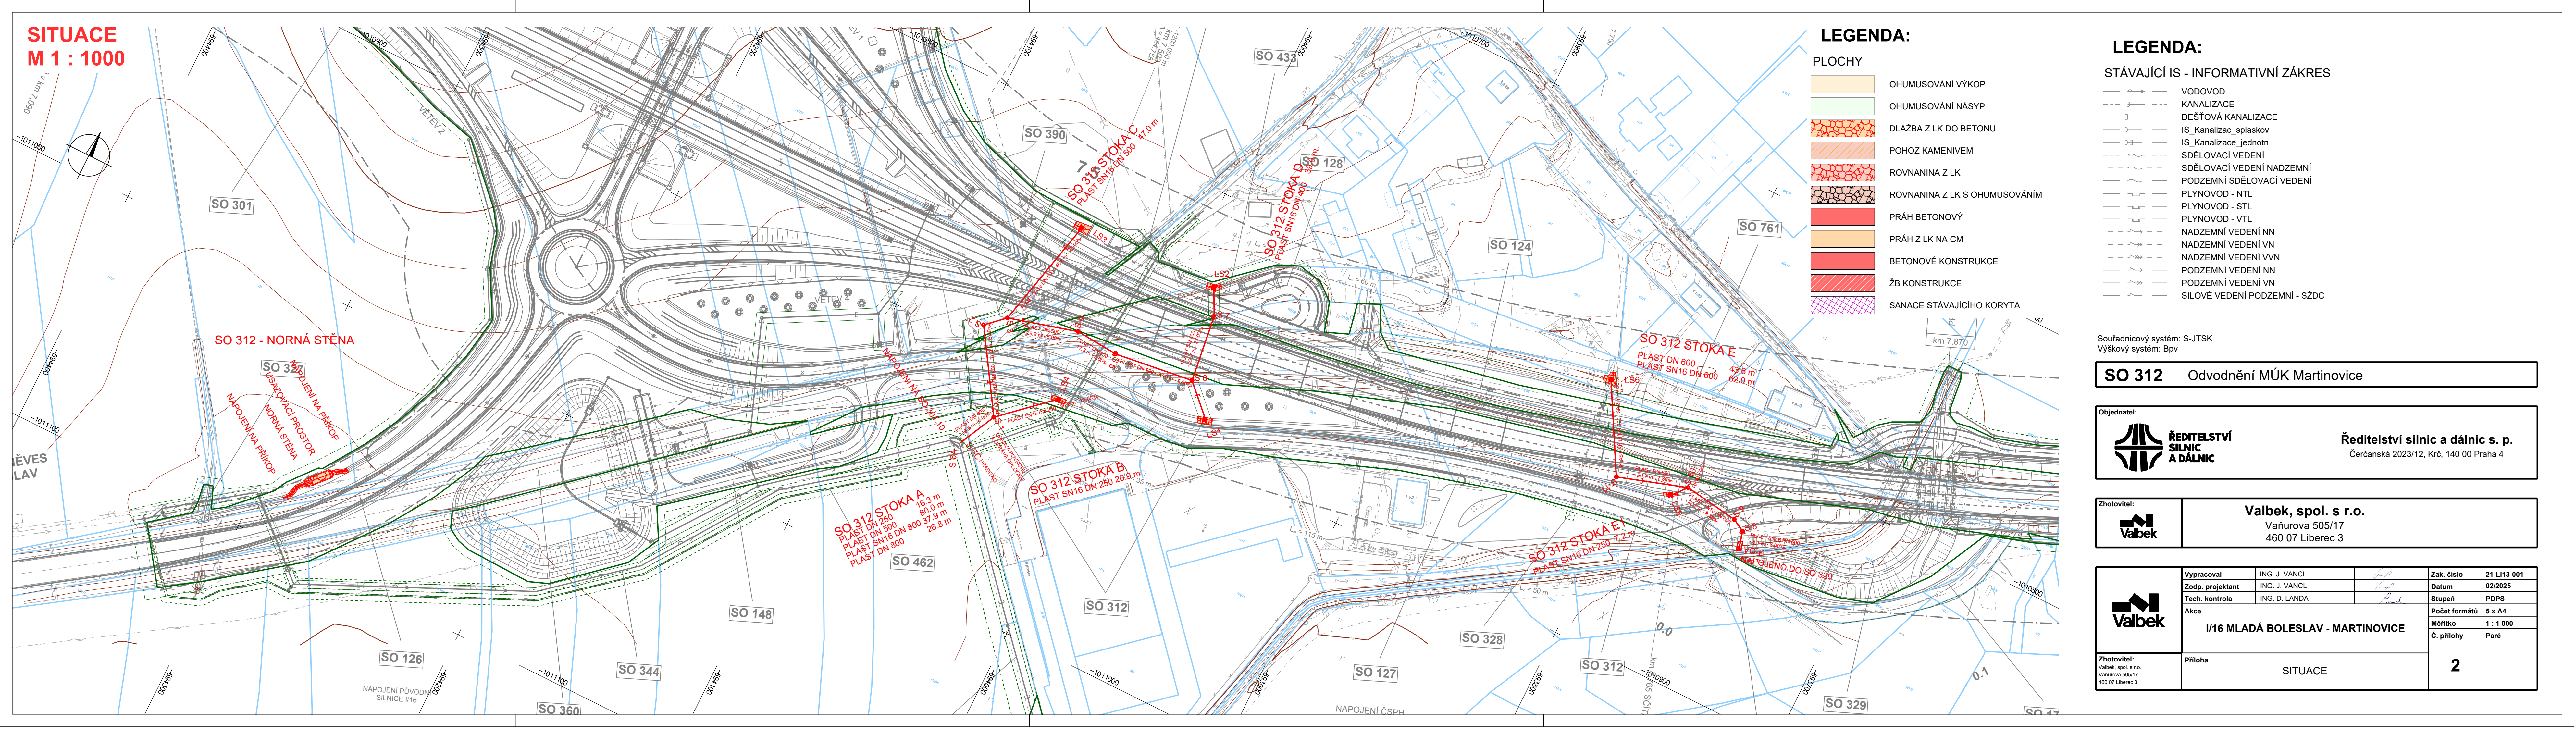

LEGENDA:

PLOCHY

- OHUMUSOVÁNÍ VÝKOP
- OHUMUSOVÁNÍ NÁSYP
- DLAŽBA Z LK DO BETONU
- POHOZ KAMENIVEM
- ROVNANINA Z LK
- ROVNANINA Z LK S OHUMUSOVÁNÍM
- PRÁH BETONOVÝ
- PRÁH Z LK NA CM
- BETONOVÉ KONSTRUKCE
- ŽB KONSTRUKCE
- SANACE STÁVAJÍCÍHO KORYTA

LEGENDA:

STÁVAJÍCÍ IS - INFORMATIVNÍ ZÁKRES

- VODOVOD
- KANALIZACE
- DEŠŤOVÁ KANALIZACE
- IS_Kanalizac_splaskov
- IS_Kanalizace_jednotn
- SDĚLOVACÍ VEDENÍ
- SDĚLOVACÍ VEDENÍ NADZEMNÍ
- PODZEMNÍ SDĚLOVACÍ VEDENÍ
- PLYNOVOD - NTL
- PLYNOVOD - STL
- PLYNOVOD - VTl
- NADZEMNÍ VEDENÍ NN
- NADZEMNÍ VEDENÍ VN
- NADZEMNÍ VEDENÍ VVN
- PODZEMNÍ VEDENÍ NN
- PODZEMNÍ VEDENÍ VN
- SILOVÉ VEDENÍ PODZEMNÍ - SŽDC

Souřadnicový systém: S-JTSK
Výškový systém: Bpv

SO 312 Odvodnění MÚK Martinovice

Objednatel:
ŘEDITELSTVÍ SILNIC A DÁLNIC
Ředitelství silnic a dálnic s. p.
Čerčanská 2023/12, Krč, 140 00 Praha 4

Zhotovitel:
Valbek
Valbek, spol. s r.o.
Vaňurova 505/17
460 07 Liberec 3

	Vypracoval	ING. J. VANCL		Zak. číslo	21-L113-001
	Zodp. projektant	ING. J. VANCL		Datum	02/2025
	Tech. kontrola	ING. D. LANDA		Stupeň	PDPS
	Akce	I/16 MLADÁ BOLESLAV - MARTINOVICE			Počet formátů
Zhotovitel: spol. s r.o. ra 505/17 Liberec 3	Měřítko				1 : 1 000
	Č. přílohy				Paré
	Příloha	SITUACE			2