
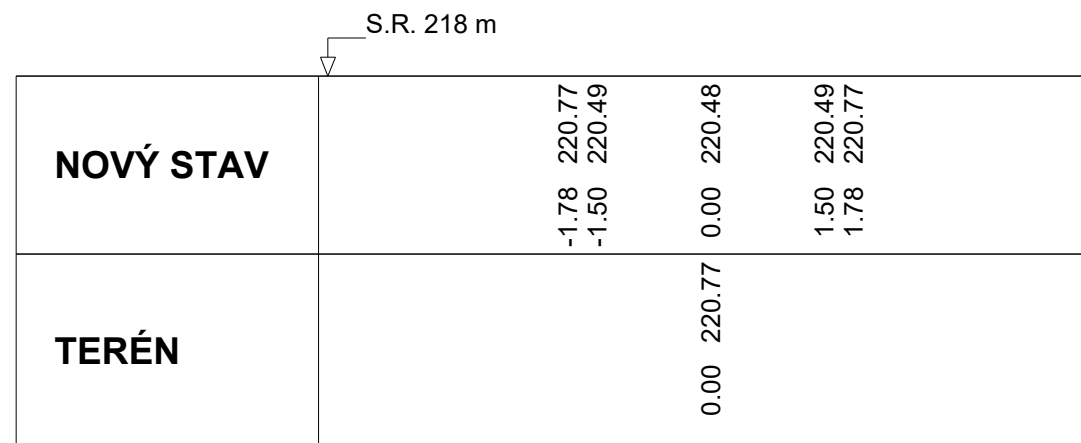


M 1 : 100

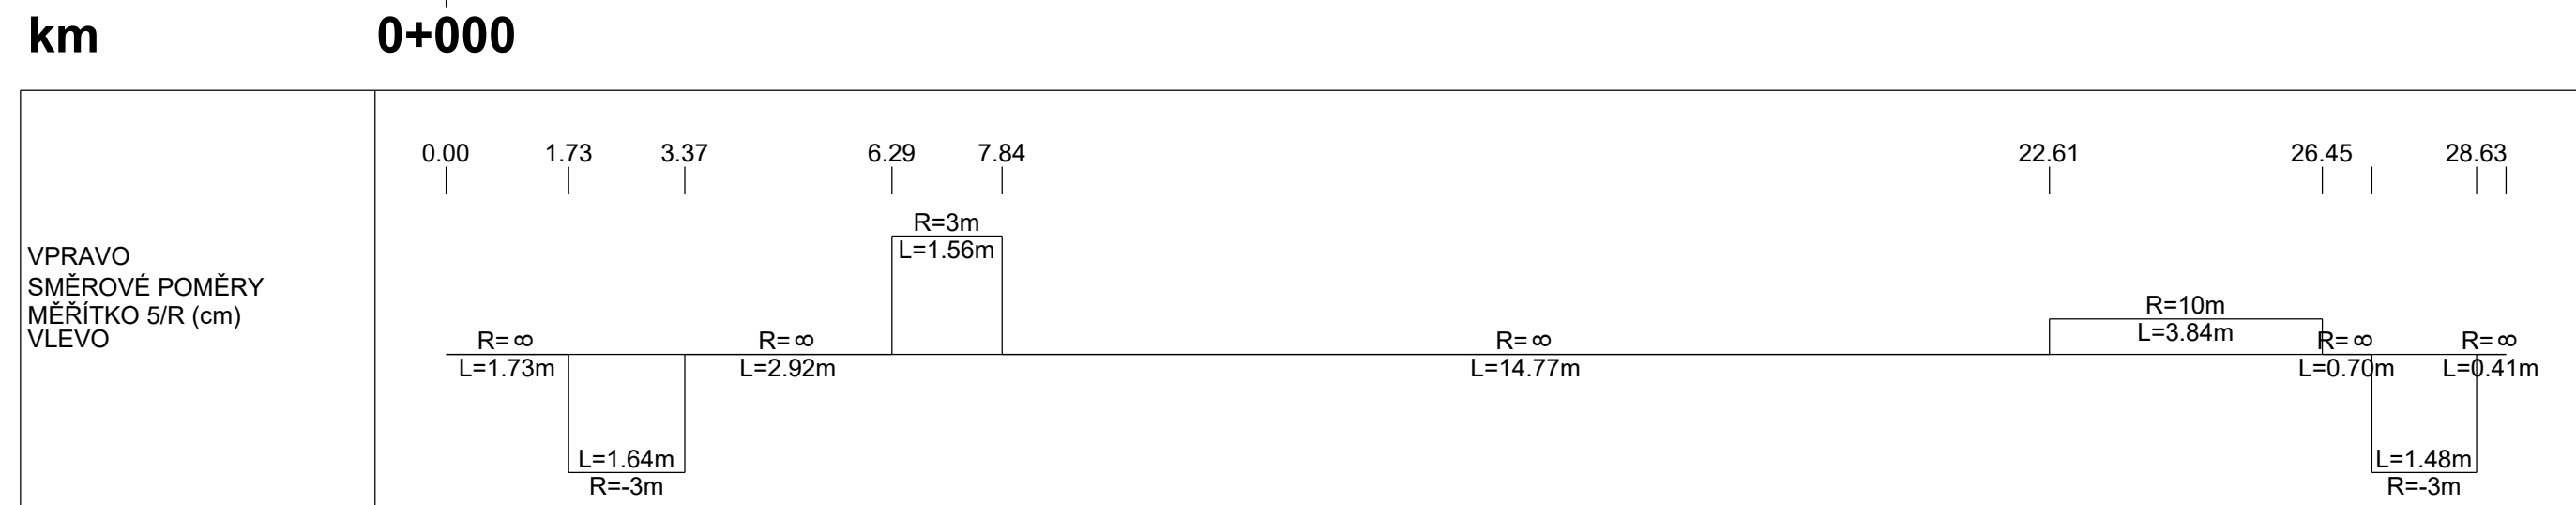

	S.R. 218 m	
NOVÝ STAV	-0.88 220.82 -0.30 220.53 0.00 220.53 0.30 220.53 1.02 220.82	
TERÉN	0.00 220.82	

	Vypracoval	ING. J. VANCL		Zak. číslo	21-L1(3)-001	
	Zodp. projektant	ING. J. VANCL		Datum	02/2025	
	Tech. kontrola	ING. D. LANDA		Stupeň	PDPS	
	Akce			Počet formátů	5 x A4	
Zhotovitel: Valbek, spol. s r.o. Vaňurova 505/17 460 07 Liberec 3	I/16 MLADÁ BOLESLAV - MARTINOVICE			Měřítko	1 : 100	
				Č. přílohy	Paré	
	Příloha	DISPOZIČNÍ VÝKRES NORNÉ STĚNY			3	