
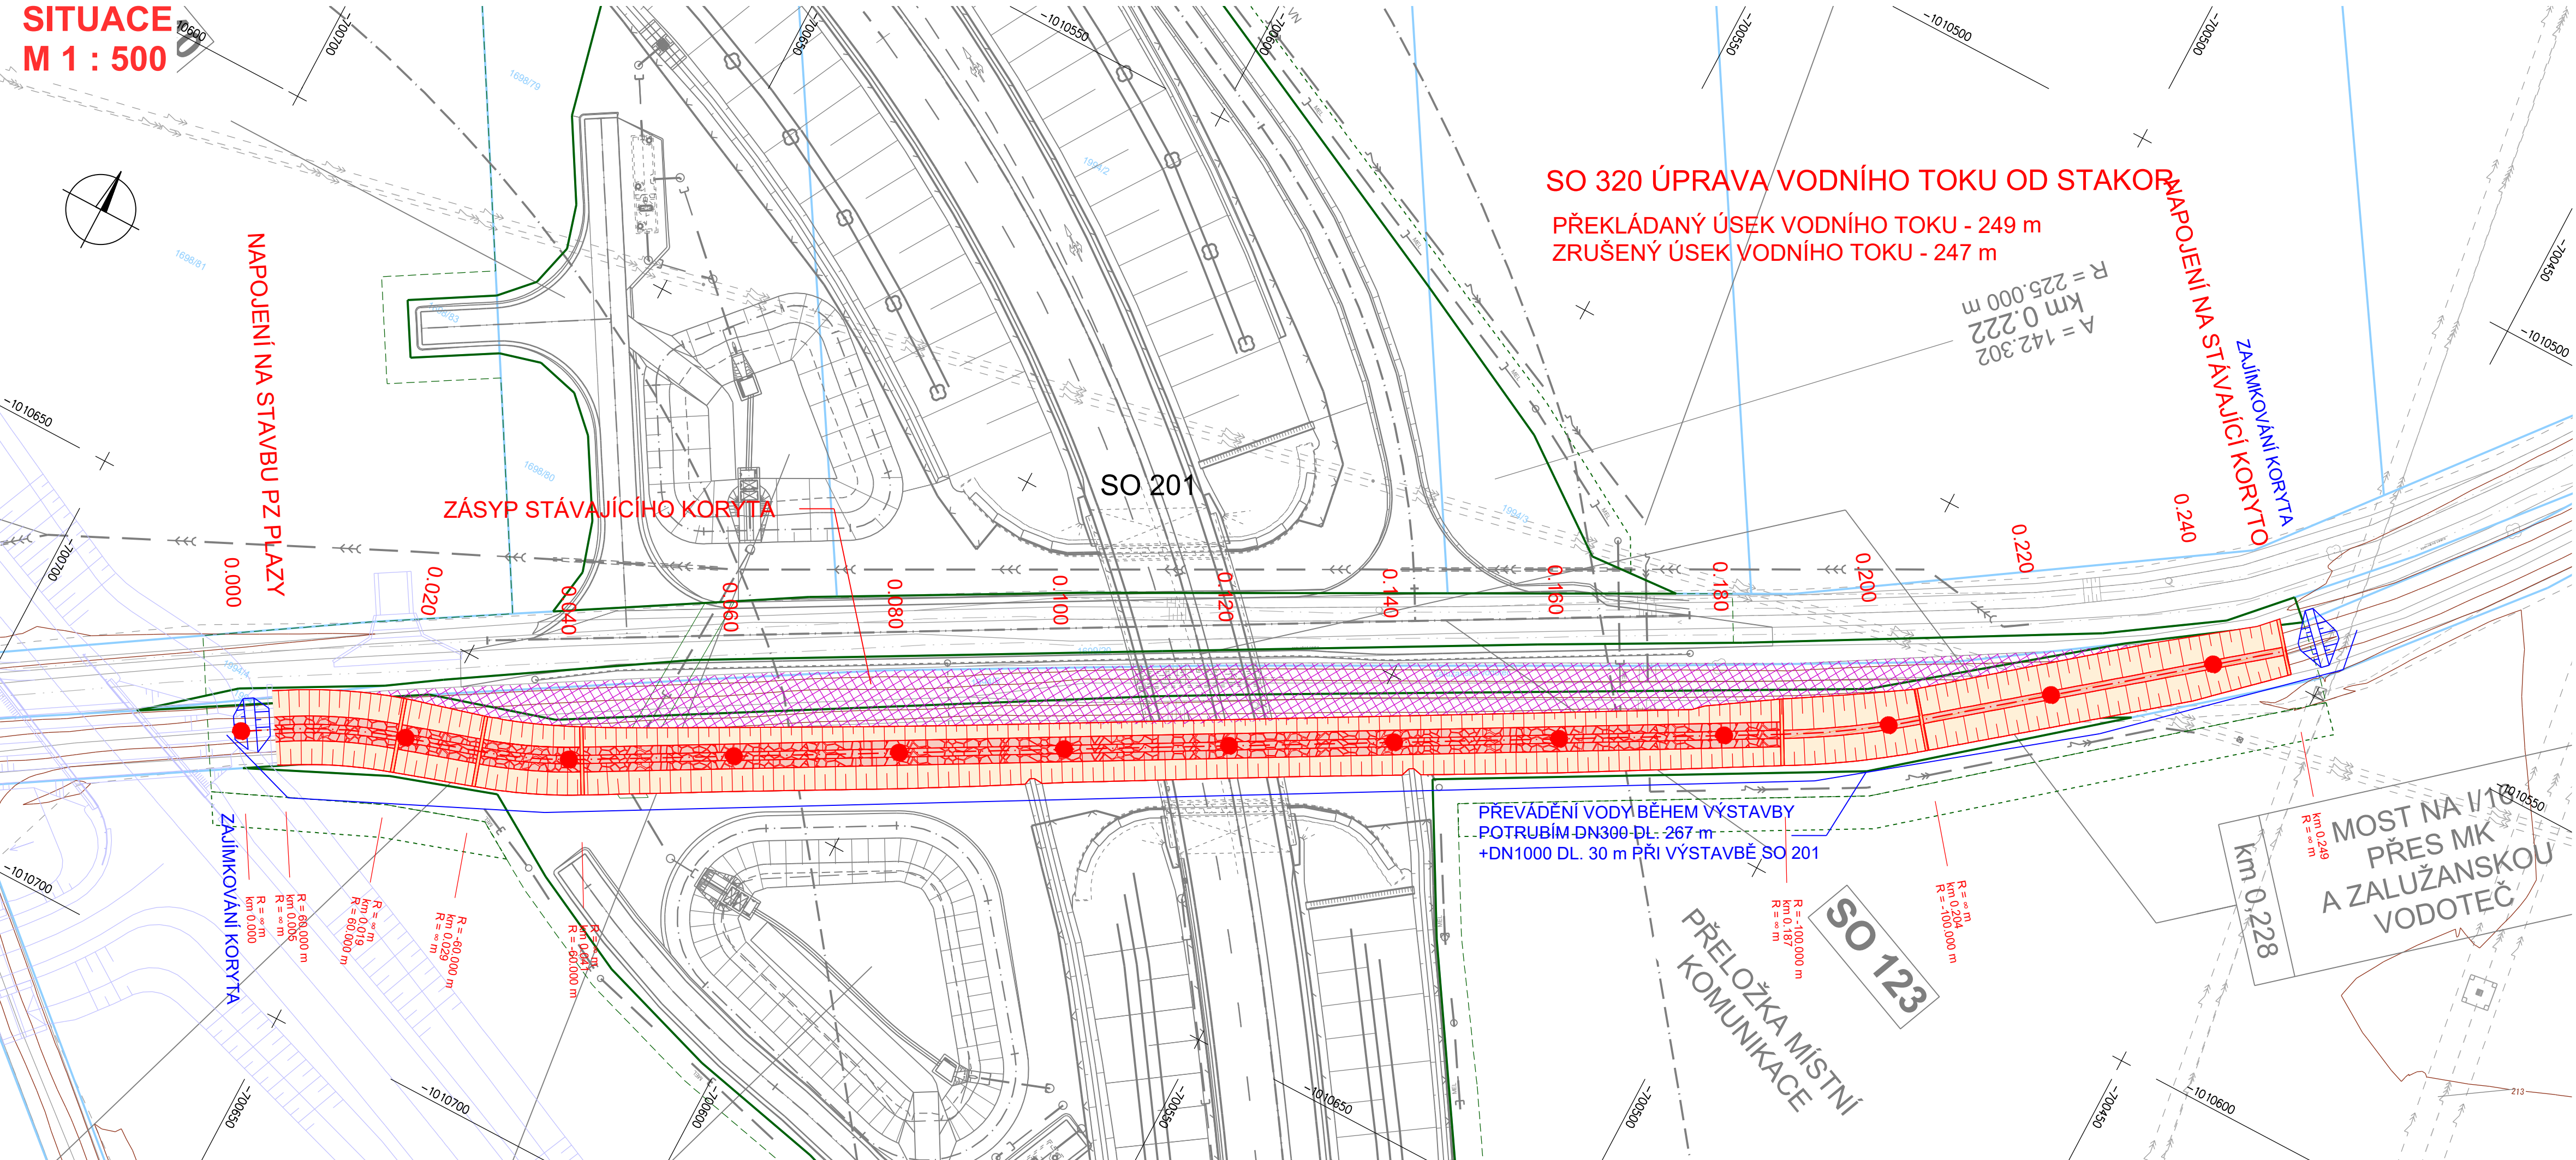


SITUACE
M 1 : 500

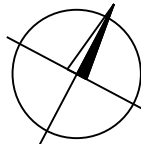

LEGENDA:

PLOCHY

- OHUMUSOVÁNÍ VÝKOP
- OHUMUSOVÁNÍ NÁSYP
- DLAŽBA Z LK DO BETONU
- POHOZ KAMENIVEM
- ROVNANINA Z LK
- ROVNANINA Z LK S OHUMUSOVÁNÍM
- PRÁH BETONOVÝ
- PRÁH Z LK NA CM
- BETONOVÉ KONSTRUKCE
- ŽB KONSTRUKCE
- SANACE STÁVAJÍCÍHO KORYTA

Souřadnicový systém: S-JTSK
Výškový systém: Bpv

SO 320 Úprava vodního toku od Strakor

Objednatel:



Ředitelství silnic a dálnic s. p.
Čerčanská 2023/12, Krč, 140 00 Praha 4

Zhotovitel:



Valbek, spol. s r.o.
Vaňurova 505/17
460 07 Liberec 3



Vypracoval	ING. J. VANCL	Zak. číslo	21-L113-001
Zodp. projektant	ING. J. VANCL	Datum	02/2025
Tech. kontrola	ING. D. LANDA	Stupeň	PDPS
Akce		Počet formátů	4 x A4
I/16 MLADÁ BOLESLAV - MARTINOVICE		Měřítko	1 : 500
		Č. přílohy	Paré
Příloha		SITUACE	

Zhotovitel:
Valbek, spol. s r.o.
Vaňurova 505/17
460 07 Liberec 3