


VZOROVÉ PŘÍČNÉ ŘEZY

M 1:100


VZOROVÝ ŘEZ NEOPEVNĚNÝM KORYTEM

PLATNOST: KM 0,187 13 - KÚ

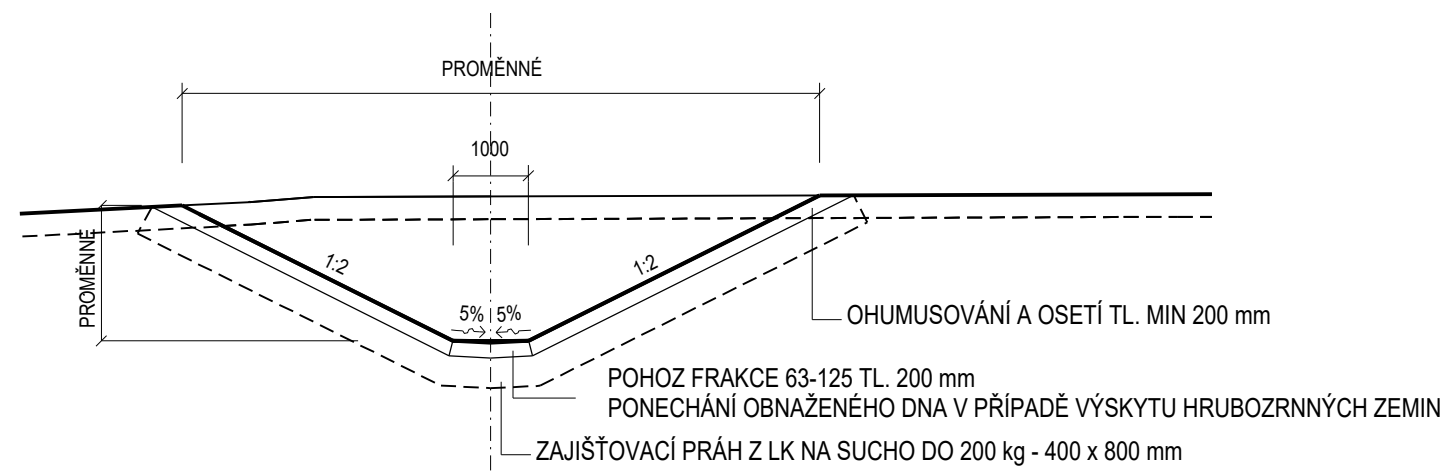

VZOROVÝ ŘEZ OPEVNĚNÝM KORYTEM
OPEVNĚNÍ - ROVNANINA Z LOMOVÉHO KAMENE

PLATNOST: KM ZÚ - 0,187 13

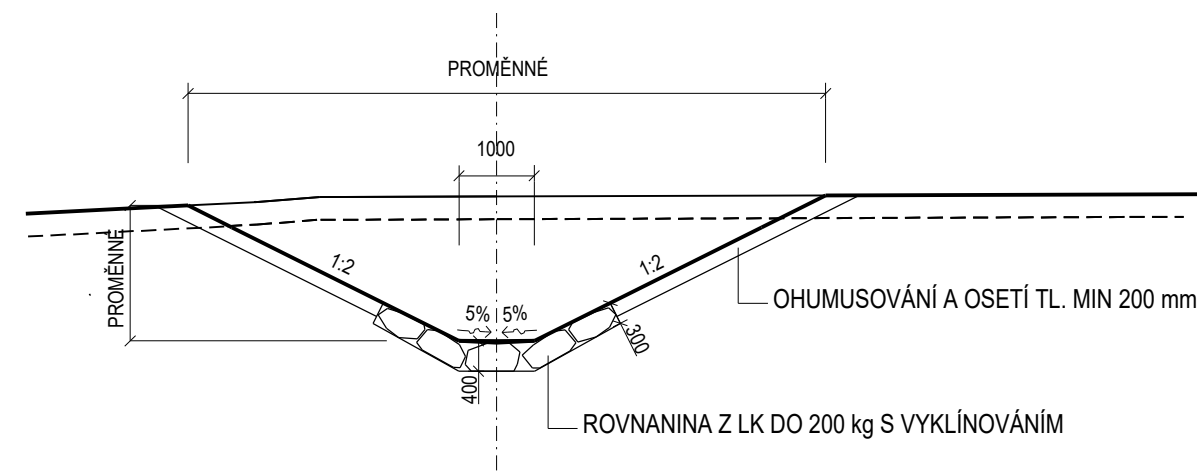

Souřadnicový systém: S-JTSK
Výškový systém: Bpv

SO 320 Úprava vodního toku od Strakor

Objednatel:

**ŘEDITELSTVÍ
SILNIC
A DÁLNIC**

Ředitelství silnic a dálnic s. p.

Čerčanská 2023/12, Krč, 140 00 Praha 4

Zhotovitel:

**Valbek, spol. s r.o.**

Vaňurova 505/17
460 07 Liberec 3



Vypracoval	ING. J. VANCL		Zak. číslo	21-L113-001
Zodp. projektant	ING. J. VANCL		Datum	02/2025
Tech. kontrola	ING. D. LANDA		Stupeň	PDPS
Akce I/16 MLADÁ BOLESLAV - MARTINOVICE			Počet formátů	3 x A4
			Měřítko	1 : 100
			Č. přílohy	Paré
Příloha	VZOROVÉ PŘÍČNÉ ŘEZY		4	