
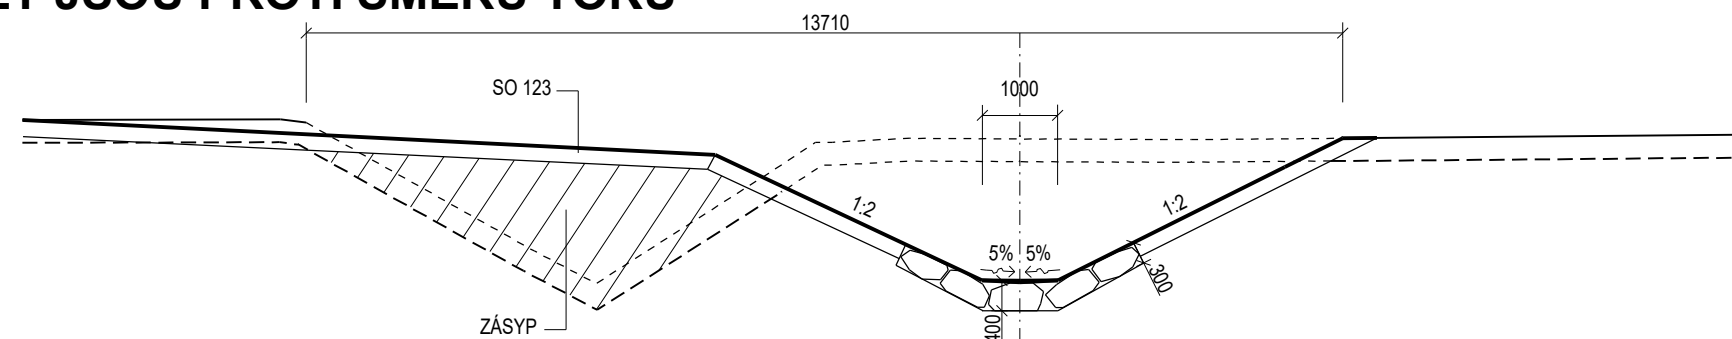
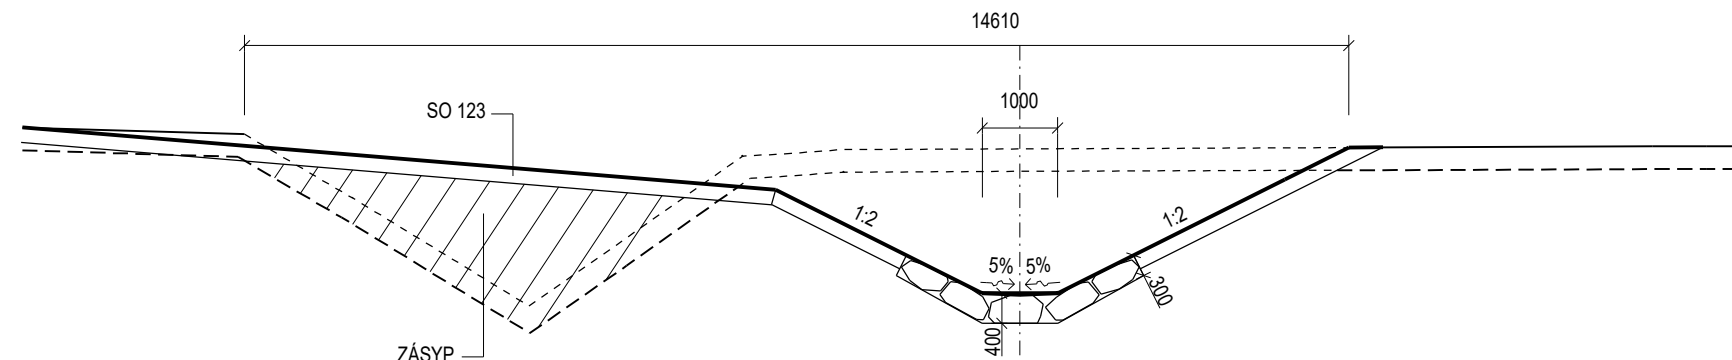



ŘEZY JSOU PROTI SMĚRU TOKU

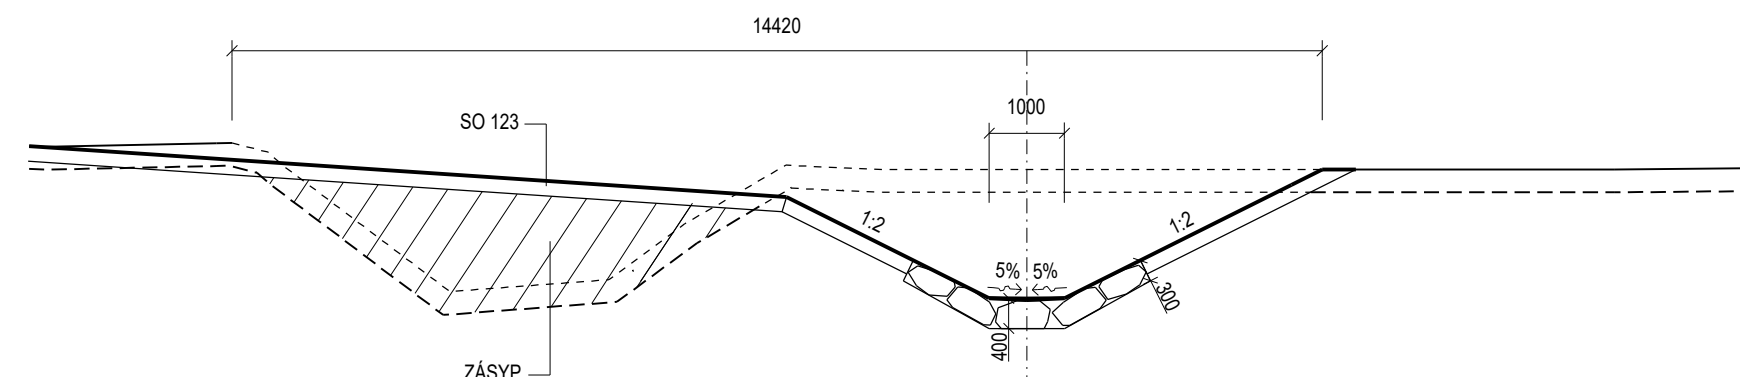


NOVÝ STAV	TERÉN
	-9.78 212.54 -9.44 212.50
	-6.42 210.80 -5.61 210.37
	-4.03 212.07 -3.32 211.83 -2.71 212.23 -2.48 212.24
	-1.47 212.29 -0.50 210.41 0.00 210.41 0.50 210.41
	2.27 212.28 4.30 212.30

[illegible]


NOVÝ STAV	SR.ROVINA 208 m									
	-8.83	212.43								
TERÉN	-7.63	210.77								
	-5.53	210.93								
	-4.53	211.66								
	-3.19	212.44								
	-2.42	212.40								
	-1.91	212.38								
	0.00	212.38								
	7.77	212.38								

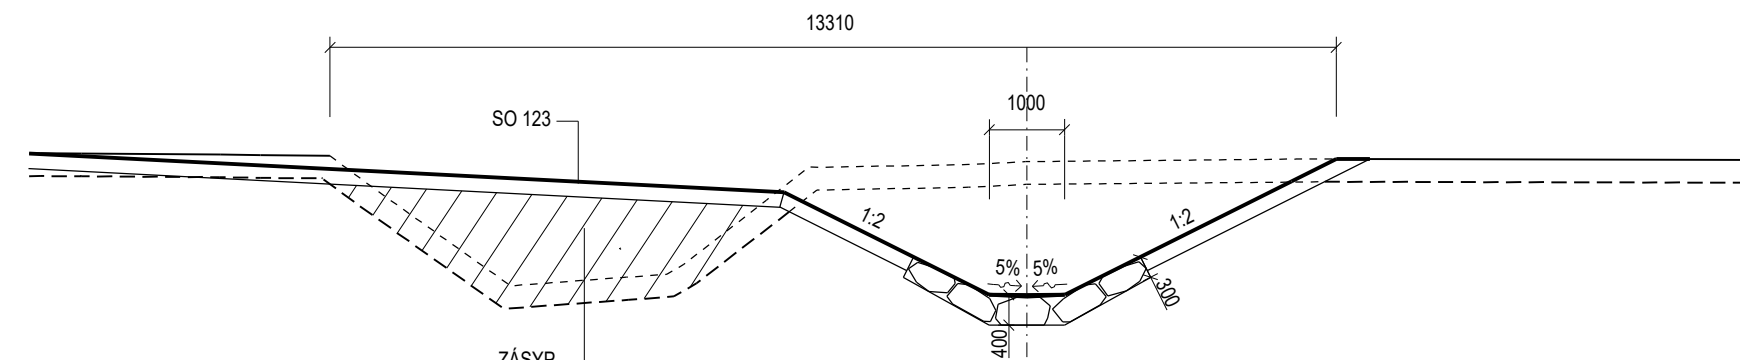

NOVÝ STAV	SR.ROVINA 208 m									
	-9.22	212.65	-8.65	212.23	-6.83	210.93	-5.30	211.04	-4.76	211.08
TERÉN	-4.54	211.21	-3.21	212.17	-2.87	212.50	-2.73	212.50	-0.78	212.53
	-0.02	212.57	-0.50	210.81	-0.50	210.81	0.00	210.81	0.50	210.81
	3.56	212.61	4.09	212.61						

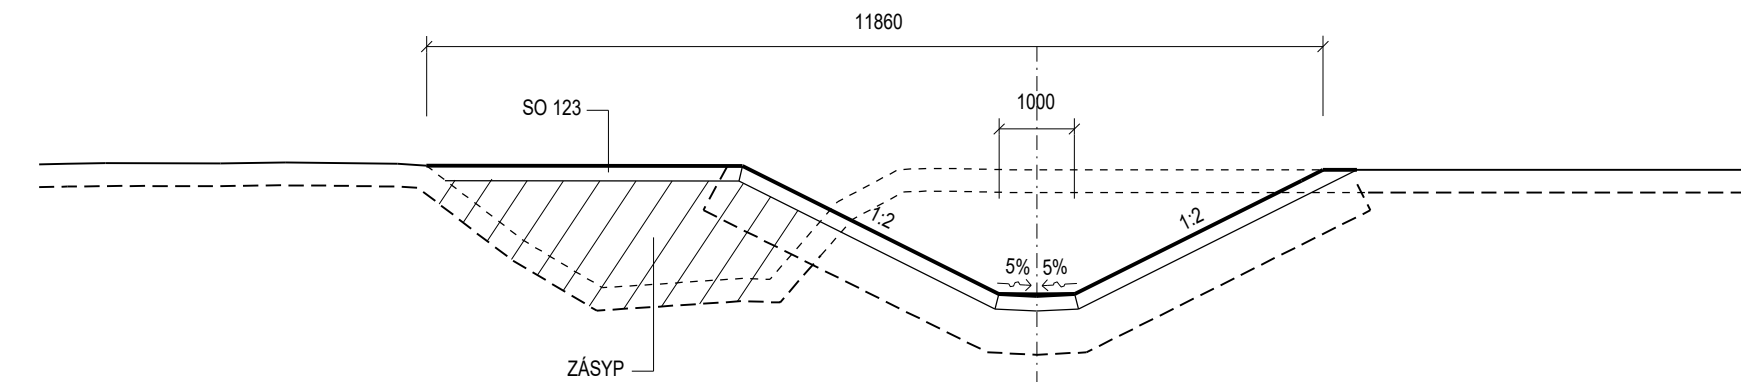

SR.ROVINA 208 m	
NOVÝ STAV	212.69
TERÉN	-9.93
	212.67
	-8.45
	212.64
	-8.07
	211.66
	-6.79
	211.03
	-5.75
	211.15
	-3.88
	211.14
	-3.53
	212.17
	-2.64
	212.59
	-1.83
	212.61
	-1.39
	212.59
	-0.25
	212.59
	0.00
	210.94
	-0.50
	210.94
	0.50
	210.94
	3.79
	212.59

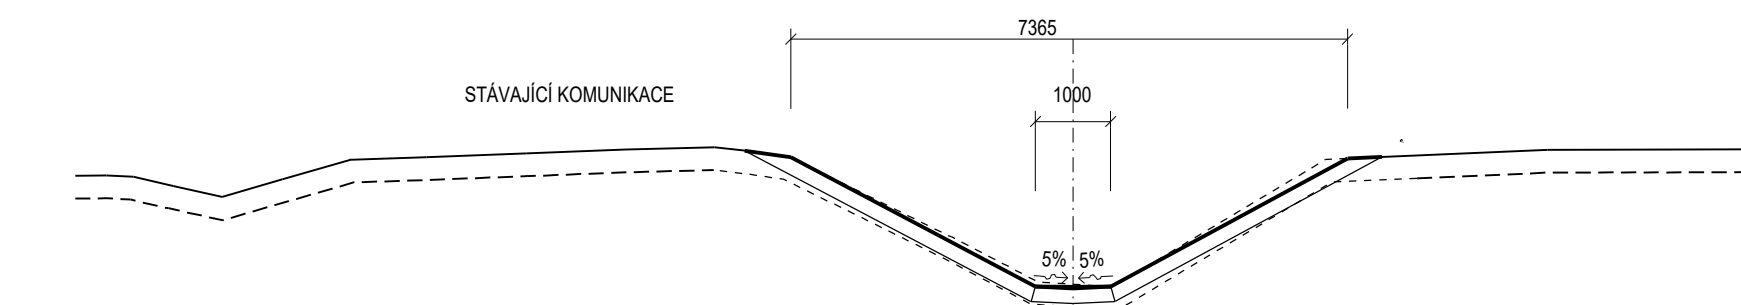

SR. ROVINA 208 m	
NOVÝ STAV	
TERÉN	
-9.56	212.76
-8.55	212.79
-7.23	212.84
-5.92	212.89
-4.74	212.92
-4.28	212.87
-3.73	212.79
-1.61	211.74
-0.47	211.14
0.00	211.11
0.26	211.09
0.50	211.06
0.52	211.08
3.28	212.73
3.34	212.76
6.28	212.89

SO 320 Úprava vodního toku od Strakon



Ředitelství silnic a dálnic s. p.
Čerčanská 2023/12, Krč, 140 00 Praha 4



Valbek, spol. s r.o.
Vaňurova 505/17
460 07 Liberec 3

	Vypracoval	ING. J. VANCL		Zak. číslo	21-L113-001
	Zodp. projektant	ING. J. VANCL		Datum	02/2025
	Tech. kontrola	ING. D. LANDA		Stupeň	PDPS
	Akce	I/16 MLADÁ BOLESLAV - MARTINOVICE			Počet formátů
	Měřítko				1 : 100
	Č. přílohy				Paré
Zhotovitel: Valbek, spol. s r.o. Vauřuova 505/17 460 07 Liberec 3	Příloha	PŘÍČNÉ ŘEZY			5