

VZOROVÉ PŘÍČNÉ ŘEZY

M 1:100

VZOROVÝ ŘEZ NEOPEVNĚNÝM KORYTEM


PLATNOST: KM 0,056 00 - KÚ

VZOROVÝ ŘEZ OPEVNĚNÝM KORYTEM
OPEVNĚNÍ - ROVNANINA Z LOMOVÉHO KAMENE

PLATNOST: KM ZÚ - 0,007 60
0,044 00 - 0,056 00

VZOROVÝ ŘEZ KORYTEM
OPEVNĚNÍ DLAŽBOU Z LOMOVÉHO KAMENE
- V MÍSTĚ PŘED PROPUSTKY
- ČÁSTEČNĚ SOUČÁST SO 101

PLATNOST: KM 0,007 60 - 0,044 00

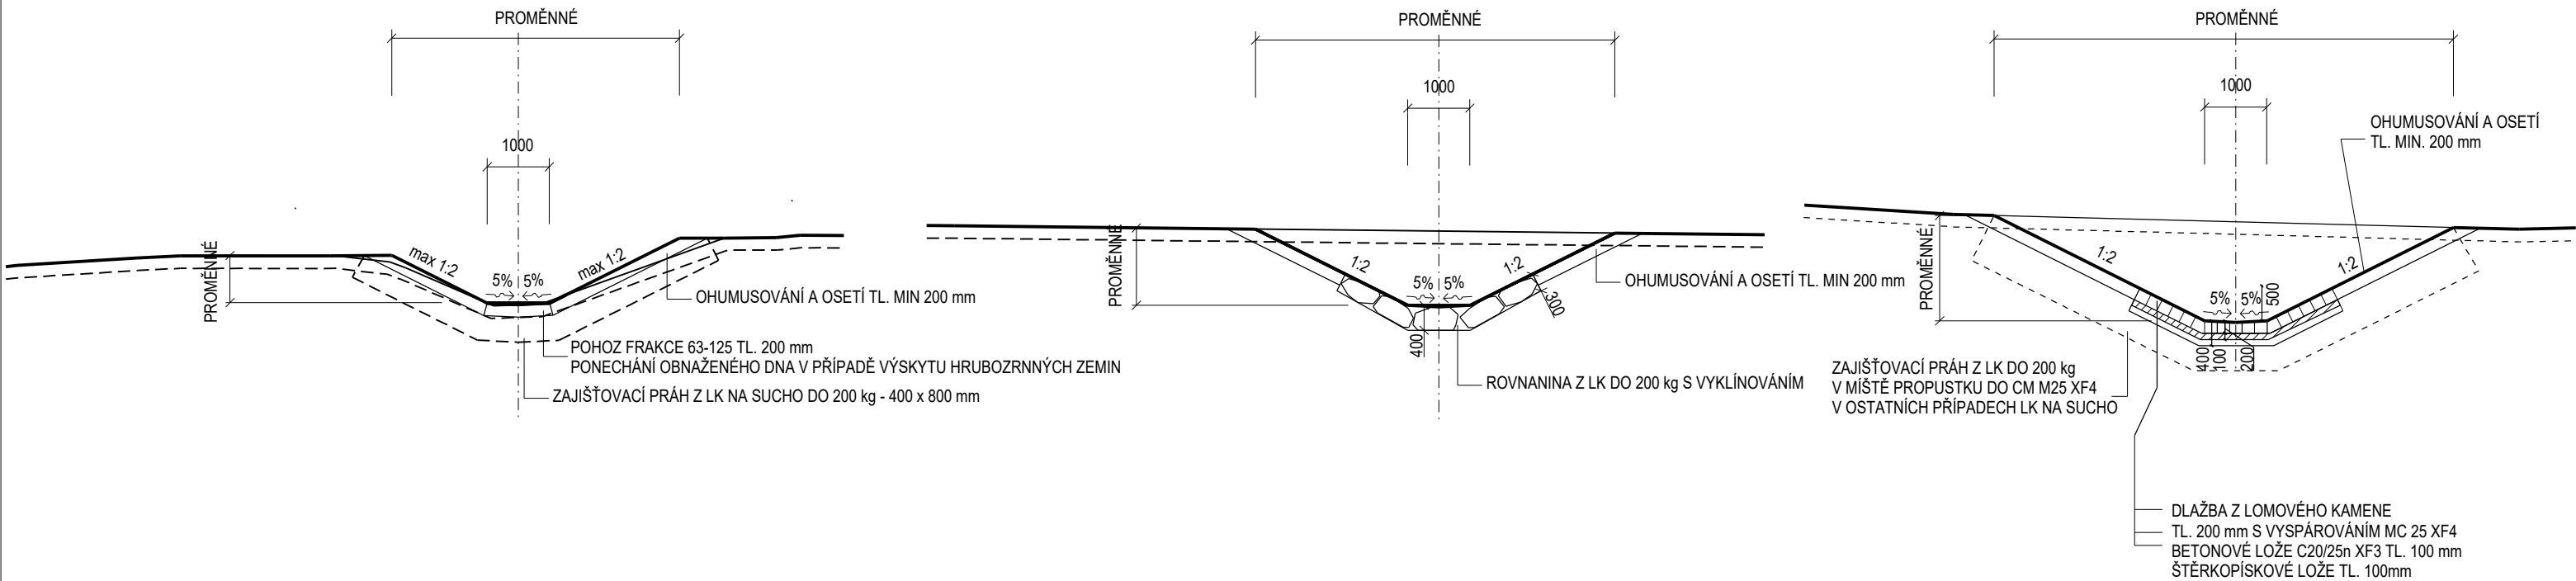

Souřadnicový systém: S-JTSK
Výškový systém: Bpv

SO 321 Úprava HOZ 1 v km 0,654

Objednatel:



**ŘEDITELSTVÍ
SILNIC
A DÁLNIC**

Ředitelství silnic a dálnic s. p.
Čerčanská 2023/12, Krč, 140 00 Praha 4

Zhotovitel:



Valbek, spol. s r.o.
Vaňurova 505/17
460 07 Liberec 3

	Vypracoval	ING. J. VANCL		Zak. číslo	21-LI13-001
	Zodp. projektant	ING. J. VANCL		Datum	02/2025
	Tech. kontrola	ING. D. LANDA		Stupeň	PDPS
	Akce I/16 MLADÁ BOLESLAV - MARTINOVICE			Počet formátů	3 x A4
				Měřítko	1 : 100
Zhotovitel: Valbek, spol. s r.o. Vaňurova 505/17 460 07 Liberec 3	Příloha VZOROVÉ PŘÍČNÉ ŘEZY			Č. přílohy	Paré
				4	