
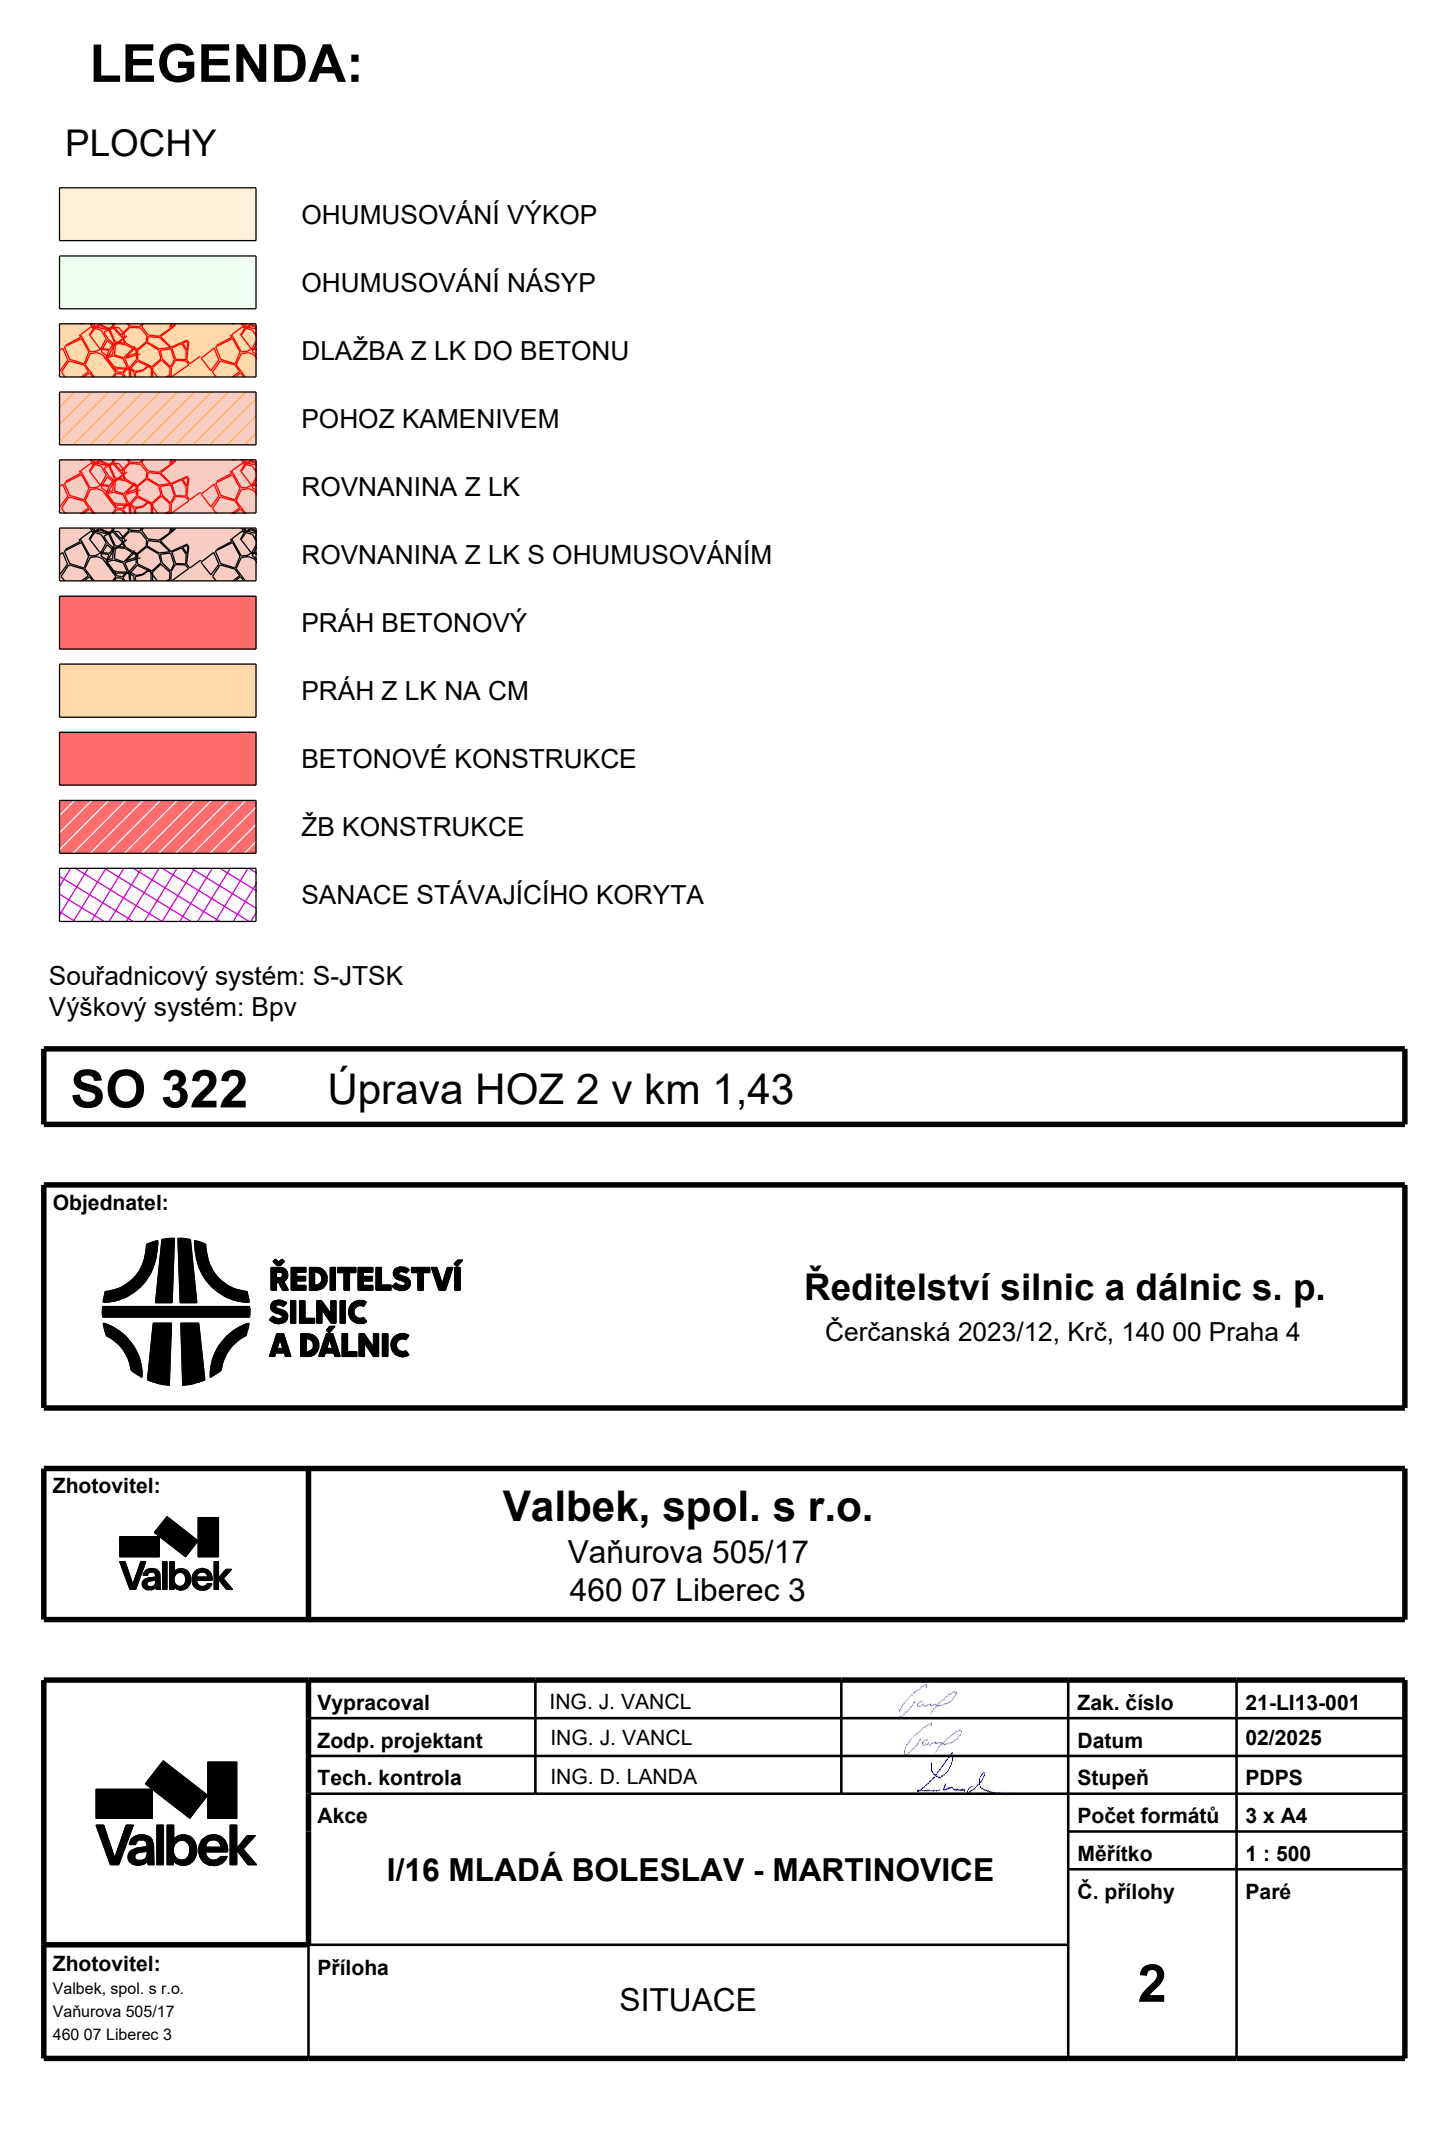
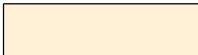


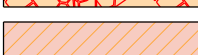

PLOCHY

- | | |
|---|-------------------------------|
|  | OHUMUSOVÁNÍ VÝKOP |
|  | OHUMUSOVÁNÍ NÁSYP |
|  | DLAŽBA Z LK DO BETONU |
|  | POHOZ KAMENIVEM |
|  | ROVNANINA Z LK |
|  | ROVNANINA Z LK S OHUMUSOVÁNÍM |
|  | PRÁH BETONOVÝ |
|  | PRÁH Z LK NA CM |
|  | BETONOVÉ KONSTRUKCE |
|  | ŽB KONSTRUKCE |
|  | SANACE STÁVAJÍCÍHO KORYTA |

Souřadnicový systém: S-JTSK
Výškový systém: Bpv

SO 322	Úprava HOZ 2 v km 1,43
---------------	------------------------

Objednatel:



**ŘEDITELSTVÍ
SILNIC
A DÁLNIC**

Ředitelství silnic a dálnic s. p.
Čerčanská 2023/12, Krč, 140 00 Praha 4

Zhotovitel:



Valbek, spol. s r.o.
Vaňurova 505/17
460 07 Liberec 3



Vypracoval	ING. J. VANCEL
Zodp. projektant	ING. J. VANCEL
Tech. kontrola	ING. D. LANDA

I/16 MLADÁ BOLESLAV - MARTINOVICE

Zhotovitel:
Valbek, spol. s r.o.
Vaňurova 505/17
460 07 Liberec 3

Příloha	SITUACE
---------	---------

Zak. číslo	21-LI13-001
Datum	02/2025
Stupeň	PDPS
Počet formátů	3 x A4
Měřítko	1 : 500
Č. přílohy	Paré

2