



VZOROVÉ PŘÍČNÉ ŘEZY
M 1:100


VZOROVÝ ŘEZ BRODEM - V OSE PŘÍSTUPOVÉ KOMUNIKACE SO 143 / SO 151.5
SOUČÁST SO 143 A SO 151.5
PLATNOST: KM 0,091 04 - 0,142 27

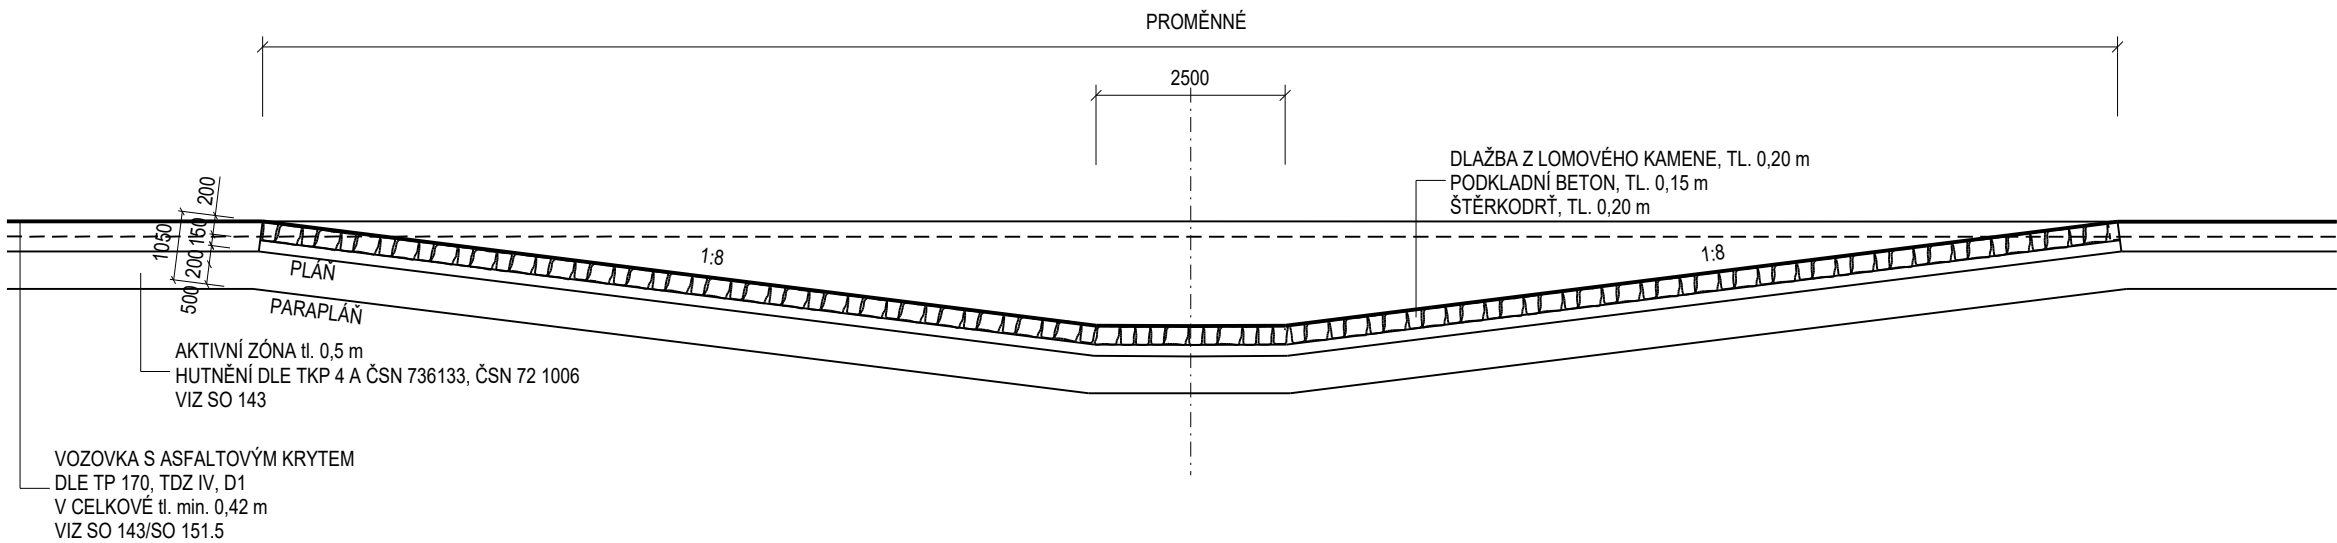

VZOROVÝ ŘEZ NEOPEVNĚNÝM KORYTEM
PLATNOST: KM ZÚ - 0,006 52
0,142 27 - KÚ

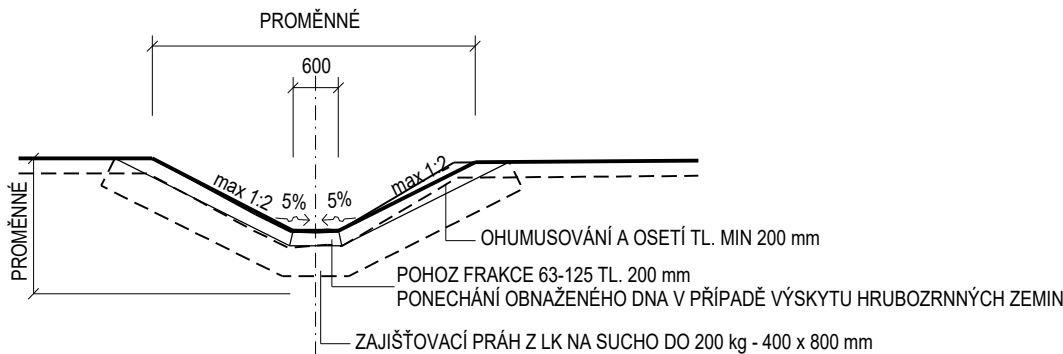

VZOROVÝ ŘEZ OPEVNĚNÝM KORYTEM
OPEVNĚNÍ - ROVNANINA Z LOMOVÉHO KAMENE
PLATNOST: KM 0,006 52 - 0,091 04

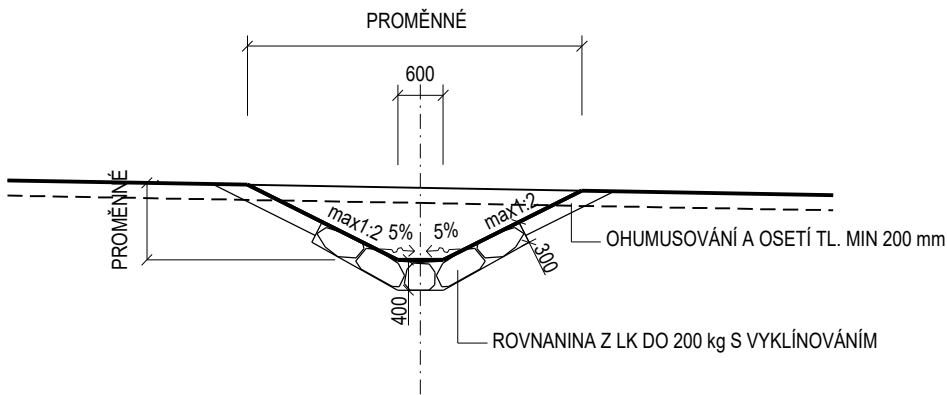

Souřadnicový systém: S-JTSK
Výškový systém: Bpv

SO 322 Úprava HOZ 2 v km 1,43

Objednatel:



ŘEDITELSTVÍ
SILNIC
A DÁLNIC

Ředitelství silnic a dálnic s. p.
Čerčanská 2023/12, Krč, 140 00 Praha 4

Zhotovitel:



Valbek

Valbek, spol. s r.o.
Vaňurova 505/17
460 07 Liberec 3

	Vypracoval	ING. J. VANCL		Zak. číslo	21-L113-001
	Zodp. projektant	ING. J. VANCL		Datum	02/2025
	Tech. kontrola	ING. D. LANDA		Stupeň	PDPS
	Akce			Počet formátů	4 x A4
Zhotovitel: Valbek, spol. s r.o. Vaňurova 505/17 460 07 Liberec 3	I/16 MLADÁ BOLESLAV - MARTINOVICE			Měřítko	1 : 100
				Č. přílohy	Paré
	Příloha	VZOROVÉ PŘÍČNÉ ŘEZY			4