
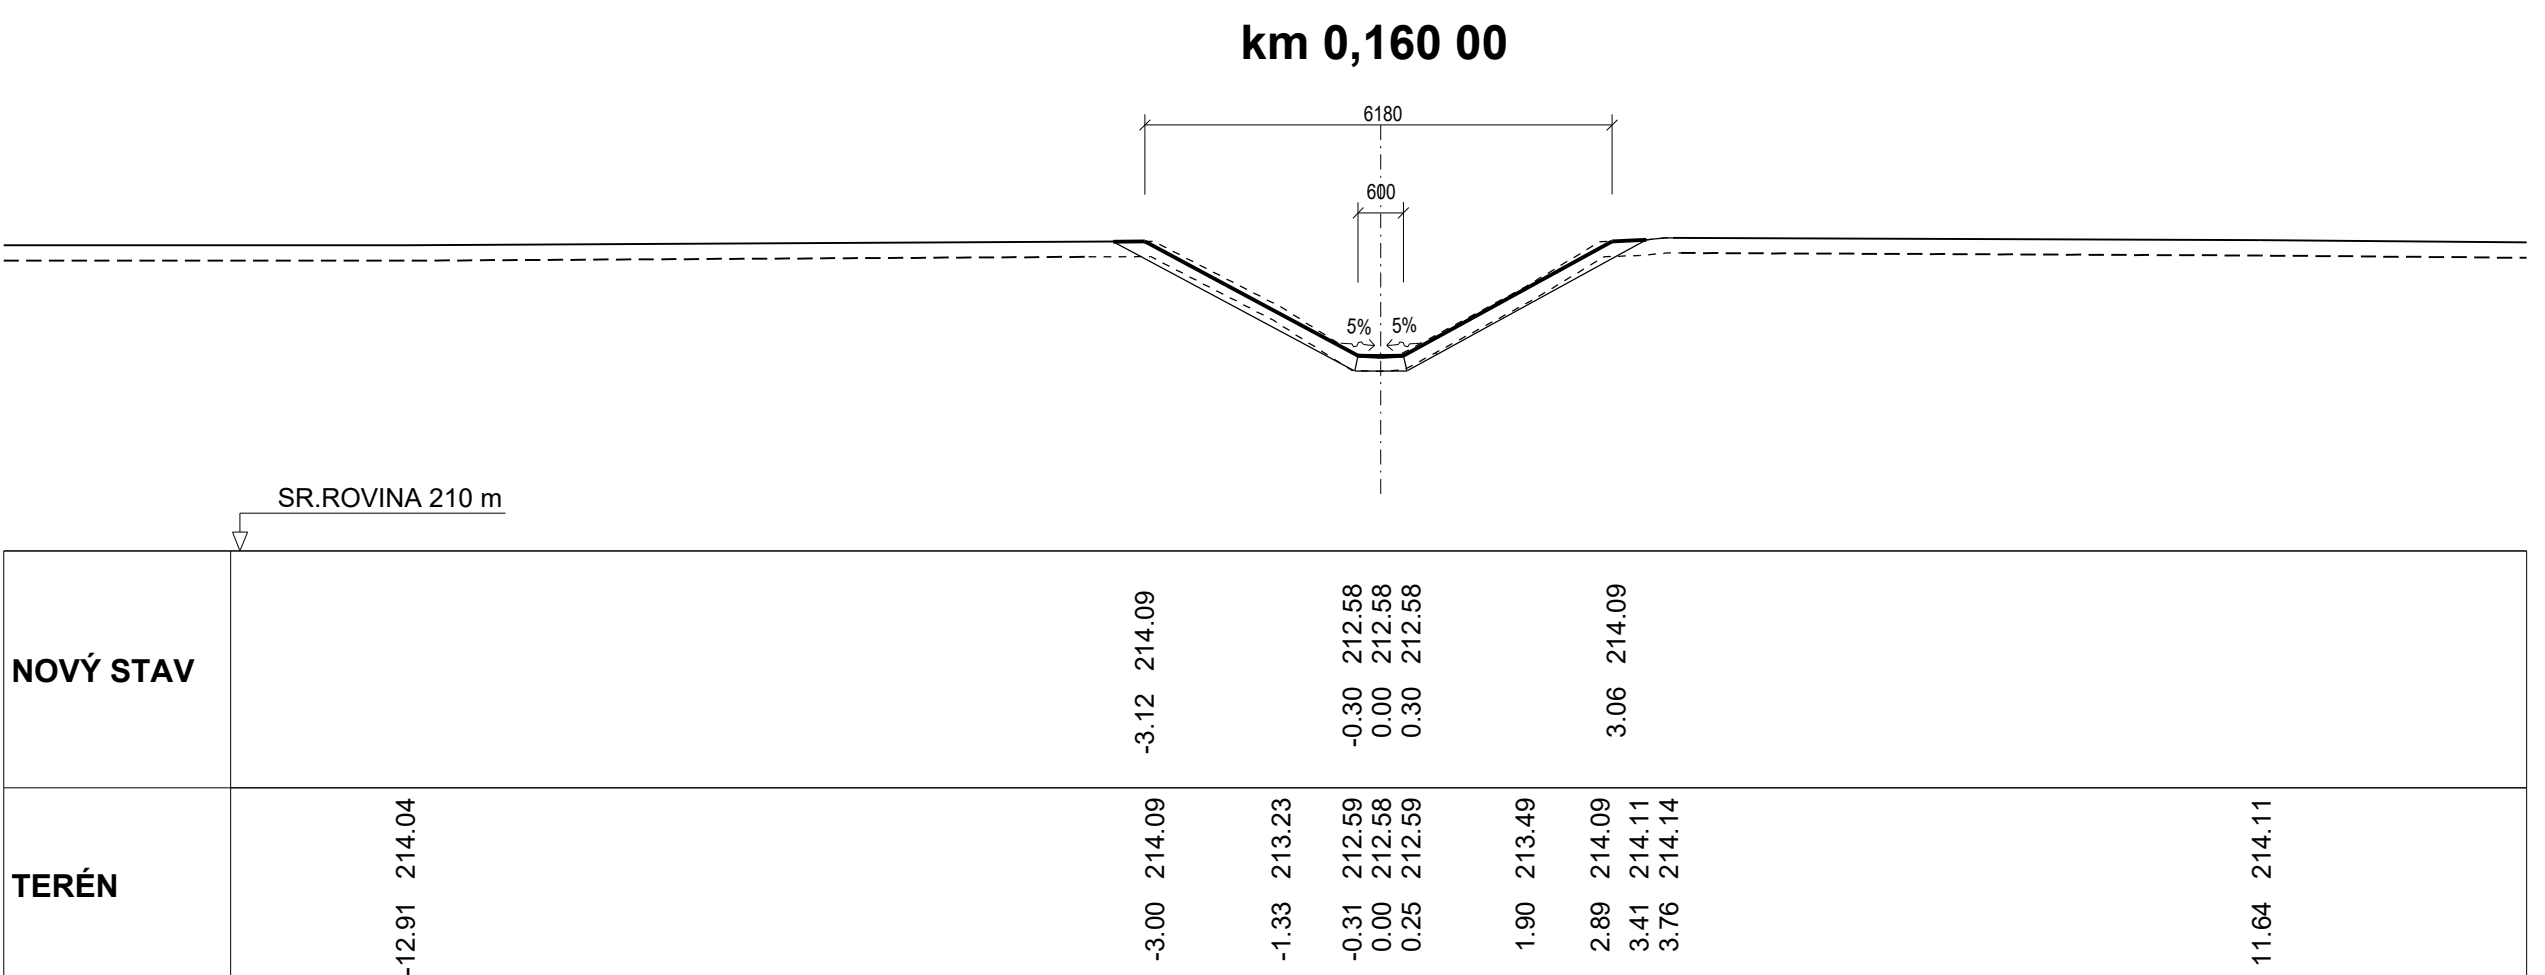
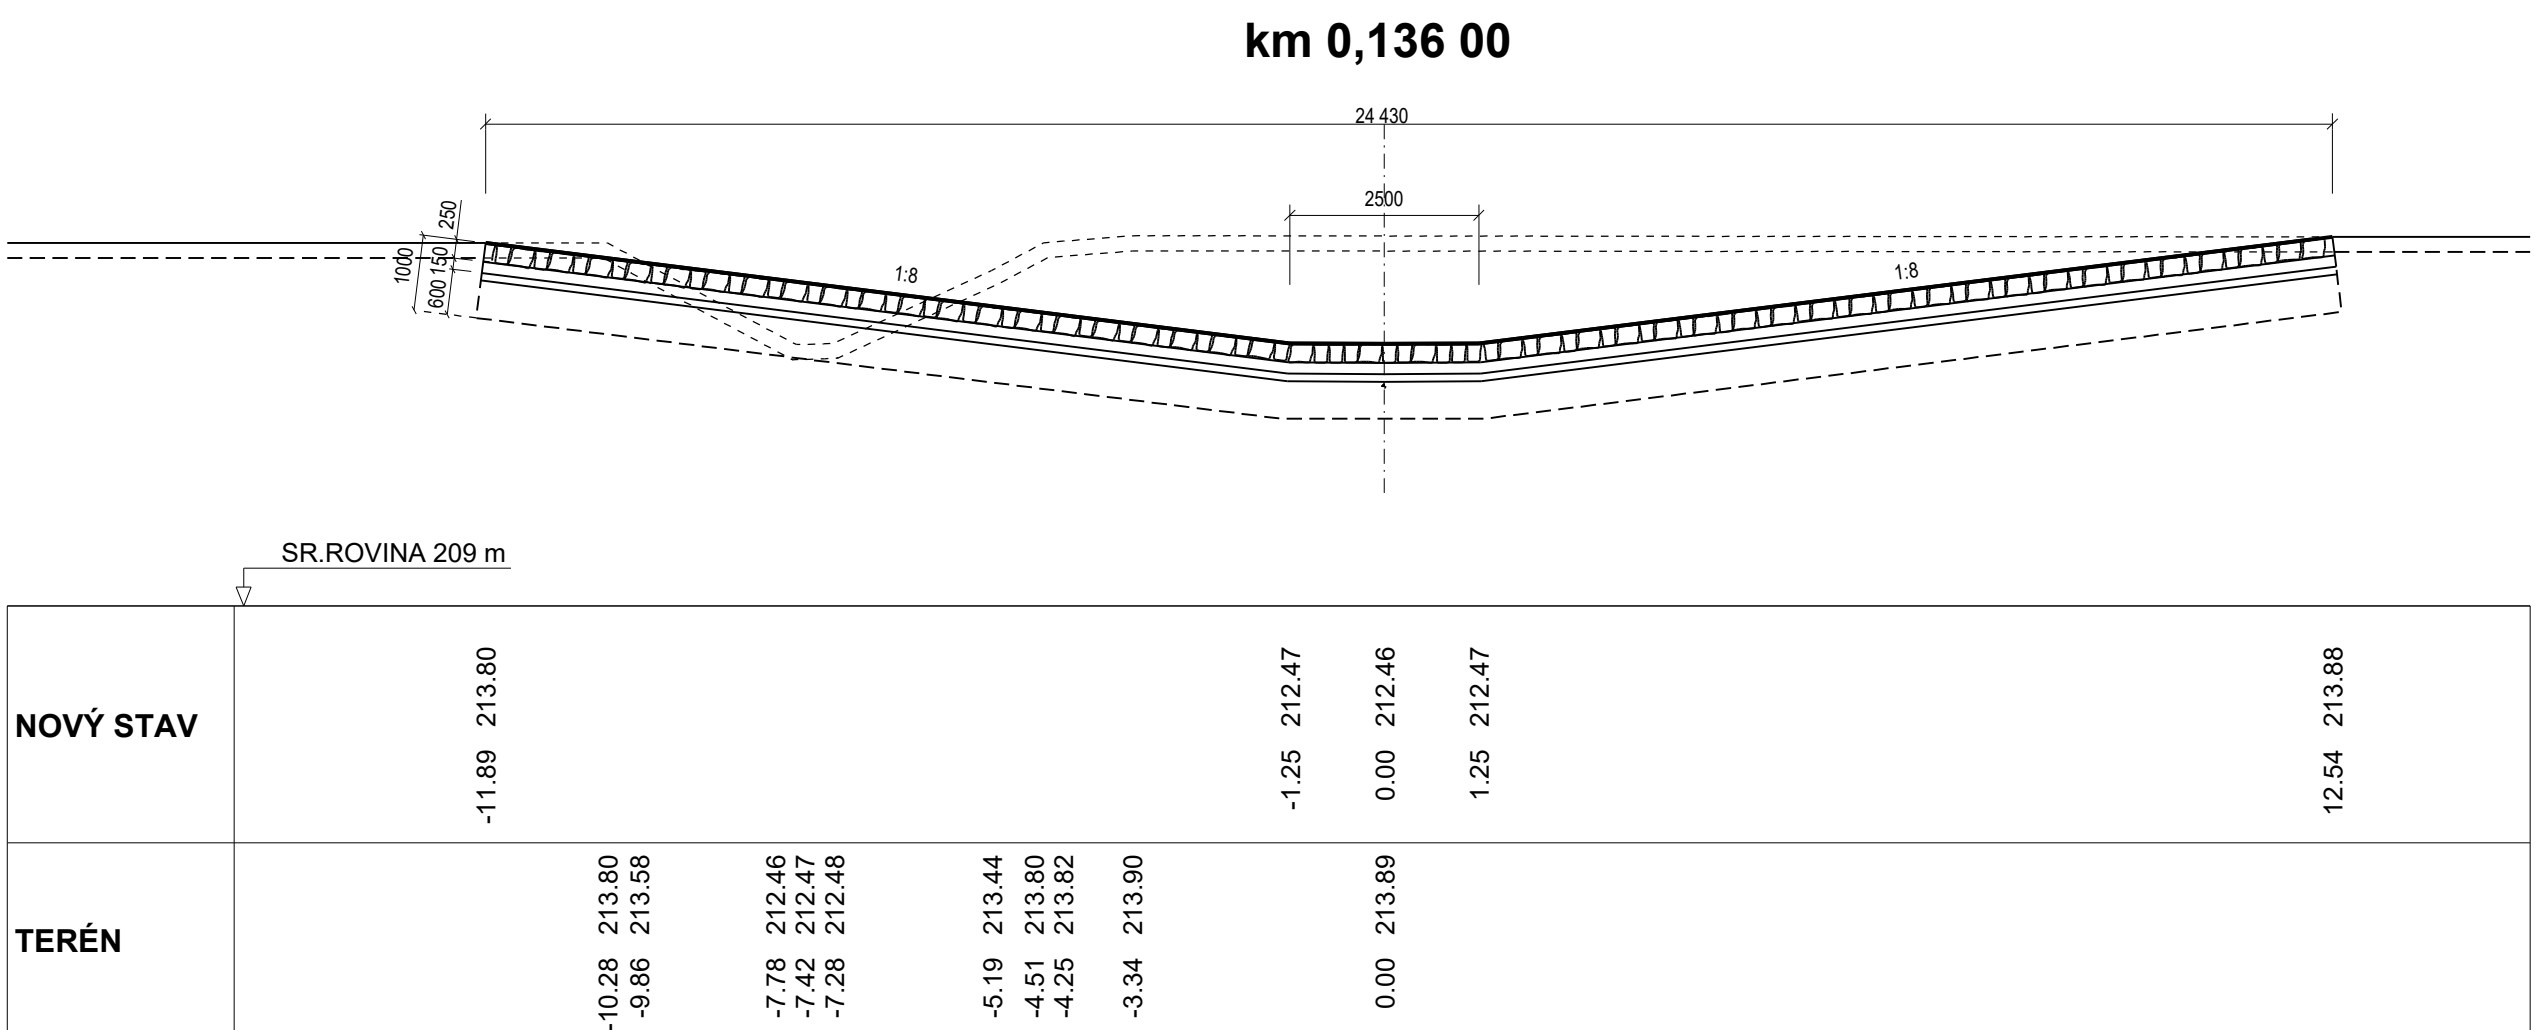


ŘEZY JSOU PROTI SMĚRU TOK

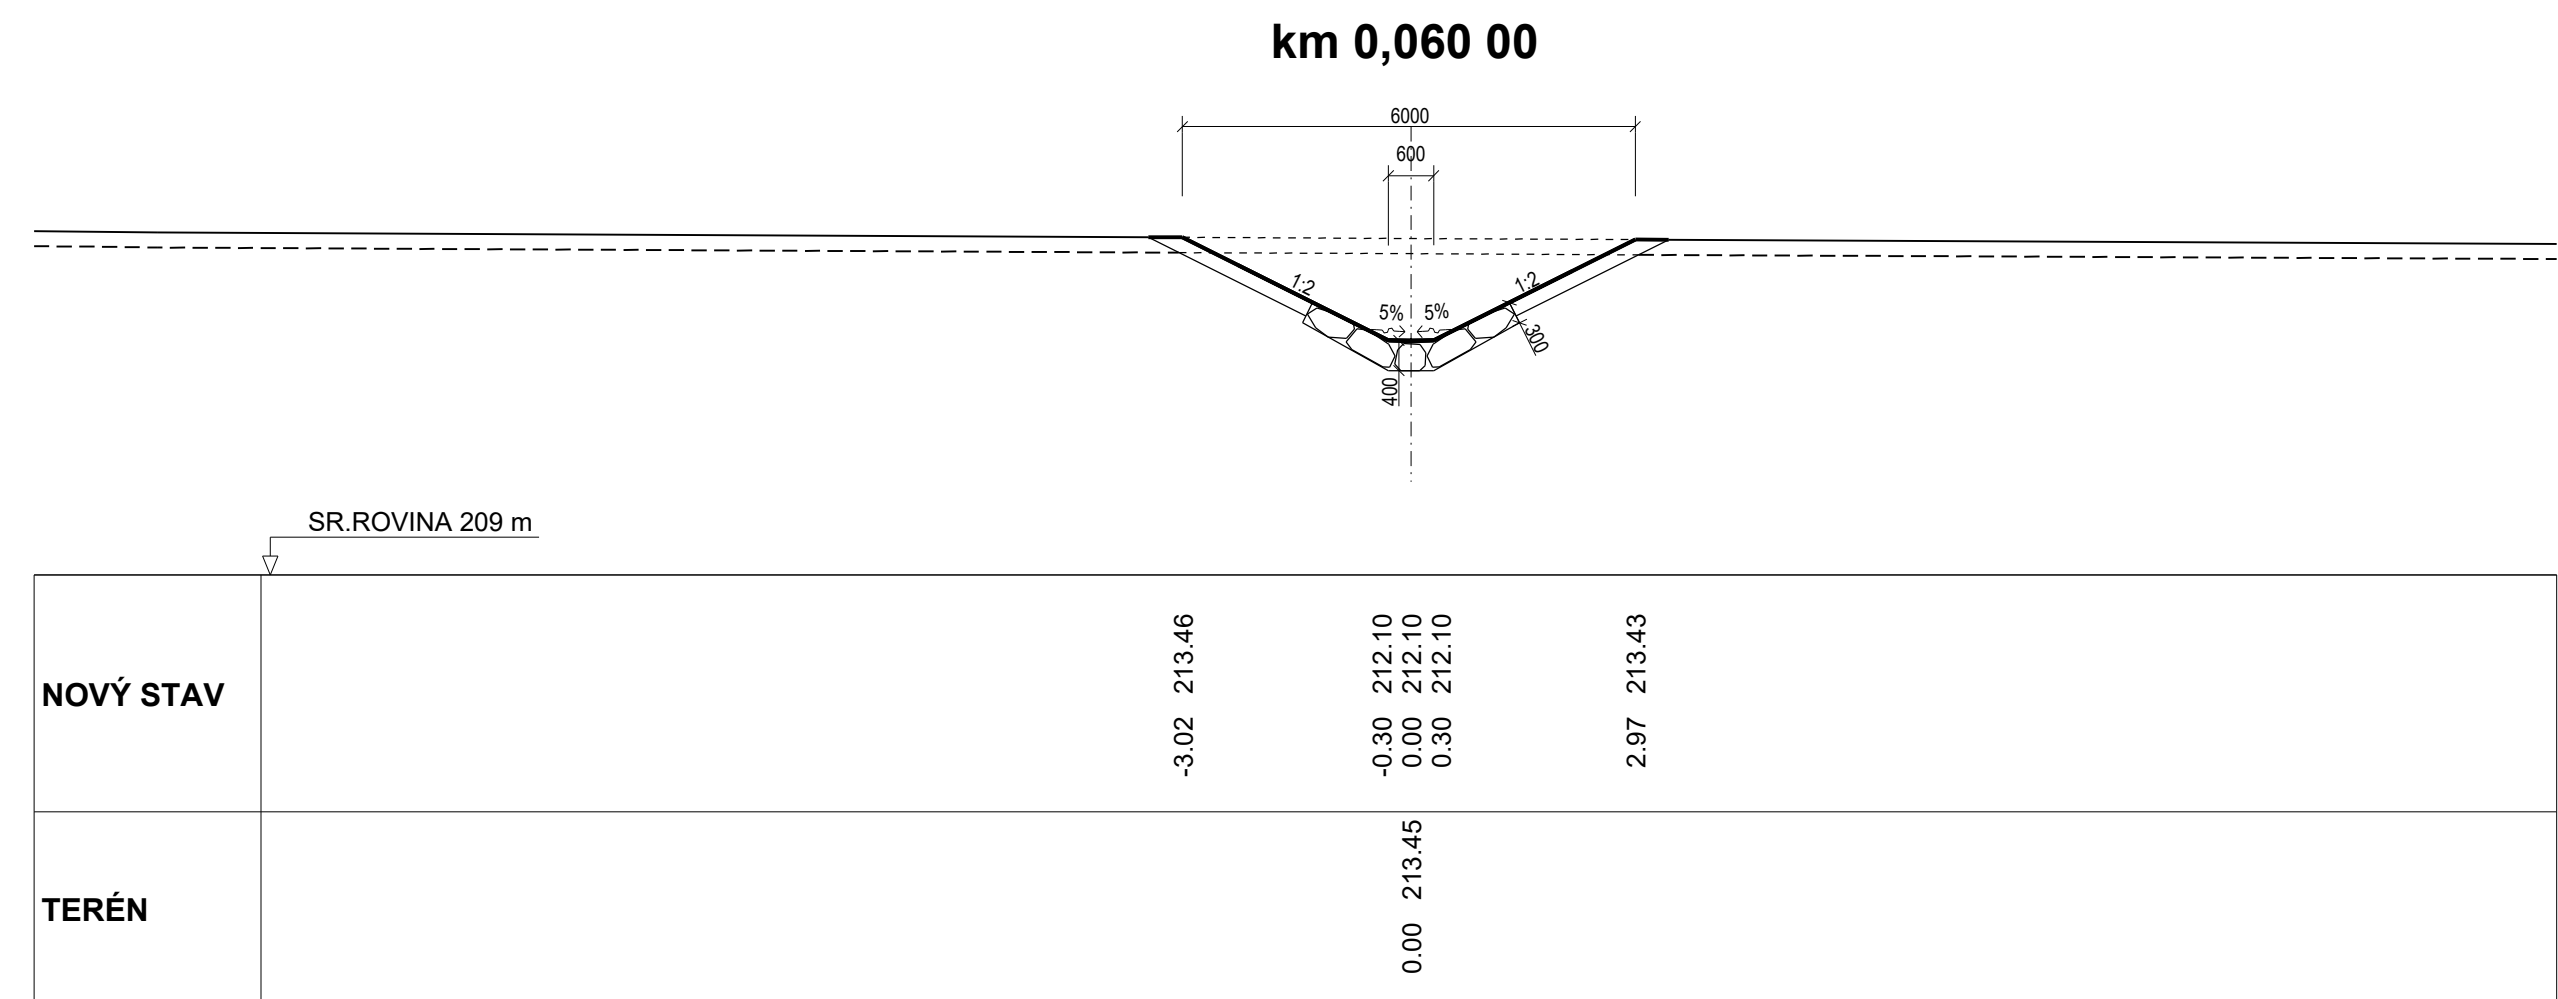

SO 322 Úprava HOZ 2 v km 1,43

Zhotovitel: 	Valbek, spol. s r.o. Vaňurova 505/17 460 07 Liberec 3
--	--

	Vypracoval	ING. J. VANCL	<i>Jancl</i>	Zak. číslo	21-LH3-001
	Zodp. projektant	ING. J. VANCL	<i>Jancl</i>	Datum	02/2025
	Tech. kontrola	ING. D. LANDA	<i>Land</i>	Stupeň	PDPŠ
	Akce	I/16 MLADÁ BOLESLAV - MARTINOVICE		Počet formátů	7 x A4
Zhotovitel: Valbek, spol. s r.o. Vahurova 505/17 460 07 Liberec 3	Příloha	PŘÍČNÉ ŘEZY		Měřitko	1 : 100
				Č. přílohy	Paré
				5	