
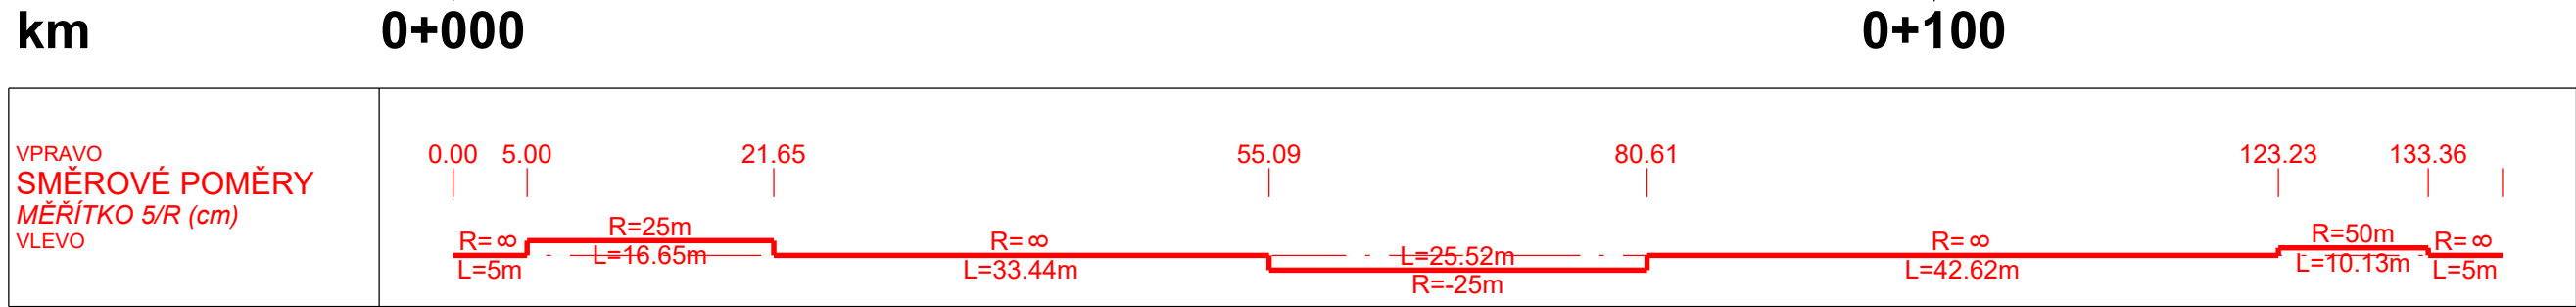


PODÉLNÝ PROFIL  
M 1:500/100

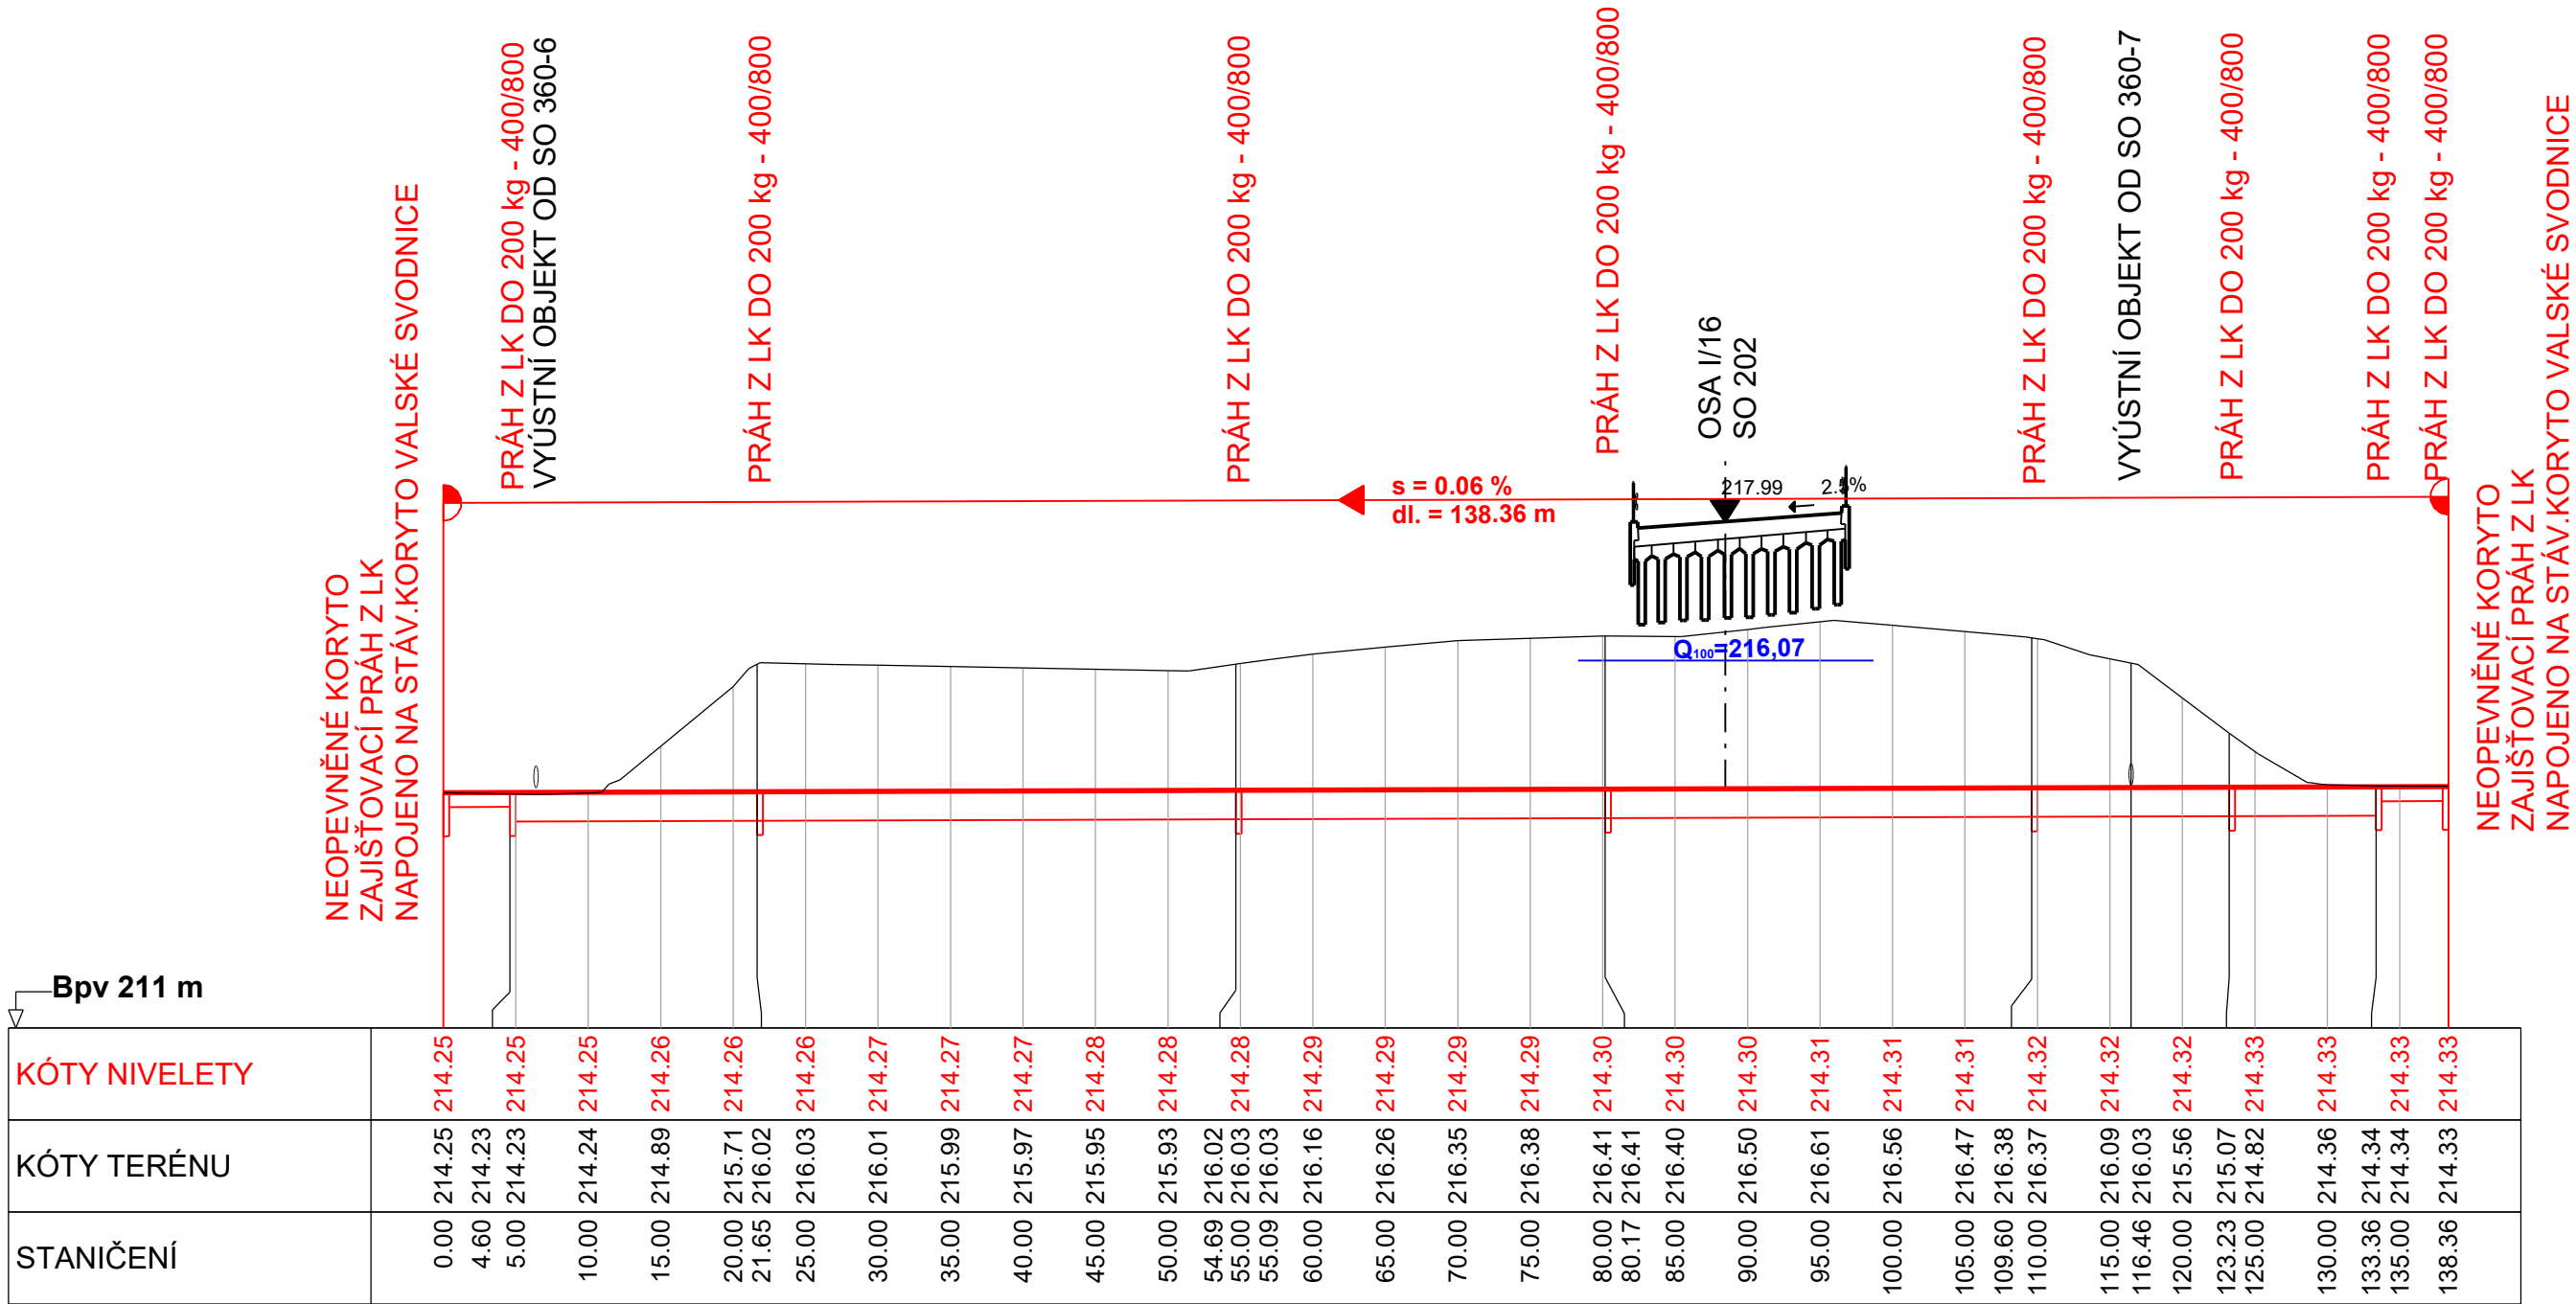

Souřadnicový systém: S-JTSK  
Výškový systém: Bpv

SO 323 Úprava Valské svodnice

Objednatel:



ŘEDITELSTVÍ  
SILNIC  
A DÁLNIC

Ředitelství silnic a dálnic s. p.  
Čerčanská 2023/12, Krč, 140 00 Praha 4

Zhotovitel:



Valbek

Valbek, spol. s r.o.  
Vaňurova 505/17  
460 07 Liberec 3

|                                                                                       |                                               |               |                                                                                       |               |             |
|---------------------------------------------------------------------------------------|-----------------------------------------------|---------------|---------------------------------------------------------------------------------------|---------------|-------------|
|  | Vypracoval                                    | ING. J. VANCL |  | Zak. číslo    | 21-LI13-001 |
|                                                                                       | Zodp. projektant                              | ING. J. VANCL |  | Datum         | 02/2025     |
|                                                                                       | Tech. kontrola                                | ING. D. LANDA |  | Stupeň        | PDPS        |
|                                                                                       | Akce<br><br>I/16 MLADÁ BOLESLAV - MARTINOVICE |               |                                                                                       | Počet formátů | 3 x A4      |
|                                                                                       |                                               |               |                                                                                       | Měřítko       | 1 : 500/100 |
| Zhotovitel:<br>Valbek, spol. s r.o.<br>Vaňurova 505/17<br>460 07 Liberec 3            | Příloha<br><br>PODÉLNÝ PROFIL                 |               |                                                                                       | 3             | Paré        |