

VZOROVÉ PŘÍČNÉ ŘEZY
M 1:50

VZOROVÝ ŘEZ NEOPEVNĚNÝM KORYTEM


PLATNOST: KM ZÚ - 0,004 60
0,133 36 - KÚ

VZOROVÝ ŘEZ OPEVNĚNÝM KORYTEM
OPEVNĚNÍ - ROVNANINA Z LOMOVÉHO KAMENE

PLATNOST: KM 0,004 60 - 0,055 09
0,123 63 - 0,133 36

VZOROVÝ ŘEZ OPEVNĚNÝM KORYTEM S BERMOU
OPEVNĚNÍ - ROVNANINA Z LOMOVÉHO KAMENE

PLATNOST: KM 0,055 09 - 0,109 60

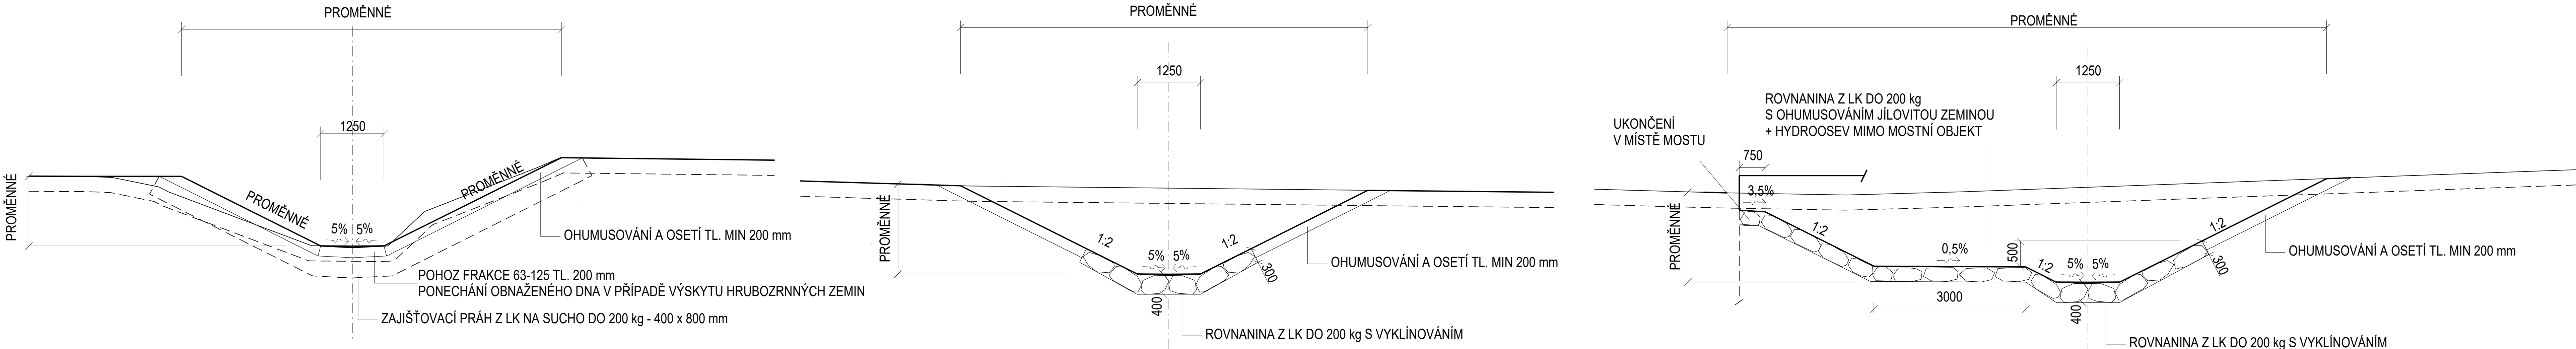

Souřadnicový systém: S-JTSK
Výškový systém: Bpv

SO 323 Úprava Valské svodnice

Objednatel:



Ředitelství silnic a dálnic s. p.
Čerčanská 2023/12, Krč, 140 00 Praha 4

Zhotovitel:



Valbek, spol. s r.o.
Vaňurova 505/17
460 07 Liberec 3

	Vypracoval	ING. J. VANCL		Zak. číslo	21-LI13-001
	Zodp. projektant	ING. J. VANCL		Datum	02/2025
	Tech. kontrola	ING. D. LANDA		Stupeň	PDPS
	Akce I/16 MLADÁ BOLESLAV - MARTINOVICE			Počet formátů	6 x A4
				Měřítko	1 : 50
Zhotovitel: Valbek, spol. s r.o. Vaňurova 505/17 460 07 Liberec 3	Příloha	VZOROVÉ PŘÍČNÉ ŘEZY			Č. přílohy 4