



PŘÍČNÉ ŘEZY
M 1:100


ŘEZY JSOU PROTI SMĚRU TOKU

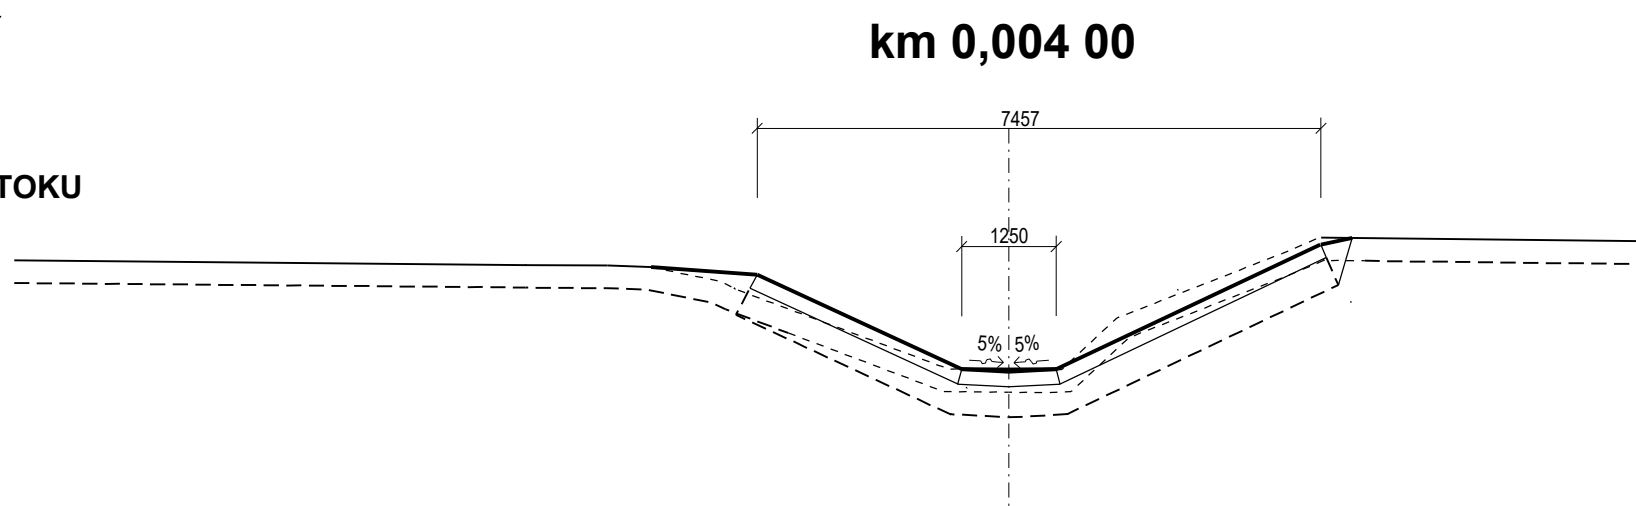


SR.ROVINA 211 m	
NOVÝ STAV	
TERÉN	
	-6.39 215.63
	-5.31 215.62
	-4.73 215.60
	-3.81 215.42
	-3.62 215.32
	-0.80 214.26
	0.00 214.25
	0.53 214.24
	0.70 214.25
	1.43 214.93
	3.62 215.79
	4.09 215.99
	4.13 215.99
	8.34 215.95

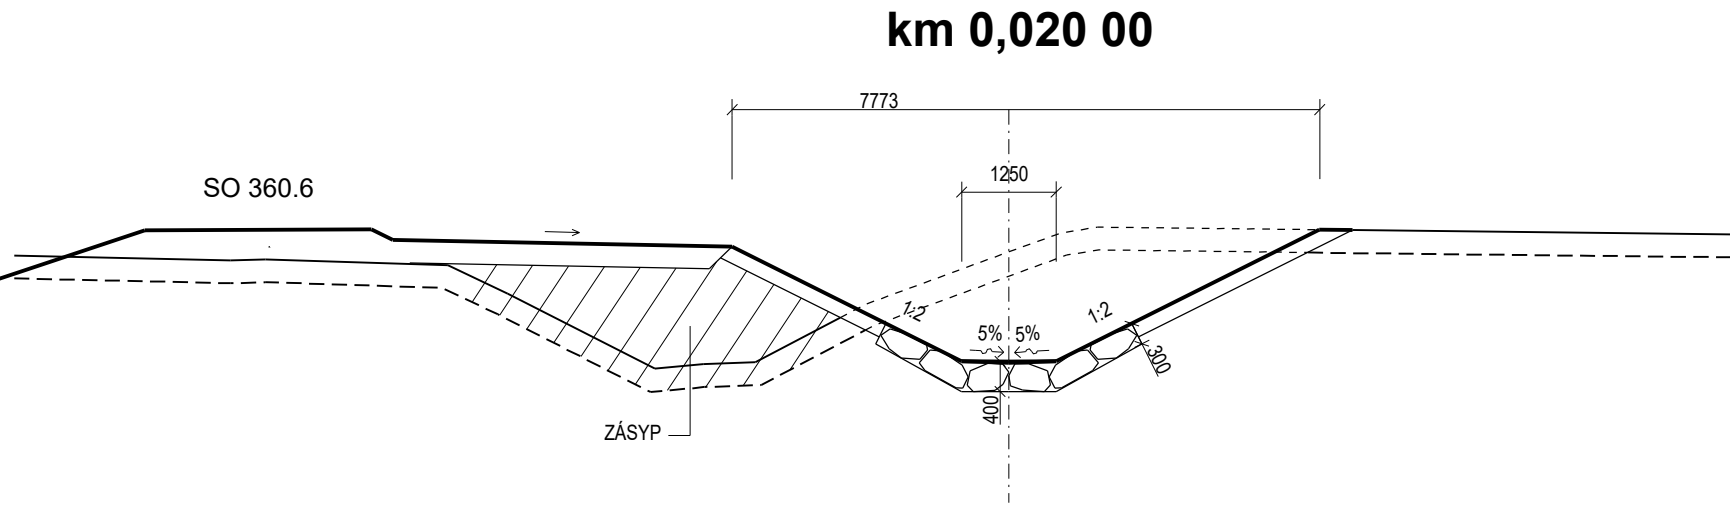


SR.ROVINA 211 m	
NOVÝ STAV	
TERÉN	
	-9.83 215.61
	-7.42 215.53
	-6.63 215.16
	-4.68 214.17
	-4.05 214.22
	-3.35 214.25
	-1.91 215.01
	0.00 215.71
	0.68 215.96
	1.17 216.04
	4.11 216.00

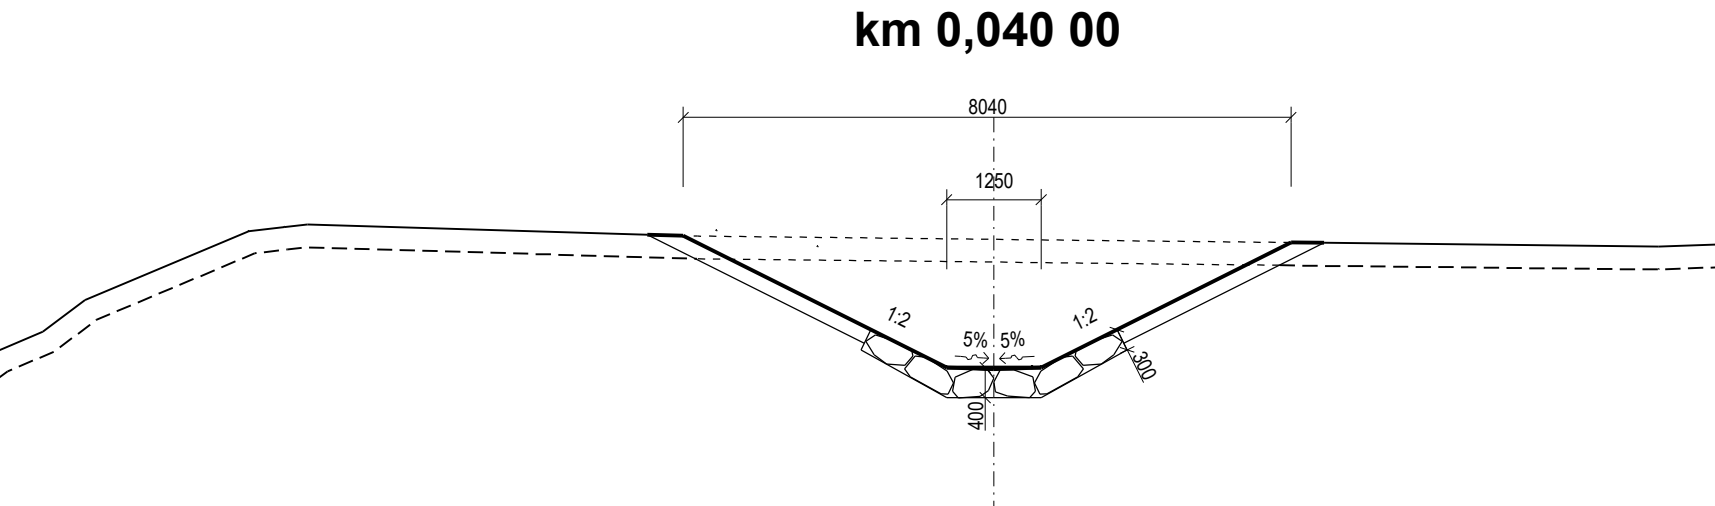


SR.ROVINA 211 m	
NOVÝ STAV	
TERÉN	
	-9.86 216.08
	-9.38 216.13
	-9.08 216.17
	-3.92 216.01
	-4.11 216.02
	-0.63 214.28
	0.00 214.27
	0.63 214.28
	3.93 215.93
	8.79 215.88

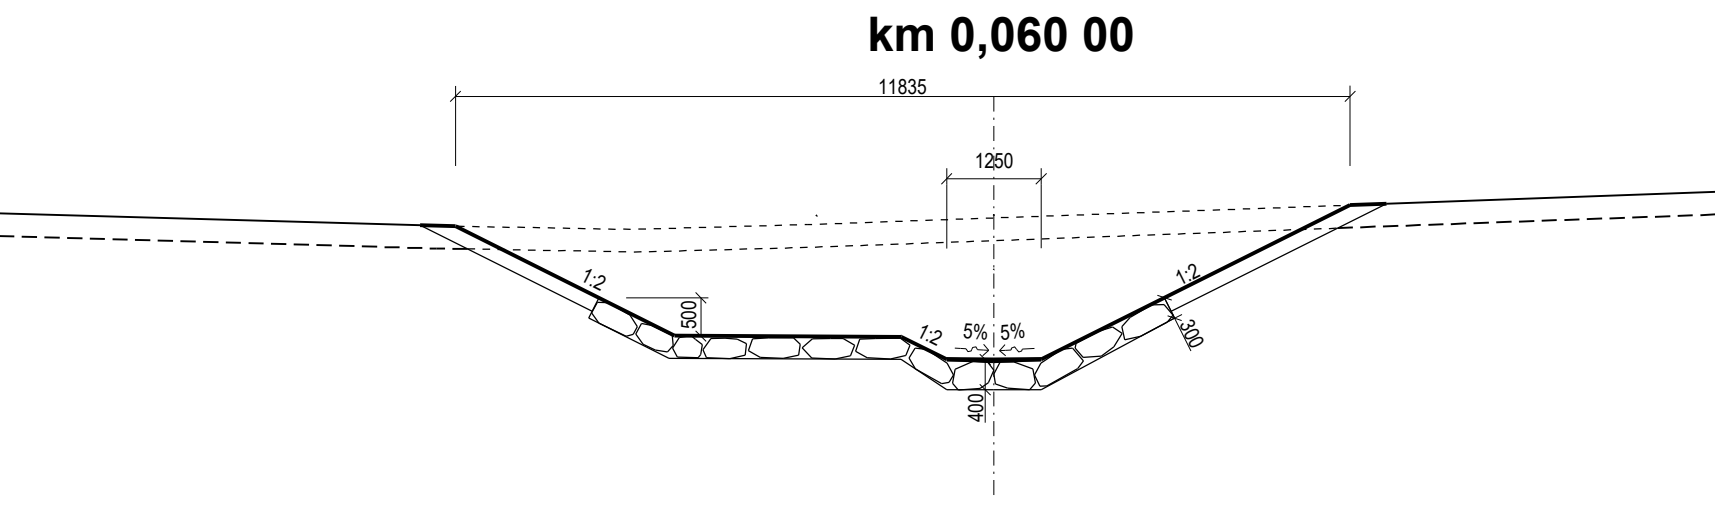

SR.ROVINA 211 m	
NOVÝ STAV	
TERÉN	
	-7.37 216.06
	-7.12 216.05
	-4.23 214.60
	-1.23 214.59
	-0.63 214.29
	0.00 214.29
	0.63 214.29
	3.63 215.79
	4.71 216.33

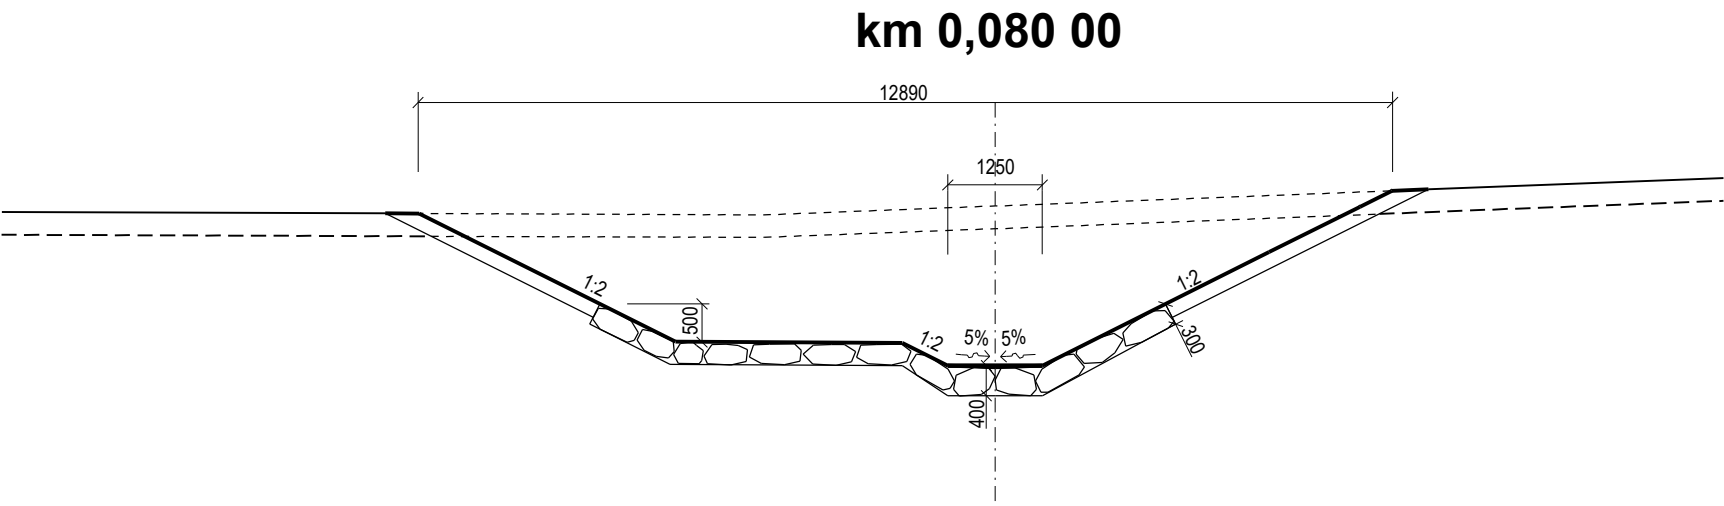

SR.ROVINA 211 m	
NOVÝ STAV	
TERÉN	
	-7.62 216.31
	-4.23 214.62
	-1.23 214.60
	-0.63 214.30
	0.00 214.30
	0.63 214.30
	3.63 215.80
	5.25 216.61

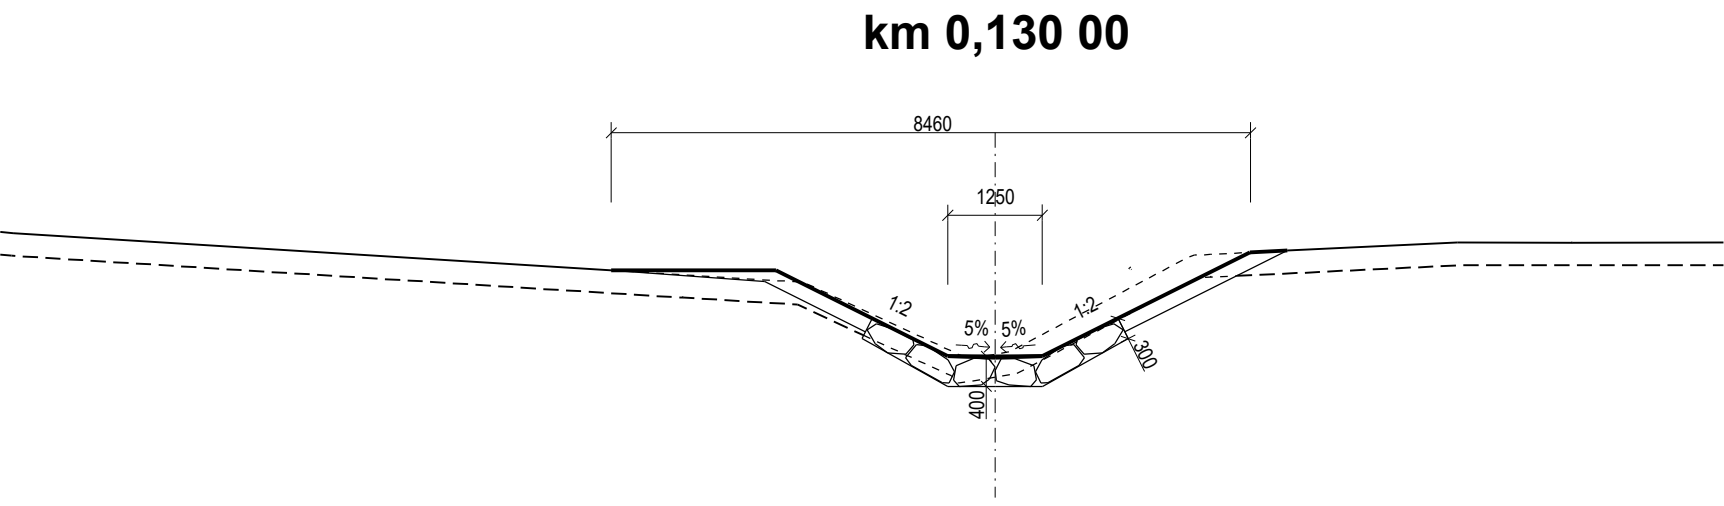

SR.ROVINA 211 m	
NOVÝ STAV	
TERÉN	
	-5.08 215.47
	-2.90 215.47
	-0.63 214.33
	0.00 214.33
	0.63 214.33
	3.37 215.70
	-4.11 215.41
	-2.54 215.31
	-0.40 214.32
	-0.38 214.30
	0.00 214.36
	0.17 214.39
	0.19 214.39
	2.54 215.63
	2.64 215.67
	2.85 215.68
	6.11 215.83
	7.63 215.83

Souřadnicový systém: S-JTSK
Výškový systém: Bpv

SO 323 Úprava Valské svodnice

Objednatel:



Ředitelství silnic a dálnic s. p.
Čerčanská 2023/12, Krč, 140 00 Praha 4

Zhotovitel:



Valbek, spol. s r.o.
Vaňurova 505/17
460 07 Liberec 3



Zhotovitel:
Valbek, spol. s r.o.
Vaňurova 505/17
460 07 Liberec 3

Vypracoval
Zodp. projektant
Tech. kontrola
Akce

ING. J. VANCL
ING. J. VANCL
ING. D. LANDA

I/16 MLADÁ BOLESLAV - MARTINOVICE

Příloha

PŘÍČNÉ ŘEZY

Zak. číslo
Datum
Stupeň
Počet formátů
Měřítko
Č. přílohy

21-L113-001
02/2025
PDPS
5 x A4
1 : 100
Paré

5