


PODÉLNÝ PROFIL
M 1:500/100

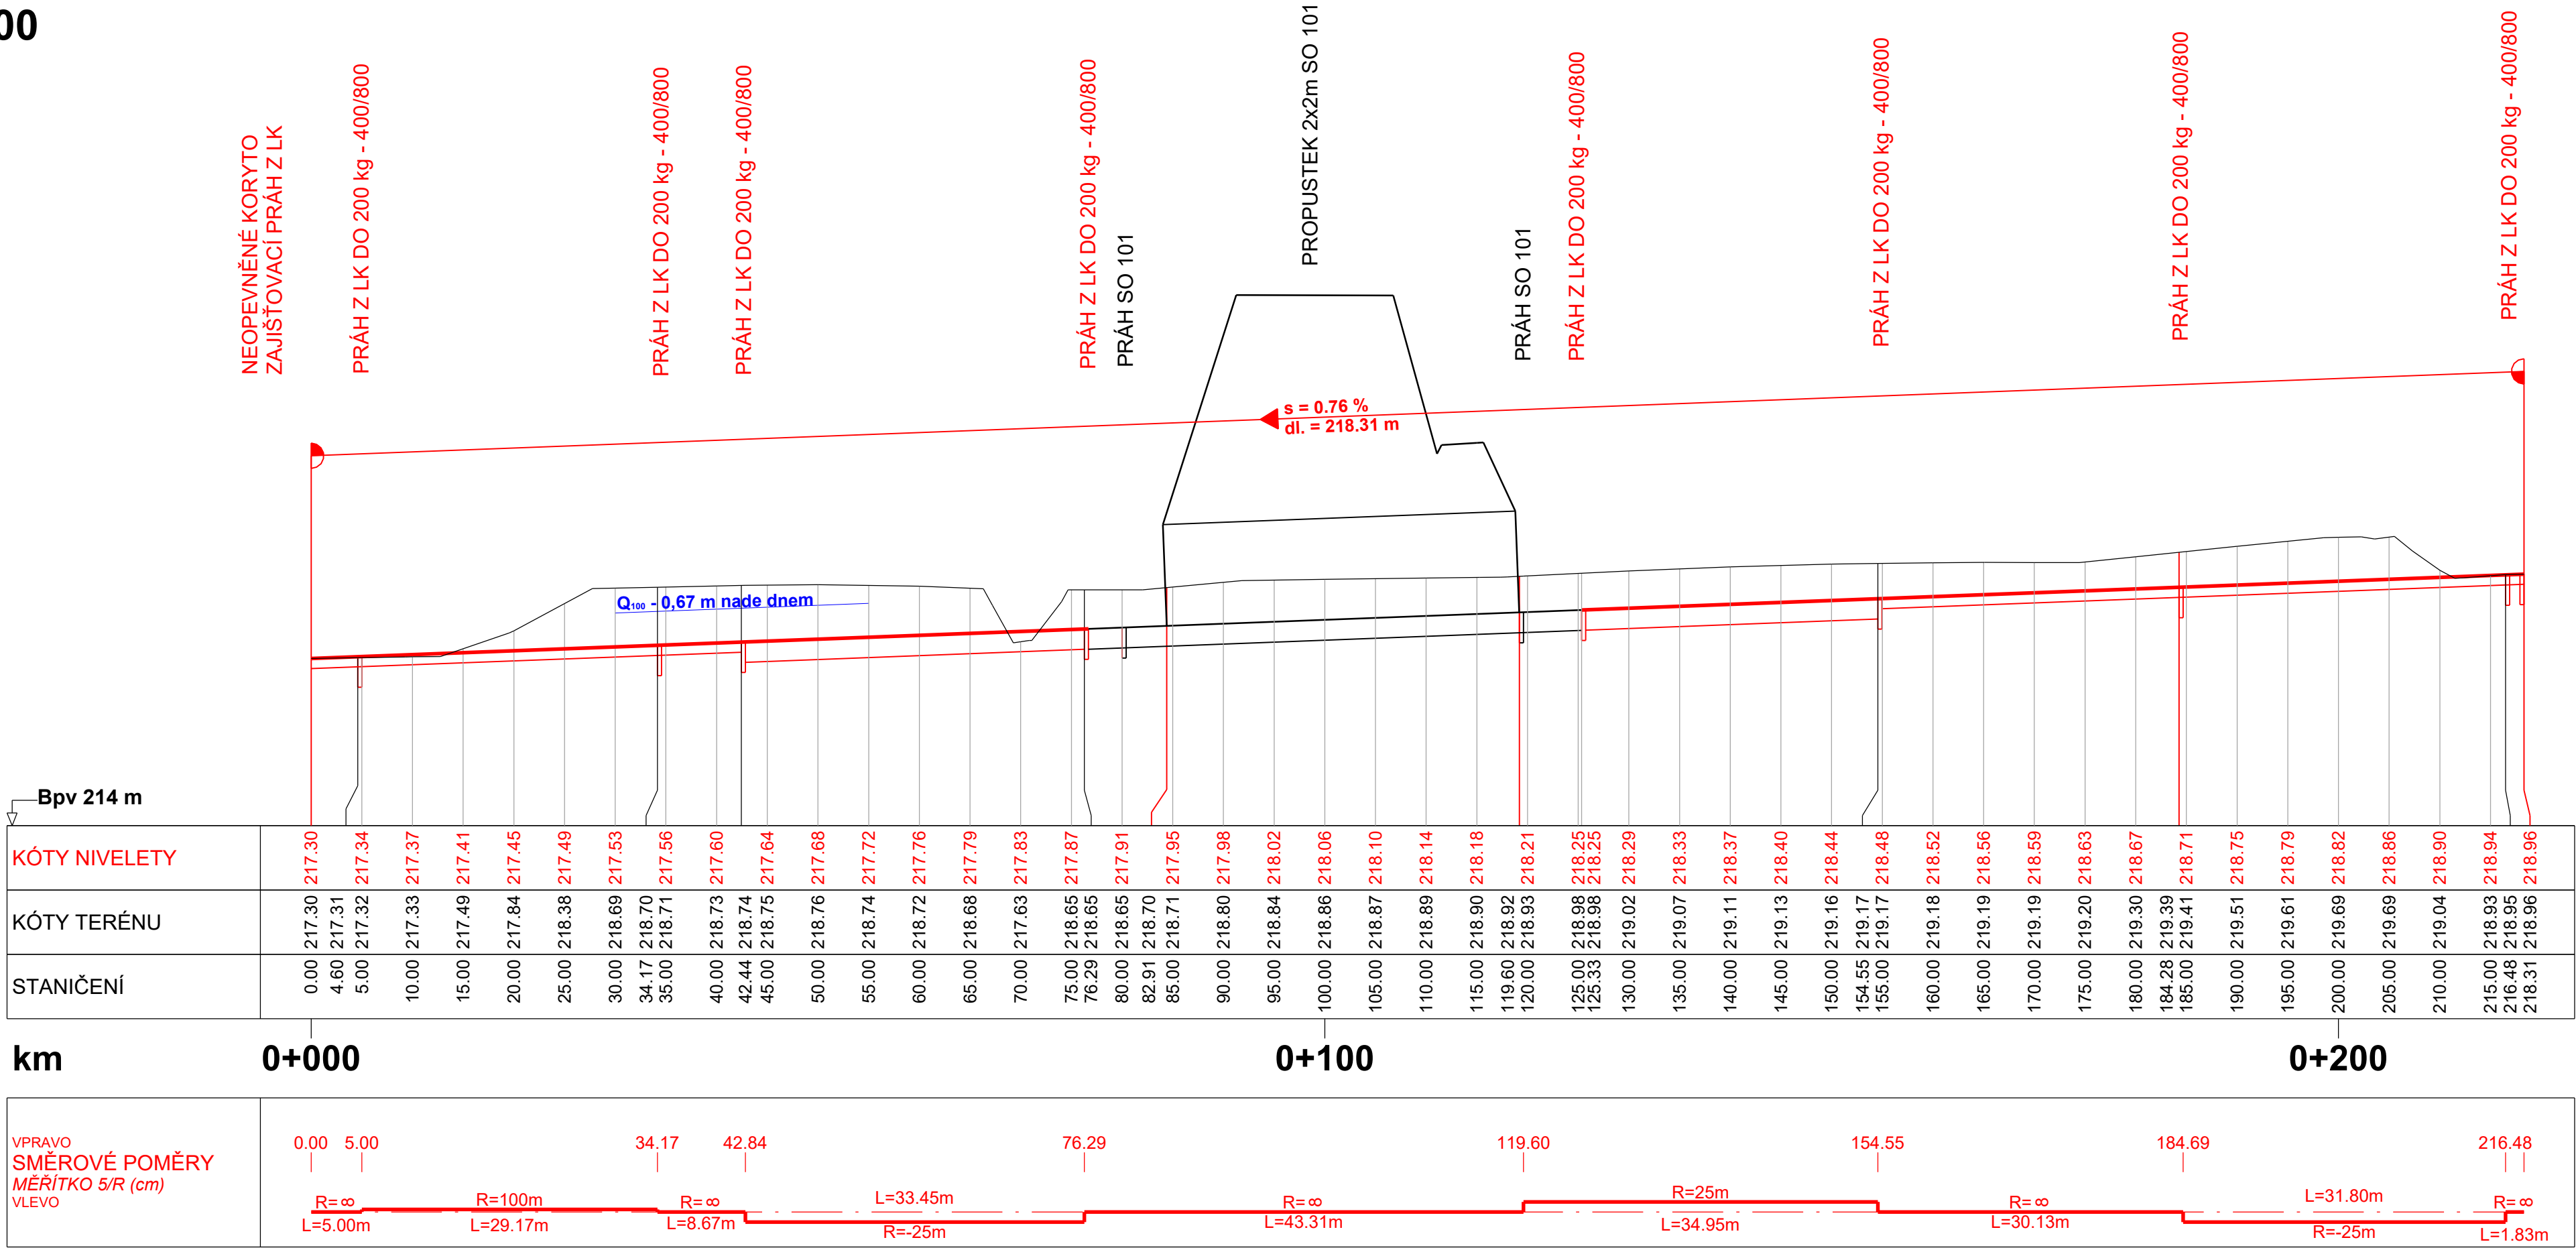

Souřadnicový systém: S-JTSK
Výškový systém: Bpv

SO 324 Úprava HOZ 3 v km 3,96

Objednatel:



ŘEDITELSTVÍ
SILNIC
A DÁLNIC

Ředitelství silnic a dálnic s. p.
Čerčanská 2023/12, Krč, 140 00 Praha 4

Zhotovitel:



Valbek, spol. s r.o.
Vaňurova 505/17
460 07 Liberec 3



Vypracoval	ING. J. VANCL		Zak. číslo	21-L113-001
Zodp. projektant	ING. J. VANCL		Datum	02/2025
Tech. kontrola	ING. D. LANDA		Stupeň	PDPS
Akce I/16 MLADÁ BOLESLAV - MARTINOVICE			Počet formátů	4 x A4
			Měřítka	1 : 500/100
			Č. přílohy	Paré
Zhotovitel: Valbek, spol. s r.o. Vaňurova 505/17 460 07 Liberec 3			Příloha	PODÉLNÝ PROFIL
				3