
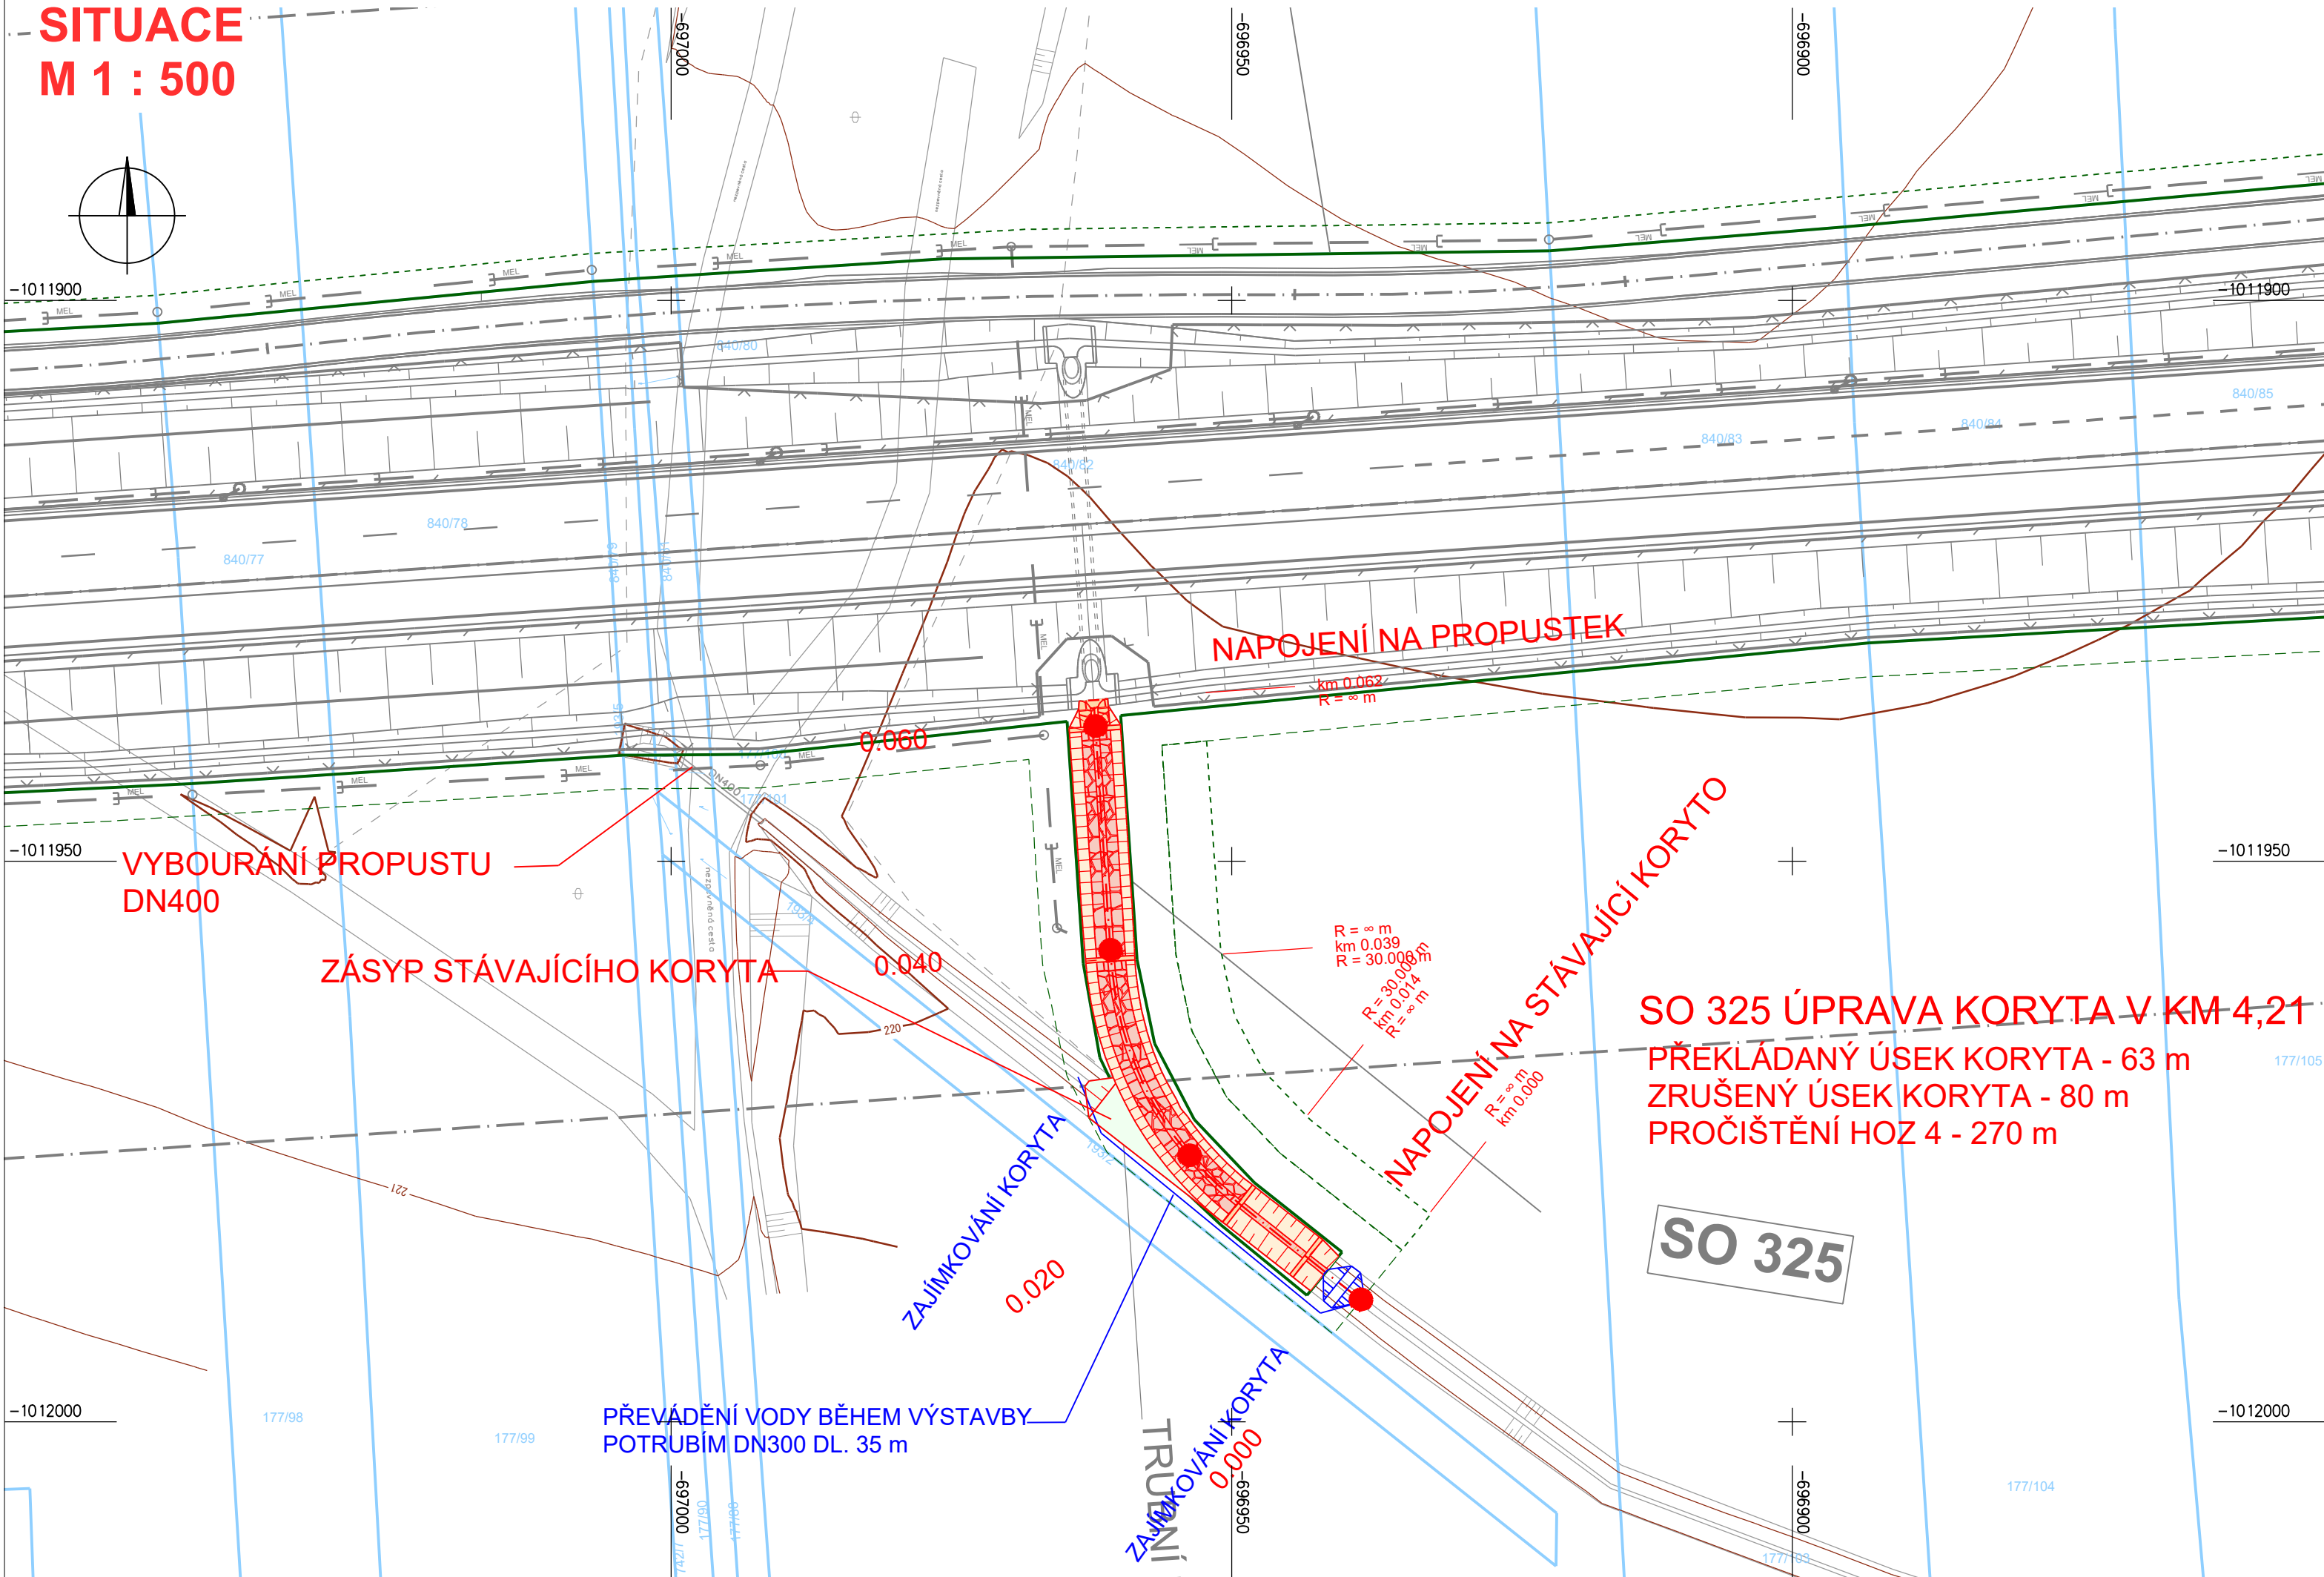


SITUACE
M 1 : 500

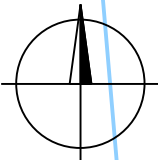

LEGENDA:

PLOCHY

- OHUMUSOVÁNÍ VÝKOP
- OHUMUSOVÁNÍ NÁSYP
- DLAŽBA Z LK DO BETONU
- POHOZ KAMENIVEM
- ROVNANINA Z LK
- ROVNANINA Z LK S OHUMUSOVÁNÍM
- PRÁH BETONOVÝ
- PRÁH Z LK NA CM
- BETONOVÉ KONSTRUKCE
- ŽB KONSTRUKCE
- SANACE STÁVAJÍCÍHO KORYTA

Souřadnicový systém: S-JTSK
Výškový systém: Bpv

SO 325 Úprava koryta v km 4,21

Objednatel:



ŘEDITELSTVÍ
SILNIC
A DÁLNIC

Ředitelství silnic a dálnic s. p.
Čerčanská 2023/12, Krč, 140 00 Praha 4

Zhotovitel:



Valbek, spol. s r.o.
Vaňurova 505/17
460 07 Liberec 3



Vypracoval
Zodp. projektant
Tech. kontrola

ING. J. VANCL
ING. J. VANCL
ING. D. LANDA

Akce
I/16 MLADÁ BOLESLAV - MARTINOVICE

Příloha
SITUACE Č. 1

Zak. číslo
Datum
Stupeň
Počet formátů
Měřítko
Č. přílohy

21-LI13-001
02/2025
PDPS
3 x A4
1 : 500
Paré

2.1

Zhotovitel:
Valbek, spol. s r.o.
Vaňurova 505/17
460 07 Liberec 3