


VZOROVÉ PŘÍČNÉ ŘEZY
M 1:50


VZOROVÝ ŘEZ NEOPEVNĚNÝM KORYTEM

PLATNOST: KM 0,013 96 - KÚ

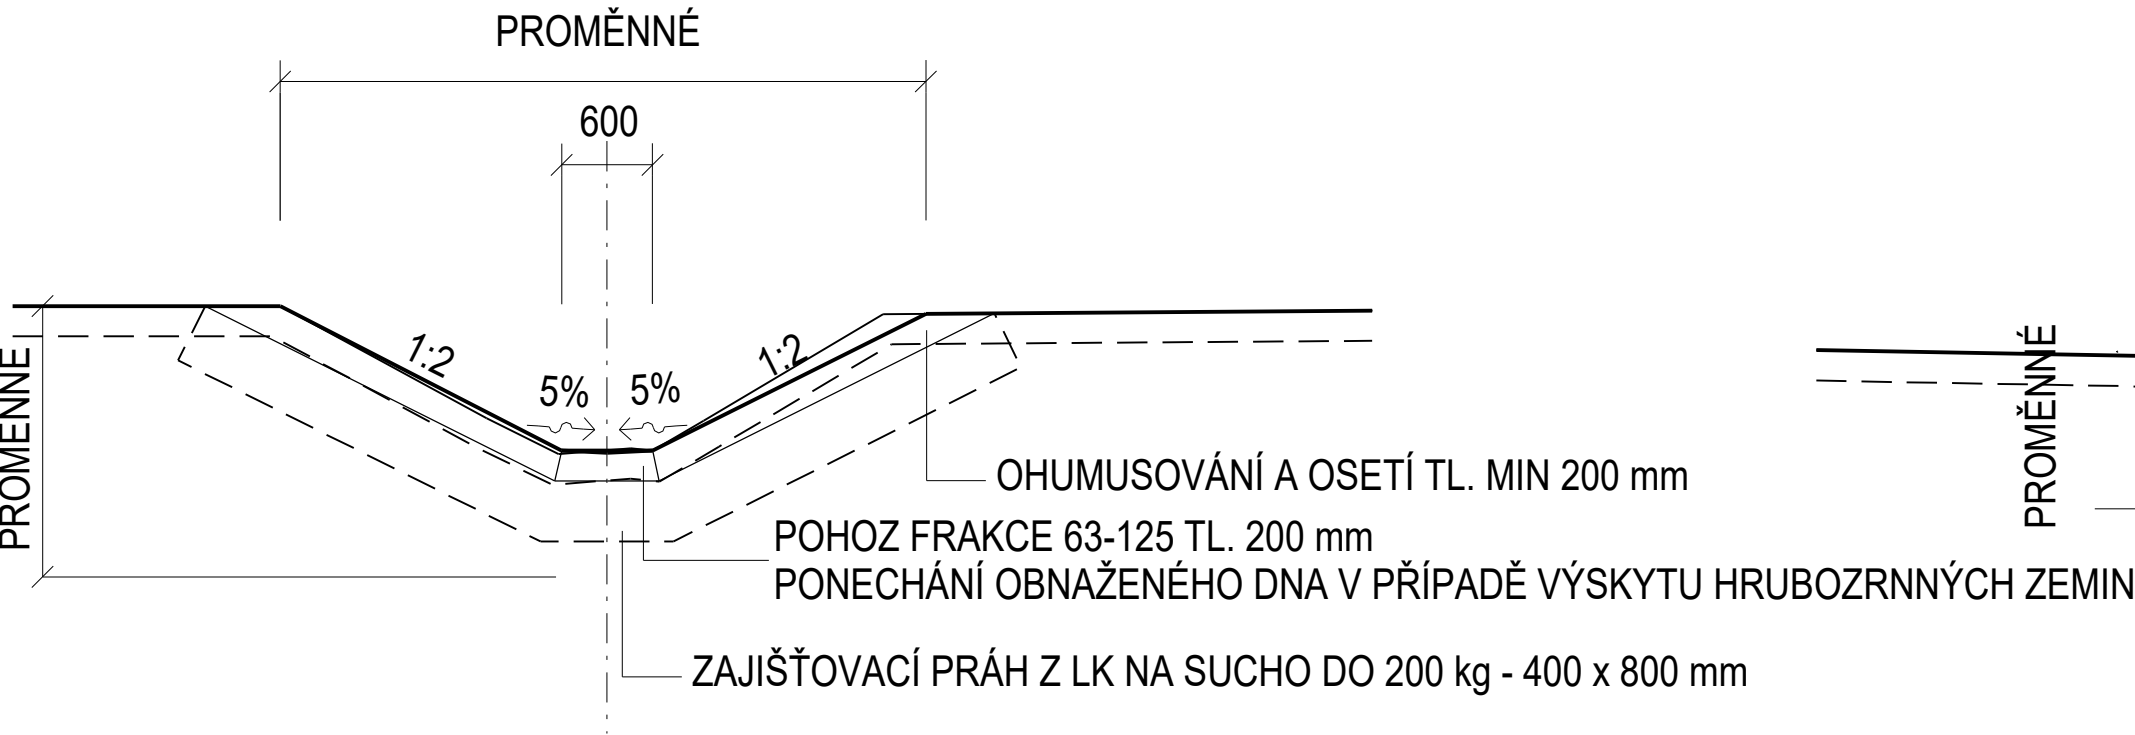

VZOROVÝ ŘEZ OPEVNĚNÝM KORYTEM
OPEVNĚNÍ - ROVNANINA Z LOMOVÉHO KAMENE

PLATNOST: KM ZÚ - 0,013 96

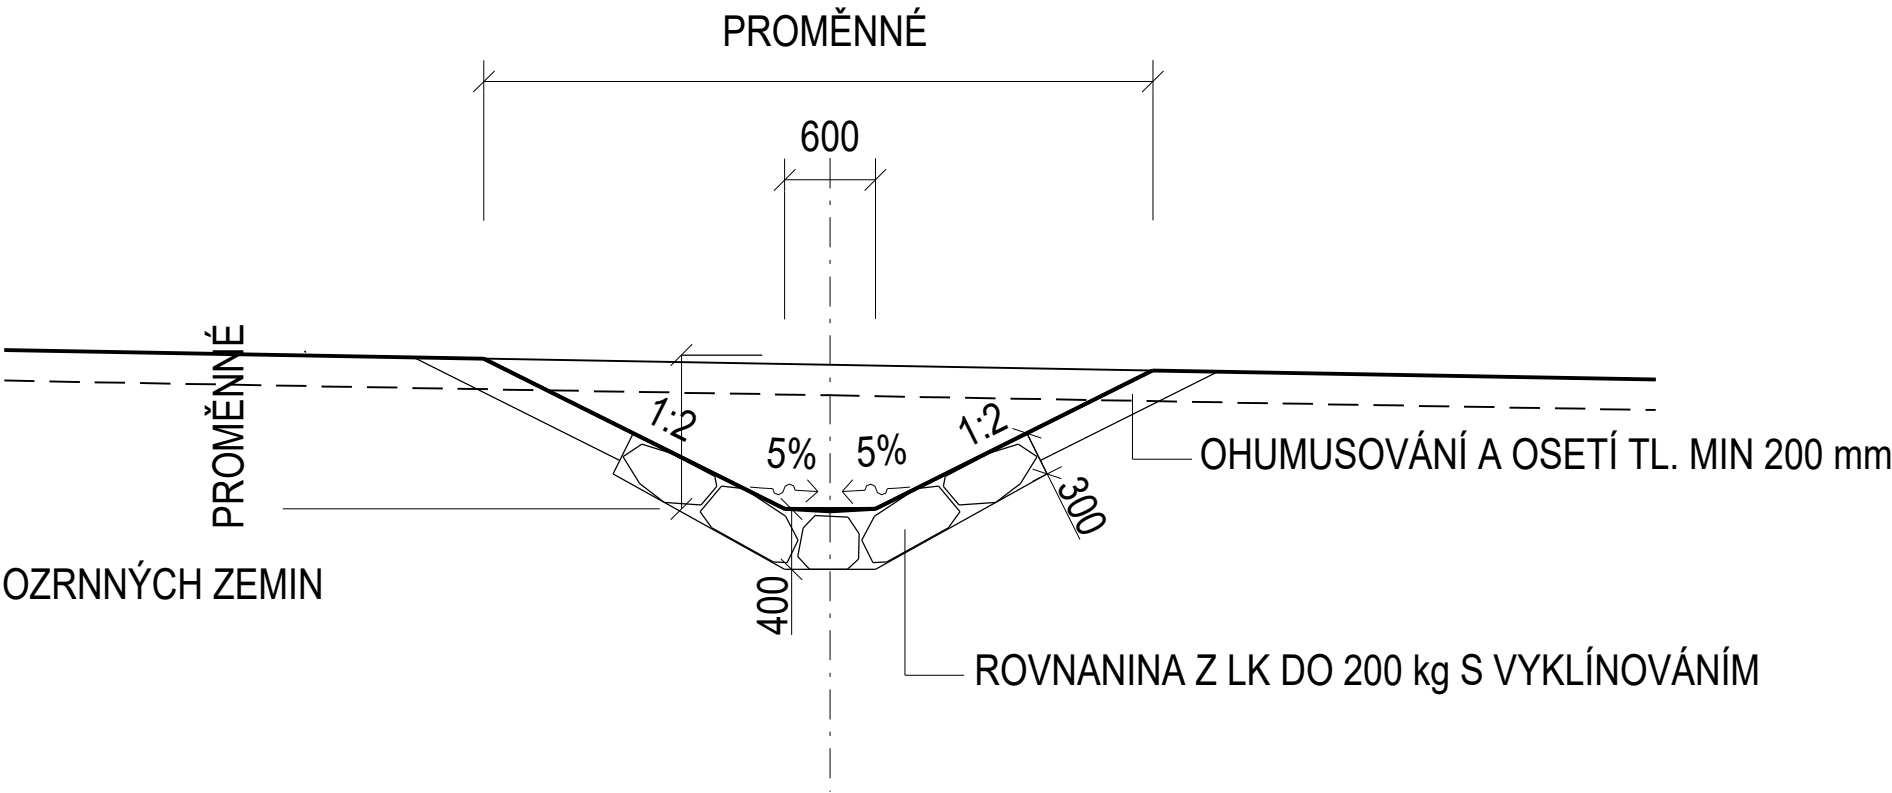

Souřadnicový systém: S-JTSK
Výškový systém: Bpv

SO 325 Úprava koryta v km 4,21

Objednatel:



**ŘEDITELSTVÍ
SILNIC
A DÁLNIC**

Ředitelství silnic a dálnic s. p.
Čerčanská 2023/12, Krč, 140 00 Praha 4

Zhotovitel:



Valbek

Valbek, spol. s r.o.
Vaňurova 505/17
460 07 Liberec 3

	Vypracoval	ING. J. VANCL		Zak. číslo	21-LI13-001
	Zodp. projektant	ING. J. VANCL		Datum	02/2025
	Tech. kontrola	ING. D. LANDA		Stupeň	PDPS
	Akce I/16 MLADÁ BOLESLAV - MARTINOVICE			Počet formátů	3 x A4
				Měřitko	1 : 50
Zhotovitel: Valbek, spol. s r.o. Vaňurova 505/17 460 07 Liberec 3	Příloha VZOROVÉ PŘÍČNÉ ŘEZY			4	Č. přílohy Paré