
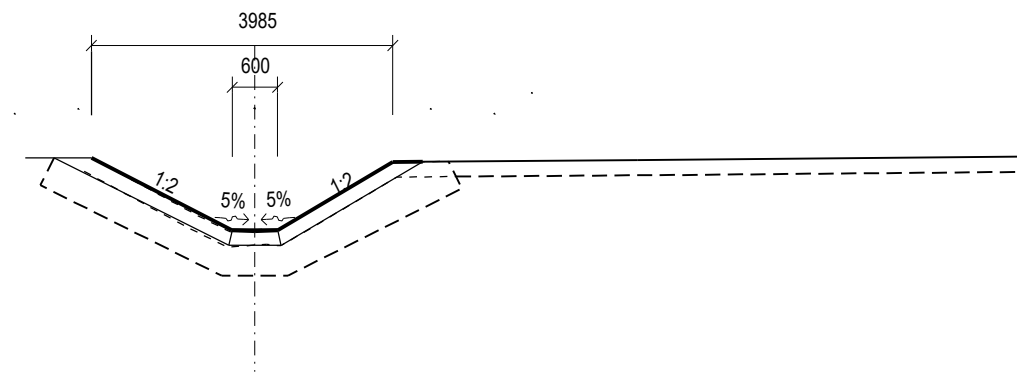
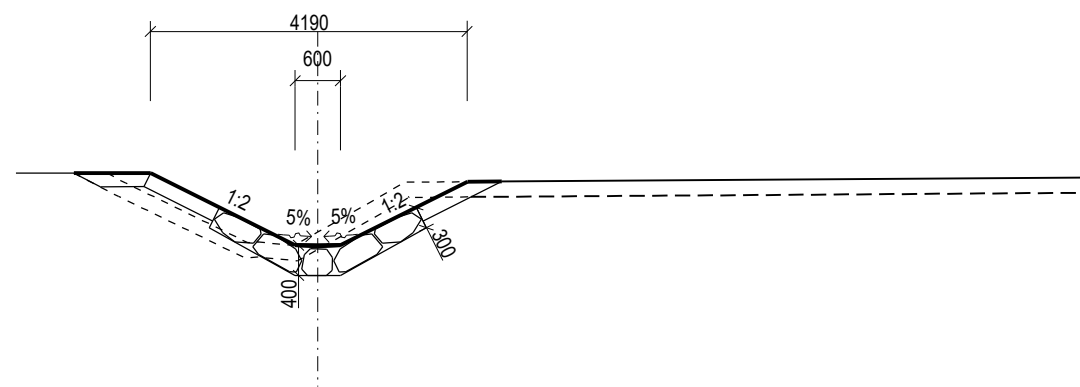



ŘEZY JSOU PROTI SMĚRU TOKU

[illegible]

	SR.ROVINA 216 m					
NOVÝ STAV						
TERÉN	-2.92	219.48	-2.21	219.45	-0.30	218.46
	-2.54	219.28			0.00	218.46
	-0.93	218.49			0.30	218.46
	-0.79	218.50				
	-0.31	218.46				
	0.00	218.63				
	0.80	219.09				
	1.15	219.29				
					1.98	219.30

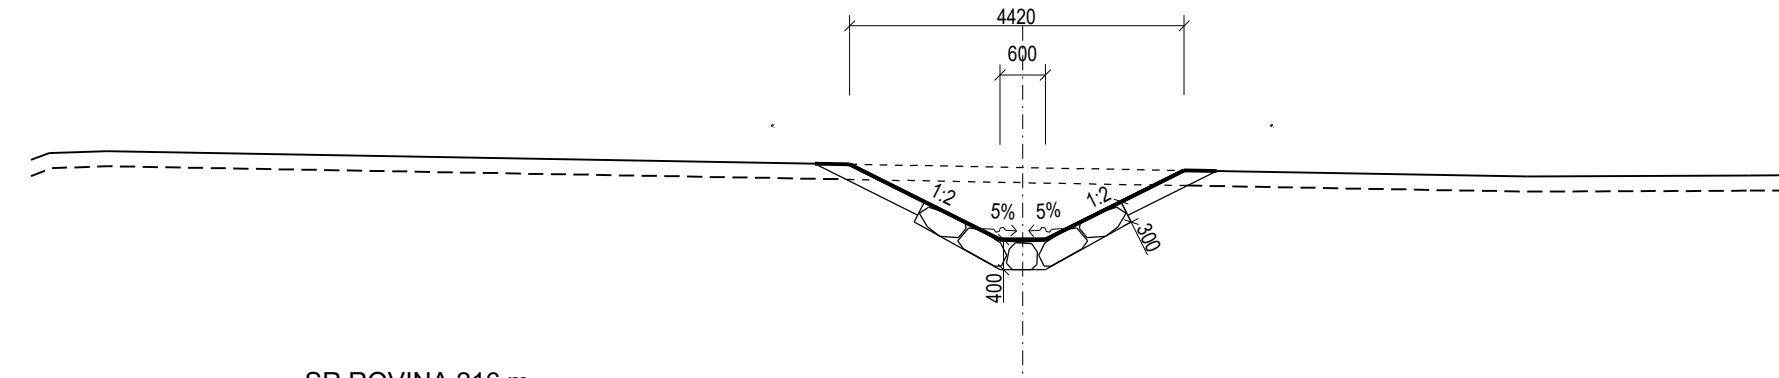

NOVÝ STAV			-2.29 219.57	-0.30 218.57 0.00 218.57 0.30 218.57	2.13 219.49				
TERÉN				0.00 219.53			6.68 219.41		9.62 219.42

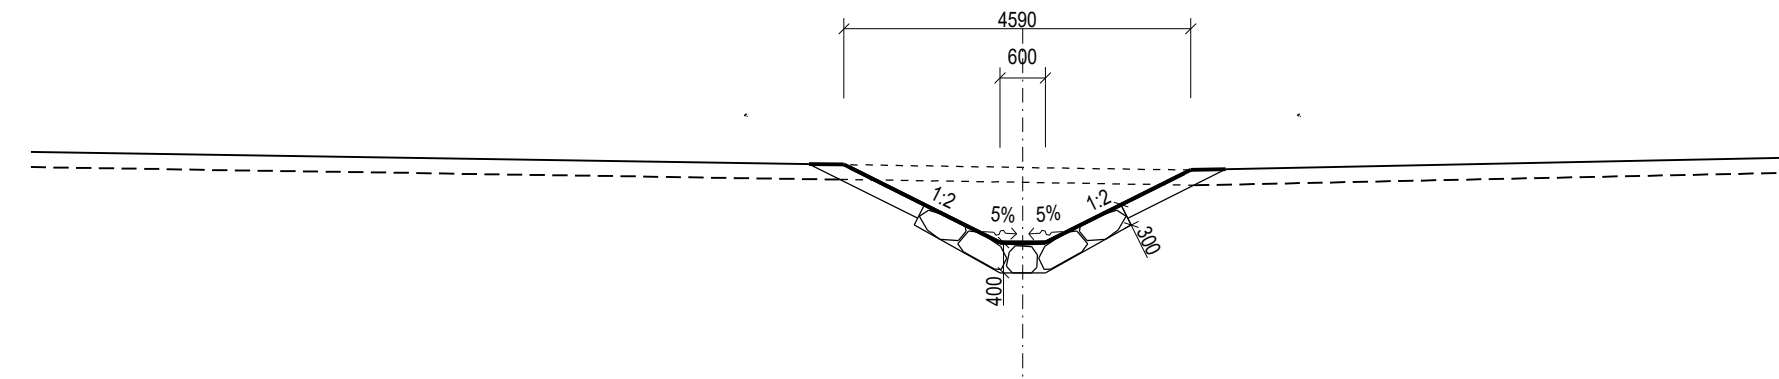

	SR.ROVINA 216 m					
NOVÝ STAV	-2.36	219.72	-0.30	218.69	0.00	218.69
TERÉN	0.00	219.69	0.30	218.69	2.22	219.65

SO 325 Úprava koryta v km 4,21

Objednatel:  ŘEDITELSTVÍ SILNIC A DÁLNIC	Ředitelství silnic a dálnic s. p. Čerčanská 2023/12, Krč, 140 00 Praha 4
---	--

Zhotovitel: 	Valbek, spol. s r.o. Vaňurova 505/17 460 07 Liberec 3
--	--

	Vypracoval	ING. J. VANCL		Zak. číslo	21-LI13-001
	Zodp. projektant	ING. J. VANCL		Datum	02/2025
	Tech. kontrola	ING. D. LANDA		Stupeň	PDPS
	Akce I/16 MLADÁ BOLESLAV - MARTINOVICE			Počet formátů	3 x A4
Zhotovitel: Valbek, spol. s r.o. Vaňurova 505/17 460 07 Liberec 3	Příloha PŘÍČNÉ ŘEZY			Měřitko	1 : 100
				Č. přílohy	Paré
				5	