
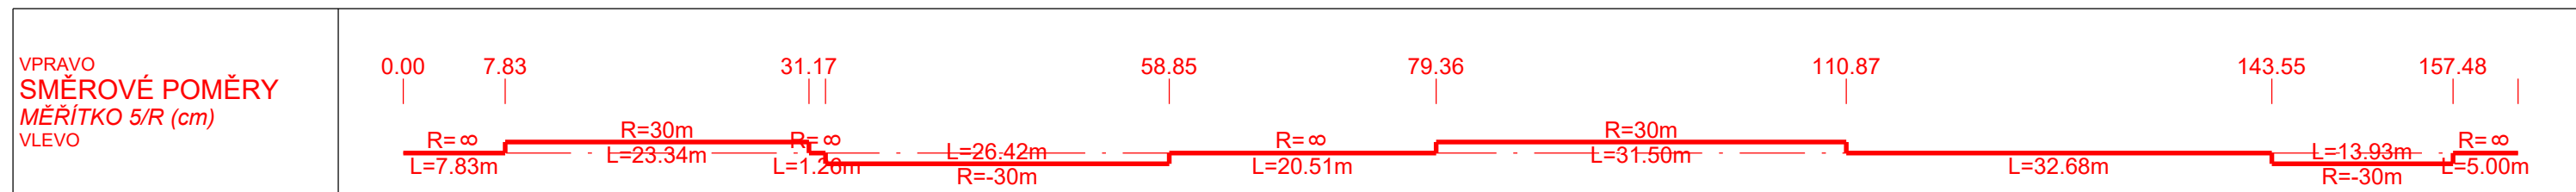


PODÉLNÝ PROFIL

M 1:500/100

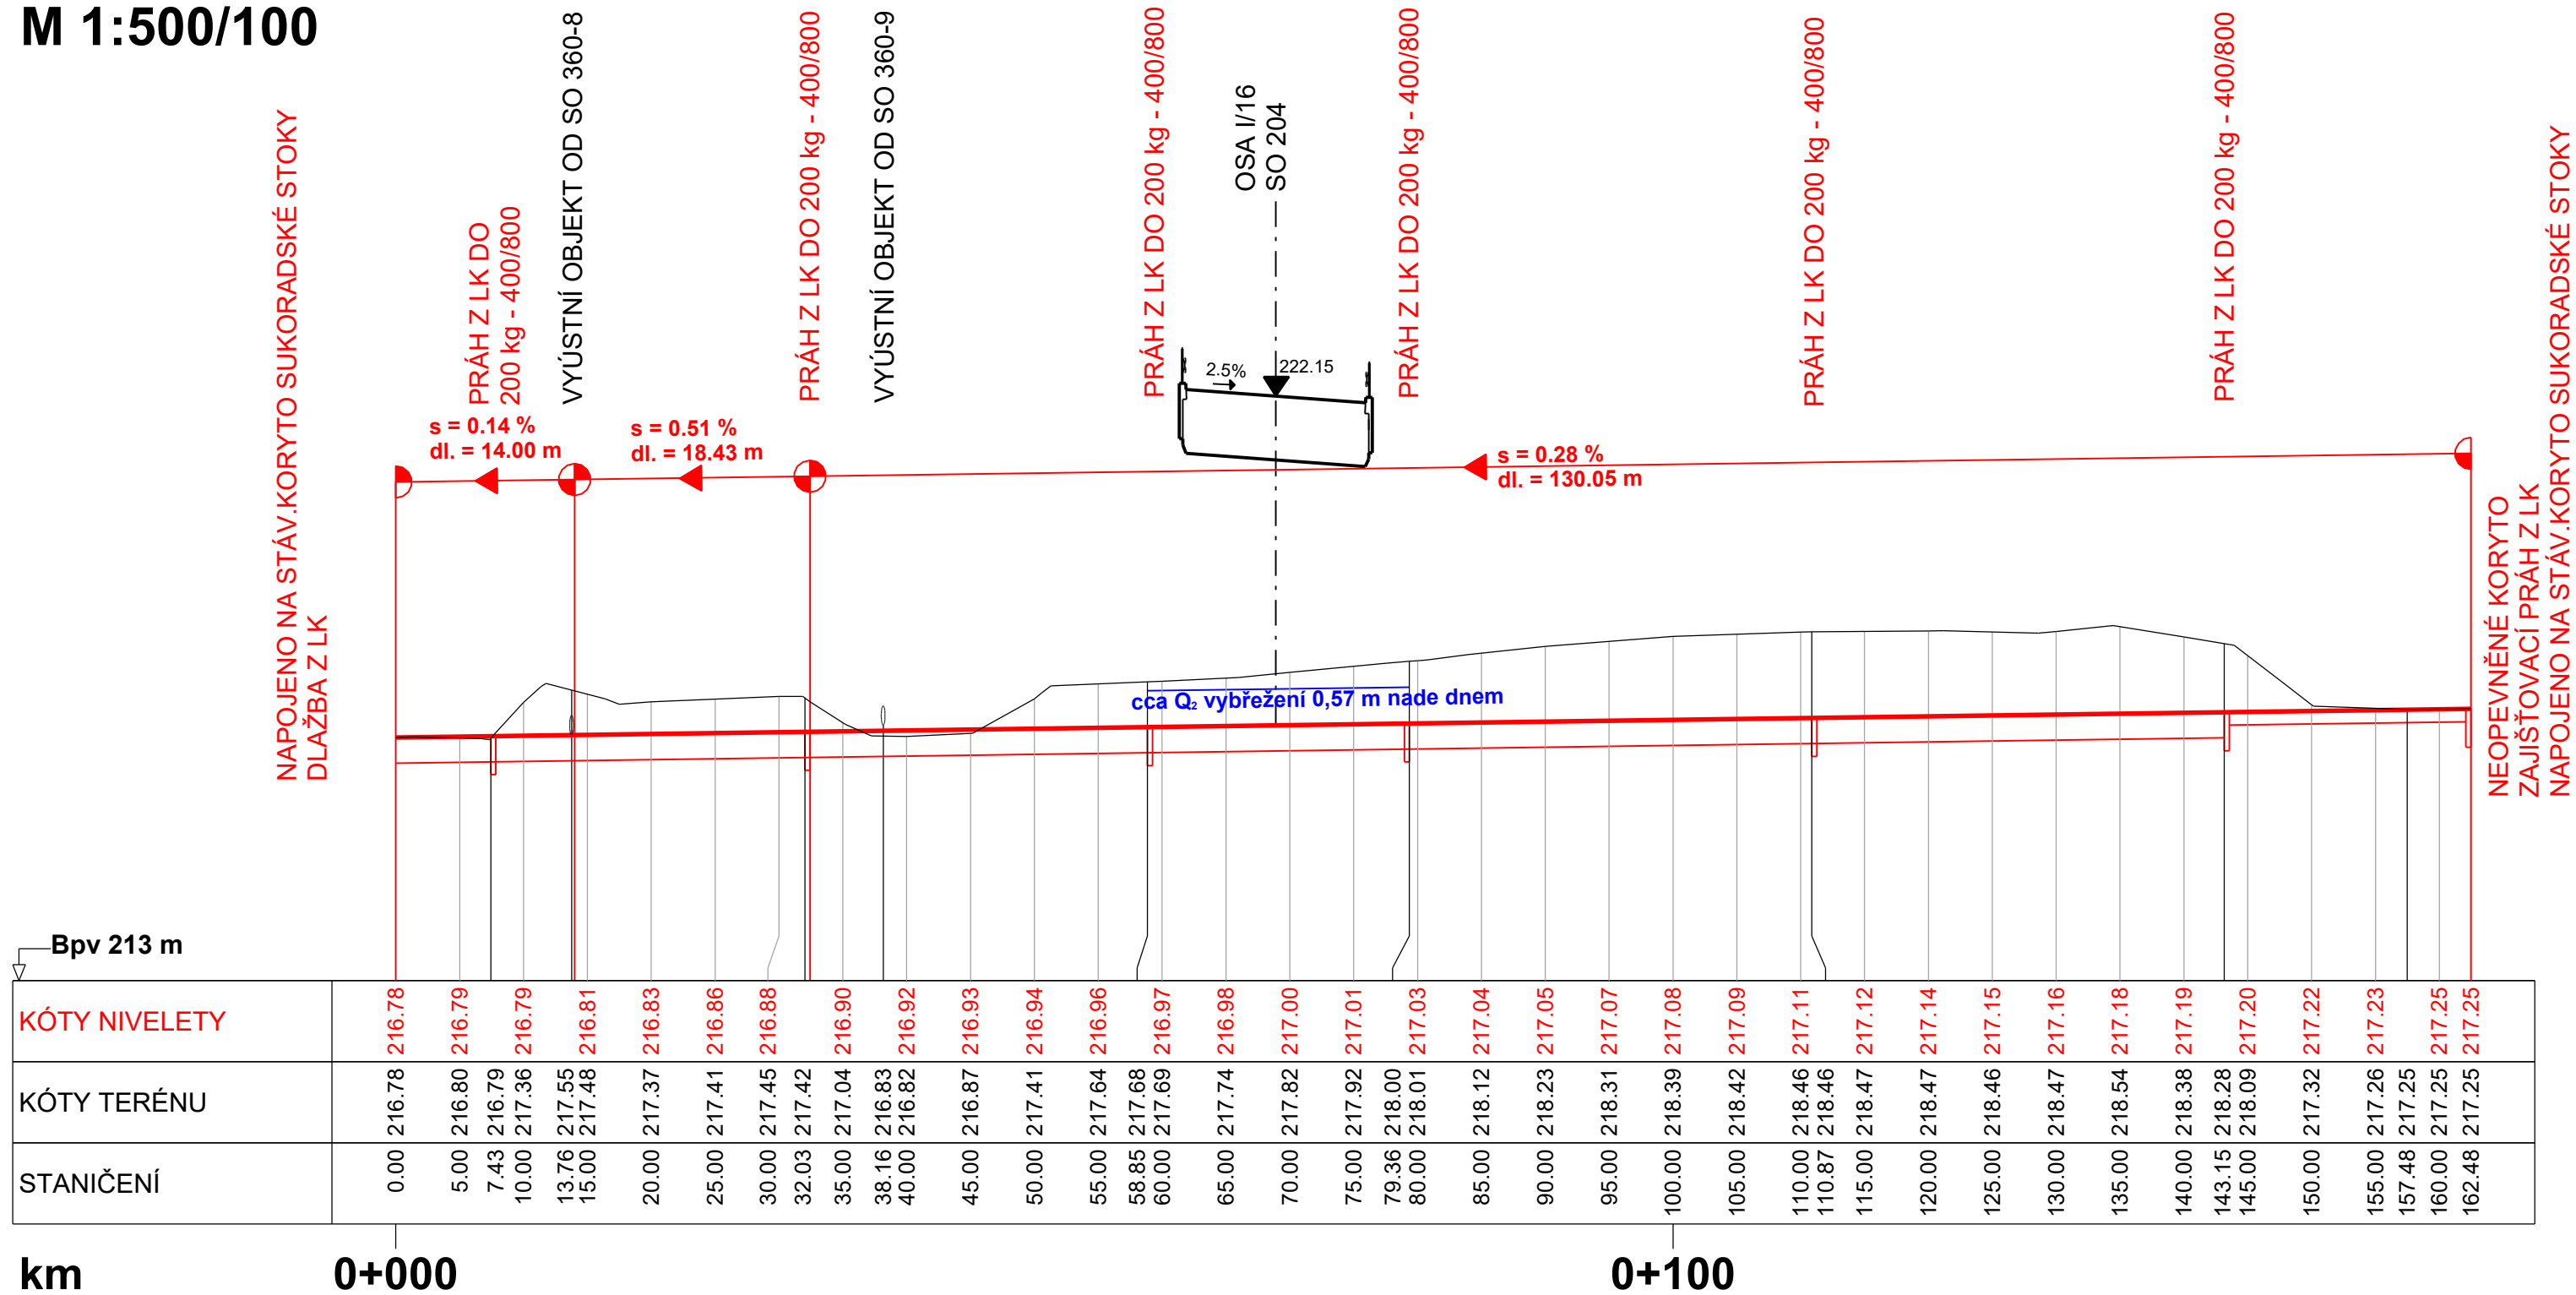

Souřadnicový systém: S-JTSK
Výškový systém: Bpv

SO 326 Úprava Sukoradskej stoky

Objednatel:



ŘEDITELSTVÍ SILNIC A DÁLNIC

Ředitelství silnic a dálnic s. p.
Čerčanská 2023/12, Krč, 140 00 Praha 4

Zhotovitel:



Valbek, spol. s r.o.
Vaňurova 505/17
460 07 Liberec 3



Vypracoval	ING. J. VANCEL
Zodp. projektant	ING. J. VANCEL
Tech. kontrola	ING. D. LANDA

I/16 MLADÁ BOLESLAV - MARTINOVICE

Zhotovitel:
Valbek, spol. s r.o.
Vaňurova 505/17
460 07 Liberec 3

Příloha	PODÉLNÝ PROFIL
---------	----------------

3