


VZOROVÉ PŘÍČNÉ ŘEZY
M 1:50


VZOROVÝ ŘEZ KORYTEM
OPEVNĚNÍ DLAŽBOU Z LOMOVÉHO KAMENE
- V MÍSTĚ PŘED PROPUSTKY

PLATNOST: KM ZÚ - 0,007 83

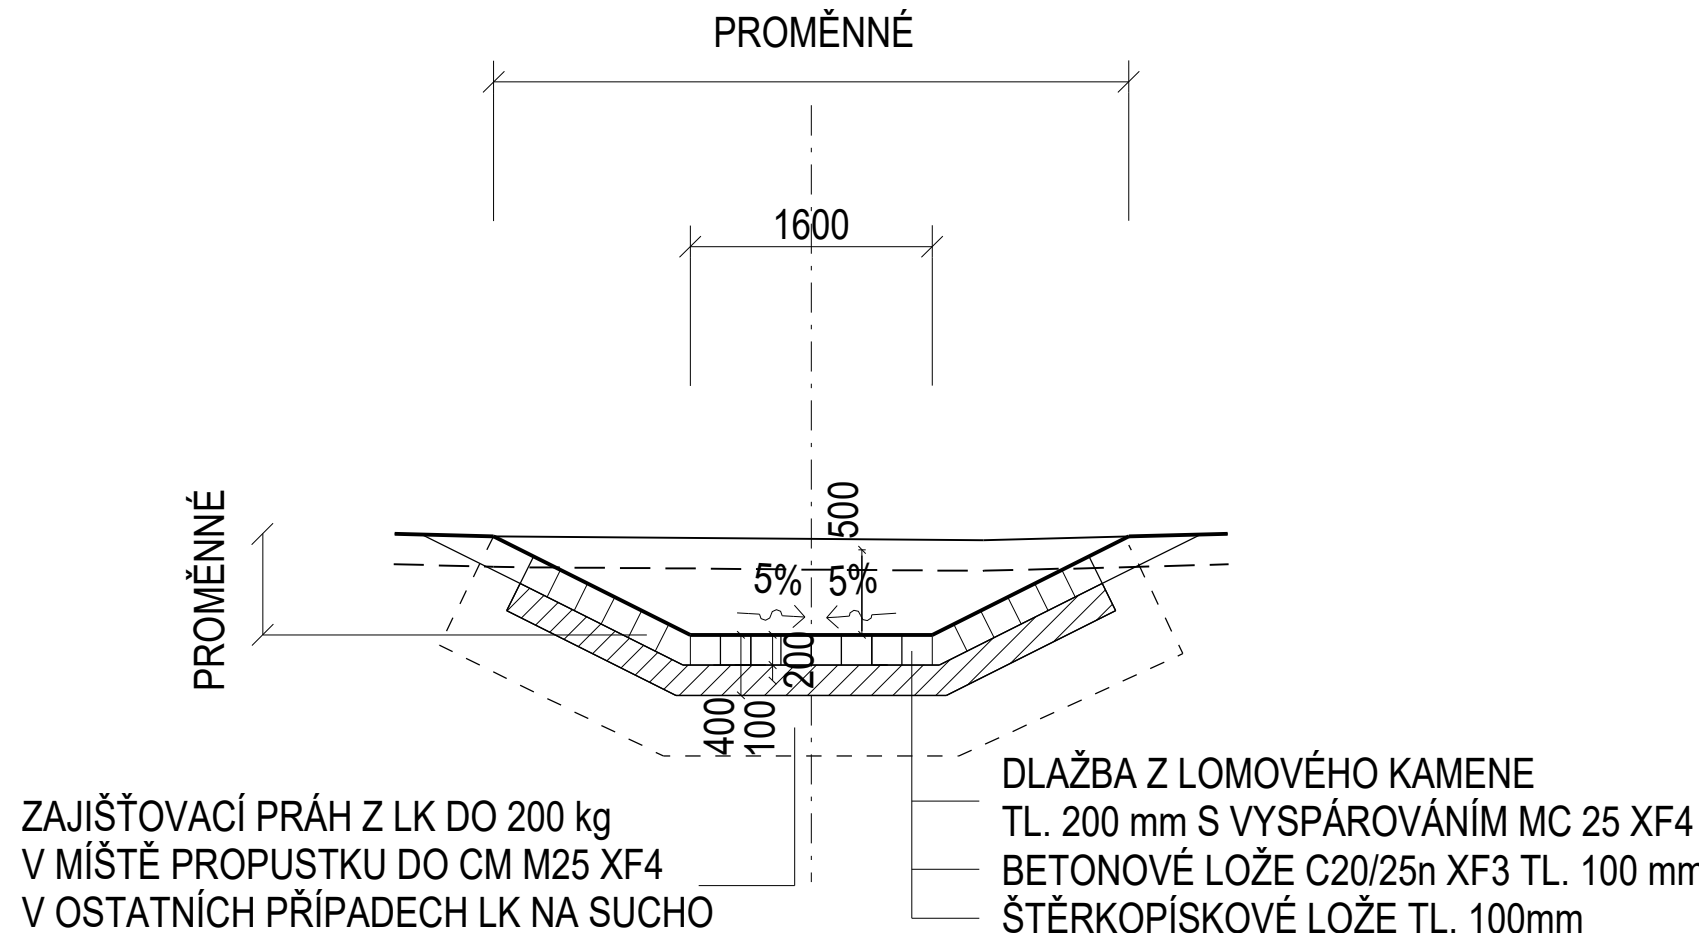


VZOROVÝ ŘEZ OPEVNĚNÝM KORYTEM
OPEVNĚNÍ - ROVNANINA Z LOMOVÉHO KAMENE

PLATNOST: KM 0,007 83 - 0,143 55

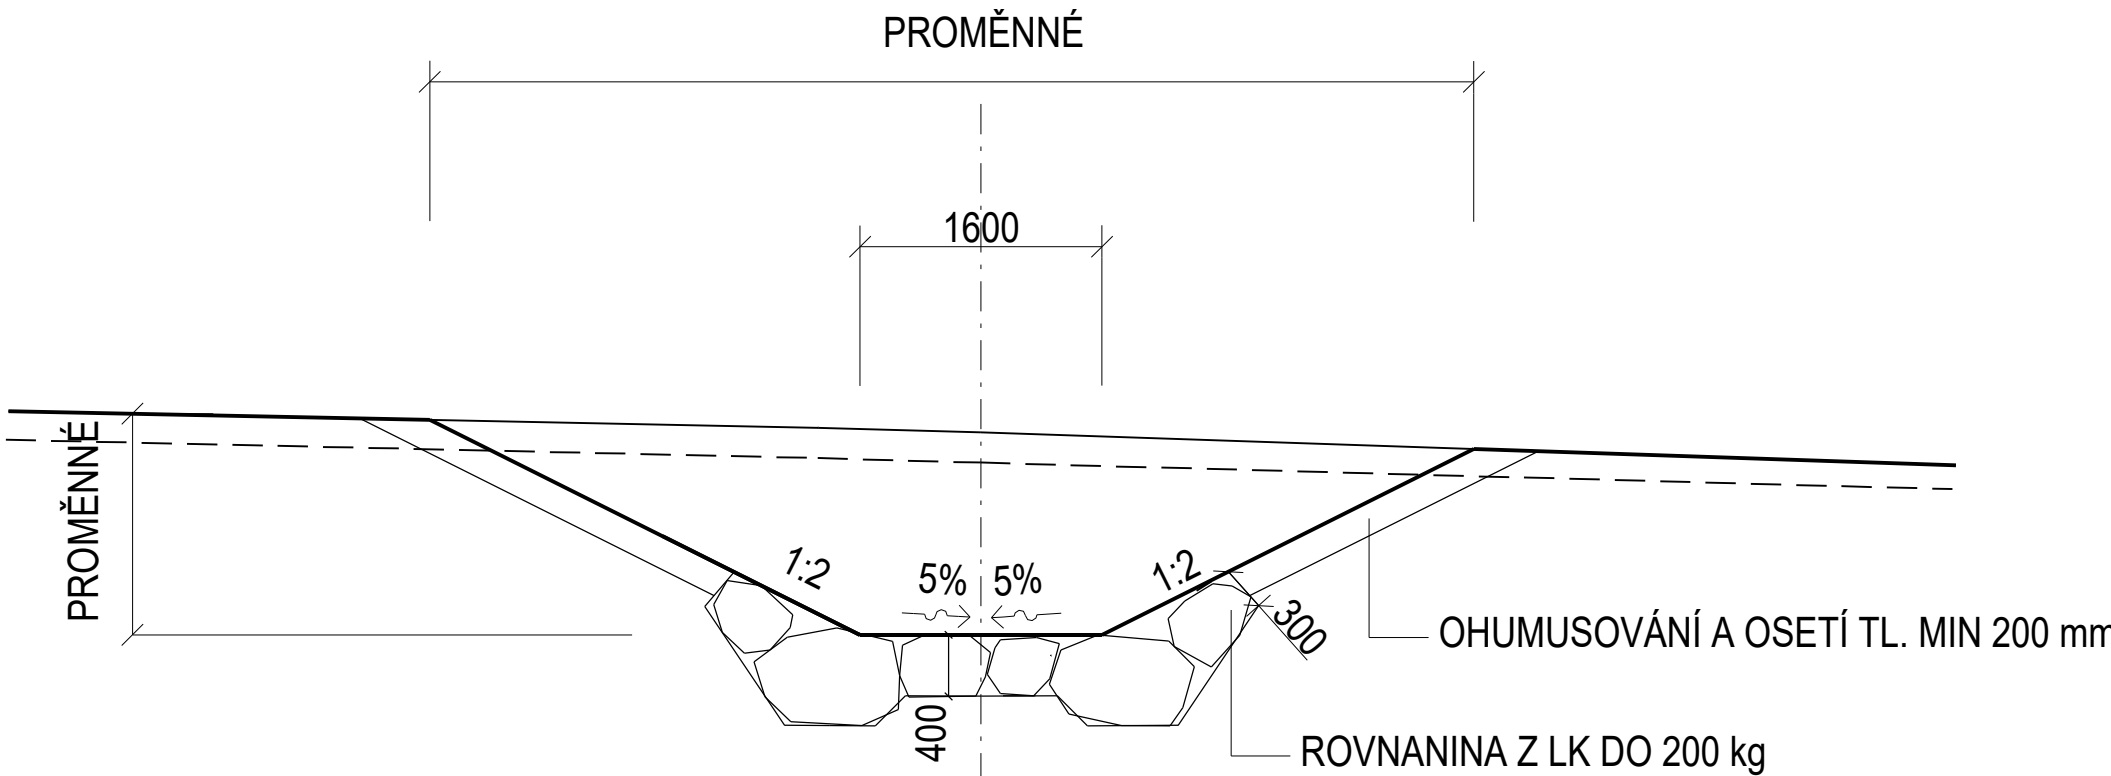

VZOROVÝ ŘEZ NEOPEVNĚNÝM KORYTEM

PLATNOST: KM 0,143 55 - KÚ

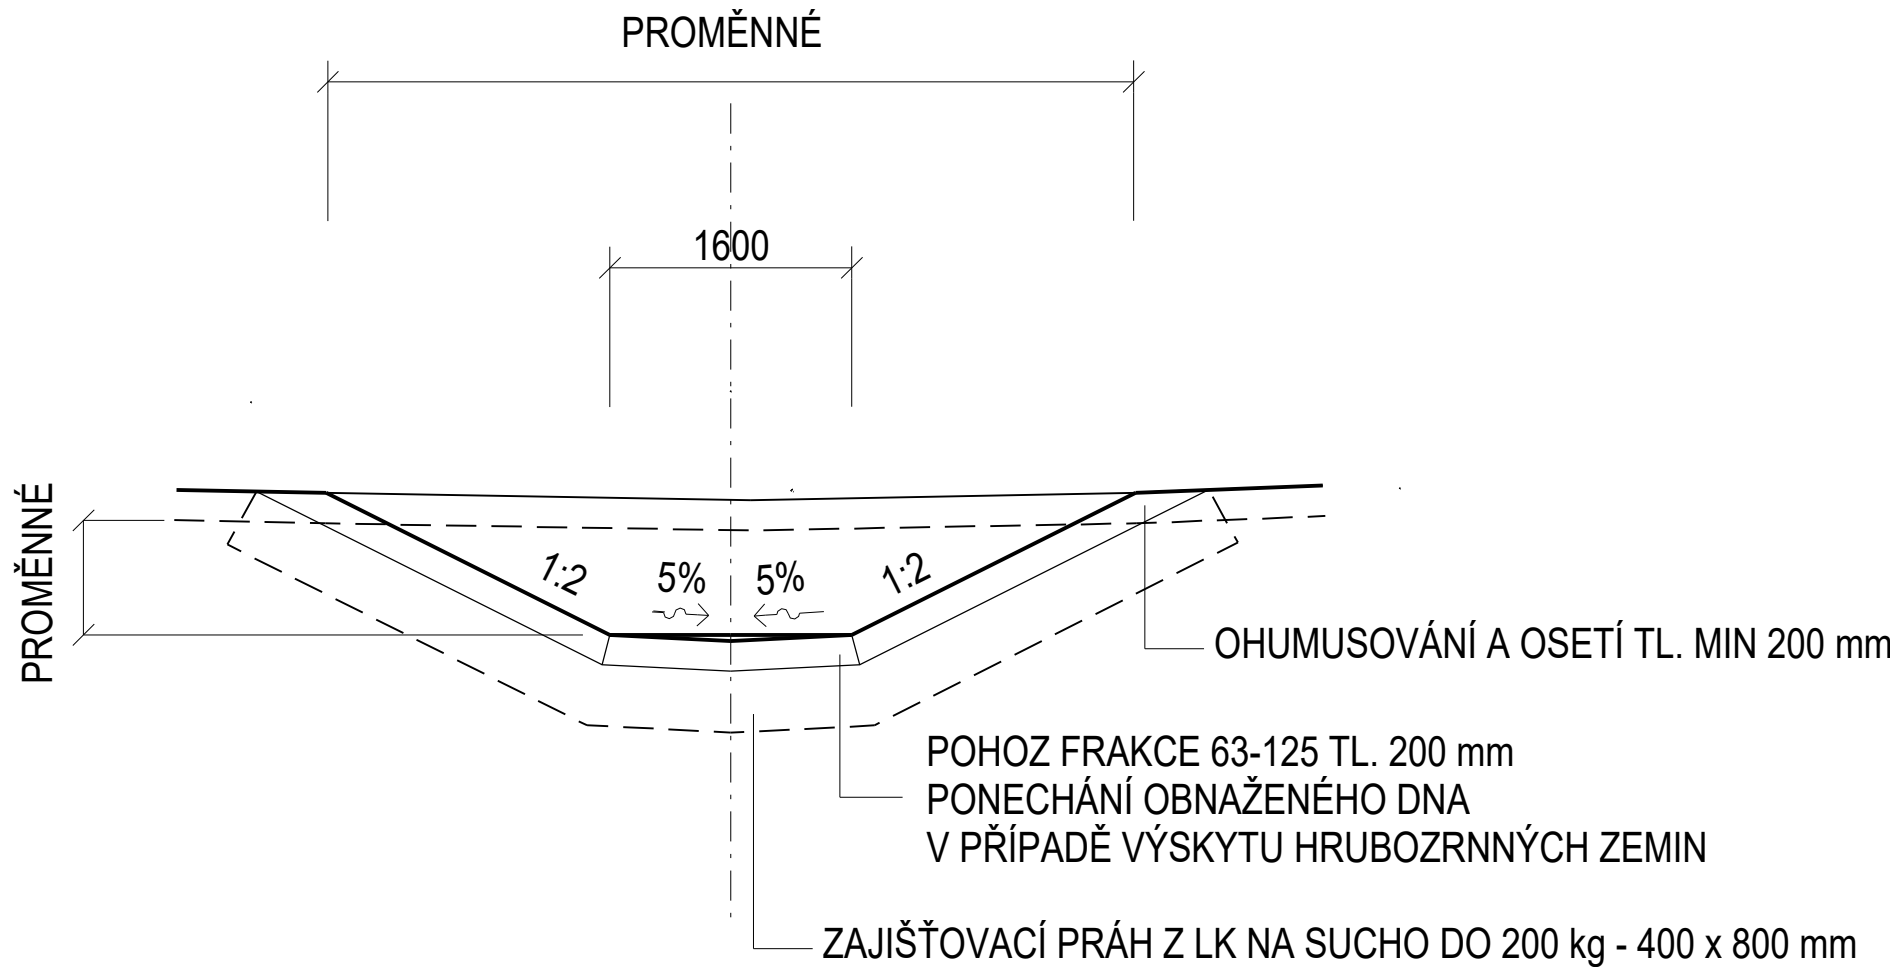

Souřadnicový systém: S-JTSK
Výškový systém: Bpv

SO 326 Úprava Sukoradské stoky

Objednatel:



Ředitelství silnic a dálnic s. p.
Čerčanská 2023/12, Krč, 140 00 Praha 4

Zhotovitel:



Valbek, spol. s r.o.
Vaňurova 505/17
460 07 Liberec 3

	Vypracoval	ING. J. VANCL		Zak. číslo	21-L113-001
	Zodp. projektant	ING. J. VANCL		Datum	02/2025
	Tech. kontrola	ING. D. LANDA		Stupeň	PDPS
	Akce I/16 MLADÁ BOLESLAV - MARTINOVICE			Počet formátů	5 x A4
Měřítko				1 : 50	
Č. přílohy				Paré	
Zhotovitel: Valbek, spol. s r.o. Vaňurova 505/17 460 07 Liberec 3	Příloha VZOROVÉ PŘÍČNÉ ŘEZY			4	