


PŘÍČNÉ ŘEZY
M 1:100


ŘEZY JSOU PROTI SMĚRU TOKU

km 0,010 00

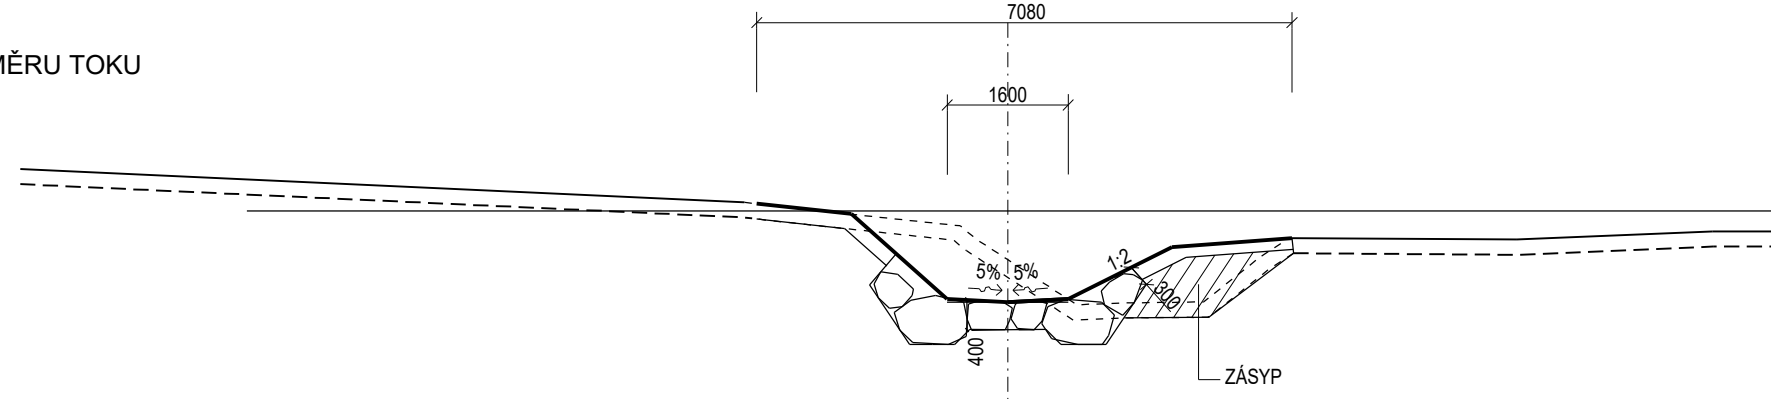


SR.ROVINA 214 m	
NOVÝ STAV	-3.32 218.09 -2.07 218.00 -0.80 216.83 0.00 216.79 0.80 216.83 2.18 217.49 3.72 217.51
TERÉN	-3.48 218.11 -0.63 217.80 -0.43 217.63 0.00 217.36 0.92 216.76 1.54 216.78 2.59 216.79 3.33 217.39 3.72 217.64 6.74 217.62 9.33 217.73

km 0,020 00

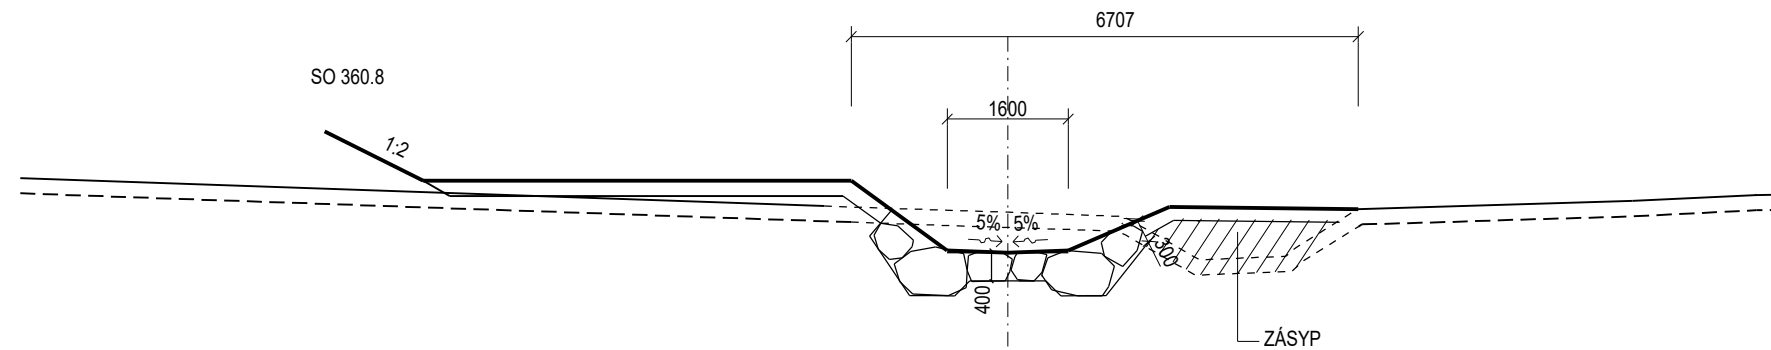


SR.ROVINA 214 m	
NOVÝ STAV	-2.07 217.78 -0.80 216.86 0.00 216.83 0.80 216.86 2.14 217.46 4.64 217.40
TERÉN	0.00 217.37 1.52 217.31 1.66 217.24 2.54 216.74 3.68 216.78 3.79 216.88 4.63 217.40 8.27 217.51 9.90 217.59

km 0,040 00

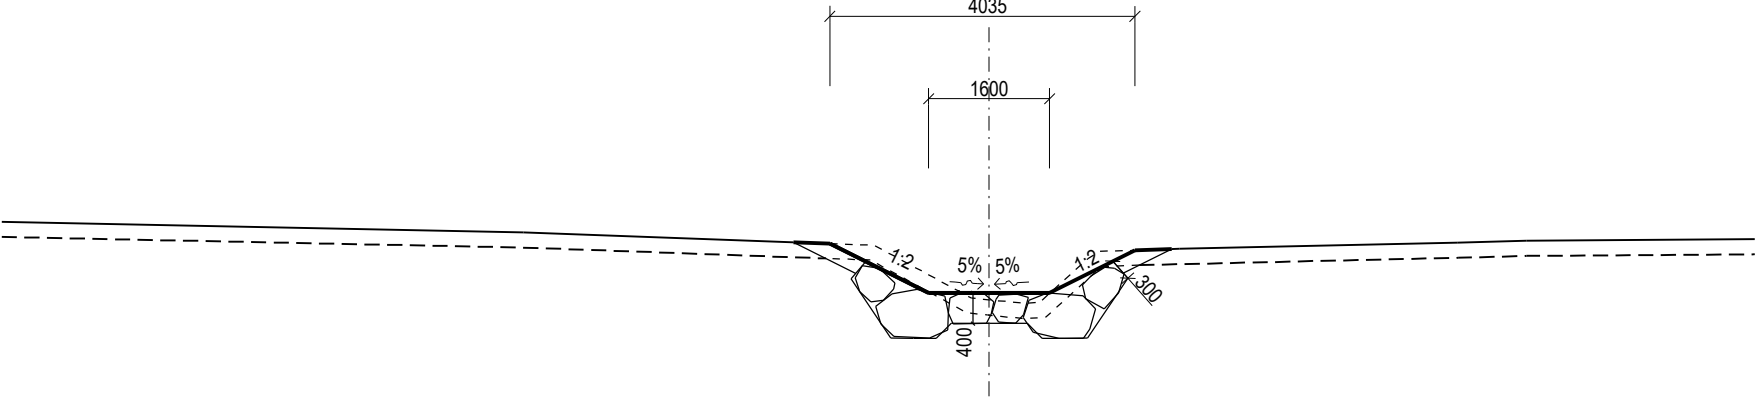


SR.ROVINA 214 m	
NOVÝ STAV	-2.11 217.57 -0.80 216.92 0.00 216.90 0.80 216.92 0.81 216.92 1.94 217.48
TERÉN	-6.16 217.71 -1.52 217.55 -0.40 216.94 -0.23 216.85 0.00 216.82 0.46 216.78 0.67 216.79 1.30 217.37 1.46 217.47 2.52 217.50 6.20 217.58 7.11 217.61

km 0,080 00

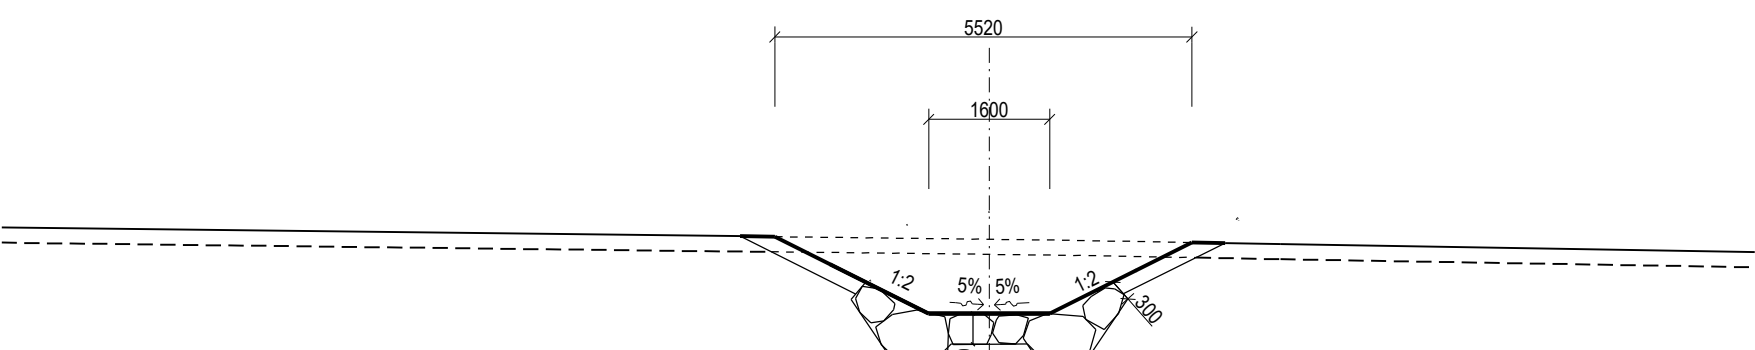


SR.ROVINA 215 m	
NOVÝ STAV	-2.84 218.04 -0.80 217.03 0.00 217.00 0.80 217.03 2.68 217.97
TERÉN	0.00 218.01 1.10 218.00 3.86 217.94

km 0,120 00

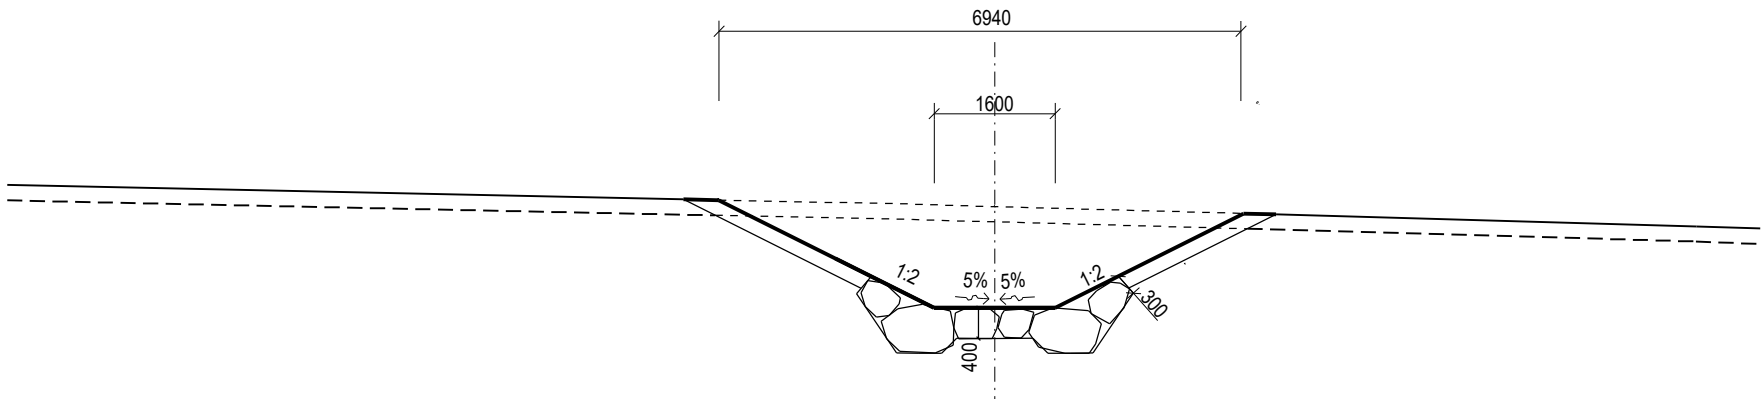

SR.ROVINA 215 m	
NOVÝ STAV	-3.65 218.56 -0.80 217.14 0.00 217.11 0.80 217.14 3.29 218.38
TERÉN	-1.08 218.51 0.00 218.47 9.29 218.21

km 0,160 00

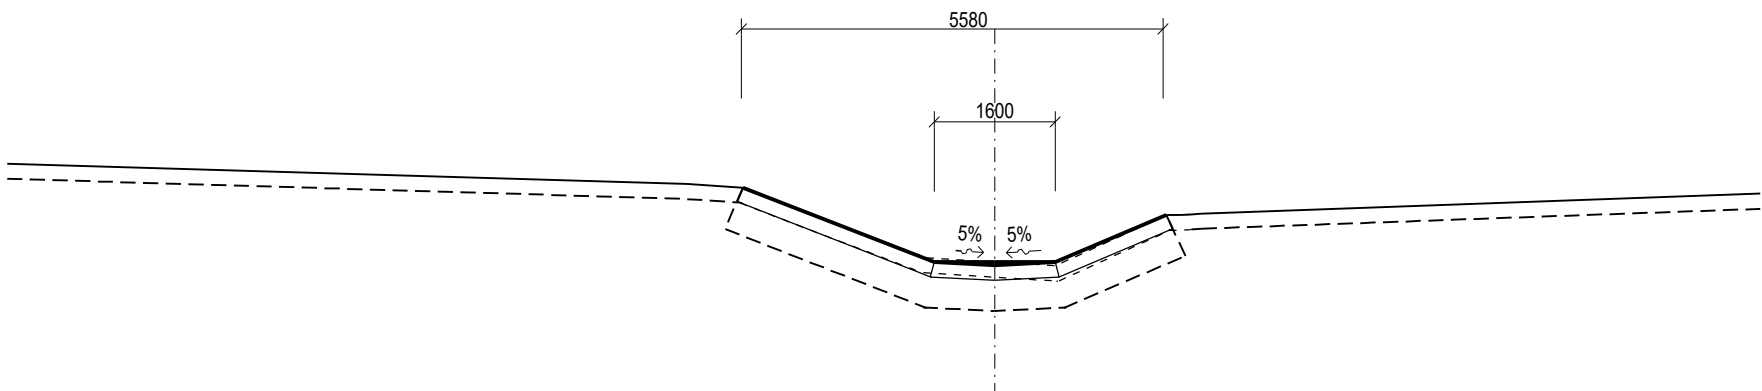

SR.ROVINA 214 m	
NOVÝ STAV	-3.33 218.23 -0.80 217.25 0.00 217.23 0.80 217.25 2.27 217.87
TERÉN	-4.07 218.28 -3.33 218.23 -0.99 217.34 -0.94 217.31 0.00 217.25 0.78 217.20 0.80 217.20 2.27 217.87 2.45 217.87 2.57 217.88 2.73 217.89

Souřadnicový systém: S-JTSK
Výškový systém: Bpv

SO 326 Úprava Sukoradské stoky

Objednatel:



Ředitelství silnic a dálnic s. p.
Čerčanská 2023/12, Krč, 140 00 Praha 4

Zhotovitel:



Valbek, spol. s r.o.
Vaňurova 505/17
460 07 Liberec 3

	Vypracoval	ING. J. VANCL		Zak. číslo	21-L113-001
	Zodp. projektant	ING. J. VANCL		Datum	02/2025
	Tech. kontrola	ING. D. LANDA		Stupeň	PDPS
	Akce I/16 MLADÁ BOLESLAV - MARTINOVICE			Počet formátů	5 x A4
Měřítko				1 : 100	
Č. přílohy				Paré	
Zhotovitel: Valbek, spol. s r.o. Vaňurova 505/17 460 07 Liberec 3	Příloha PŘÍČNÉ ŘEZY			5	