
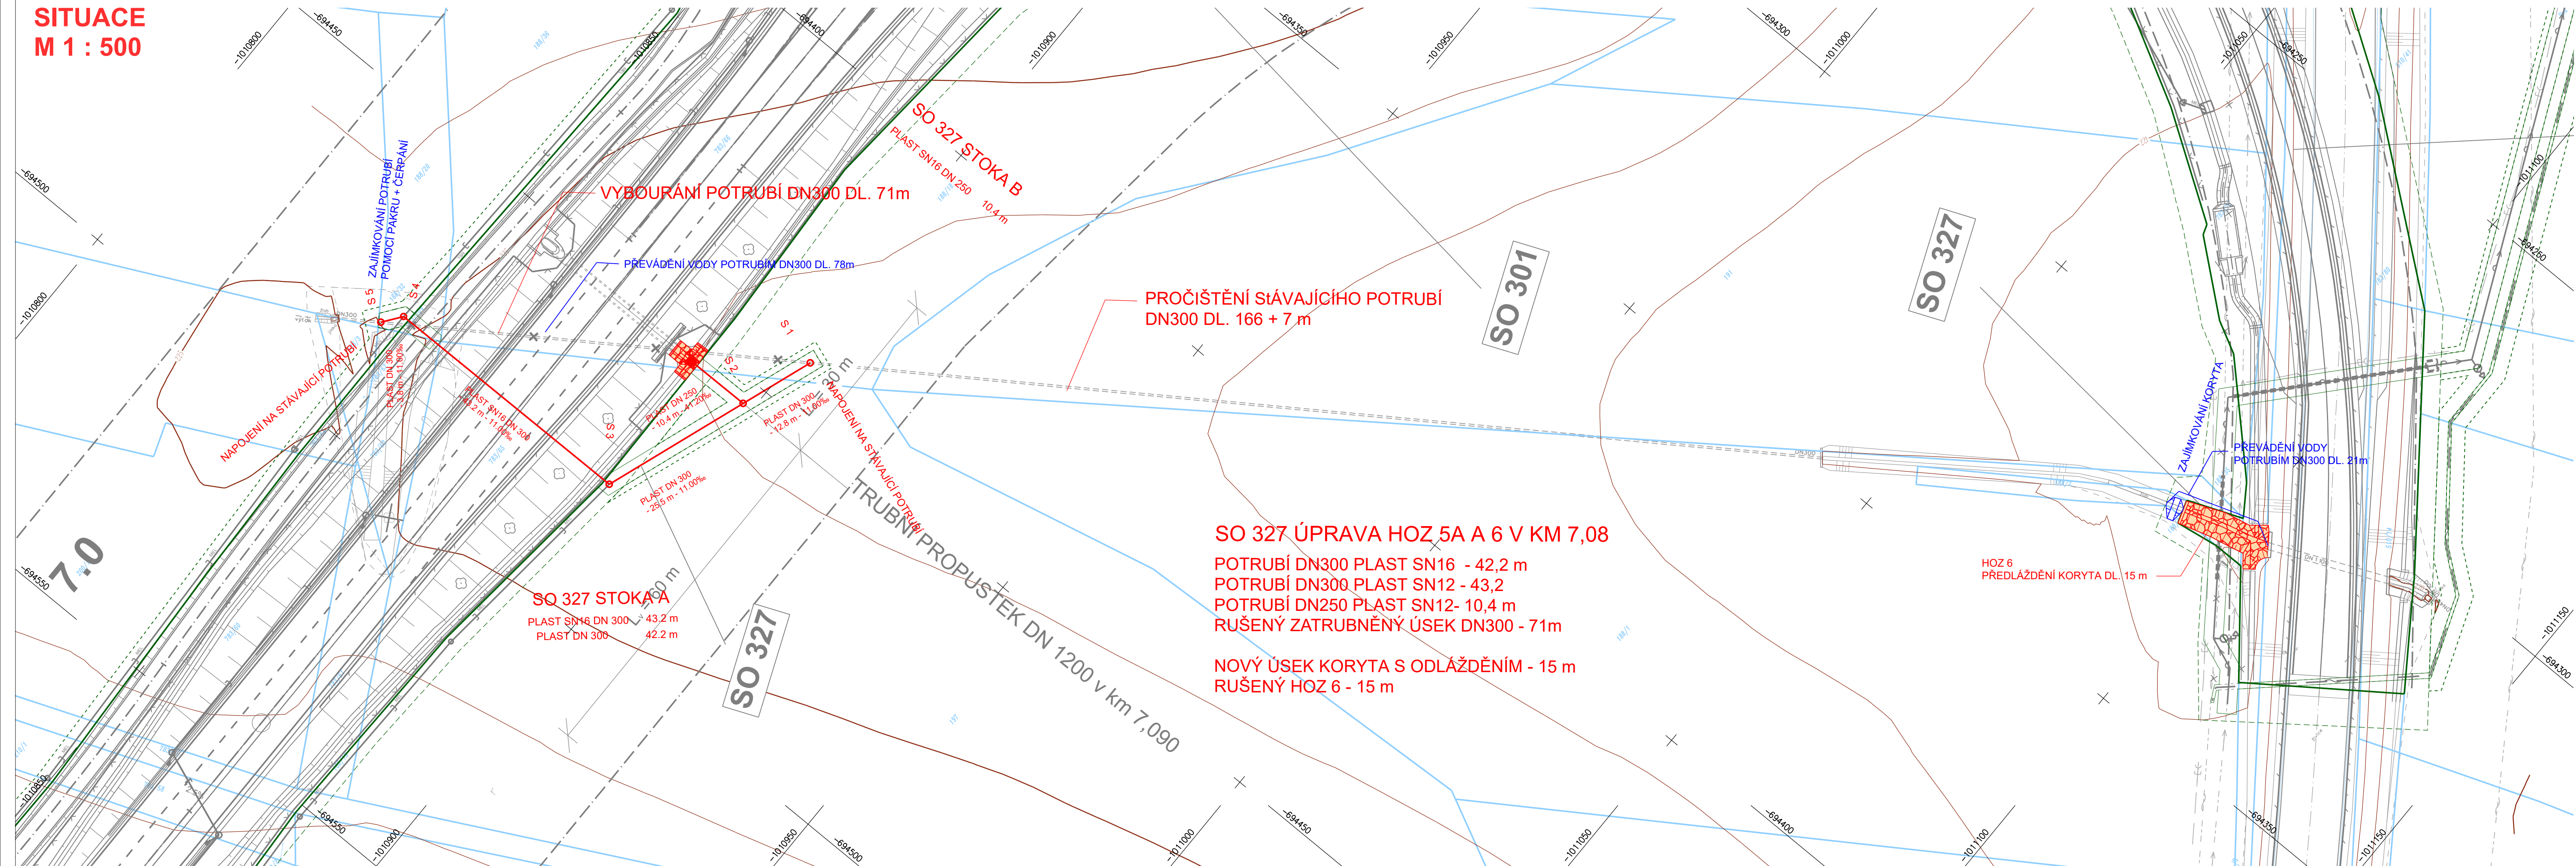
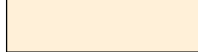


SITUACE
M 1 : 500

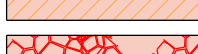

LEGENDA:

PLOCHY

- | | |
|---|-------------------------------|
|  | OHUMUSOVÁNÍ VÝKOP |
|  | OHUMUSOVÁNÍ NÁSYP |
|  | DLAŽBA Z LK DO BETONU |
|  | POHOZ KAMENIVEM |
|  | ROVNANINA Z LK |
|  | ROVNANINA Z LK S OHUMUSOVÁNÍM |
|  | PRÁH BETONOVÝ |
|  | PRÁH Z LK NA CM |
|  | BETONOVÉ KONSTRUKCE |
|  | ŽB KONSTRUKCE |
|  | SANACE STÁVAJÍCÍHO KORYTA |

Souřadnicový systém: S-JTSK
Výškový systém: Bpv

SO 327 Úprava HOZ 5A a 6 v km 7,08

Objednatel:



Ředitelství silnic a dálnic s. p.
Čerčanská 2023/12, Krč, 140 00 Praha 4

Zhotovitel:



Valbek, spol. s r.o.
Vaňurova 505/17
460 07 Liberec 3

	Vypracoval	ING. J. VANCL	<i>Jancl</i>	Zak. číslo	21-L113-001
	Zodp. projektant	ING. J. VANCL	<i>Jancl</i>	Datum	02/2025
	Techn. kontrola	ING. D. LANDA	<i>Land</i>	Stupeň	PDPS
	Akce			Počet formátů	5 x A4
I/16 MLADÁ BOLESLAV - MARTINOVICE				Měřítko	1 : 500
				Č. přílohy	Paré
Zhotovitel: Valbek, spol. s r.o. Vaňhurova 505/17 460 07 Liberec 3	Příloha SITUACE	2			