


VZOROVÝ PŘÍČNÝ ŘEZ

M 1:50

VZOROVÝ ŘEZ KORYTEM
OPEVNĚNÍ DLAŽBOU Z LOMOVÉHO KAMENE
- PŘEDLÁŽDĚNÍ KORYTA PŘED PROPUSTKEM

PLATNOST: KM ZÚ - KÚ

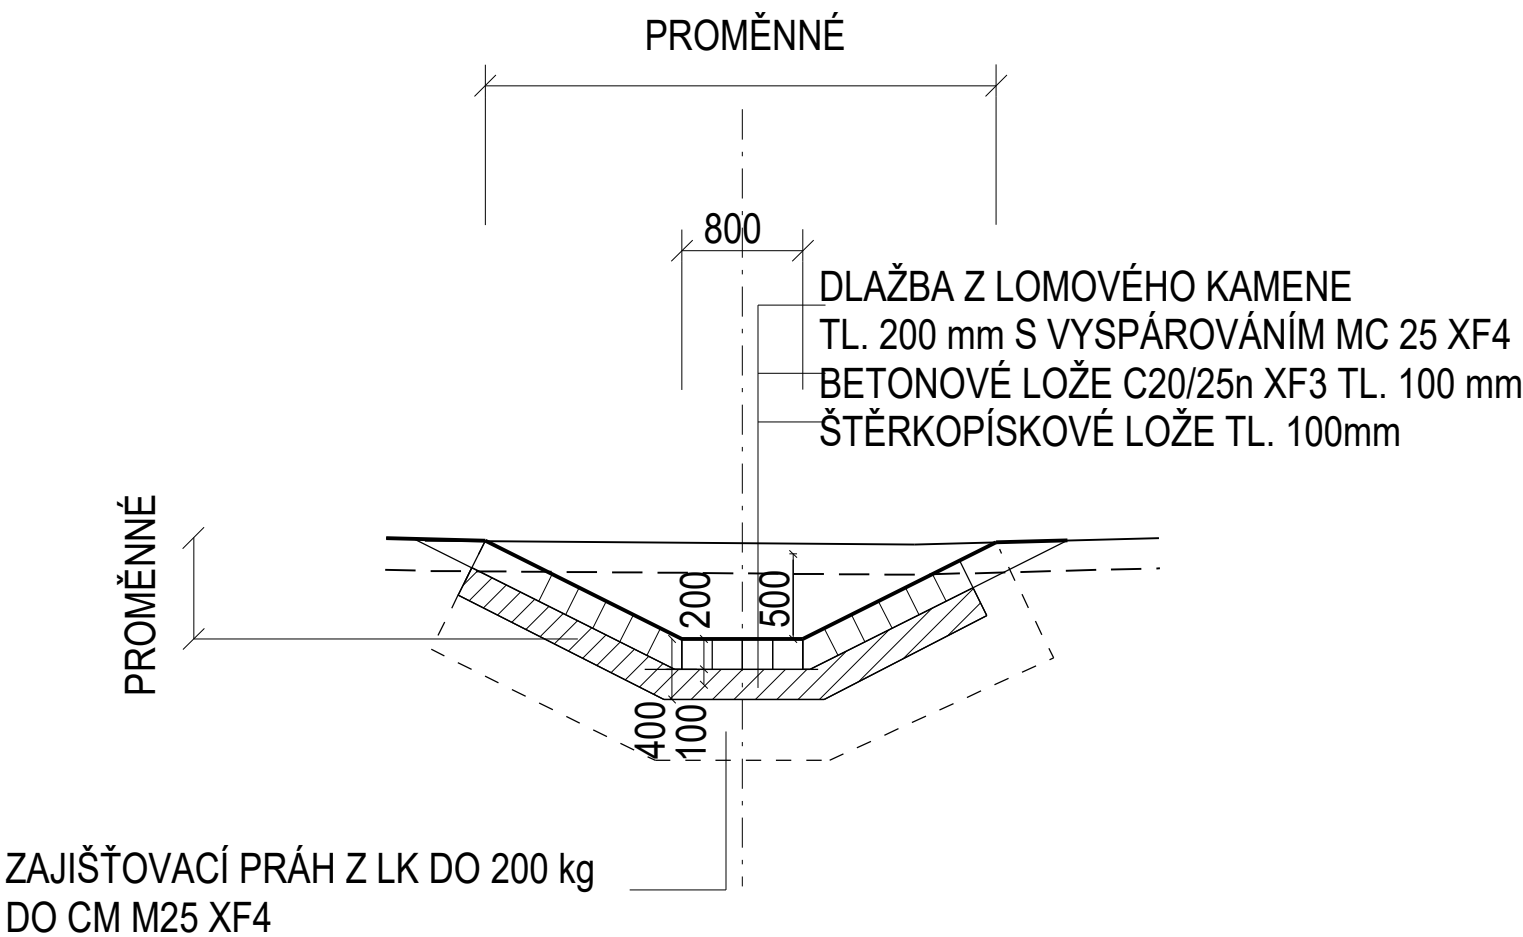

Souřadnicový systém: S-JTSK
Výškový systém: Bpv

SO 327 Úprava HOZ 5A a 6 v km 7,08

Objednatel:



**ŘEDITELSTVÍ
SILNIC
A DÁLNIC**

Ředitelství silnic a dálnic s. p.
Čerčanská 2023/12, Krč, 140 00 Praha 4

Zhotovitel:



Valbek

Valbek, spol. s r.o.
Vaňurova 505/17
460 07 Liberec 3

	Vypracoval	ING. J. VANCL		Zak. číslo	21-LI13-001
	Zodp. projektant	ING. J. VANCL		Datum	02/2025
	Tech. kontrola	ING. D. LANDA		Stupeň	PDPS
	Akce I/16 MLADÁ BOLESLAV - MARTINOVICE			Počet formátů	2 x A4
				Měřítko	1 : 50
Zhotovitel: Valbek, spol. s r.o. Vaňurova 505/17 460 07 Liberec 3		Příloha VZOROVÝ PŘÍČNÝ ŘEZ		Č. přílohy 7	Paré