


SITUACE
M 1 : 500

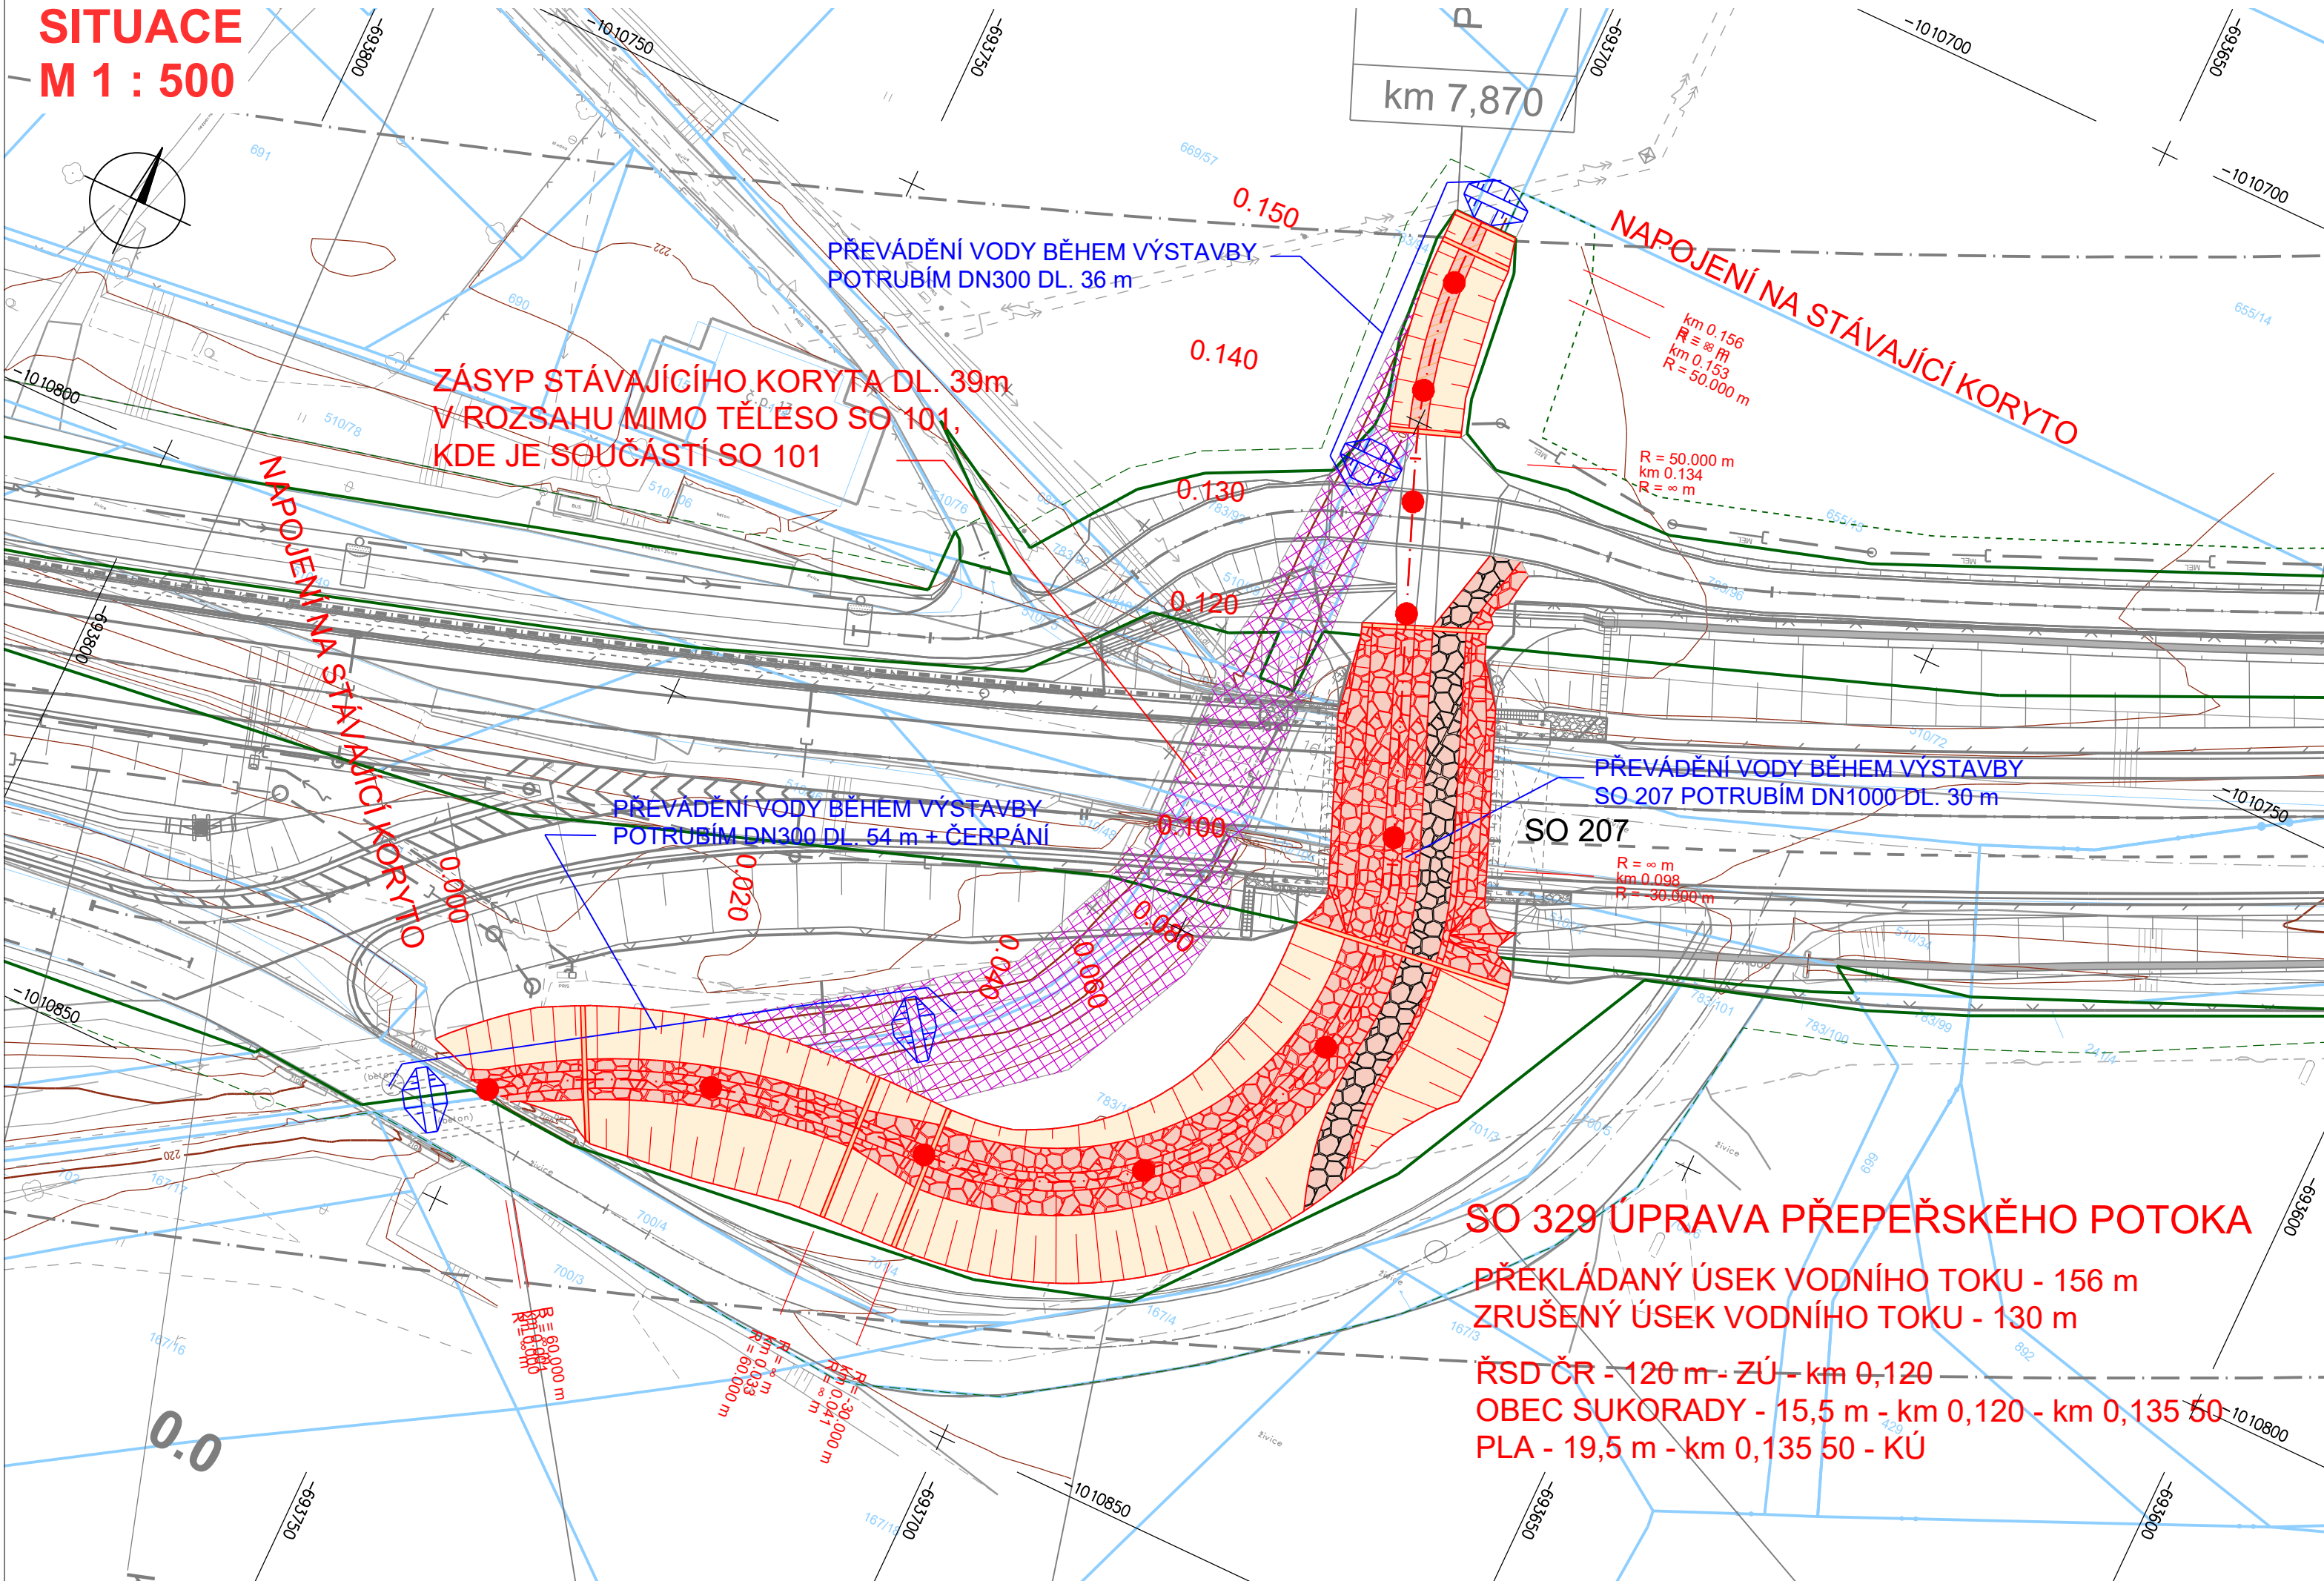

LEGENDA:

PLOCHY

- OHUMUSOVÁNÍ VÝKOP
- OHUMUSOVÁNÍ NÁSYP
- DLAŽBA Z LK DO BETONU
- POHOZ KAMENIVEM
- ROVNANINA Z LK
- ROVNANINA Z LK S OHUMUSOVÁNÍM
- PRÁH BETONOVÝ
- PRÁH Z LK NA CM
- BETONOVÉ KONSTRUKCE
- ŽB KONSTRUKCE
- SANACE STÁVAJÍCÍHO KORYTA

Souřadnicový systém: S-JTSK
Výškový systém: Bpv

SO 329 Úprava Přepeřského potoka

Objednatel:



ŘEDITELSTVÍ
SILNIC
A DÁLNIC

Ředitelství silnic a dálnic s. p.
Čerčanská 2023/12, Krč, 140 00 Praha 4

Zhotovitel:



Valbek

Valbek, spol. s r.o.
Vaňurova 505/17
460 07 Liberec 3

	Vypracoval	ING. J. VANCL		Zak. číslo	21-LI13-001
	Zodp. projektant	ING. J. VANCL		Datum	02/2025
	Tech. kontrola	ING. D. LANDA		Stupeň	PDPS
	Akce I/16 MLADÁ BOLESLAV - MARTINOVICE			Počet formátů	3 x A4
				Měřítko	1 : 500
Zhotovitel: Valbek, spol. s r.o. Vaňurova 505/17 460 07 Liberec 3	Příloha SITUACE			Č. přílohy	Paré
2					