
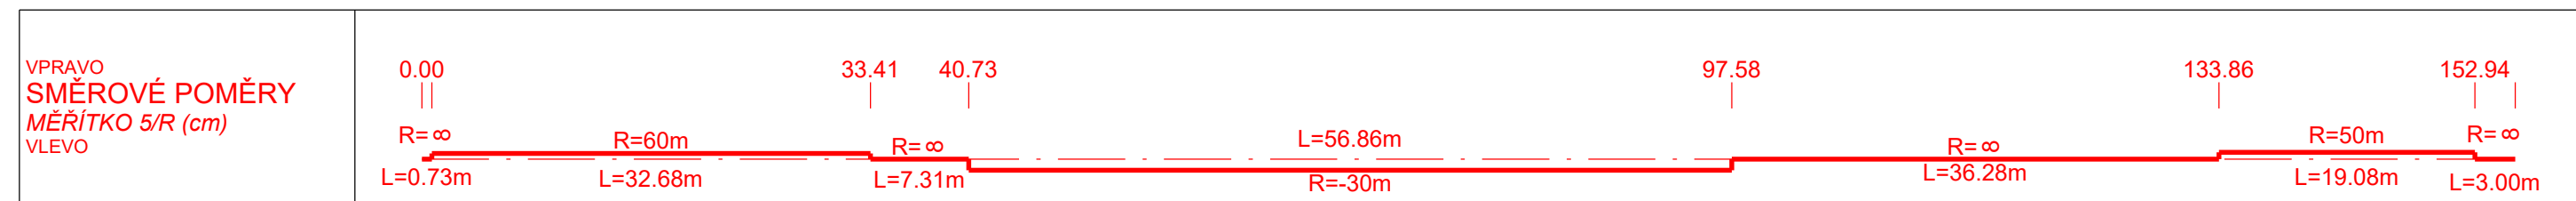


PODÉLNÝ PROFIL

M 1:500/100

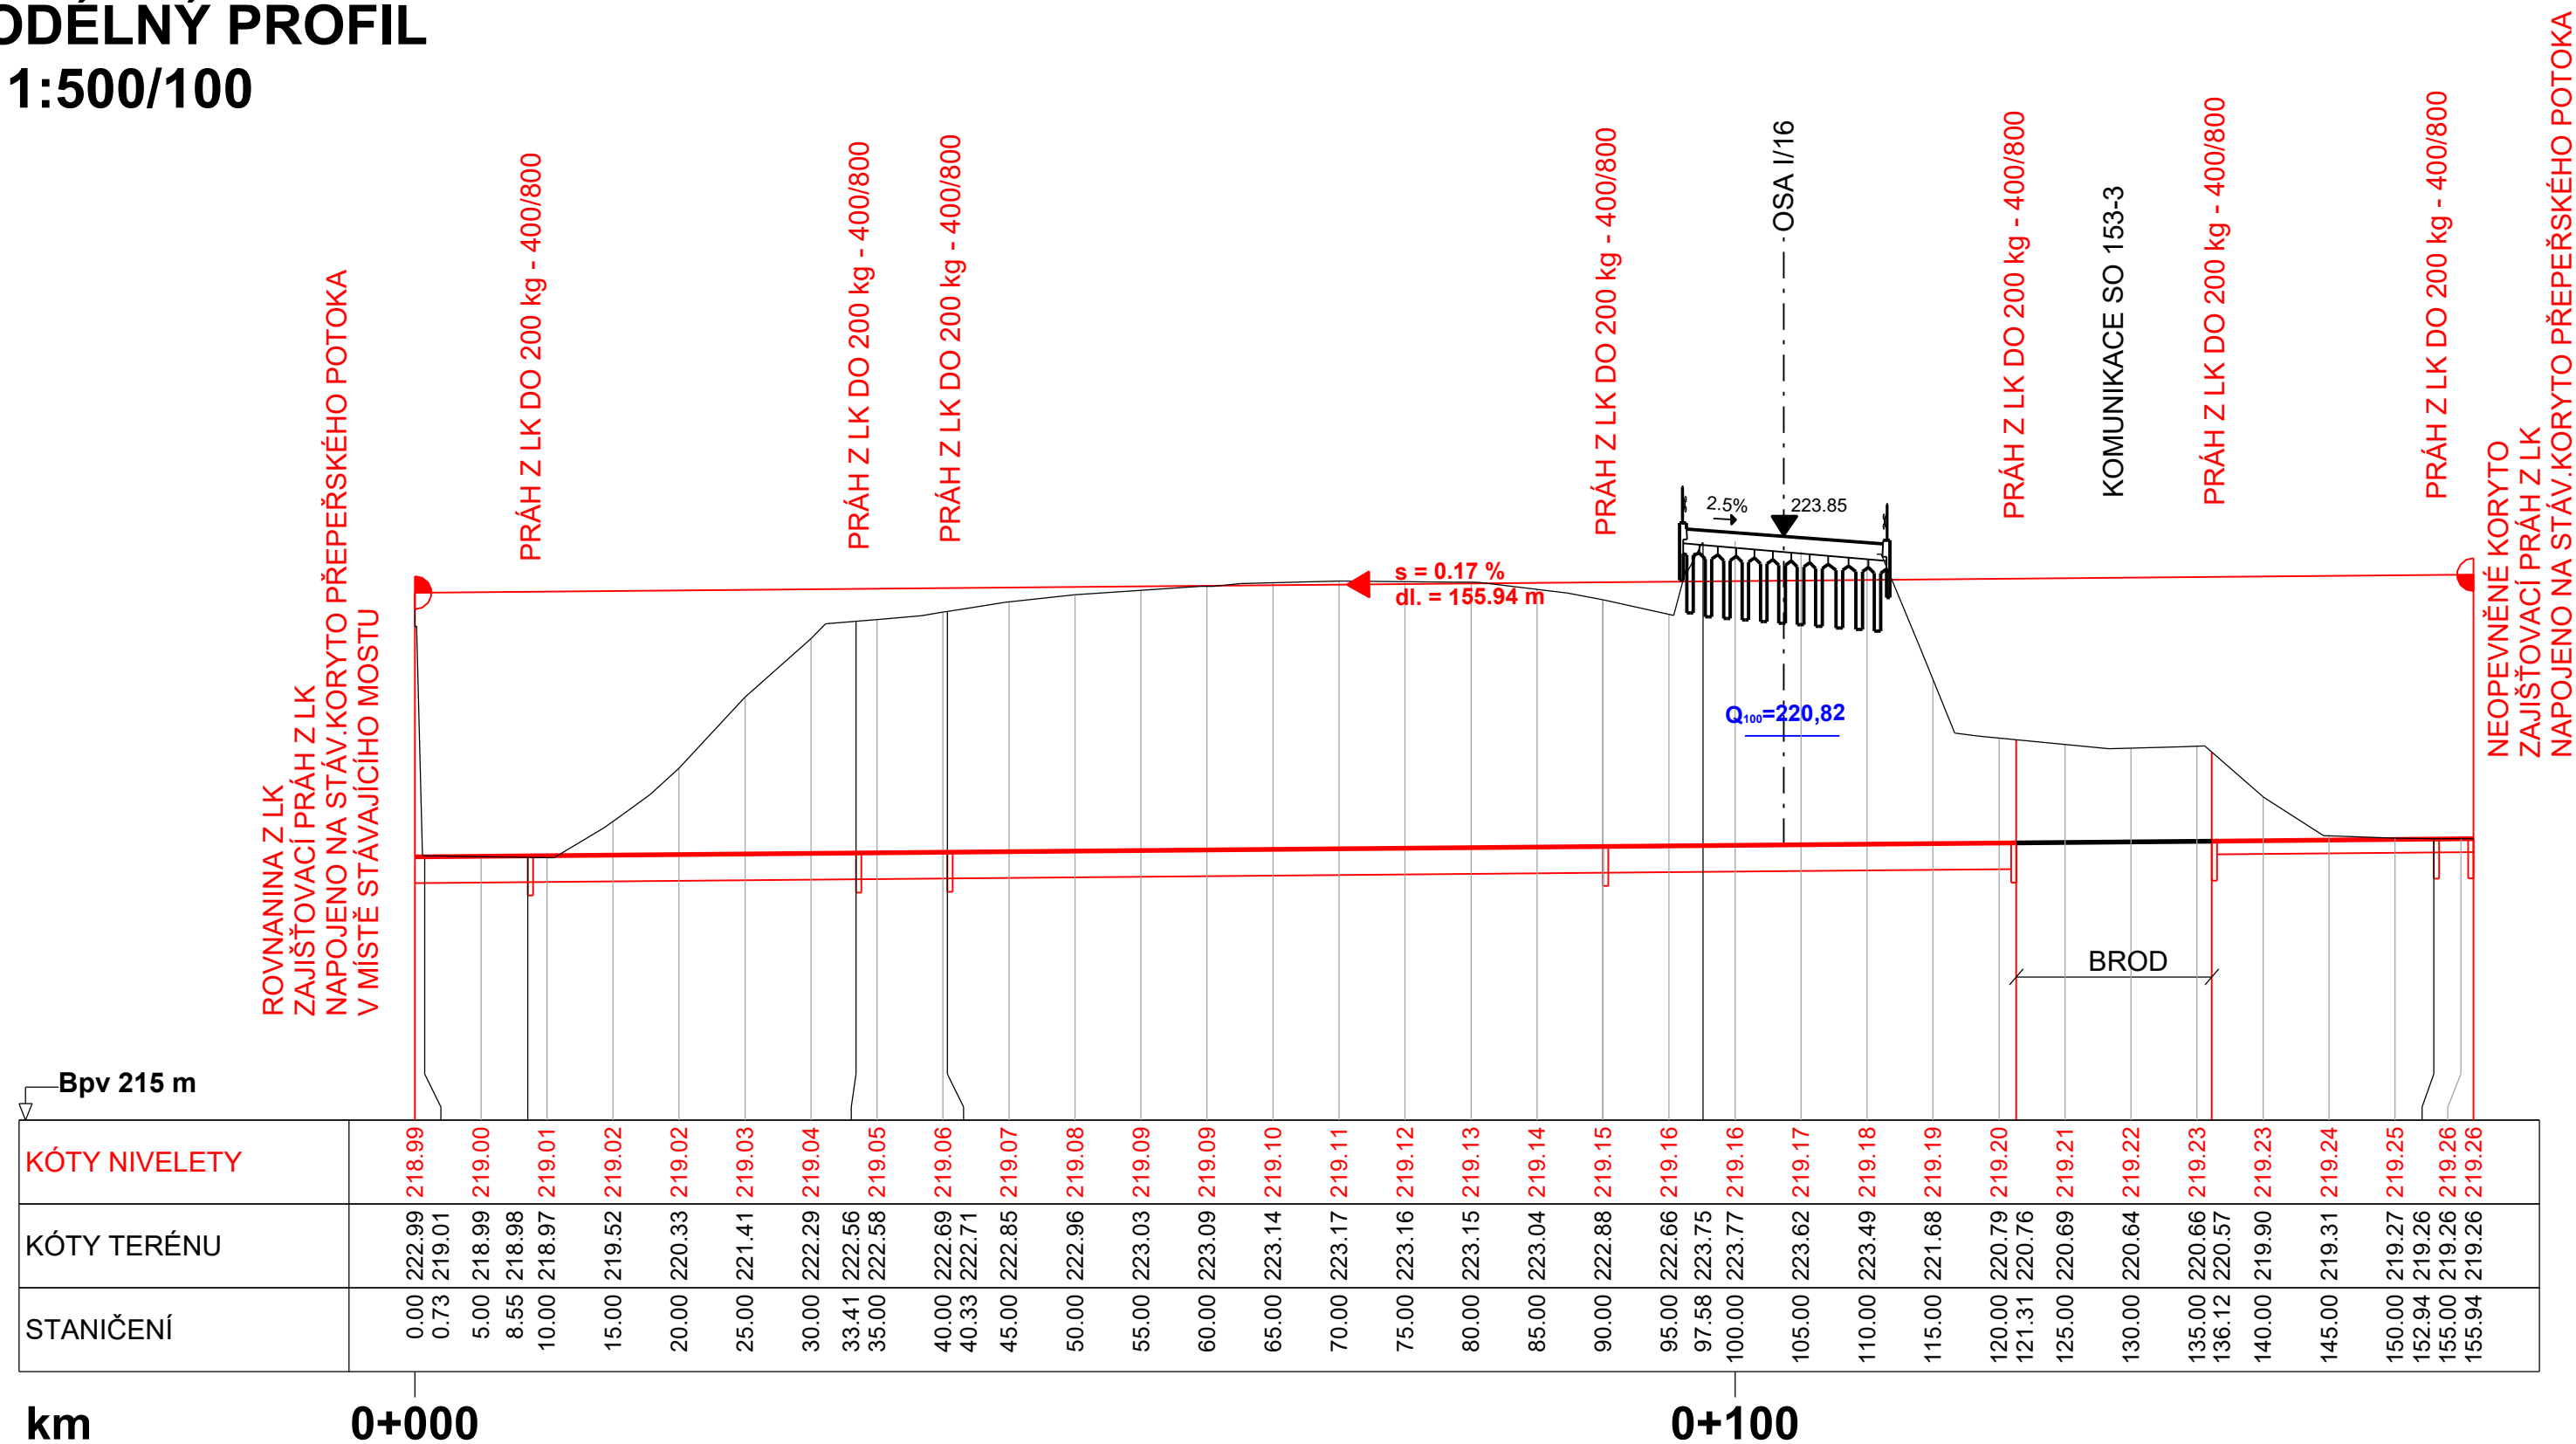

Souřadnicový systém: S-JTSK
Výškový systém: Bpv

SO 329	Úprava Přepeřského potoka
---------------	---------------------------

Objednatel:

ŘEDITELSTVÍ SILNIC A DÁLNIC

Ředitelství silnic a dálnic s. p.

Čerčanská 2023/12, Krč, 140 00 Praha 4

Zhotovitel:

**Valbek, spol. s r.o.**

Vaňurova 505/17
460 07 Liberec 3



Vypracoval	ING. J. VANCL
Zodp. projektant	ING. J. VANCL
Tech. kontrola	ING. D. LANDA

I/16 MLADÁ BOLESLAV - MARTINOVICE

Zak. číslo	21-LI13-001
------------	-------------

Datum	02/2025
-------	---------

Stupeň	PDPS
--------	------

Počet formátů	3 x A4
---------------	--------

Měřítko	1 : 500/100
---------	-------------

3

Zhotovitel:
Valbek, spol. s r.o.
Vaňurova 505/17
460 07 Liberec 3

	Příloha
--	----------------

PODÉLNÝ PROFIL