


VZOROVÉ PŘÍČNÉ ŘEZY


M 1:50

VZOROVÝ ŘEZ OPEVNĚNÝM KORYTEM
OPEVNĚNÍ - ROVNANINA Z LOMOVÉHO KAMENE


PLATNOST: KM ŽÚ- 0,040 72
0,136 12 - 0,152 94

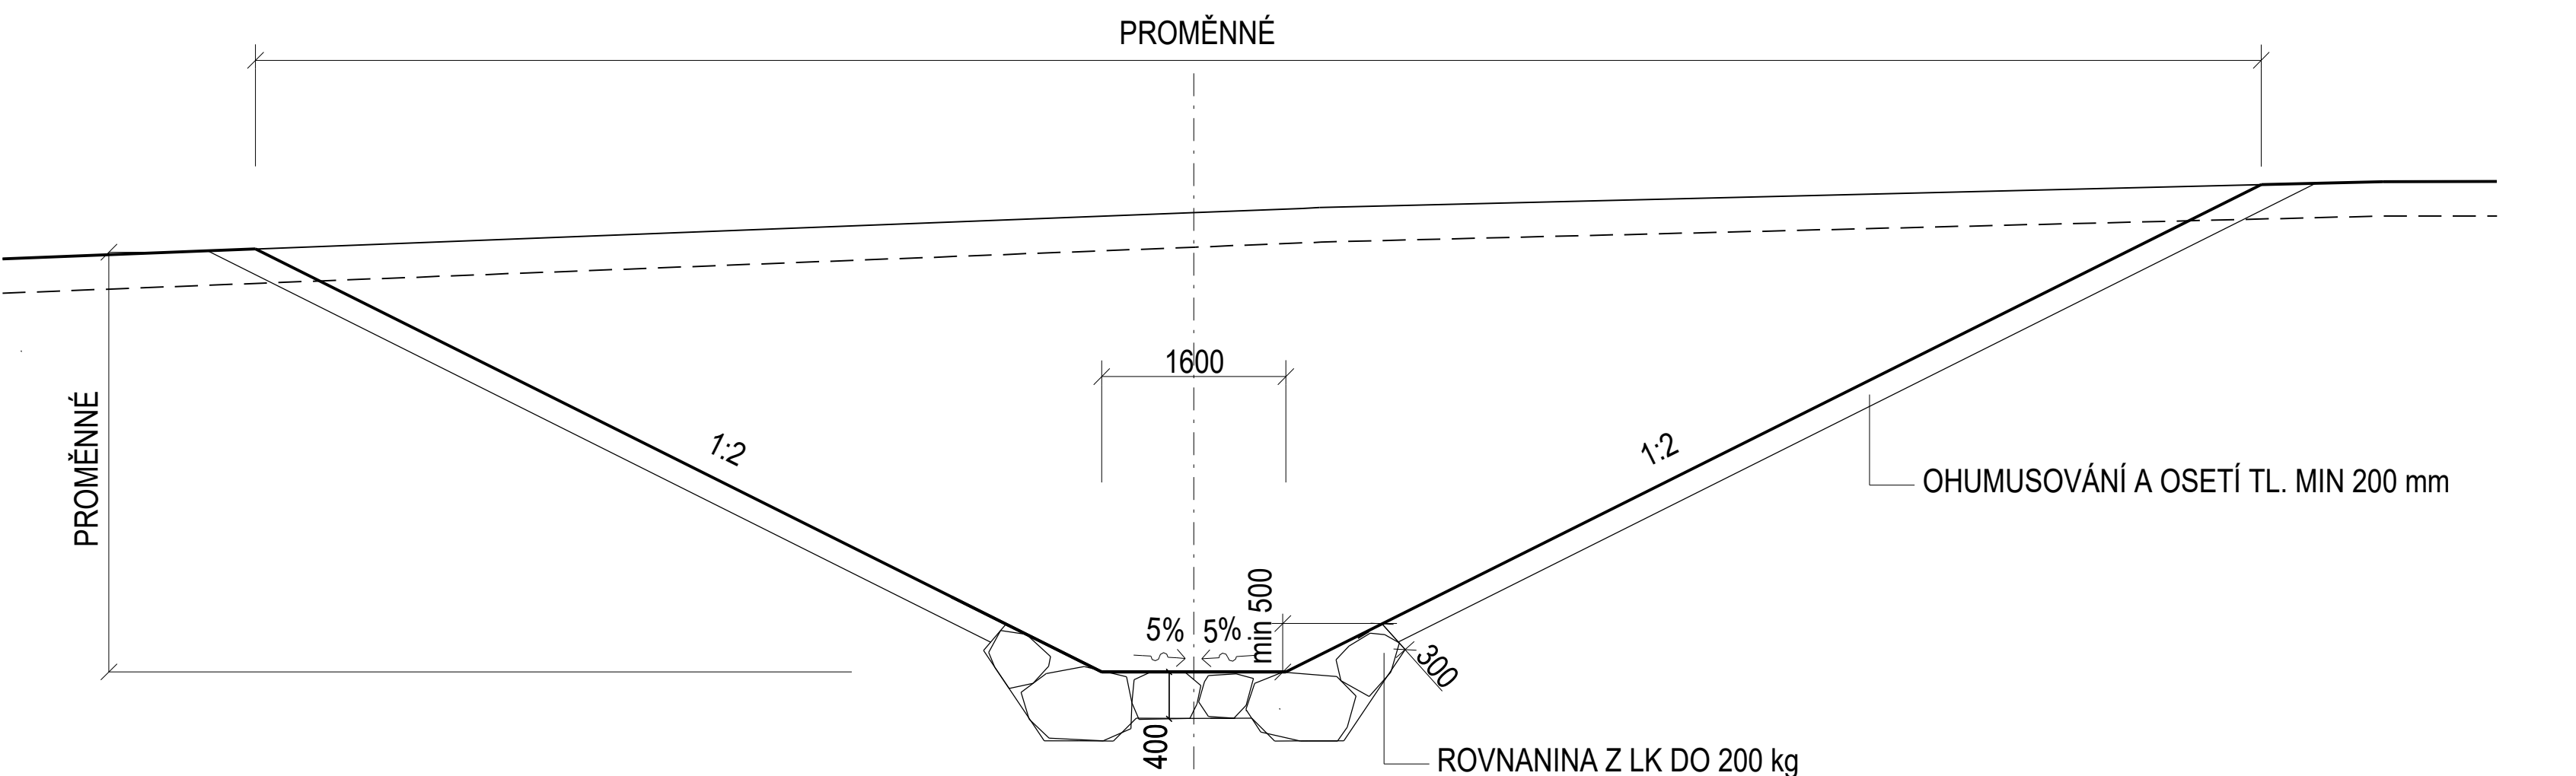


PROVÝ ŘEZ NEOPEVNĚNÝM KORYTEM
TUNOST: KM 0,152 94 - KÚ

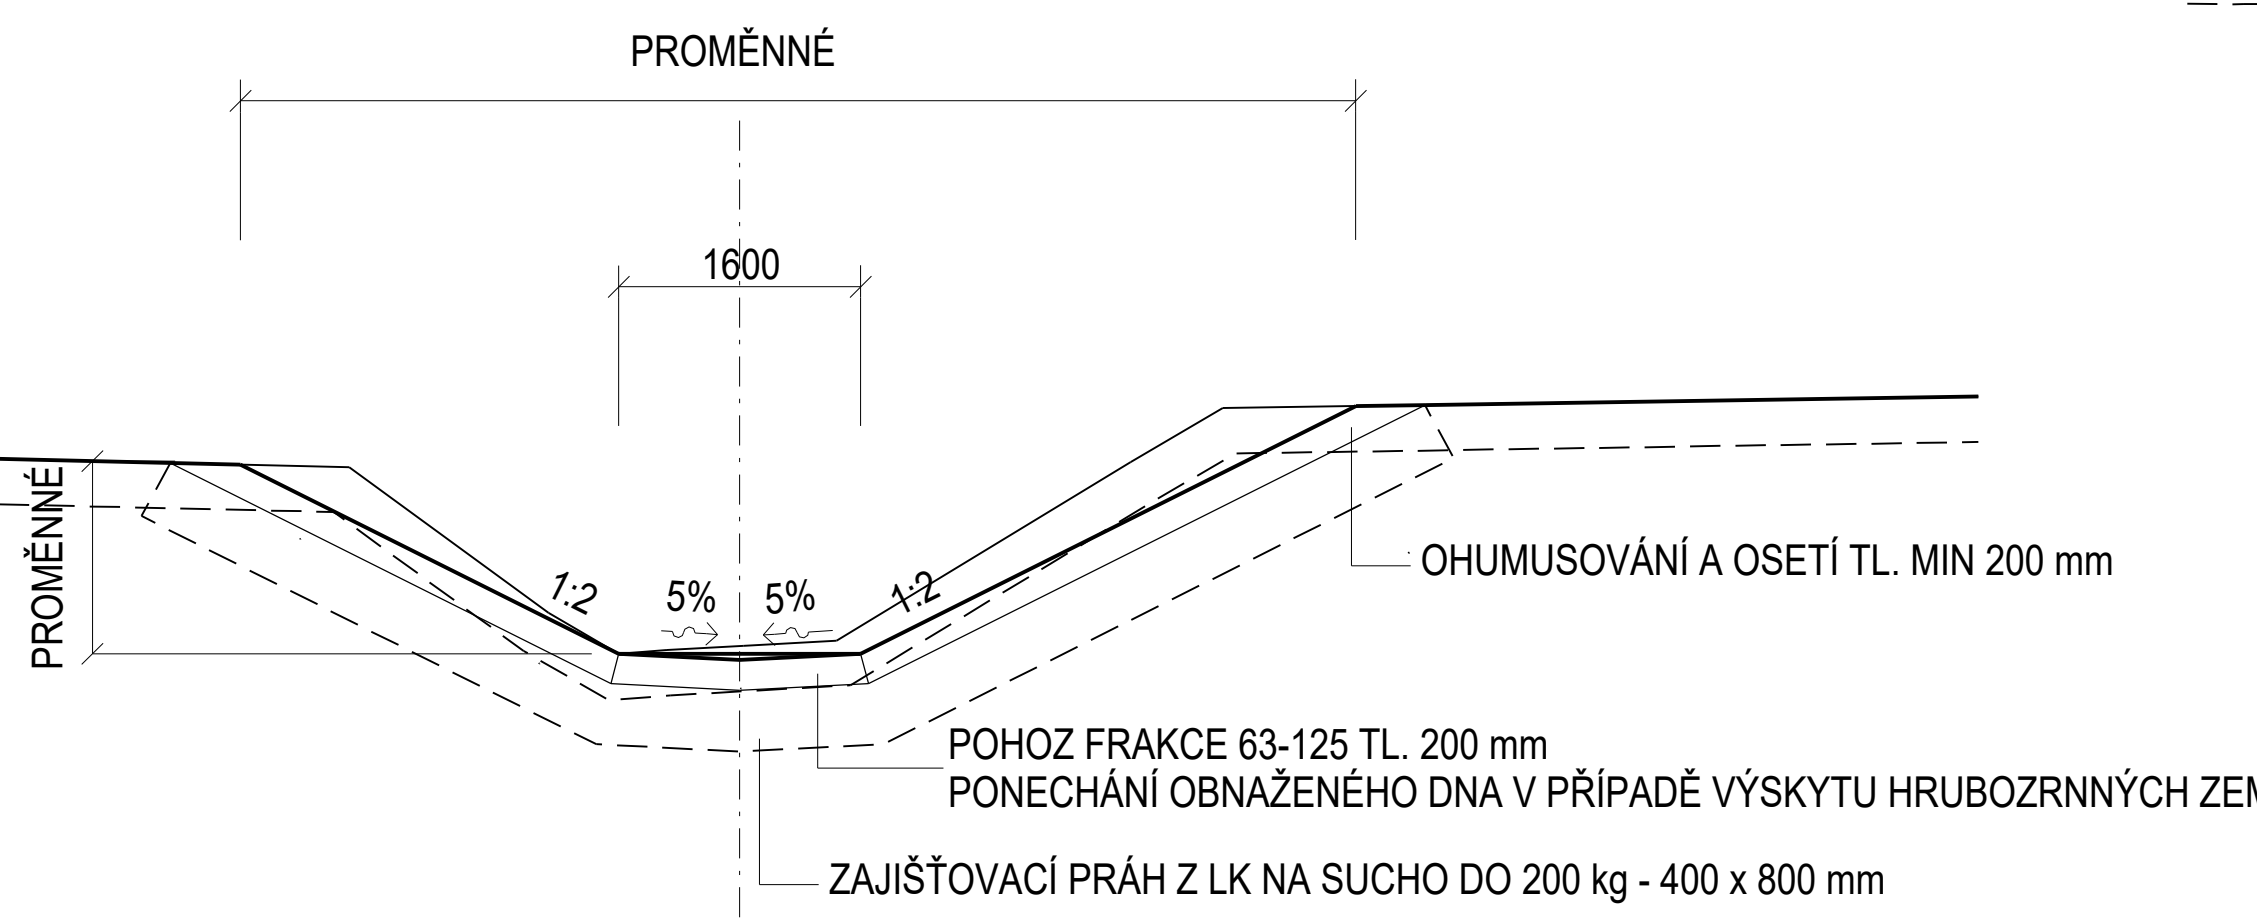

PROVÝ ŘEZ OPEVNĚNÝM KORYTEM S BERMOU
EVNĚNÍ - ROVNANINA Z LOMOVÉHO KAMENE
TNOST: KM 0,040 72 - 0,121 31

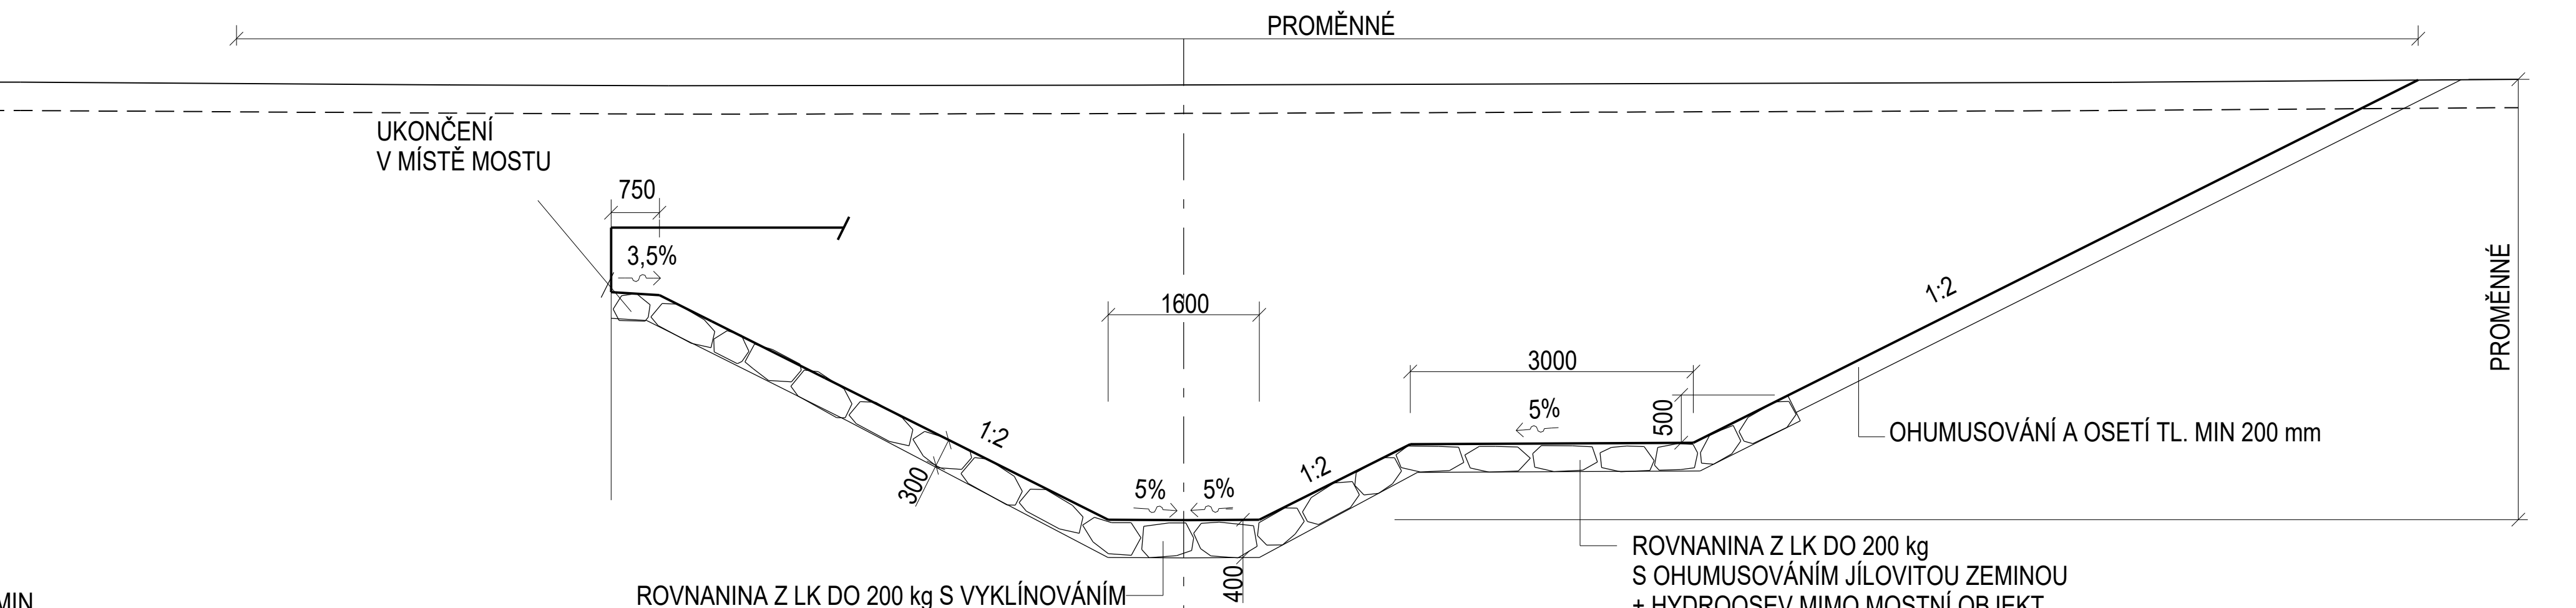

PLATNOST: KM 0,121 31 - 0,136 12

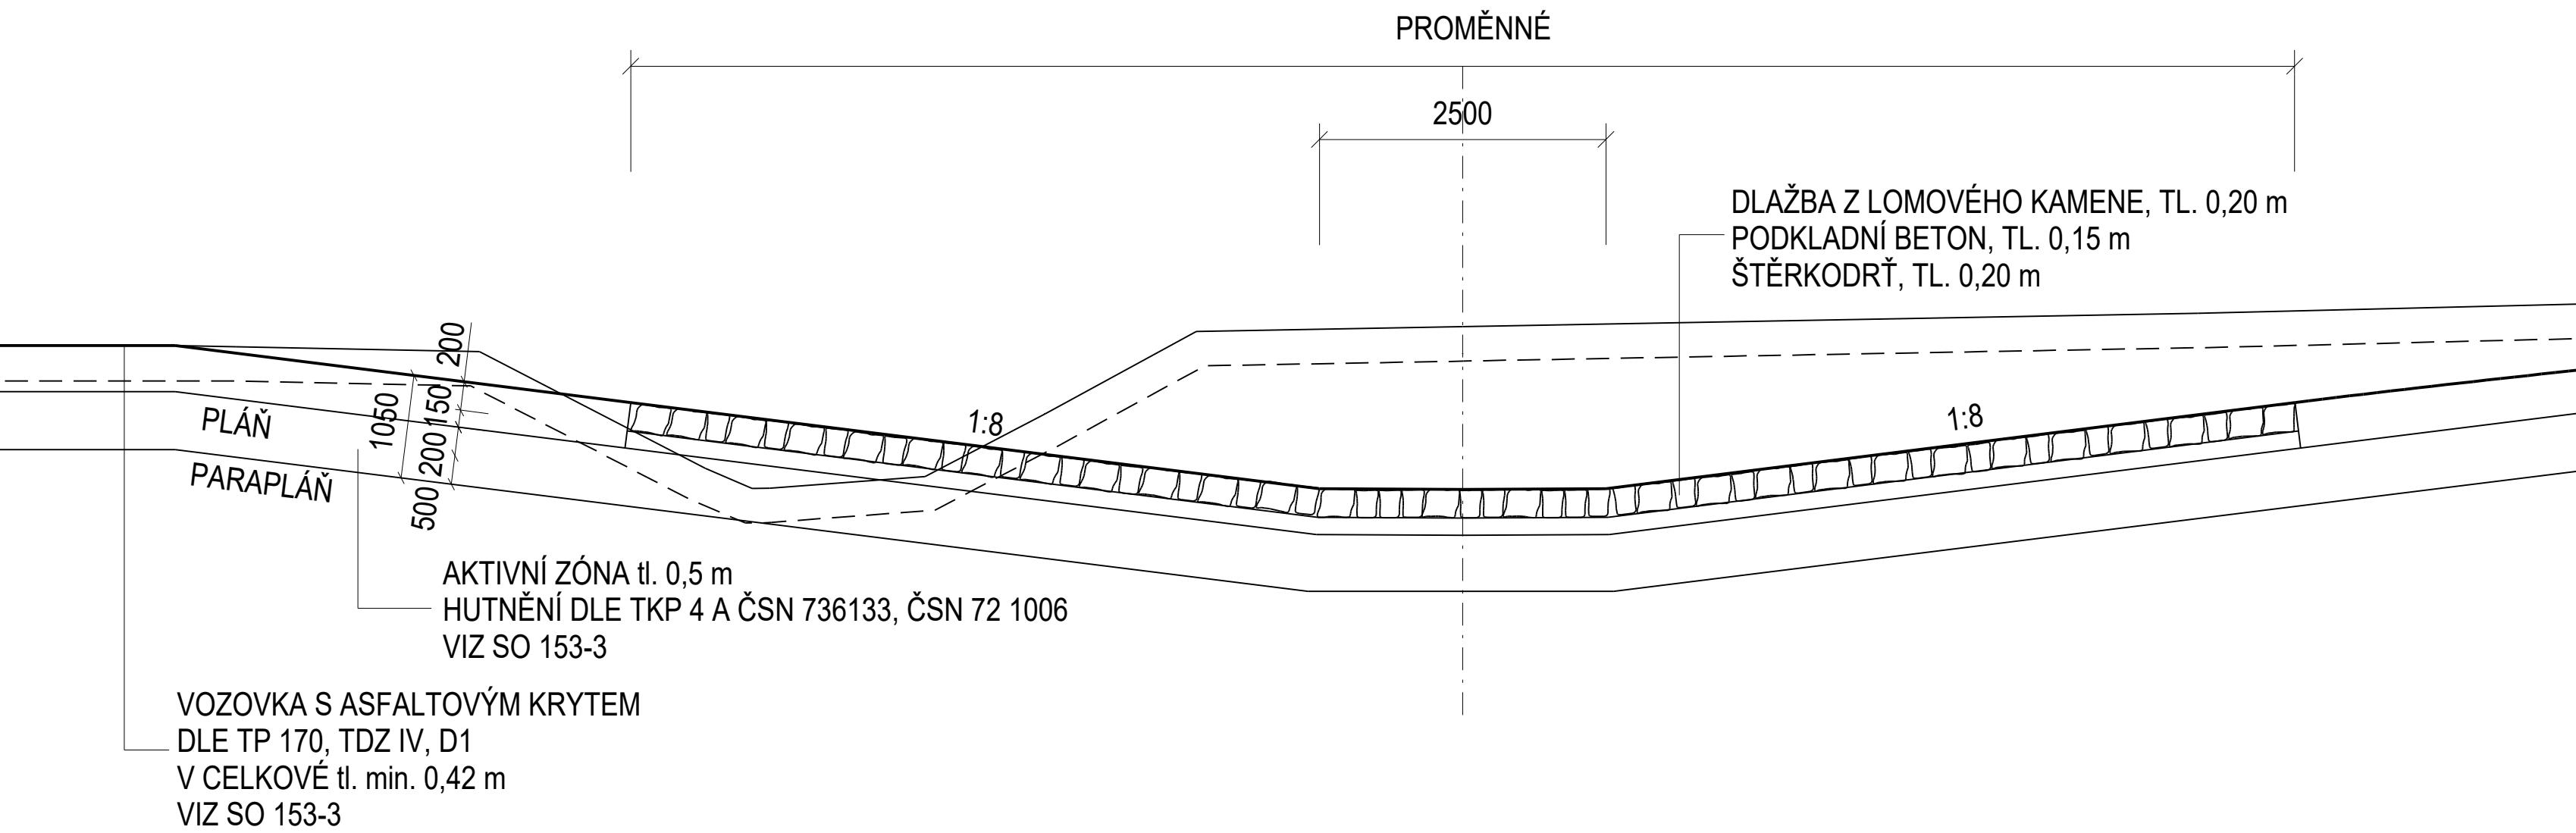

Souřadnicový systém: S-JTSK
Výškový systém: Bpv

SO 329	Úprava Přepeřského potoka
---------------	---------------------------

Objedn:




Ředitelství silnic a dálnic
Čerčanská 2023/12, Krč, 140 00 Praha

Zhotov



Valbek, spol. s r. o.
Vaňurova 505/17
460 07 Liberec 3

 	Vypracoval	ING. J. VANCIL		Zak. číslo	20
	Zodp. projektant	ING. J. VANCIL		Datum	2017
	Tech. kontrola	ING. D. LANDA		Stupeň	F
	Akce			Počet formátů	1
I/16 MLADÁ BOLESLAV - MARTINOVICE					
Zhotovitel: Valbek, spol. s r.o. Valbarkova 505/17 460 07 Liberec 3	Příloha	VZOROVÉ PŘIČNÉ REZY			4
		Měřítko			
		Č. přílohy			