

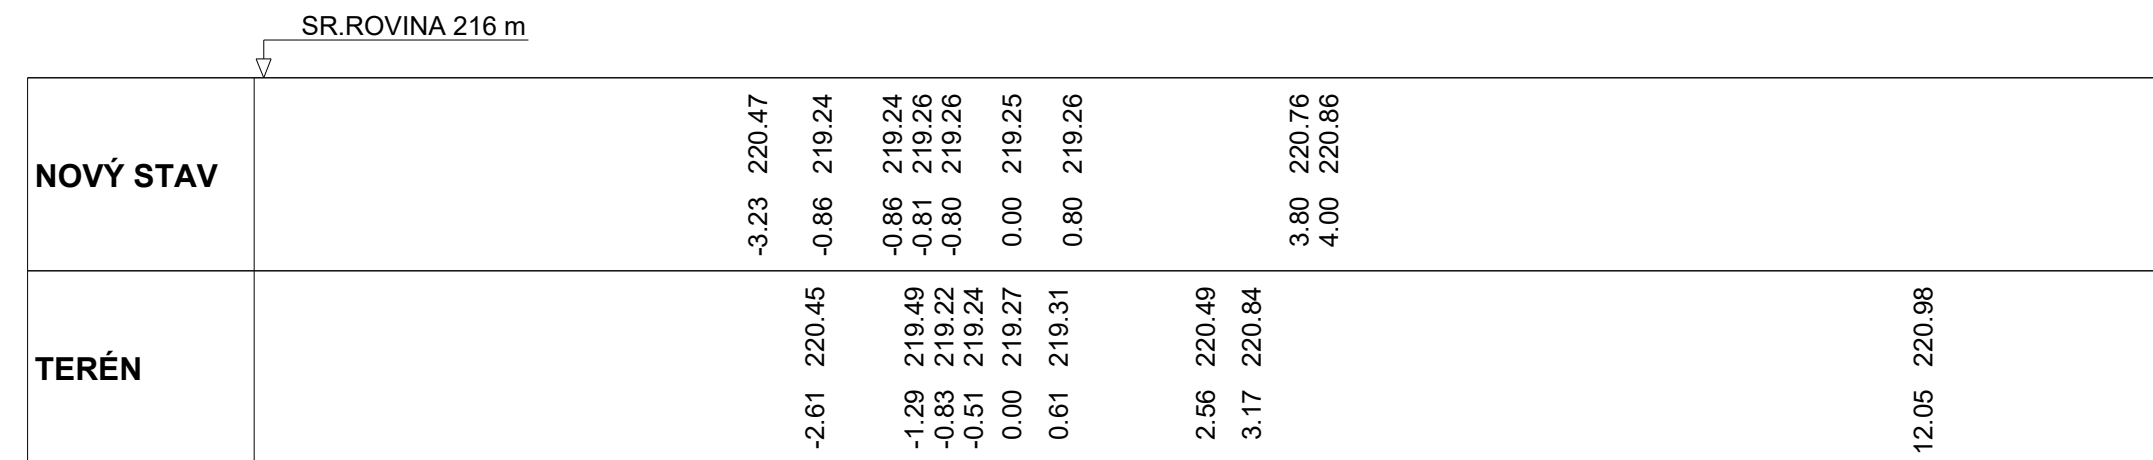
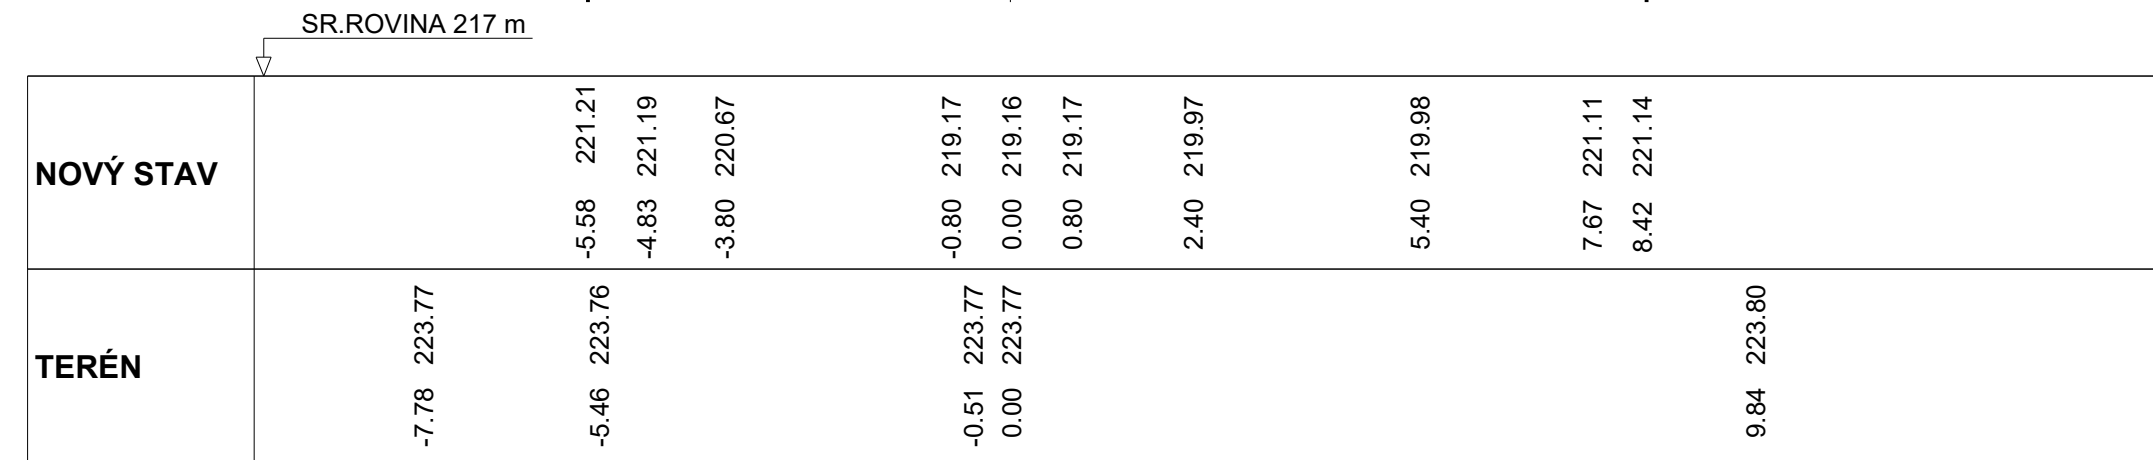
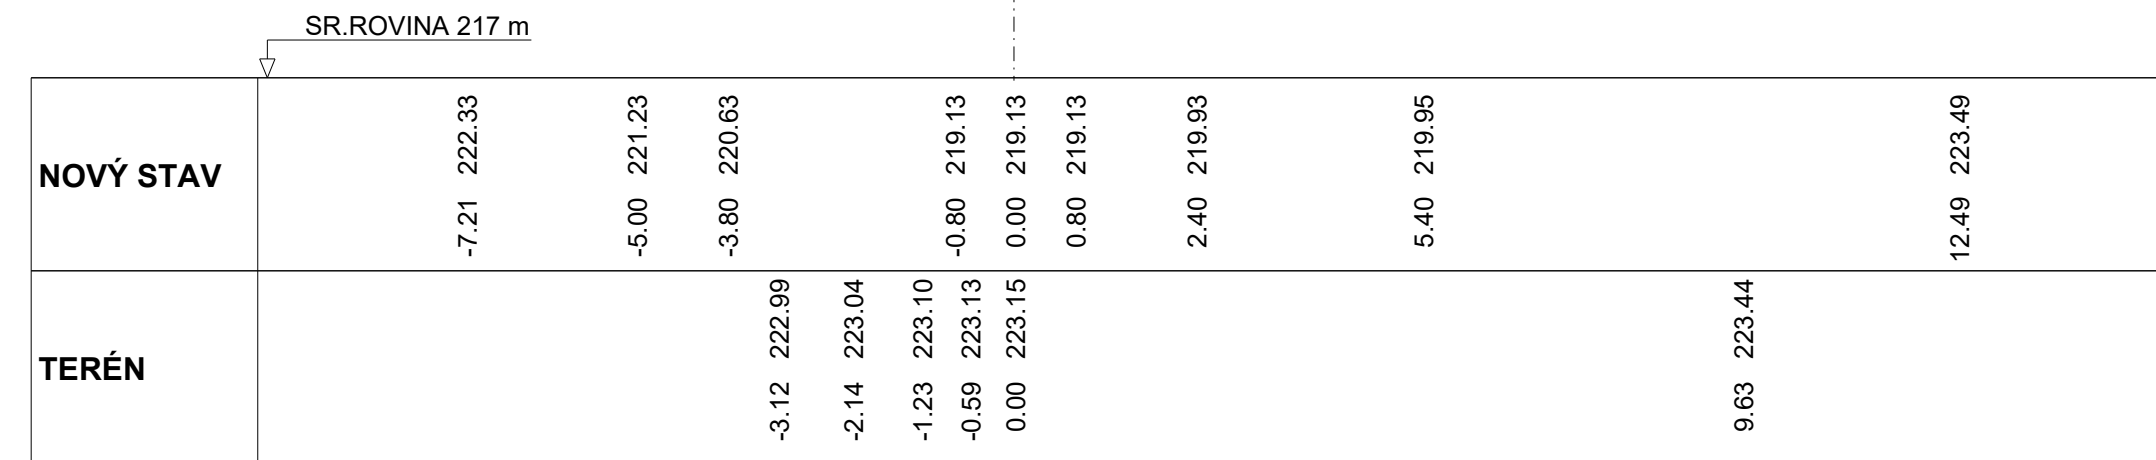
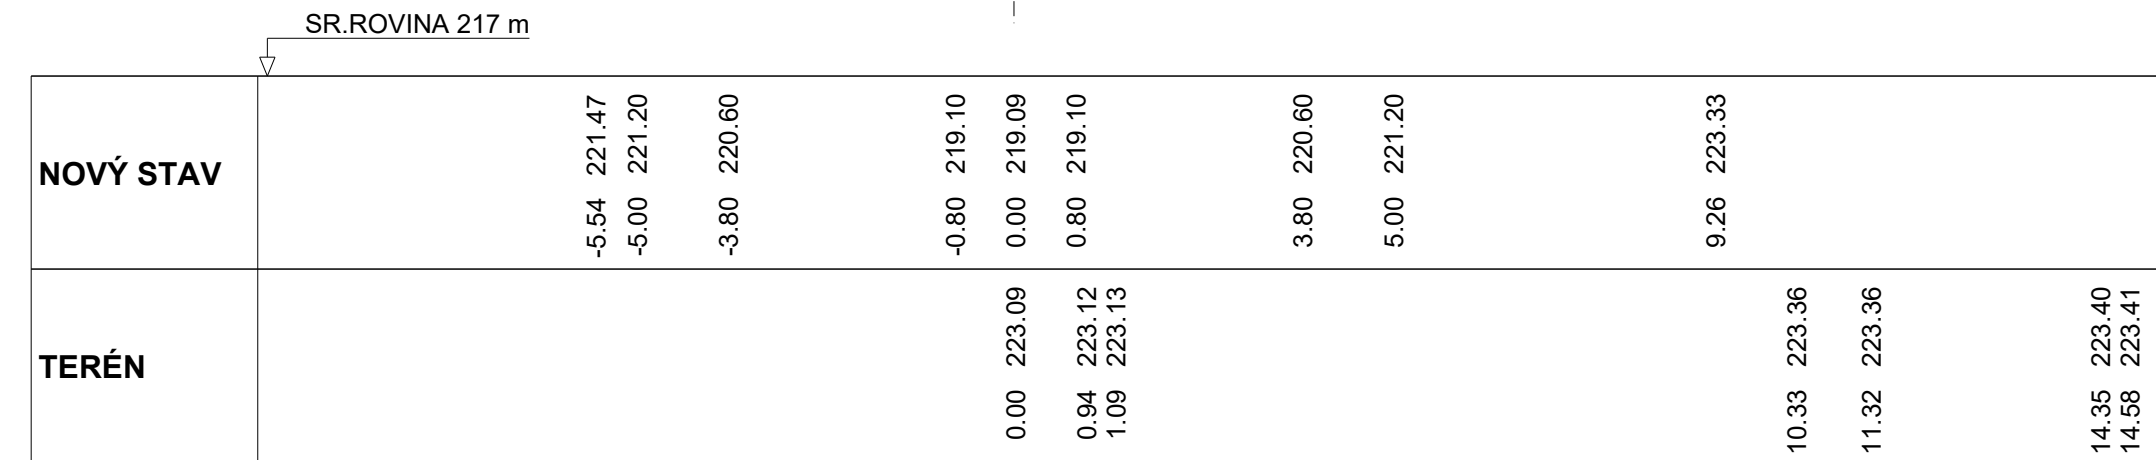


ŘEZY JSOU PROTI SMĚRU TOKU

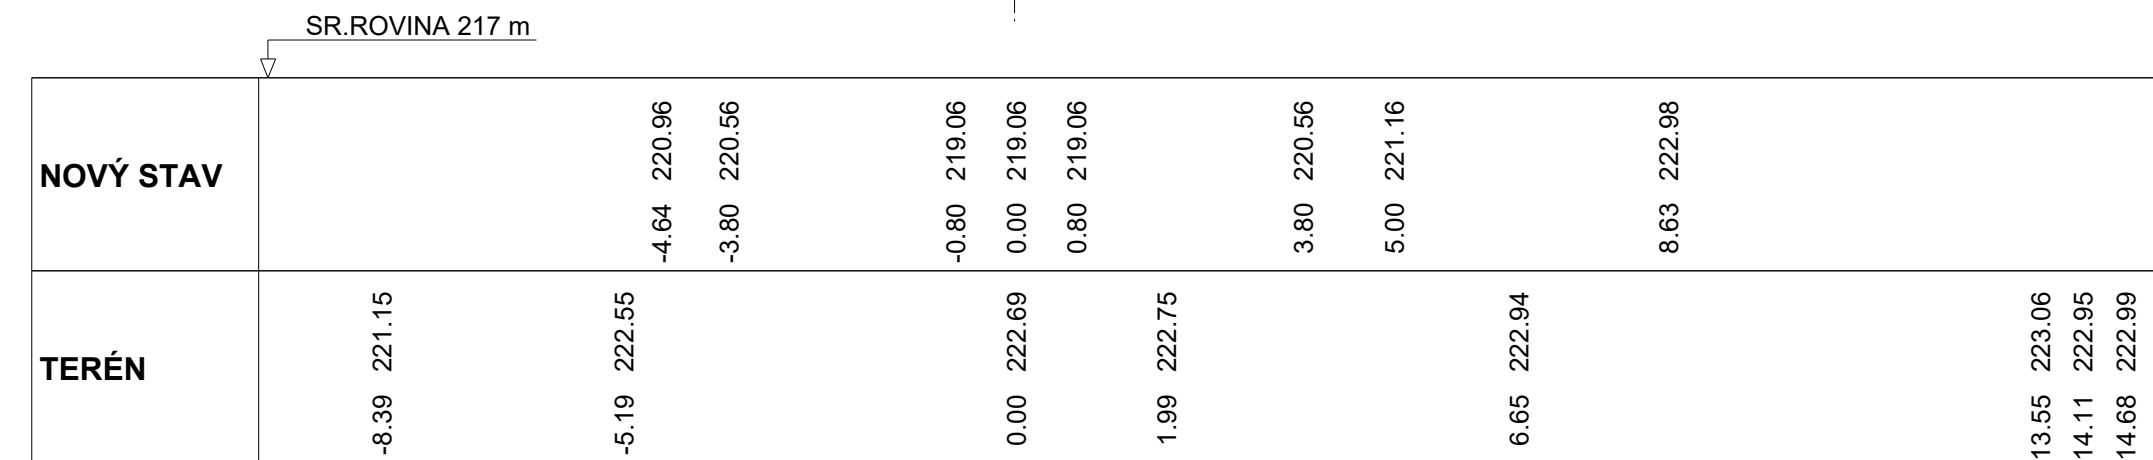

SO 329 Úprava Přepeřského potoka

Čerčanská 2023/12, Krč, 140 00 Praha 4

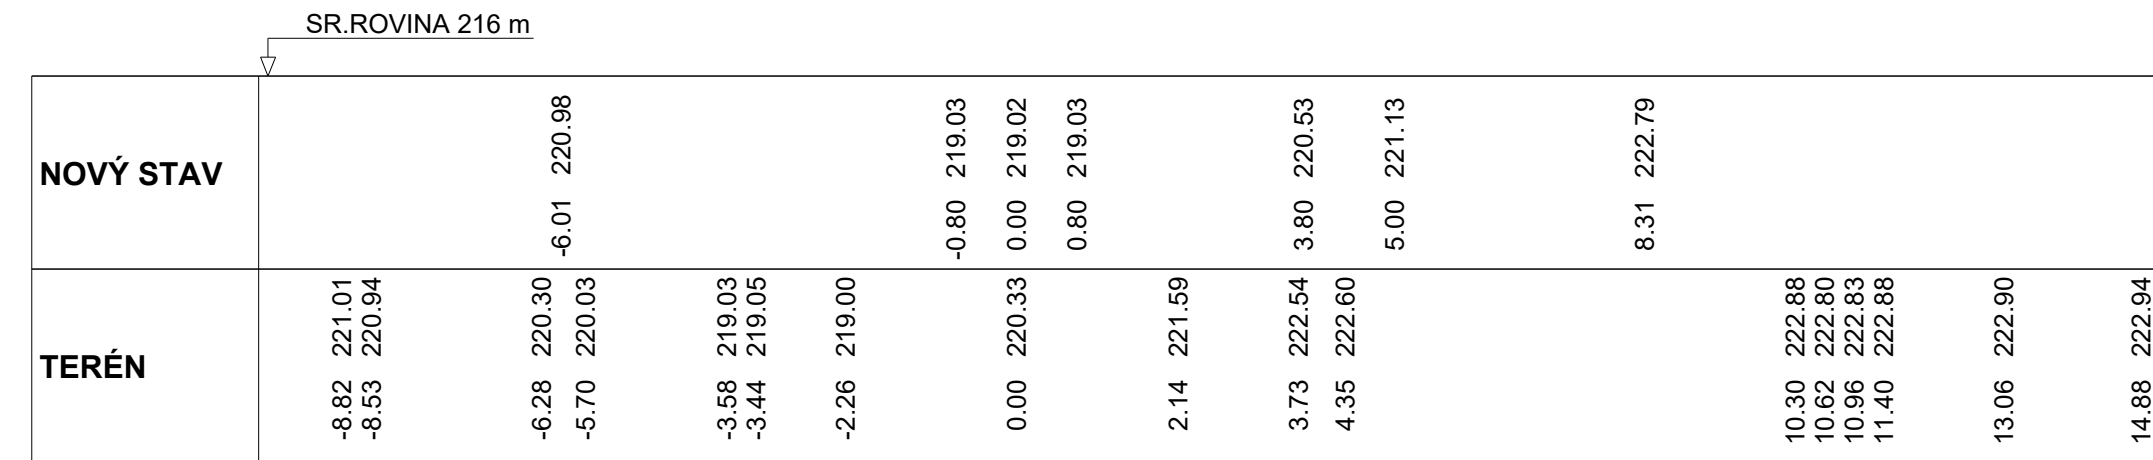

Vaňurova 505/17
460 07 Liberec 3

	Vypracoval	ING. J. VANCL		Zak. číslo	21-LI13-001	
	Zodp. projektant	ING. J. VANCL		Datum	02/2025	
	Tech. kontrola	ING. D. LANDA		Stupeň	PDPS	
	Akce	I/16 MLADÁ BOLESLAV - MARTINOVICE			Počet formátů	6 x A4
	Příloha				Měřítka	1 : 100
Zhotovitel: Valbek, spol. s r.o. Vašurkova 505/17 460 07 Liberec 3			PŘÍČNÉ ŘEZY	5	Č. přílohy	Paré