


SO 341
SITUACE M 1 : 500
POTRUBÍ DN 100 (110 x 10,0) mm HPDE 100 RC SDR11 (s ochr. pláštěm) DL. 650,3 m
POTRUBÍ TLT DN 100 min. CLASS 100 DL. 37 m (V CHRÁNIČCE)
CHRÁNIČKA OC DN 300 DL. 36,0 m



LEGENDA

STÁVAJÍCÍ IS - INFORMATIVNÍ ZÁKRES

- STÁVAJÍCÍ VODOVOD
- STÁVAJÍCÍ TLAKOVÁ KANALIZACE
- STÁVAJÍCÍ KANALIZACE JEDNOTNÁ
- STÁVAJÍCÍ NTL
- PLYNOVOD - STL
- STÁVAJÍCÍ VTL
- PODZEMNÍ VEDENÍ NN
- PODZEMNÍ VEDENÍ VN
- STÁVAJÍCÍ PODZEMNÍ VEDENÍ VVN
- NADZEMNÍ VEDENÍ NN
- NADZEMNÍ VEDENÍ VN
- NADZEMNÍ VEDENÍ VVN
- PODZEMNÍ SDĚLOVACÍ VEDENÍ
- STÁVAJÍCÍ SDĚL. VEDENÍ NADZ.

Souřadnicový systém: S-JTSK
Výškový systém: Bpv

SO 341 Přeložka vodovodu PE 110 v km 2,195

Objednatel:



Ředitelství silnic a dálnic s. p.
Čerčanská 2023/12, Krč, 140 00 Praha 4

Zhotovitel:



Valbek, spol. s r.o.
Vaňurova 505/17
460 07 Liberec 3

	Vypracoval	BC. Š. HORECKÝ	Zak. číslo	21-L113-001
	Z odp. projektant	ING. J. VANCL	Datum	02/2025
	Tech. kontrola	ING. D. LANDA	Stupeň	PDPS
	Akce	I/16 MLADÁ BOLESLAV - MARTINOVICE		Počet formátů 8 x A4
Zhotovitel: Valbek, spol. s r.o. Vaňurova 505/17 460 07 Liberec 3	Příloha SITUACE		Měřítko 1 : 500	Č. přílohy Paré
			2	