

341

[1:1000/100]

KÓTA UPRAVENÉHO TERÉNU

HLOUBKA VÝKOPU

HLOUBKA DNA POTRUBÍ

KÓTA DNA POTRUBÍ

KÓTA STÁVAJÍCÍHO TERÉNU


HLOUBKA OD NOVÉHO TERÉNU

STANIČENÍ [km]

STANIČENÍ [m]

SKLON ‰ - DÉLKA v m

DN - MATERIÁL - DÉLKA v m

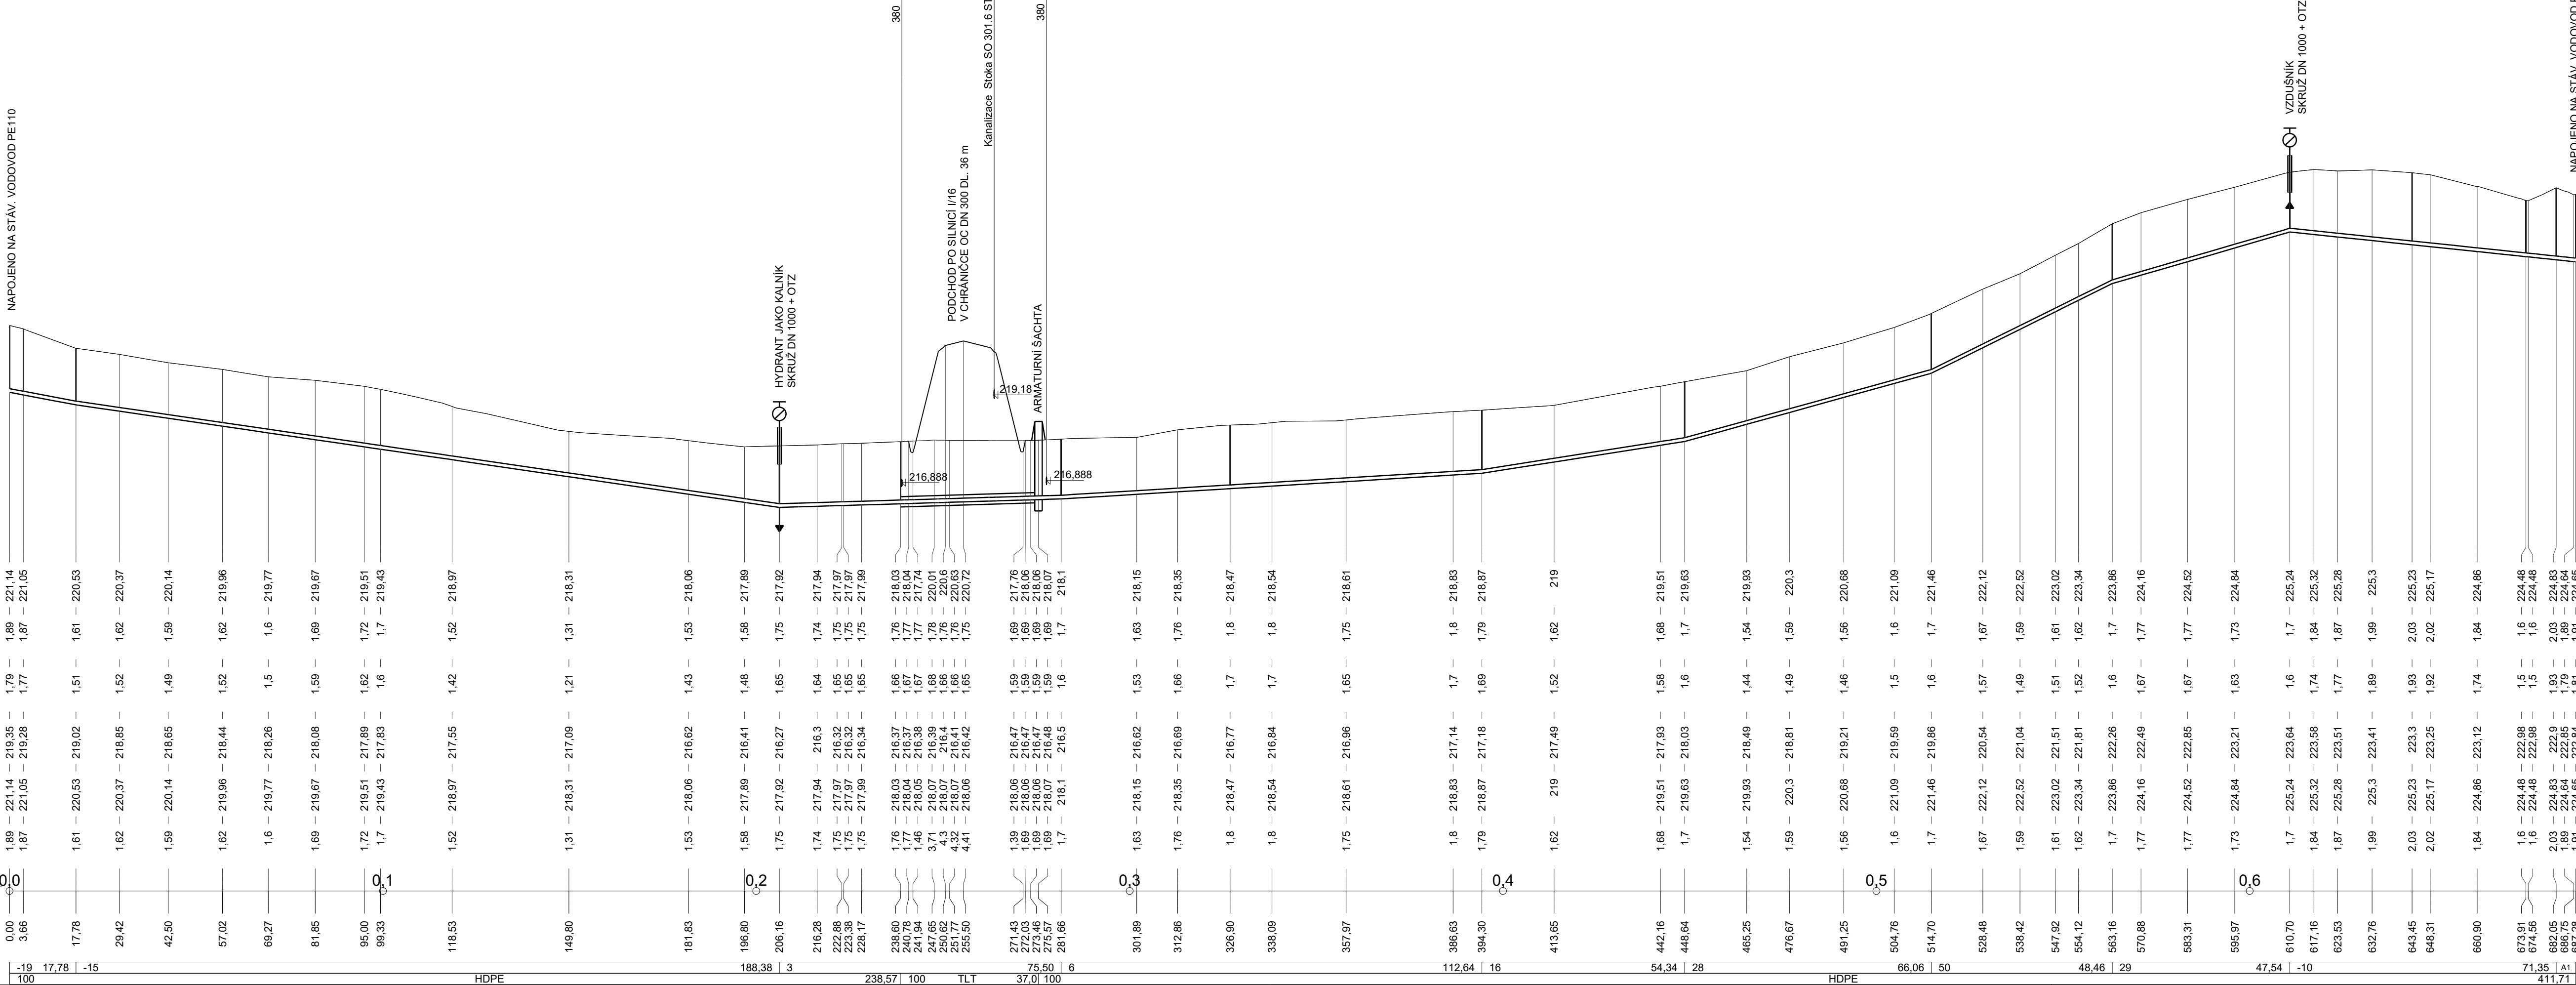

Souřadnicový systém: S-JTSK
Výškový systém: Bpv

SO 341

Přeložka vodovodu PE 110 v km 2,195

Objednatel:



ŘEDITELSTVÍ
SILNIC
A DÁLNIC

Ředitelství silnic a dálnic s. p.
Čerčanská 2023/12, Krč, 140 00 Praha 4

Zhotovitel:



Valbek

Valbek, spol. s r.o.
Vaňurova 505/17
460 07 Liberec 3

	Vypracoval	BC. Š. HORECKÝ		Zak. číslo	21-L113-001
	Zodp. projektant	ING. J. VANCL		Datum	02/2025
	Tech. kontrola	ING. D. LANDA		Stupeň	PDPS
	Akce I/16 MLADÁ BOLESLAV - MARTINOVICE			Počet formátů	5 x A4
				Měřítko	1 : 1000 / 100
Zhotovitel: Valbek, spol. s r.o. Vaňurova 505/17 460 07 Liberec 3	Příloha PODÉLNÝ PROFIL			Č. přílohy	Paré
3					