


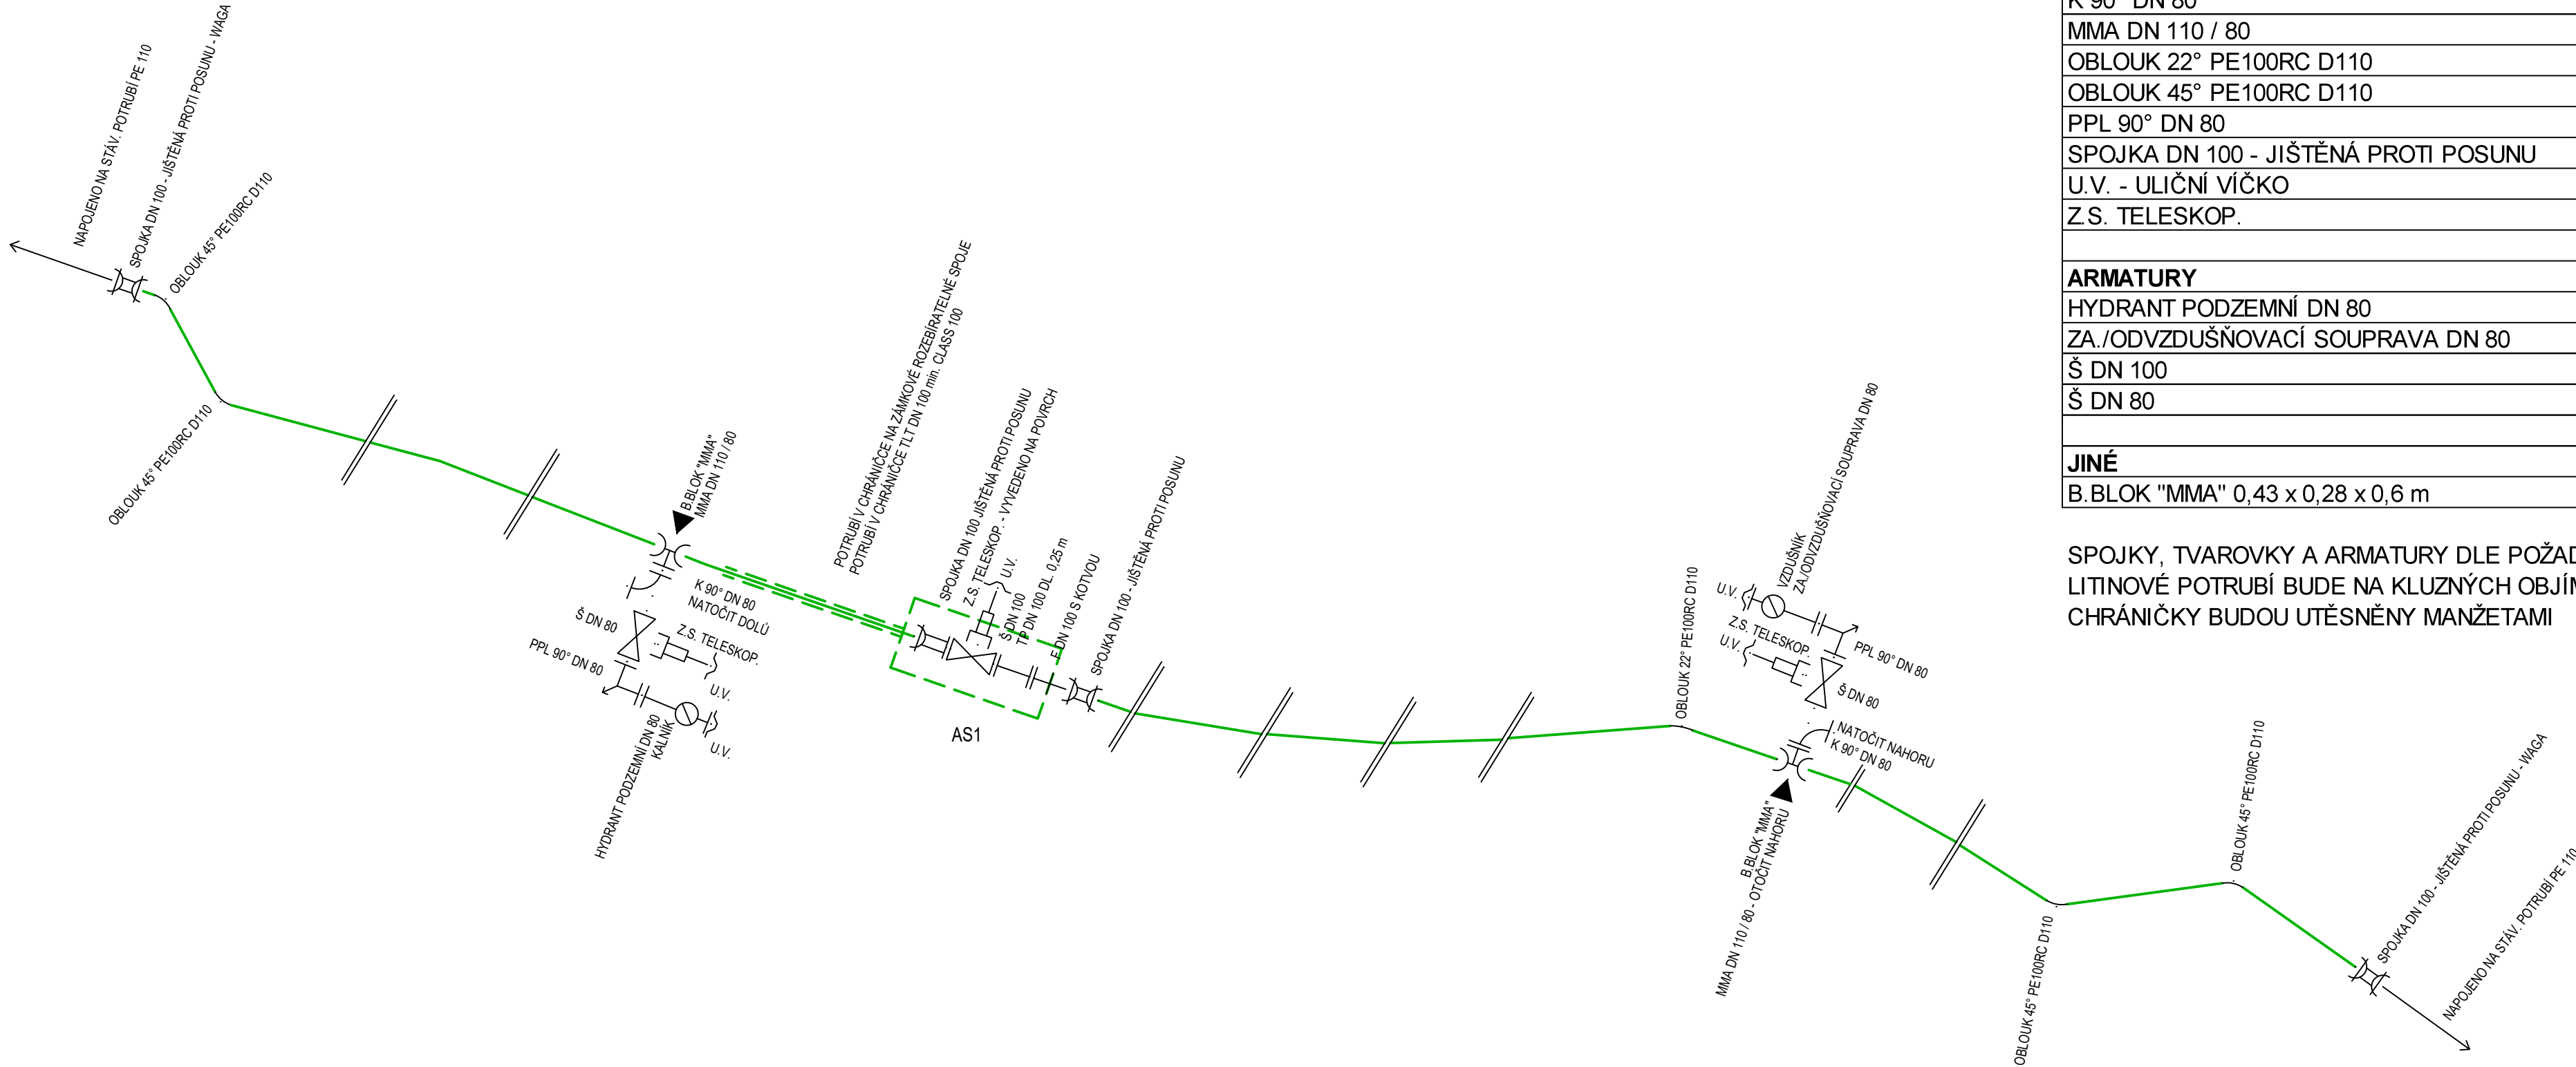

POTRUBÍ, TVAROVKY A ARMATURY	Počet	Jednotka
POTRUBÍ		
POTRUBÍ DN 100 (110 x 10,0) mm HPDE 100 RC SDR11 (s ochr. pláštěm)	650,3	m
POTRUBÍ TLT DN 100 min. CLASS 100	37,0	m
CHRÁNIČKA OC DN 300 (tl. stěny 10 mm)	36,0	m
TVAROVKY		
TP DN 100 DL. 0,25 m	1	ks
SPOJKA DN 100 - JIŠTĚNÁ PROTI POSUNU - S PŘÍRUBOU	1	ks
F DN 100 S KOTVOU	1	ks
K 90° DN 80	2	ks
MMA DN 110 / 80	2	ks
OBLOUK 22° PE100RC D110	1	ks
OBLOUK 45° PE100RC D110	4	ks
PPL 90° DN 80	2	ks
SPOJKA DN 100 - JIŠTĚNÁ PROTI POSUNU	3	ks
U.V. - ULIČNÍ VÍČKO	5	ks
Z.S. TELESKOP.	3	ks
ARMATURY		
HYDRANT PODZEMNÍ DN 80	1	ks
ZA./ODVZDUŠŇOVACÍ SOUPRAVA DN 80	1	ks
Š DN 100	1	ks
Š DN 80	2	ks
JINÉ		
B.BLOK "MMA" 0,43 x 0,28 x 0,6 m	2	ks

SPOJKY, TVAROVKY A ARMATURY DLE POŽADAVKU PROVOZOVATELE
LITINOVÉ POTRUBÍ BUDE NA KLIZNÝCH OBJÍMKÁCH PO 1 METRU
CHRÁNIČKY BUDOU UTĚSNĚNY MANŽETAMI

SO 341

Přeložka vodovodu PE 110 v km 2,195

Objednatel:



ŘEDITELSTVÍ
SILNIC
A DÁLNIC

Ředitelství silnic a dálnic s.p.
Čerčanská 2023/12, Krč, 140 00 Praha 4

Zhotovitel:



Valbek, spol. s r.o.

Vaňurova 505/17
460 07 Liberec 3

HIP:

ING. T. KLIMENT



Vypracoval

Zodp. projektant

Tech. kontrola

Akce

BC. ŠTĚPÁN HORECKÝ

ING. JIŘÍ VANCL

ING. DAVID LANDA

Zak. číslo

Datum

Stupeň

Počet formátů

Měřítko

Č. přílohy

21-L113-001

02/2025

PDPS

4 x A4

-

Paré

Zhotovitel:

Valbek, spol. s r.o.
Vaňurova 505/17
460 07 Liberec 3

Příloha

KLADĚČSKÝ PLÁN

5