

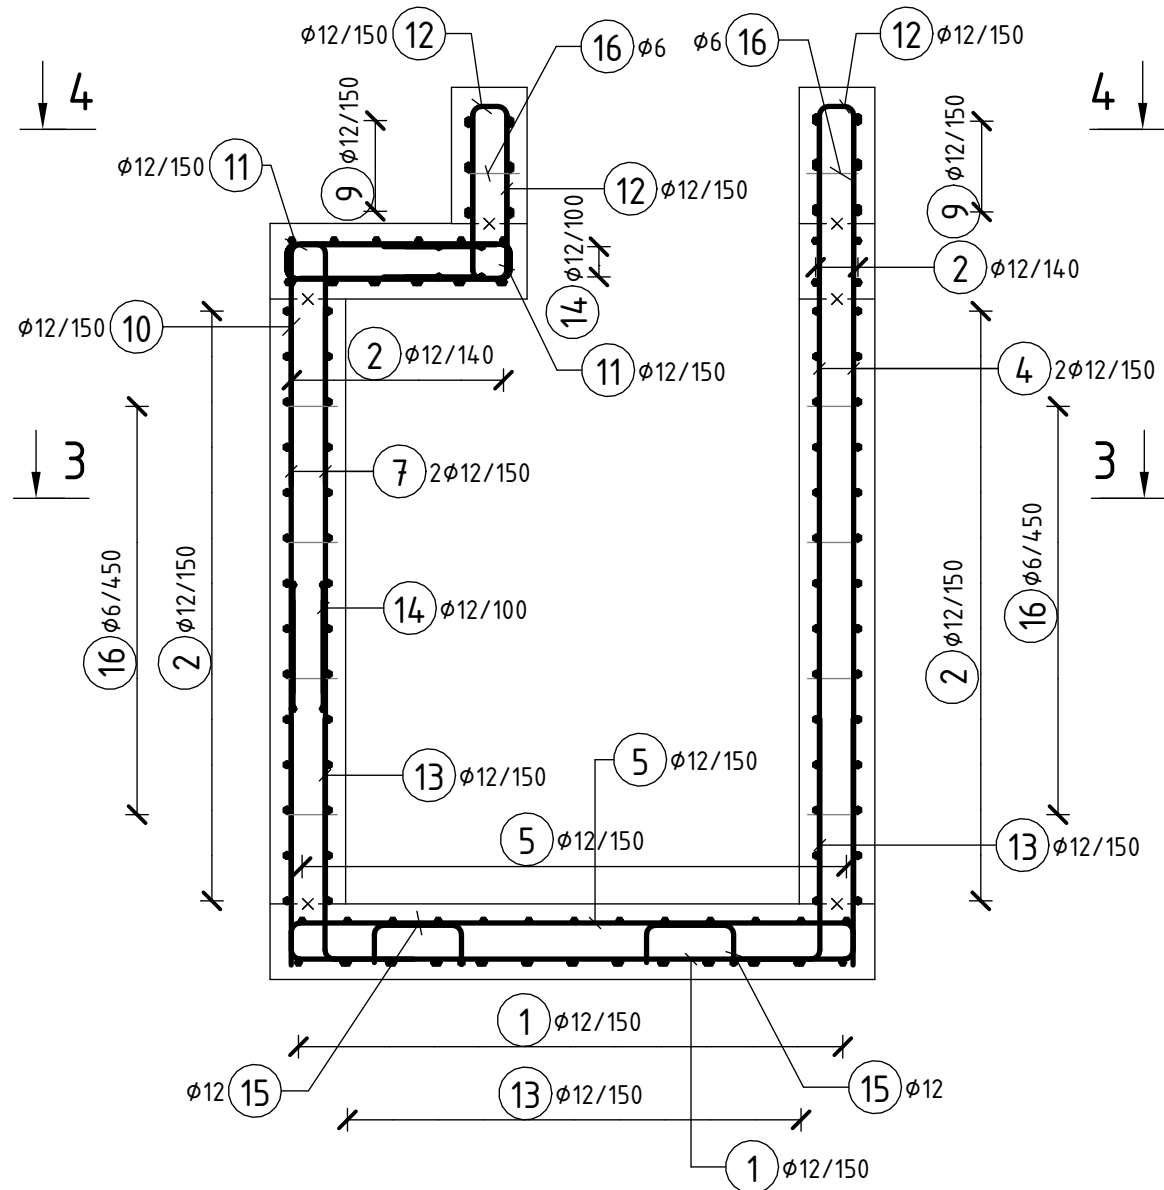


ŘEZ 1-1 1: 25

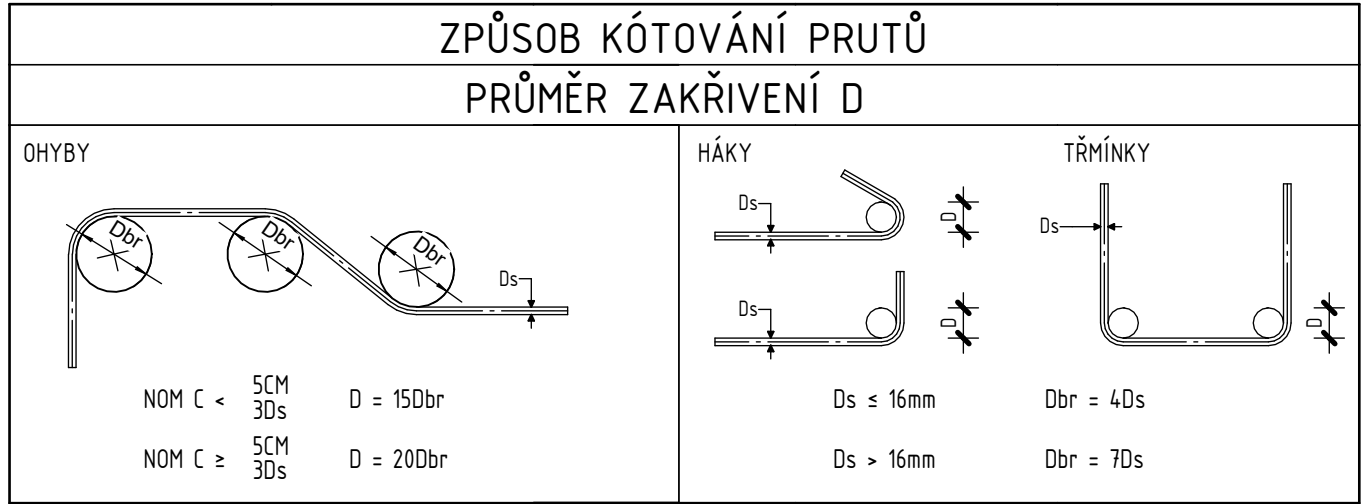

ŘEZ 2-2 1: 25

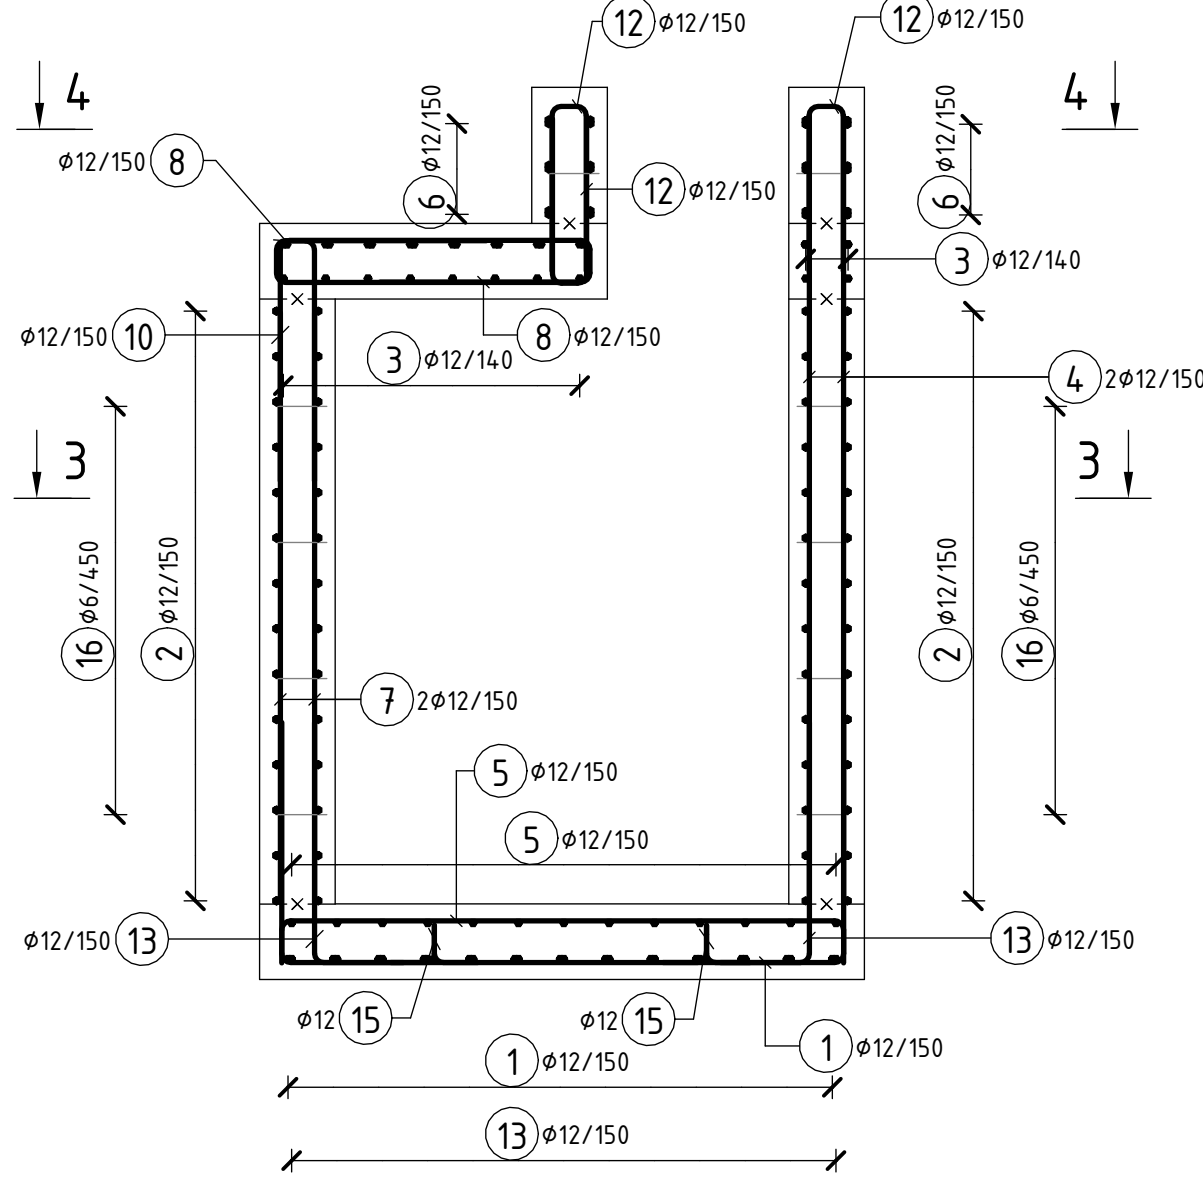

POZNÁMKY:

- V MÍSTĚ POTRUBÍ BUDE VÝZTUŽ OŘÍZNUTA.

BETON

JÍMKÁ

KRYTÍ

VŠECHNY PLOCHY

OCEL

BETONÁŘSKÁ

ČSN EN 206+A2

C30/37-XF3

MINIMÁLNÍ / JMENOVITÉ

45mm / 50 mm

ČSN EN 10027-1


B 500B

ROZMĚRY VÝZTUŽE JSOU KÓTOVÁNY NA VNĚJŠÍ HRANY


VÝKAZ VÝZTUŽE

ČÍSLO POL.	Ø [mm]	DĚLKA [mm]	POČET [ks]	DĚLKY PODLE Ø [m]	
				d6	d12
1	12	3470	26	0	90.22
2	12	2650	128	0	339.2
3	12	2675	20	0	52.5
4	12	2600	30	0	78
5	12	2160	26	0	56.16
6	12	2050	12	0	24.6
7	12	1950	66	0	128.7
8	12	1850	12	0	22.2
9	12	1750	12	0	21
10	12	1725	33	0	56.94
11	12	1525	8	0	12.2
12	12	1225	41	0	50.24
13	12	1100	48	0	52.8
14	12	1000	12	0	12
15	12	870	4	0	3.48
16	6	305	54	16.5	0
DĚLKA PODLE Ø CELKEM			[m]	16.5	1000.24
JEDNOTKOVÁ HMOTNOST			[kg/m']	0.222	0.888
HMOTNOST PODLE Ø CELKEM			[kg]	3.66	888.2
CELKOVÁ HMOTNOST VÝZTUŽE			[kg]	891.86	


ŘEZ 3-3 1: 25

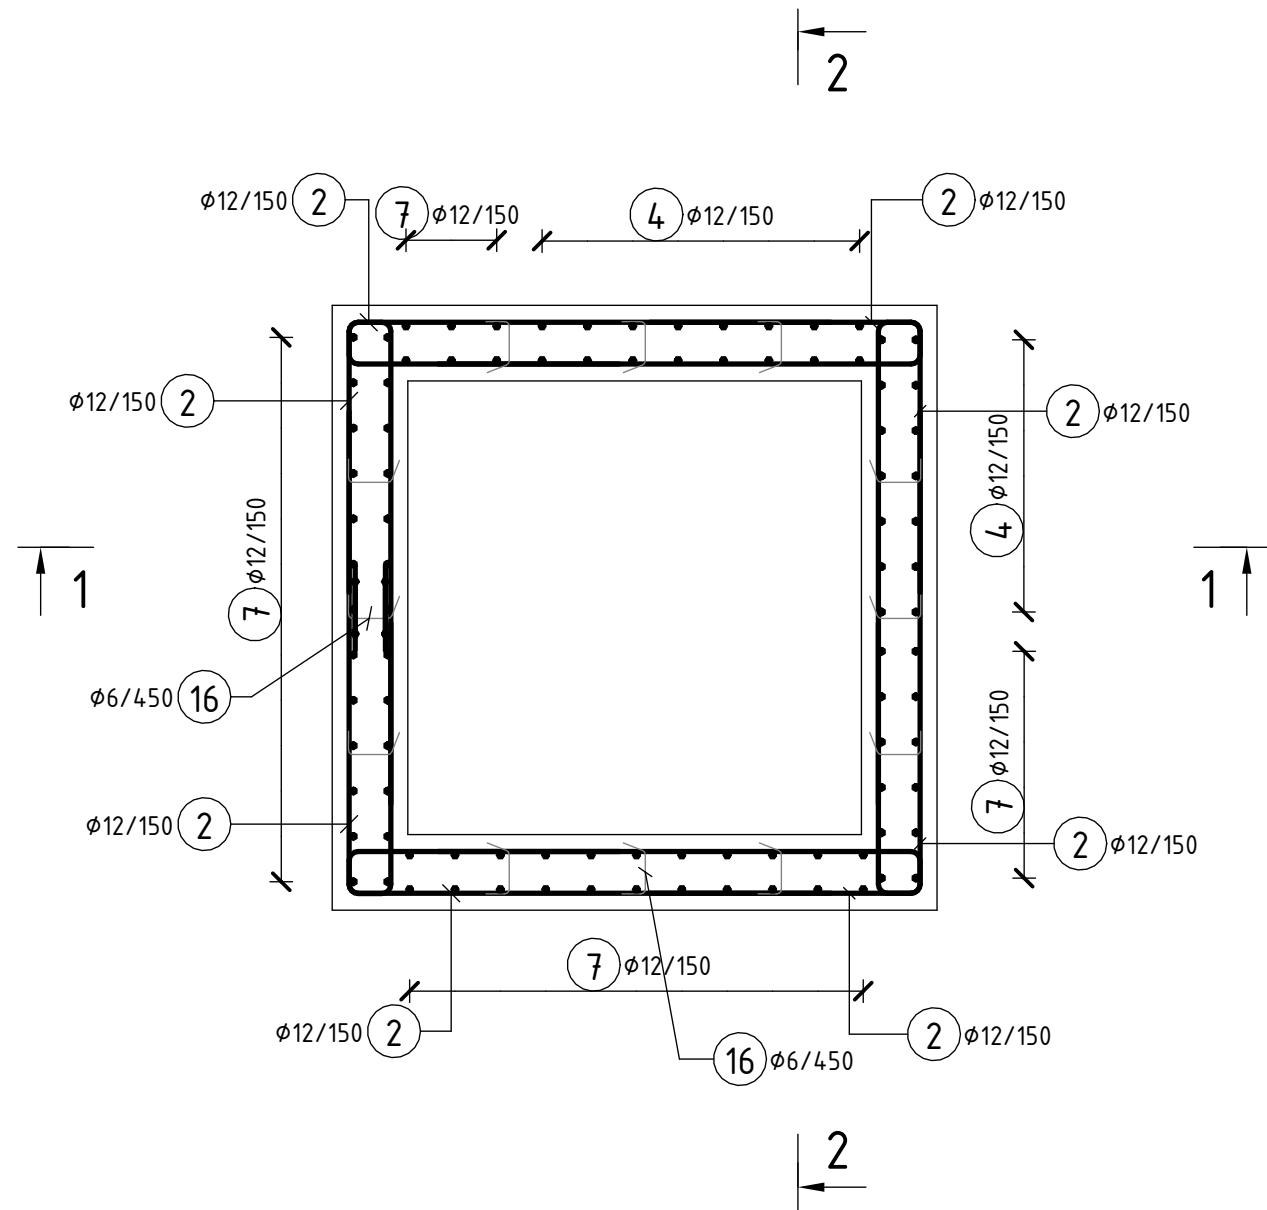

ŘEZ 4-4 1: 25

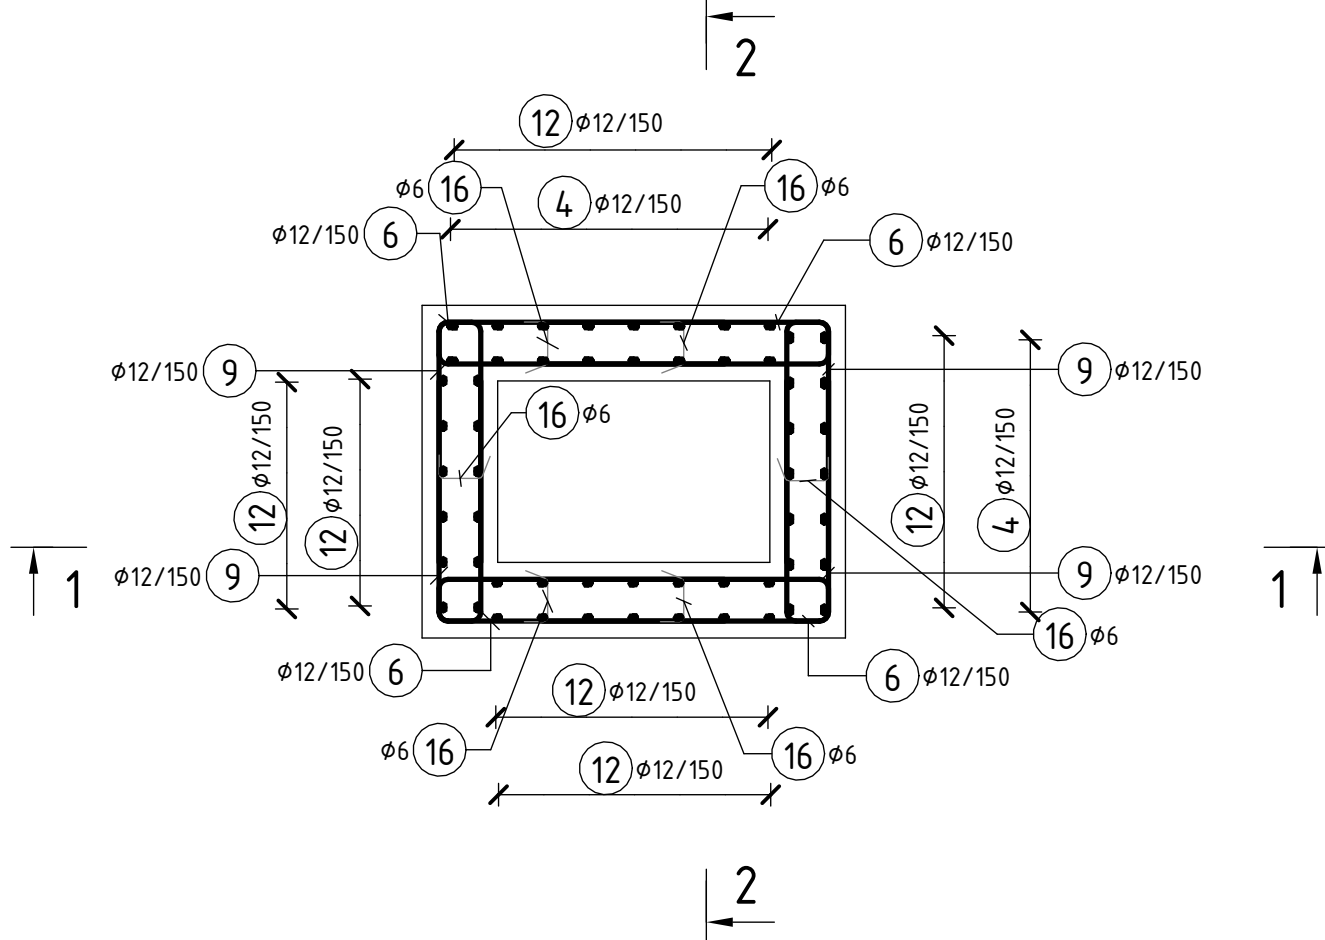

DETAIL 1 1: 25

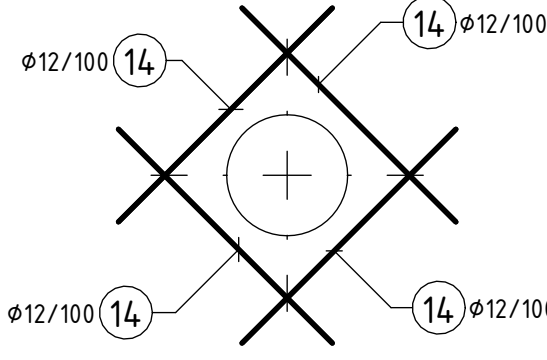

Souřadnicový systém: S-JTSK
Výškový systém: Bpv

SO 341 Přeložka vodovodu PE 110 v km 2,195

Objednatel:



Ředitelství silnic a dálnic s. p.
Čerčanská 2023/12, Krč, 140 00 Praha 4

Zhotovitel:



Valbek, spol. s r.o.
Vaňurova 505/17
460 07 Liberec 3



Zhotovitel:
Valbek, spol. s r.o.
Vaňurova 505/17
460 07 Liberec 3

Příloha
ARMATURNÍ ŠACHTA AŠ1 - VÝKRES VÝZTUŽE

Vypracoval: ING. ROMAN NAZARCHUK
Zodp. projektant: ING. JIŘÍ VANCL
Tech. kontrola: ING. DAVID LANDA
Akce: I/16 MLADÁ BOLESLAV - MARTINOVICE

Zak. číslo: 21-LI13-001
Datum: 02/2025
Stupeň: PDPS
Počet formátů: 8x A4
Měřítko: 1:25
Č. přílohy: Paré

6.3