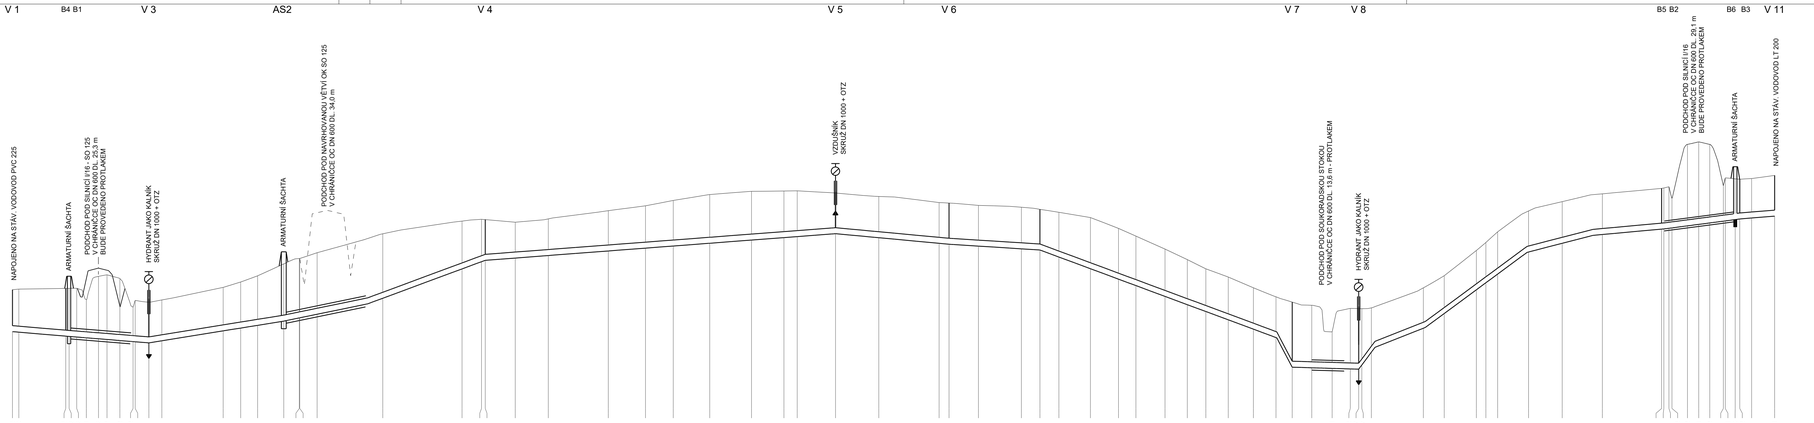

SKLON ‰ - DÉLKA v m	
A1	-191, 6,43
A2	134, 6,80
A3	15, 1,87

VRCHOLOVÝ BOD	
B1	AS1
B2	V
B3	V 10
B4	V 2
B5	V 9
B6	AS3

Souřadnicový systém: S-JTSK
Výškový systém: Bpv

SO 342 Přeložka vodovodu PVC 225 v MÚK Židněves

Objednatel:

ŘEDITELSTVÍ SILNIC A DÁLNIC

Ředitelství silnic a dálnic s. p.
Čerčanská 2023/12, Krč, 140 00 Praha 4

Zhotovitel:

Valbek

Valbek, spol. s r.o.
Vaňurova 505/17
460 07 Liberec 3

Vypracoval	BC. Š. HORECKÝ		Zak. číslo	21-LI13-001
Zodp. projektant	ING. J. VANCL		Datum	02/2025
Tech. kontrola	ING. D. LANDA		Stupeň	PDPS
Akce	I/16 MLADÁ BOLESLAV - MARTINOVICE		Počet formátů	6 x A4
			Měřítko	1 : 1000 / 100
Zhotovitel: Valbek, spol. s r.o. Vaňurova 505/17 460 07 Liberec 3	Příloha PODÉLNÝ PROFIL		Č. přílohy	Paré
		3		