

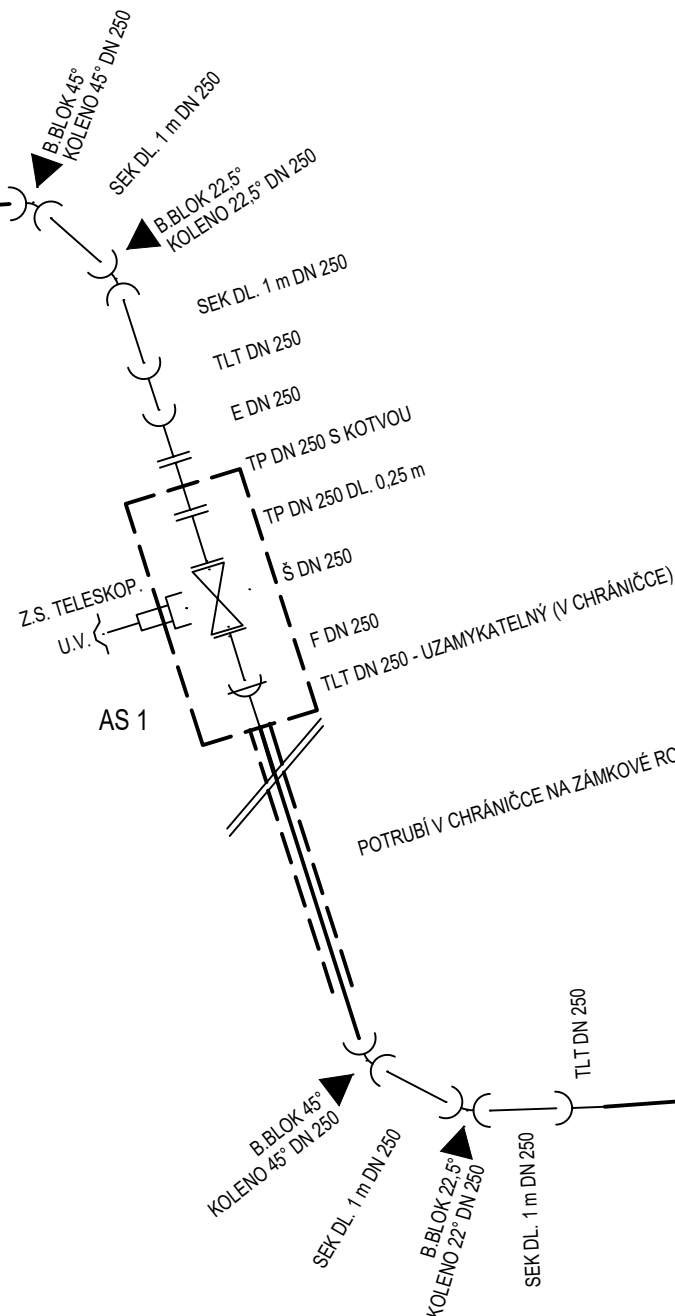


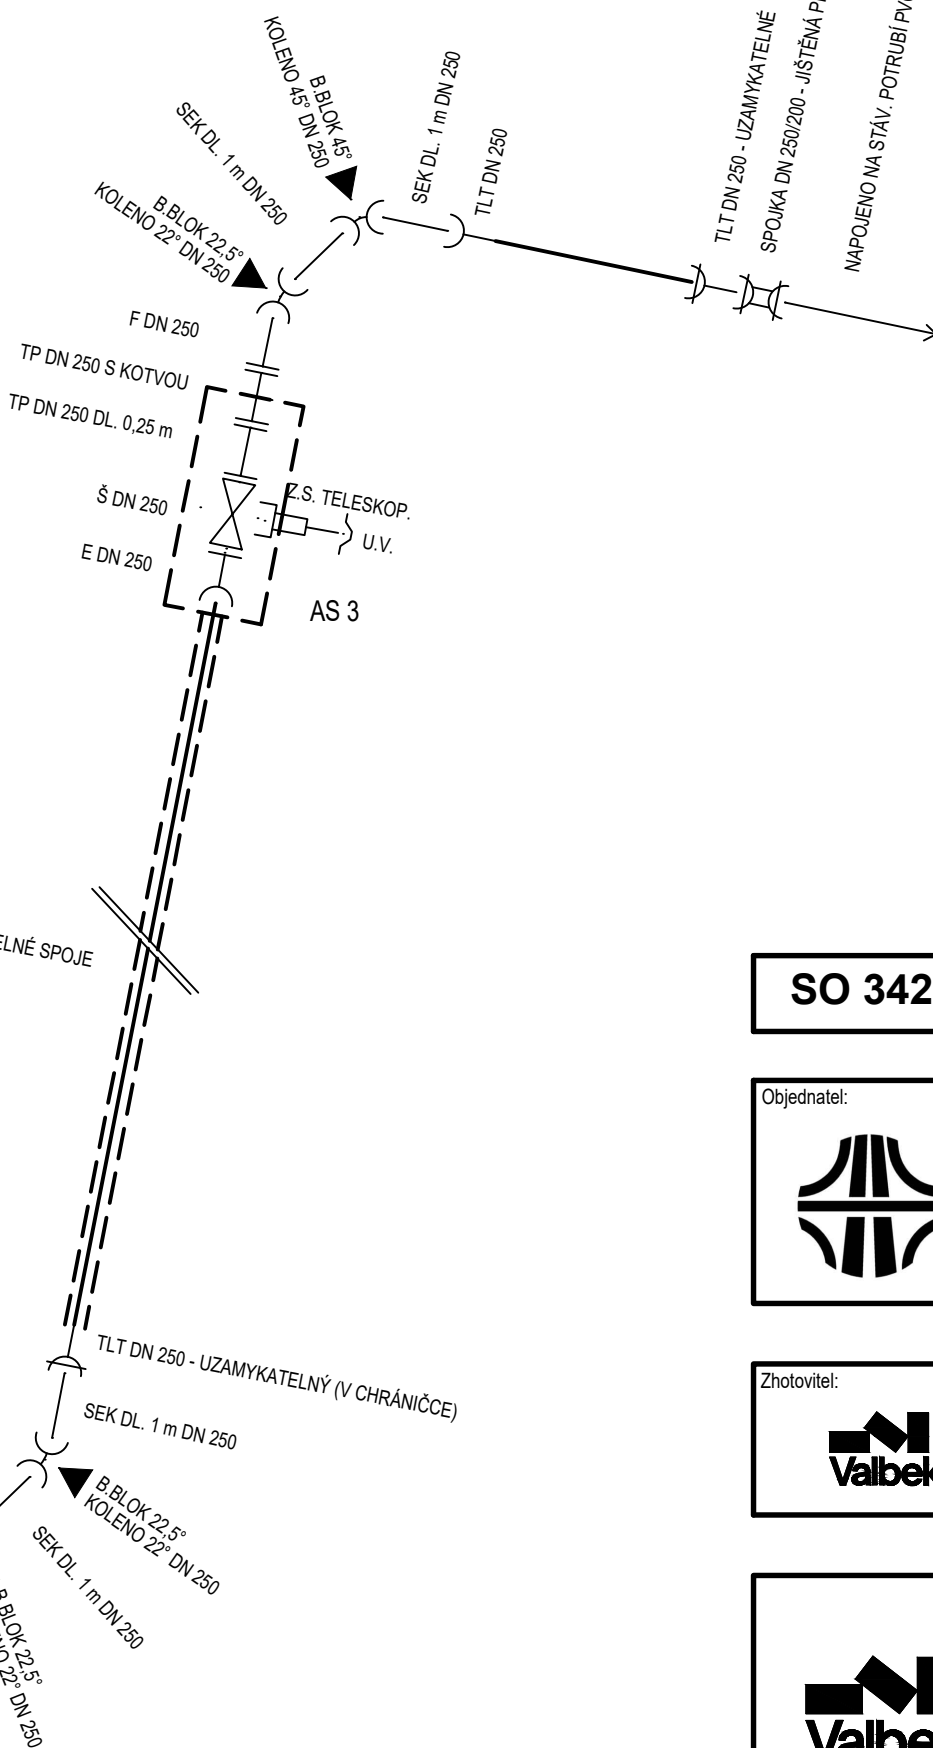

SPOJKY, TVAROVKY A ARMATURY DLE POŽADAVKU PROVOZOVATELE  
LITINOVÉ POTRUBÍ BUDE NA KLUZNÝCH OBJÍMKÁCH PO 1 METRU  
CHRÁNIČKY BUDOU UTĚSNĚNY MANŽETAMI

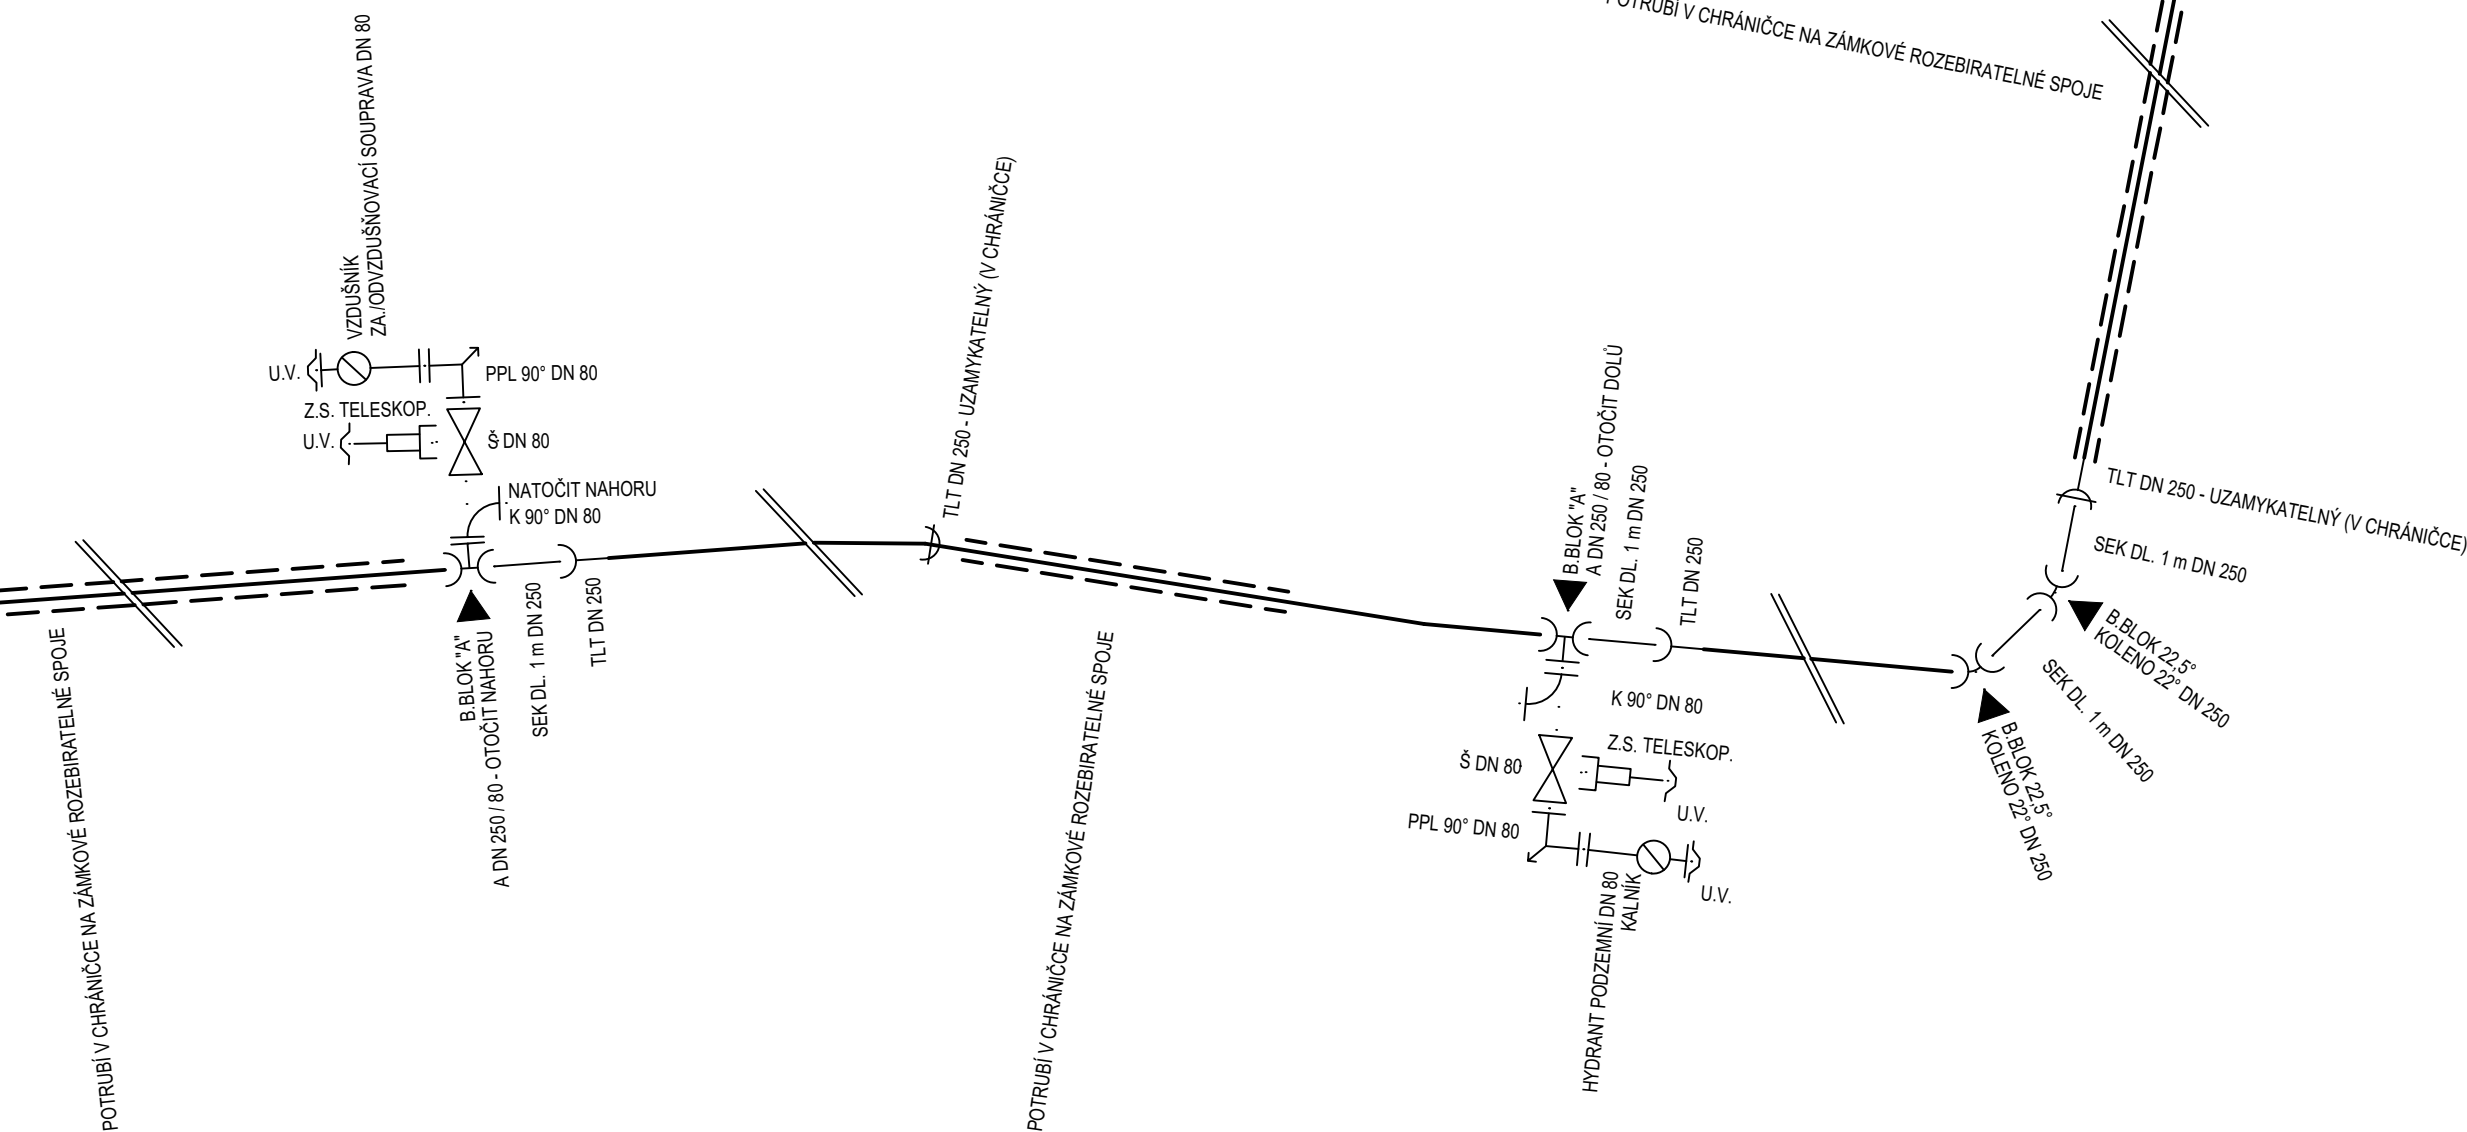


# Přeložka vodovodu PVC 225 v MÚK Židněves

**Ředitelství silnic a dálnic s.p.**  
Čerčanská 2023/12, Krč, 140 00 Praha 4

**Valbek, spol. s r.o.**  
Vaňurova 505/17  
460 07 Liberec 3

ING. T. KLIMENT

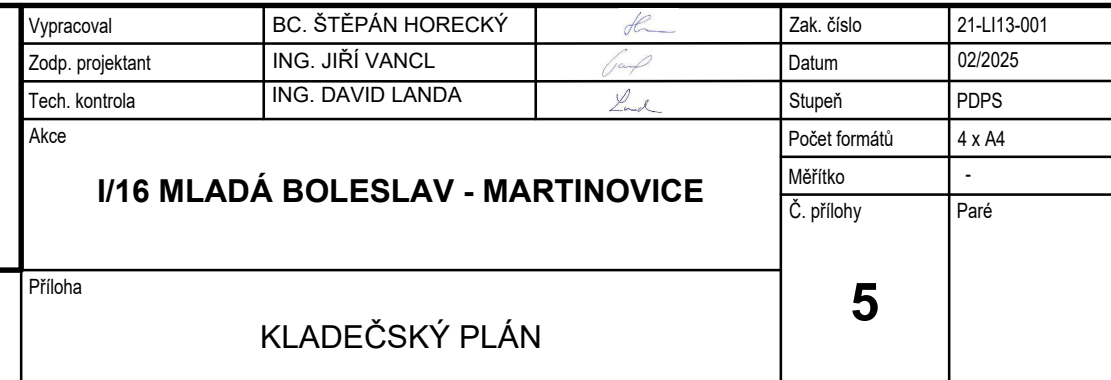

|               |                    |                                                                                       |            |             |
|---------------|--------------------|---------------------------------------------------------------------------------------|------------|-------------|
| racoval       | BC. ŠTĚPÁN HORECKÝ |  | Zak. číslo | 21-LI13-001 |
| p. projektant | ING. JIŘÍ VÁNCL    |  | Datum      | 02/2025     |
| h. kontrola   | ING. DAVID LANDA   |  | Stupeň     | PDPS        |

|                                   |               |        |
|-----------------------------------|---------------|--------|
| I/16 MLADÁ BOLESLAV - MARTINOVICE | Počet formátů | 4 x A4 |
|                                   | Měřítka       | -      |

**Zhotovitel:**  
Valbek, spol. s r.o.  
Vaňurova 505/17  
460 07 Liberec 3

|         |               |
|---------|---------------|
| Příloha | KLADČSKÝ PLÁN |
|---------|---------------|

**5**